


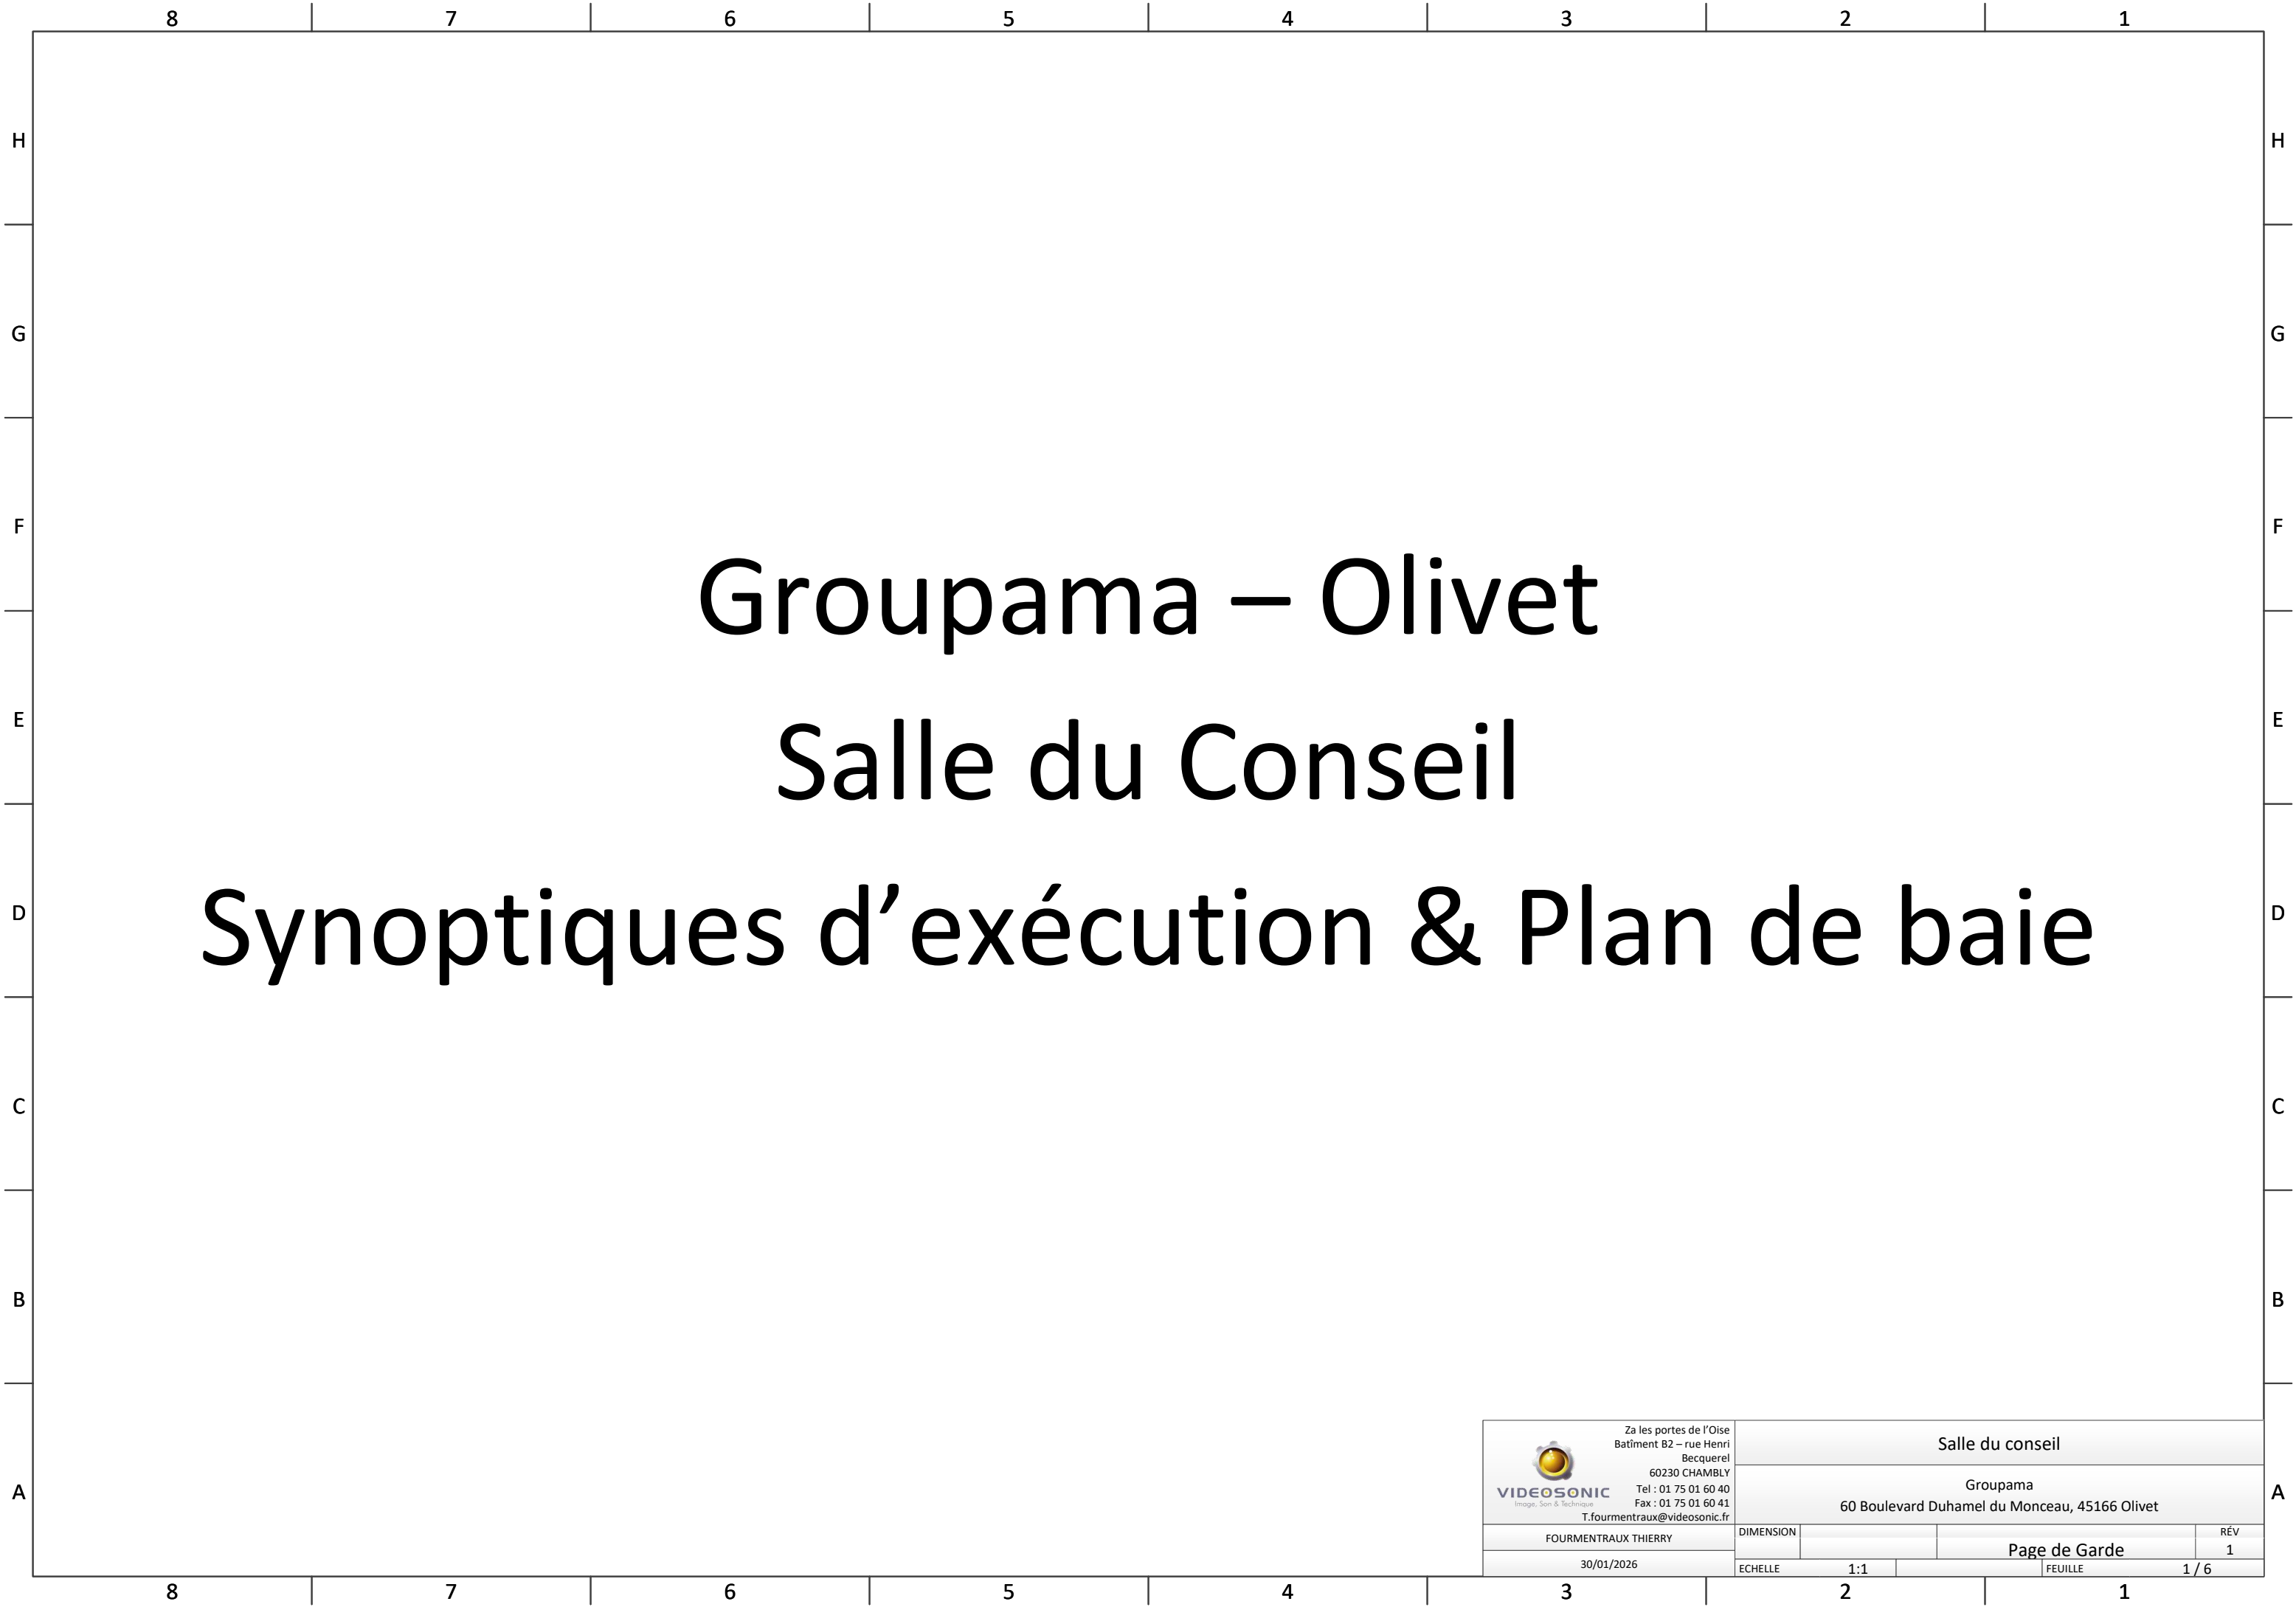


Groupama – Olivet

Salle du Conseil

Synoptiques d'exécution & Plan de baie

 VIDEOSONIC Image, Son & Technique	Za les portes de l'Oise Batiment B2 – rue Henri Becquerel 60230 CHAMBLY Tel : 01 75 01 60 40 Fax : 01 75 01 60 41 T.fourmentraux@videosonic.fr			Salle du conseil	
	Groupama 60 Boulevard Duhamel du Monceau, 45166 Olivet				
	FOURMENTRAUX THIERRY		DIMENSION		RÉV 1
30/01/2026		ECHELLE	1:1	Page de Garde FEUILLE 1 / 6	

BAIE IT 42U

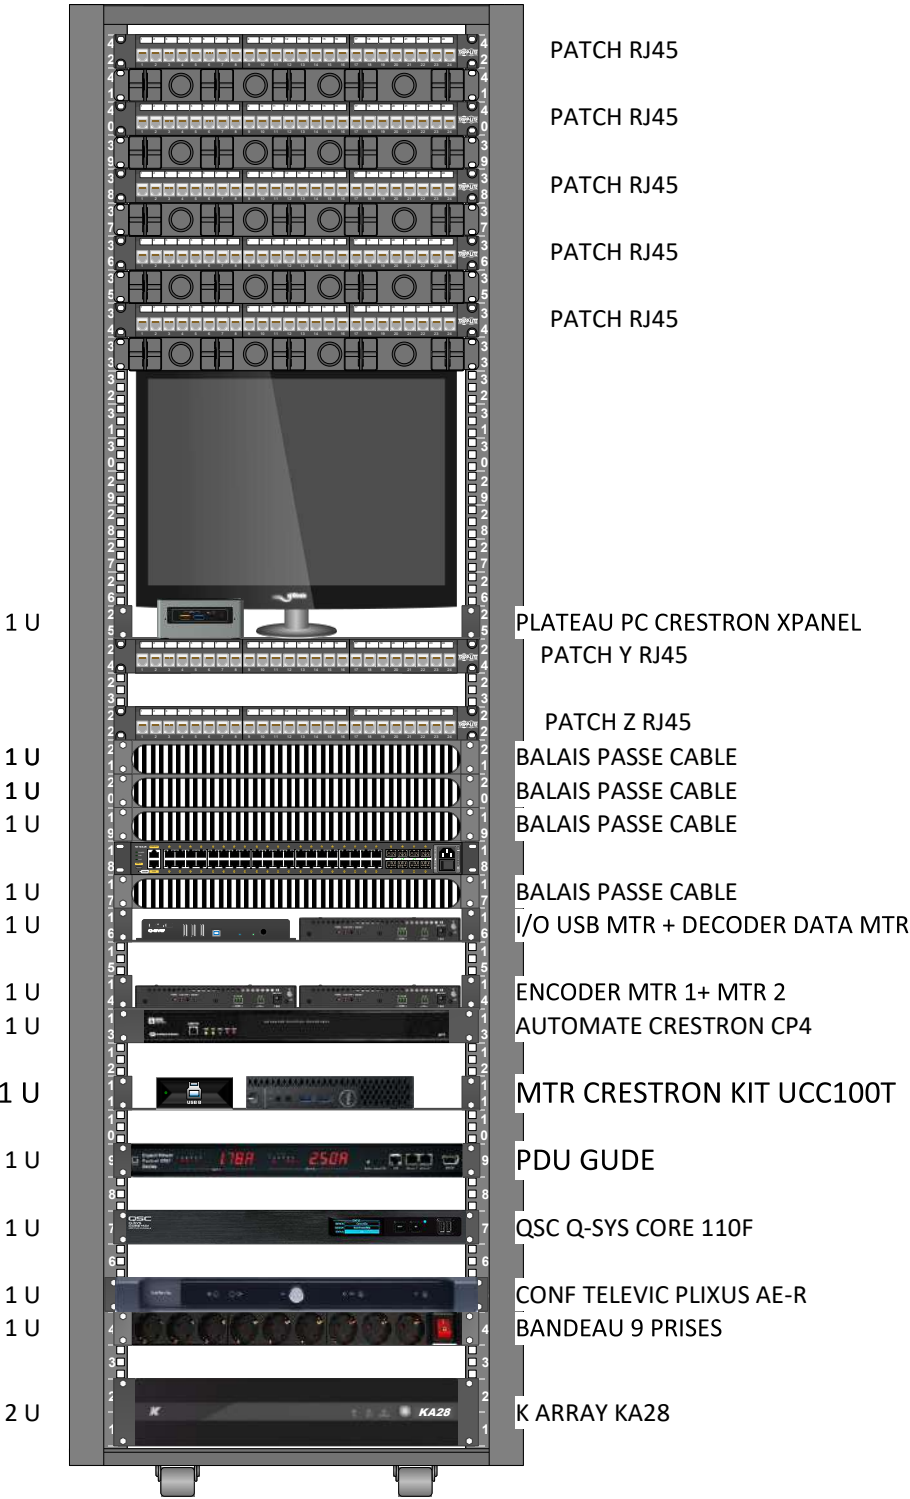

 Za les portes de l'Oise Batiment B2 – rue Henri Becquerel 60230 CHAMBLY Tel : 01 75 01 60 40 Fax : 01 75 01 60 41 @ : contact@videosonic.fr	Salle du conseil			
	Groupama 60 Boulevard Duhamel du Monceau, 45166 Olivet			
	FOURMENTRAUX THIERRY	DIMENSION		RÉV 1
30/01/2026	ECHELLE	1:10	FEUILLE	3 / 6
		Plan d e baie		



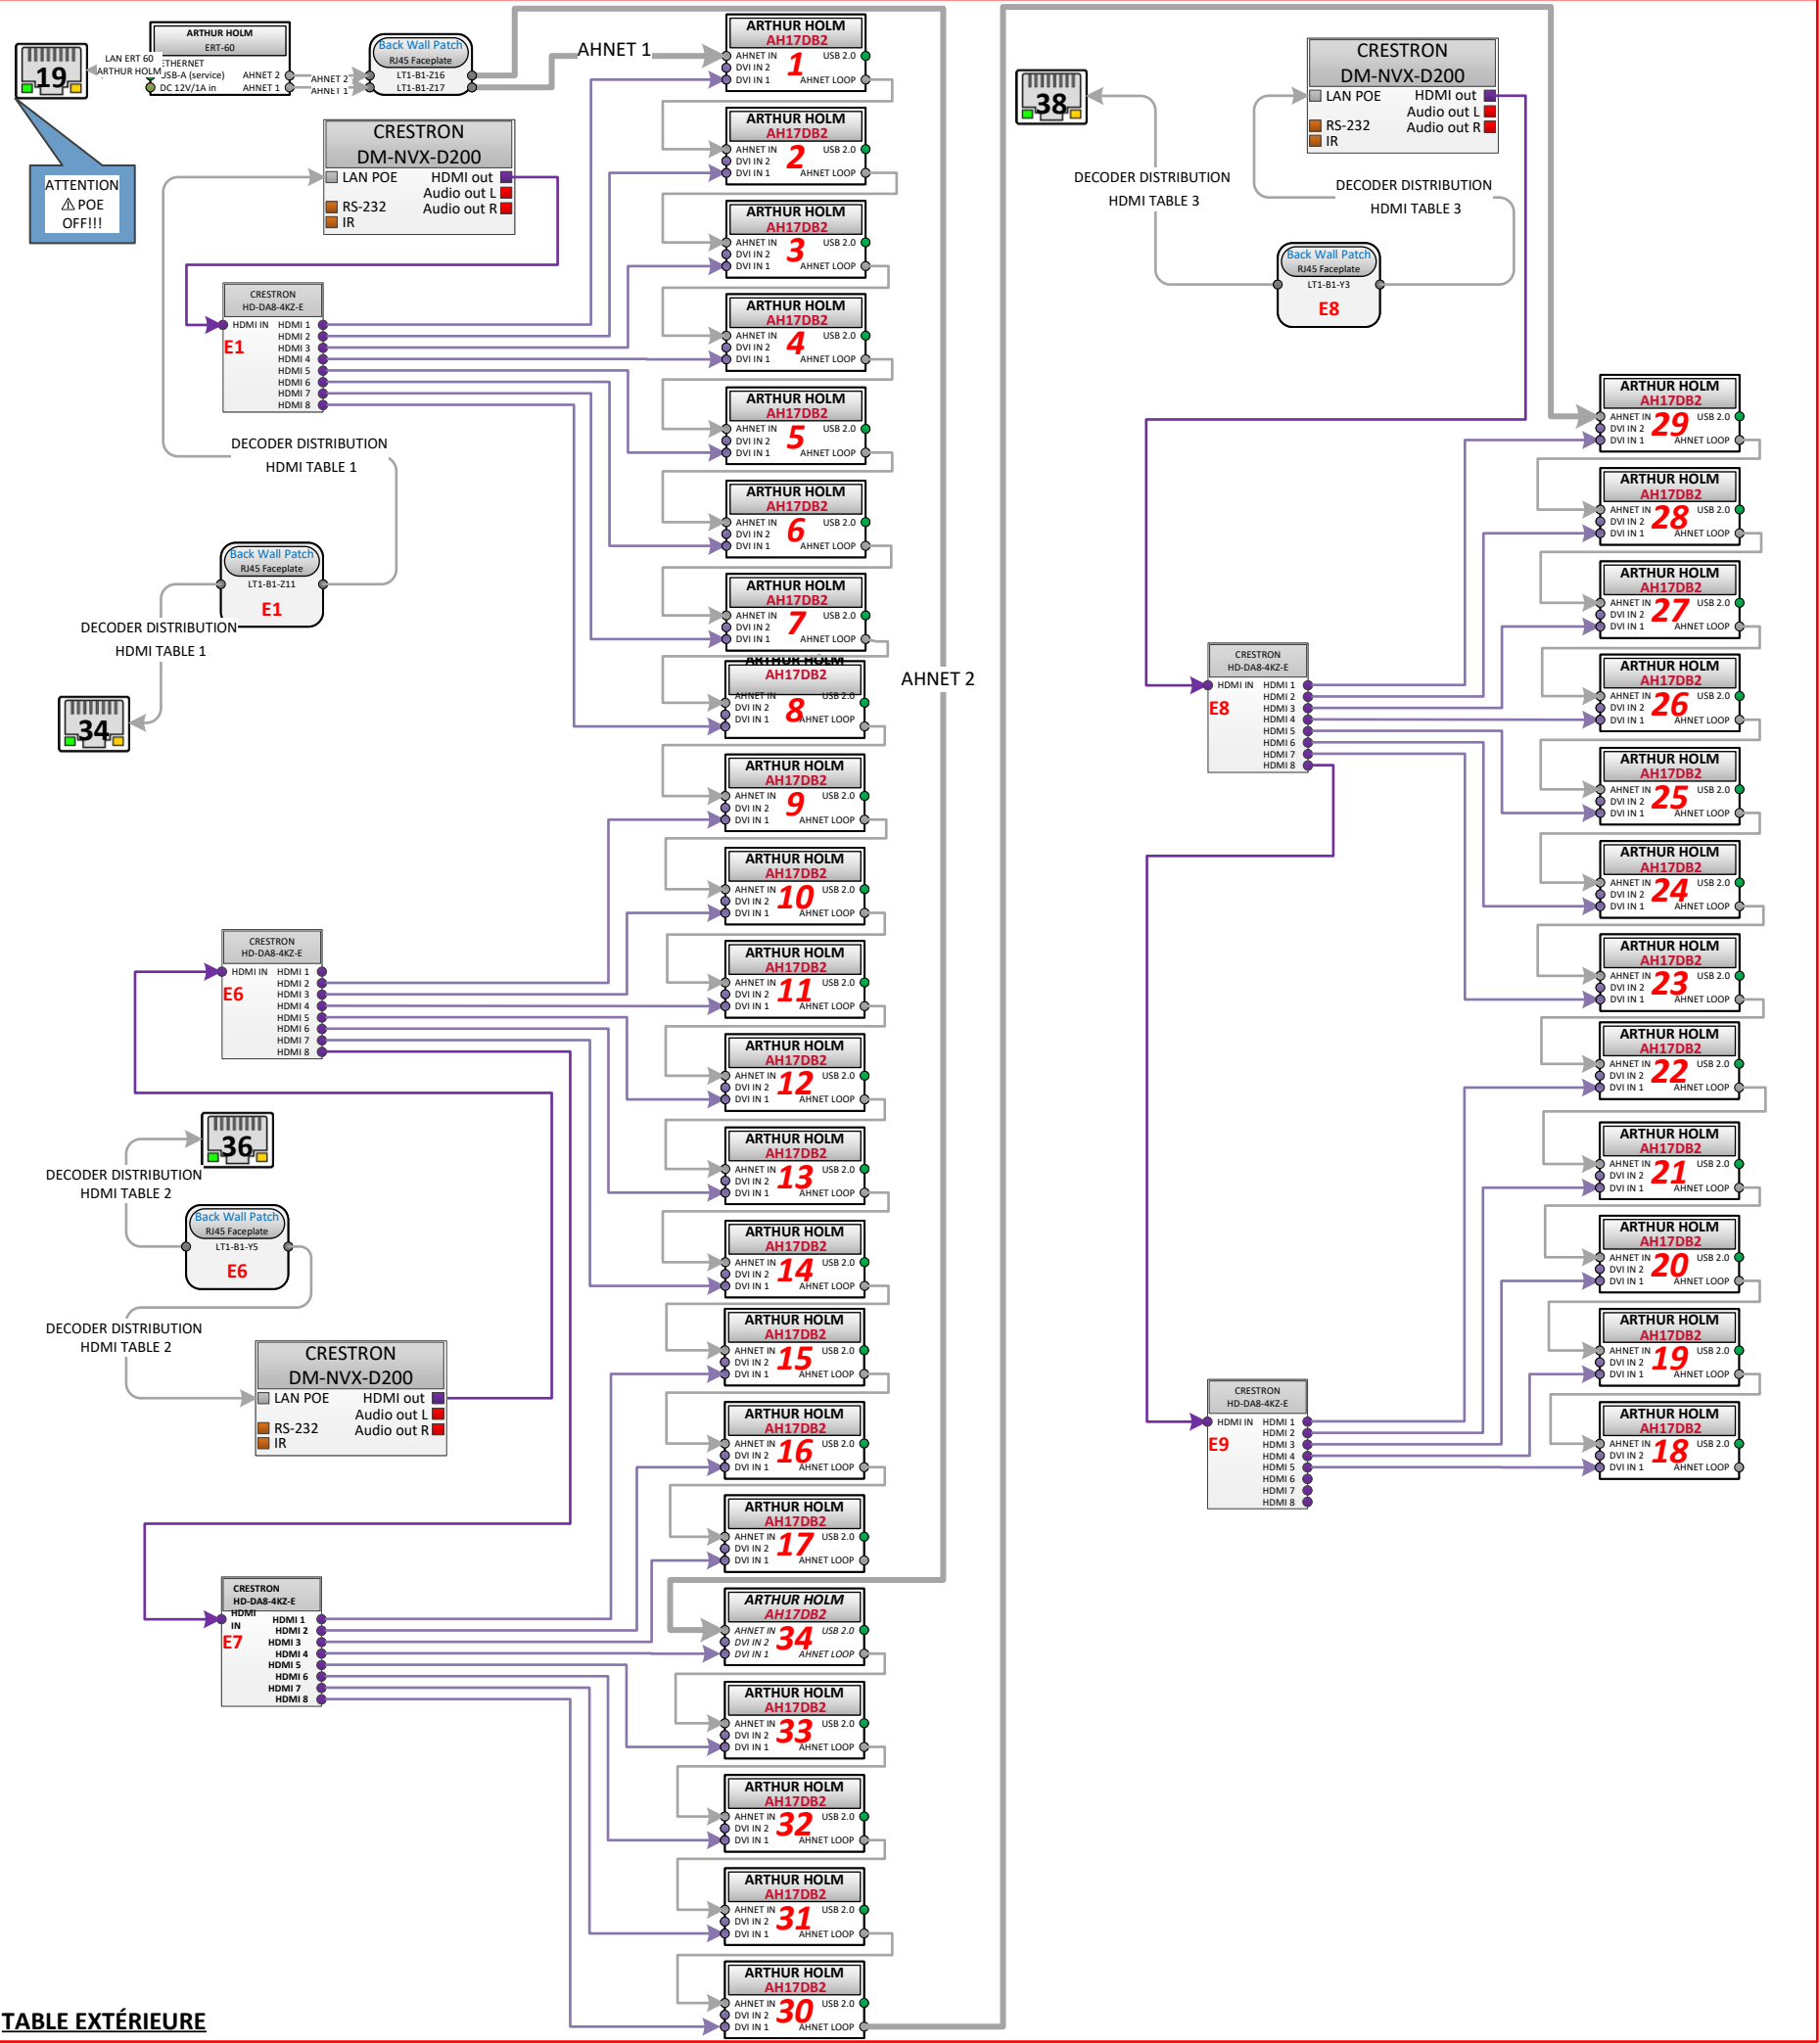



TABLE INTÉRIEURE

 VIDEOSONIC Image, Son & Technique T.fourmentraux@videosonic.fr Za les portes de l'Oise Batiment B2 – rue Henri Becquerel 60230 CHAMBLY Tel : 01 75 01 60 40 Fax : 01 75 01 60 41 T.fourmentraux@videosonic.fr Salle du conseil				
	Groupama			
	60 Boulevard Duhamel du Monceau, 45166 Olivet			
FOURMENTRAUX THIERRY	DIMENSION		DISTRIBUTION VIDÉO TABLE	RÉV 1
30/01/2026	ECHELLE	1:1	FEUILLE	4 / 7

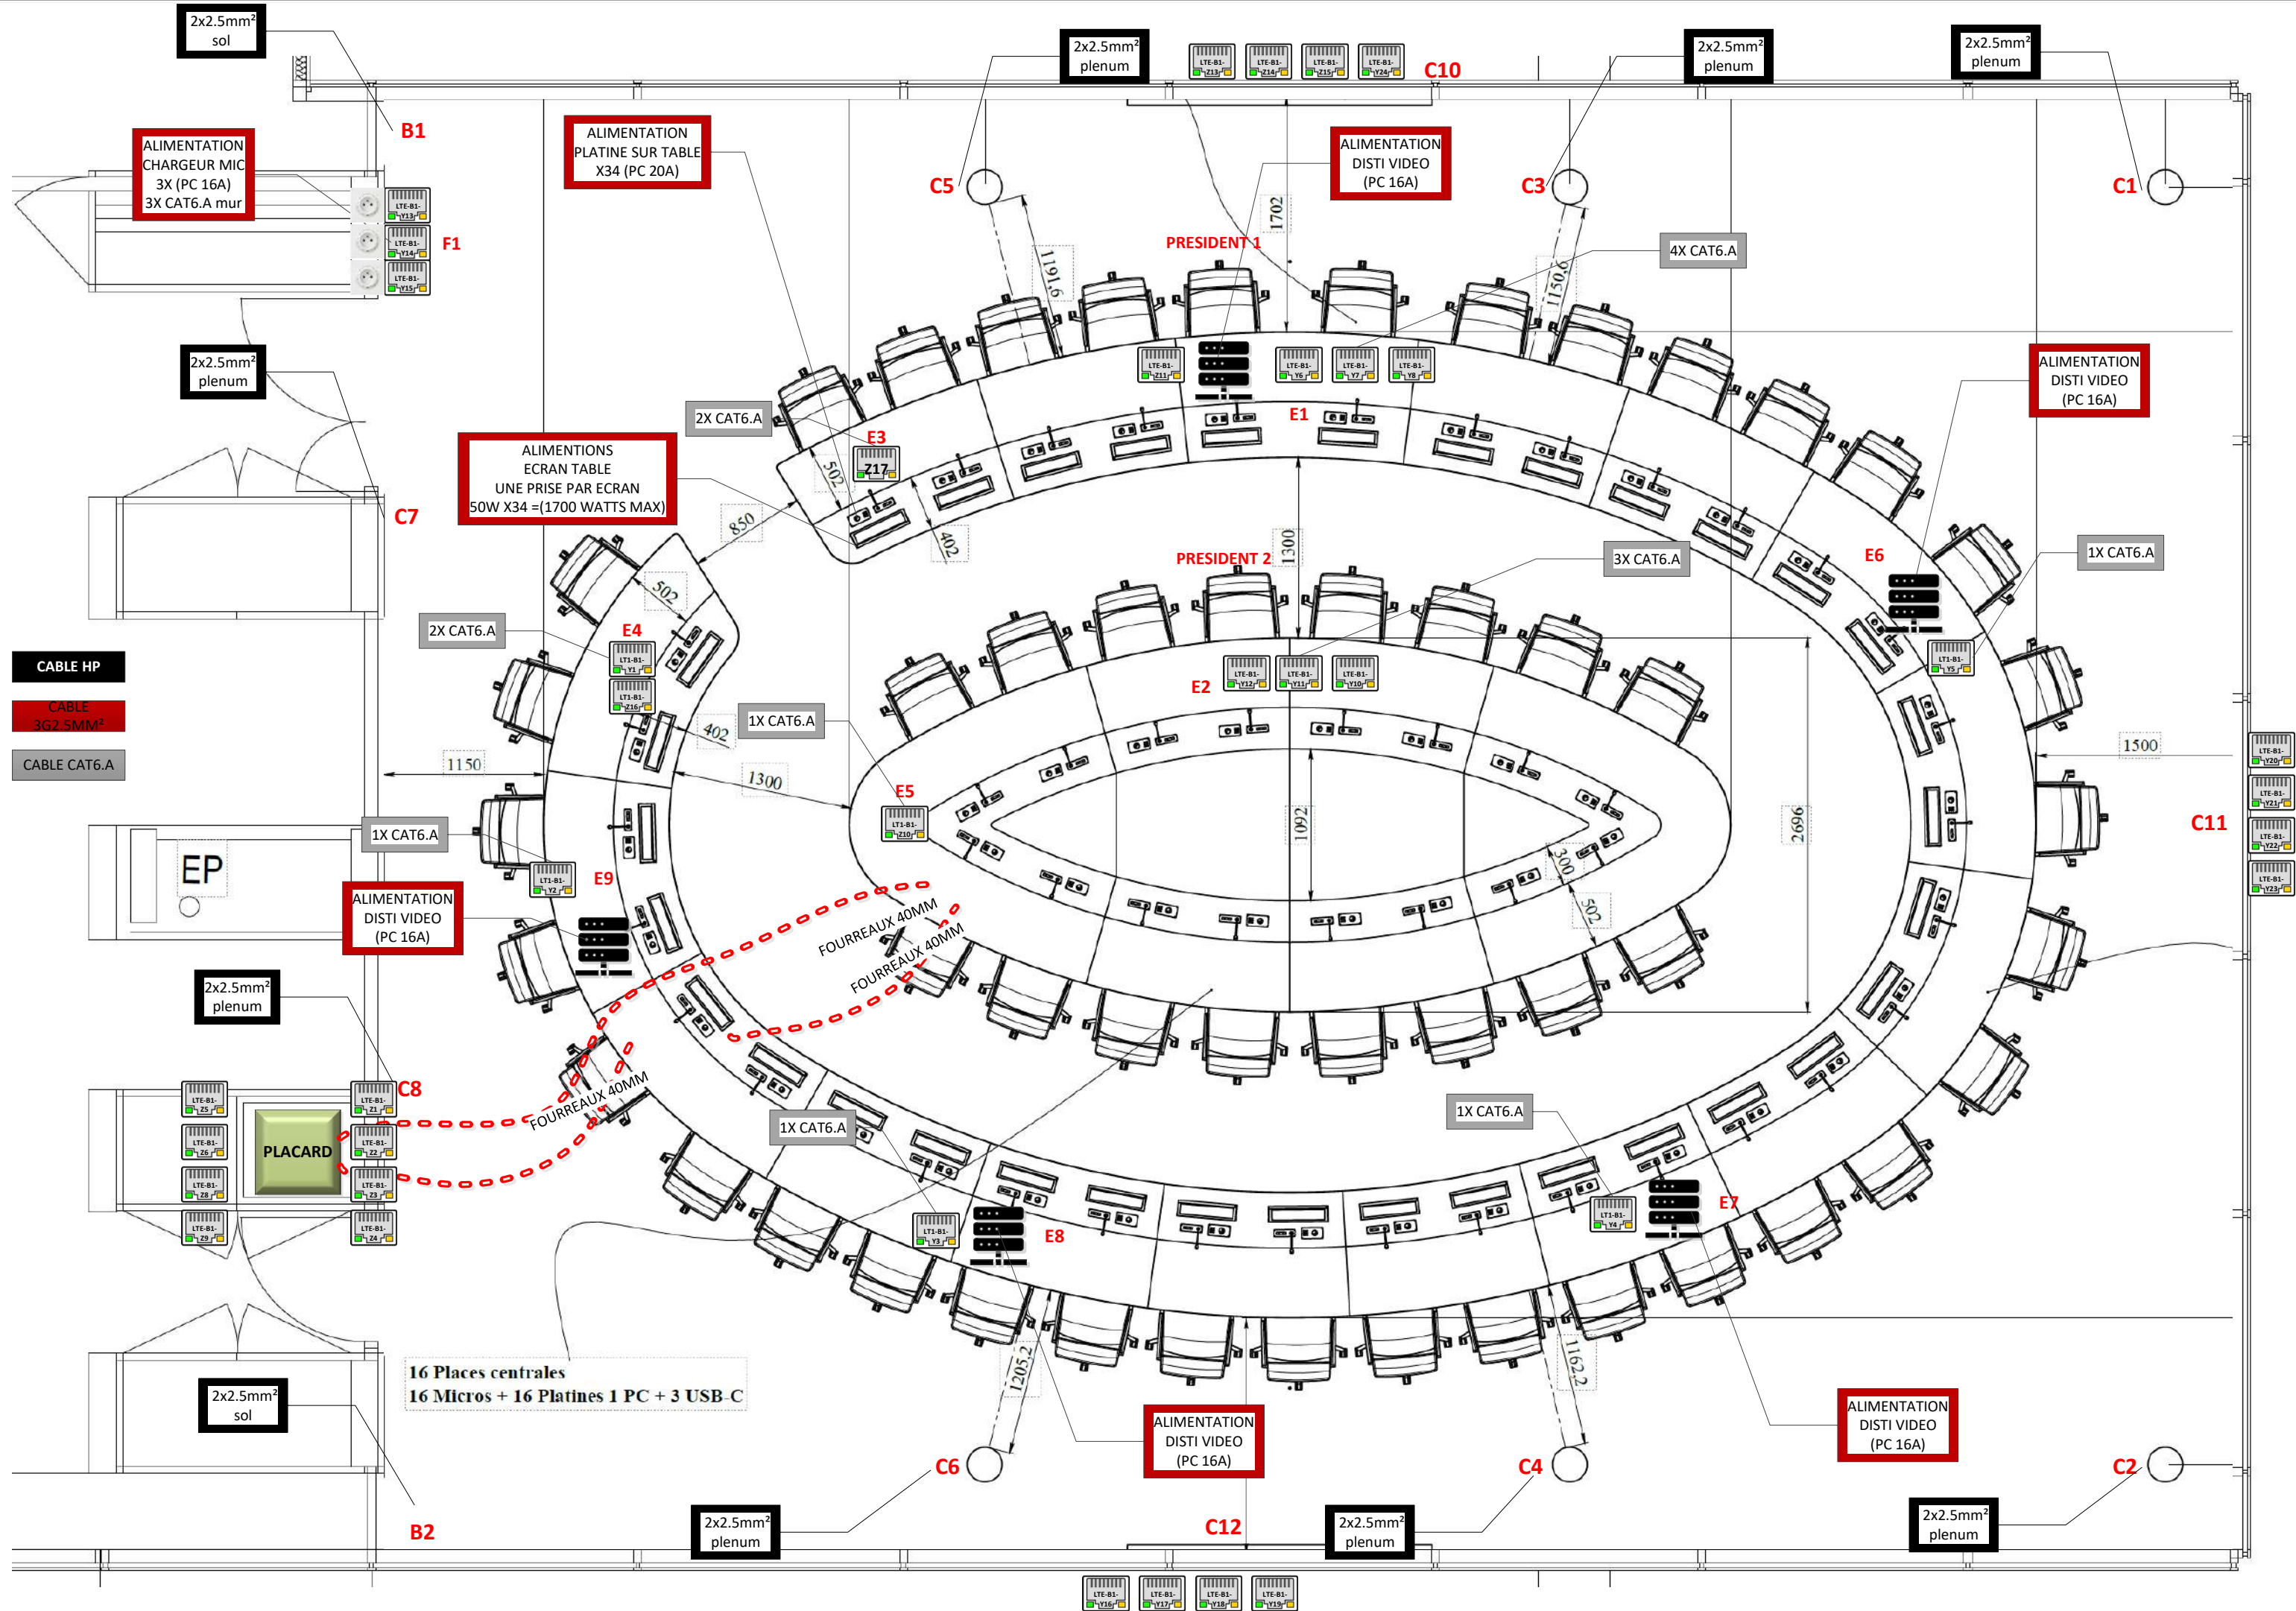

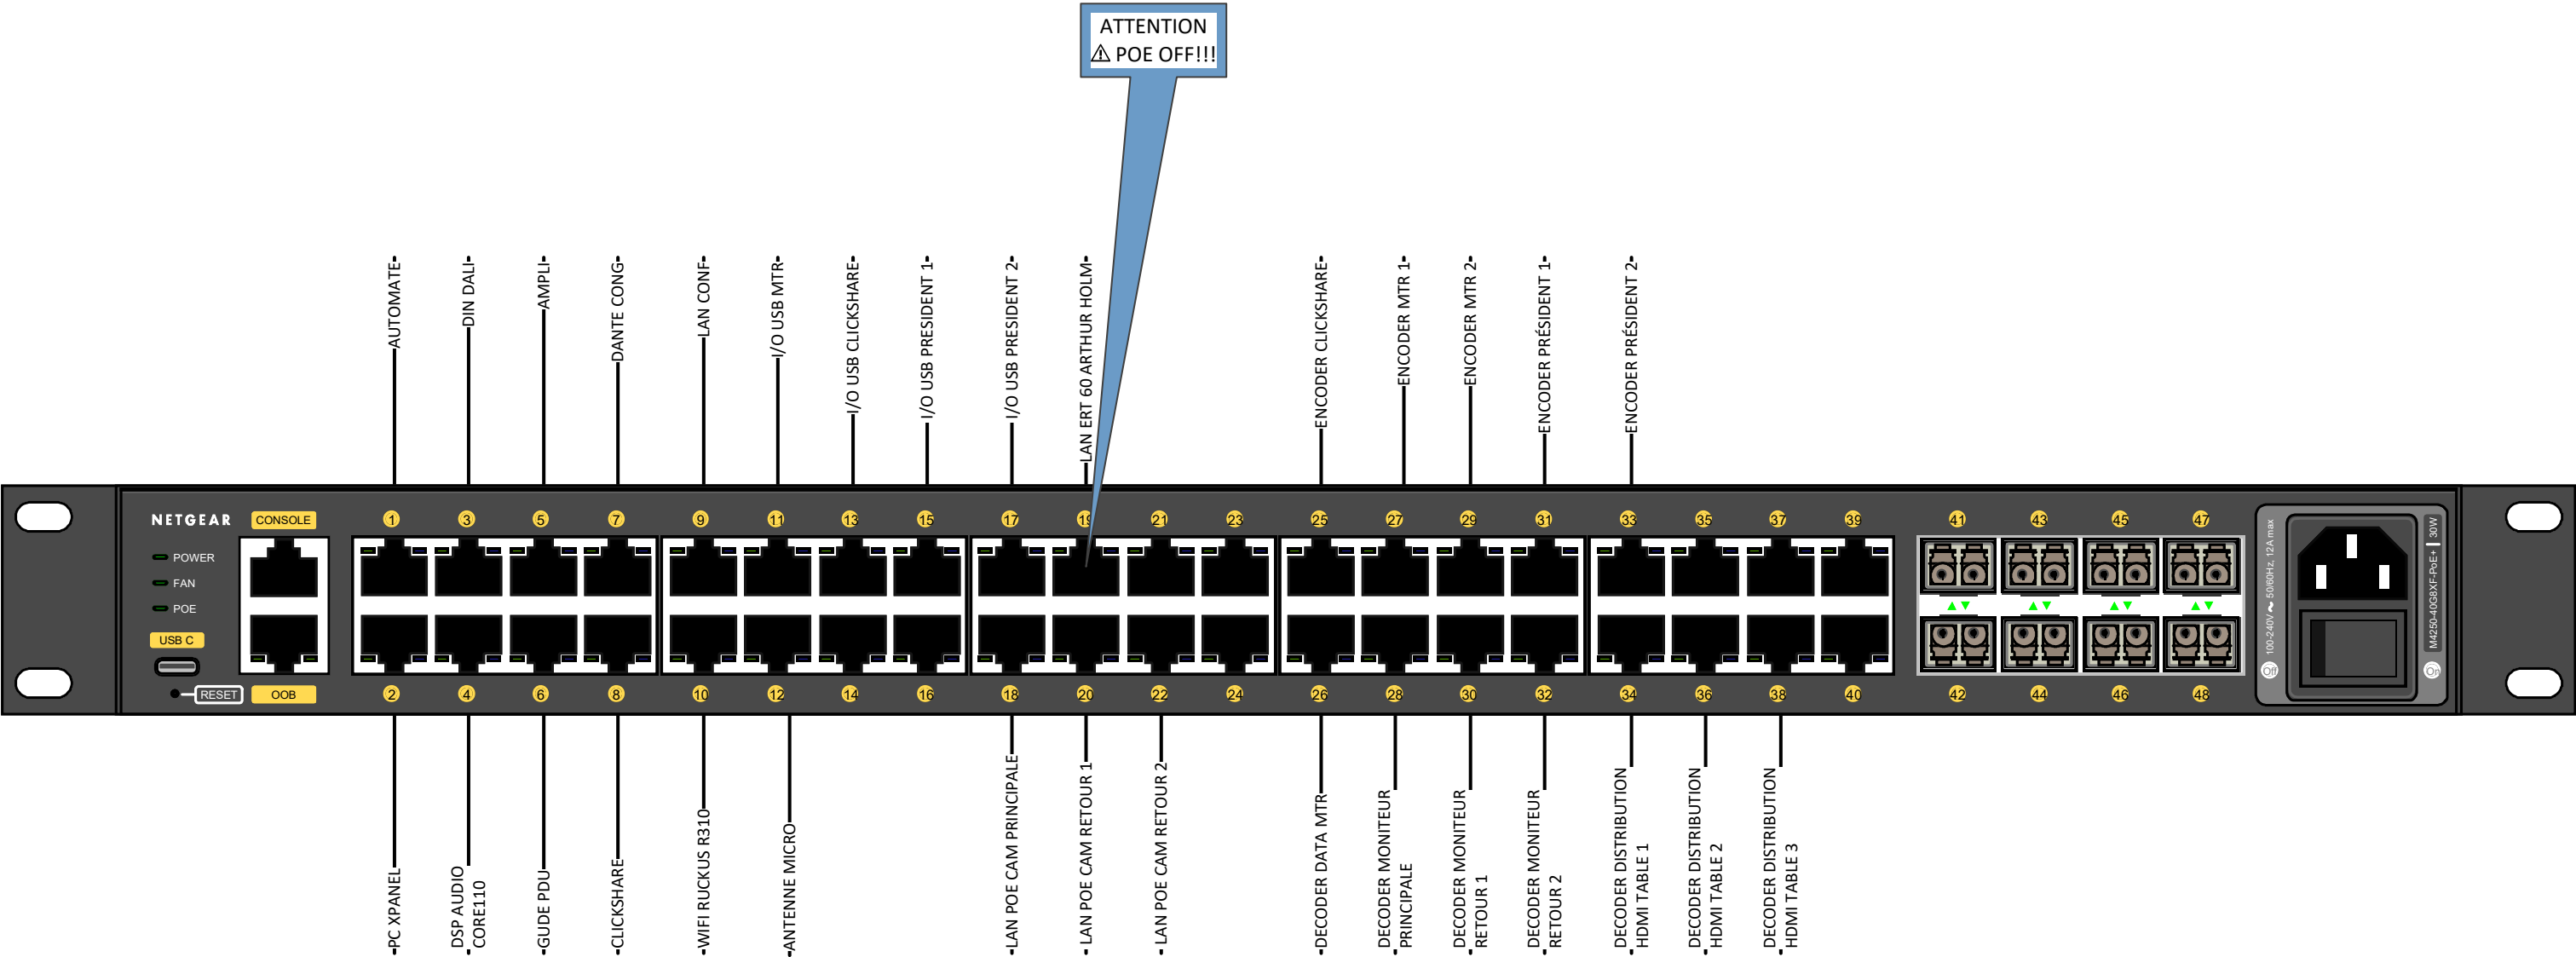


 Za les portes de l'Oise Batiment B2 - rue Henri Becquerel 60230 CHAMBLY Tel : 01 75 01 60 40 Fax : 01 75 01 60 41 T.fourmentraux@videasonic.fr	Salle du conseil		
	Groupama 60 Boulevard Duhamel du Monceau, 45166 Olivet		
	FOURMENTRAUX THIERRY	DIMENSION	RÉV 1
30/01/2026	ECHELLE 1:1	SWITCH AV FEUILLE 6 / 7	

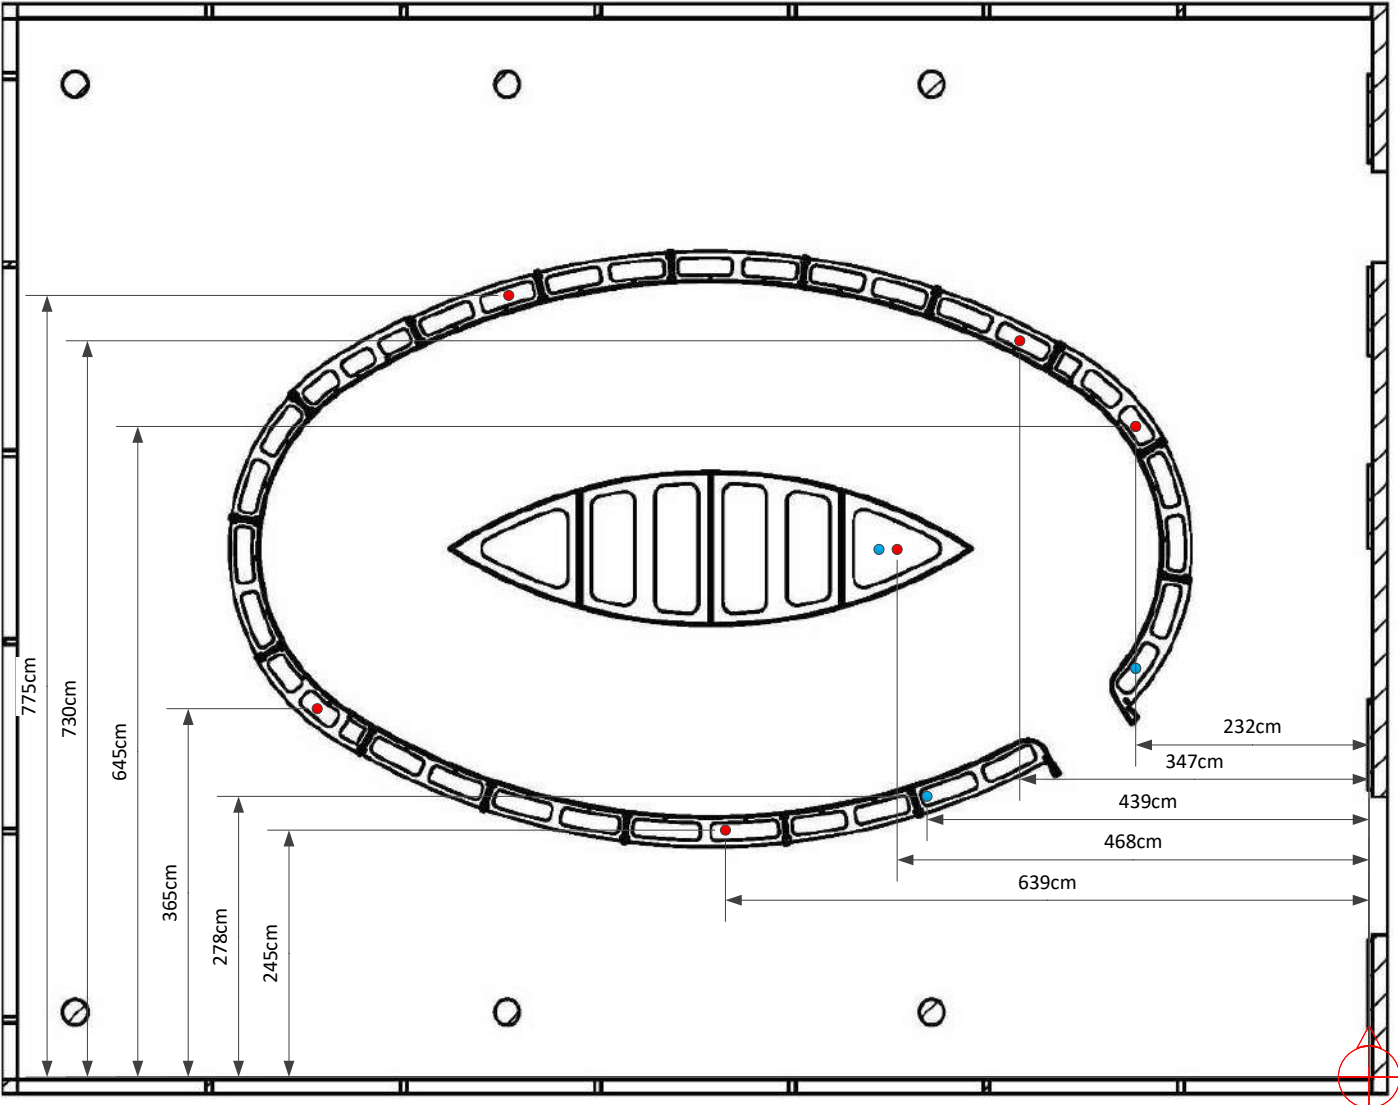

BAIE
AV

PERCEMENT
POUR
ALIMENTATION

PERCEMENT
POUR RJ 45

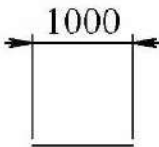

Indice	Date	Modifications		Visa
Tolérance générale Tolerie : NF-E 02-352 (n)		Tol. gén. menuiserie : +/- 1mm	Tol. gén. plasturgie : +/- 0.2mm hors épaisseurs	
Echelle: 1:75		Format: A3	Matière: Voir nomenclature	Masse (g): 100831799.1 Date:

Za les portes de l'Oise
Batiment B2
rue Henri Becquerel
60230 CHAMBLY
Tel : 01 75 01 60 40
Fax : 01 75 01 60 41
t.fourmentraux@videosonic.fr

Groupama Olivet - Salle du conseil - Synoptique d'exécution v2.vsd

Thierry FOURMENTRAUX	DIMENSION A3	N° CODE	PAGE tracé de sol	RÉV 30/01/2026
30/01/2026	ECHELLE	1:75	FEUILLE	7 / 7