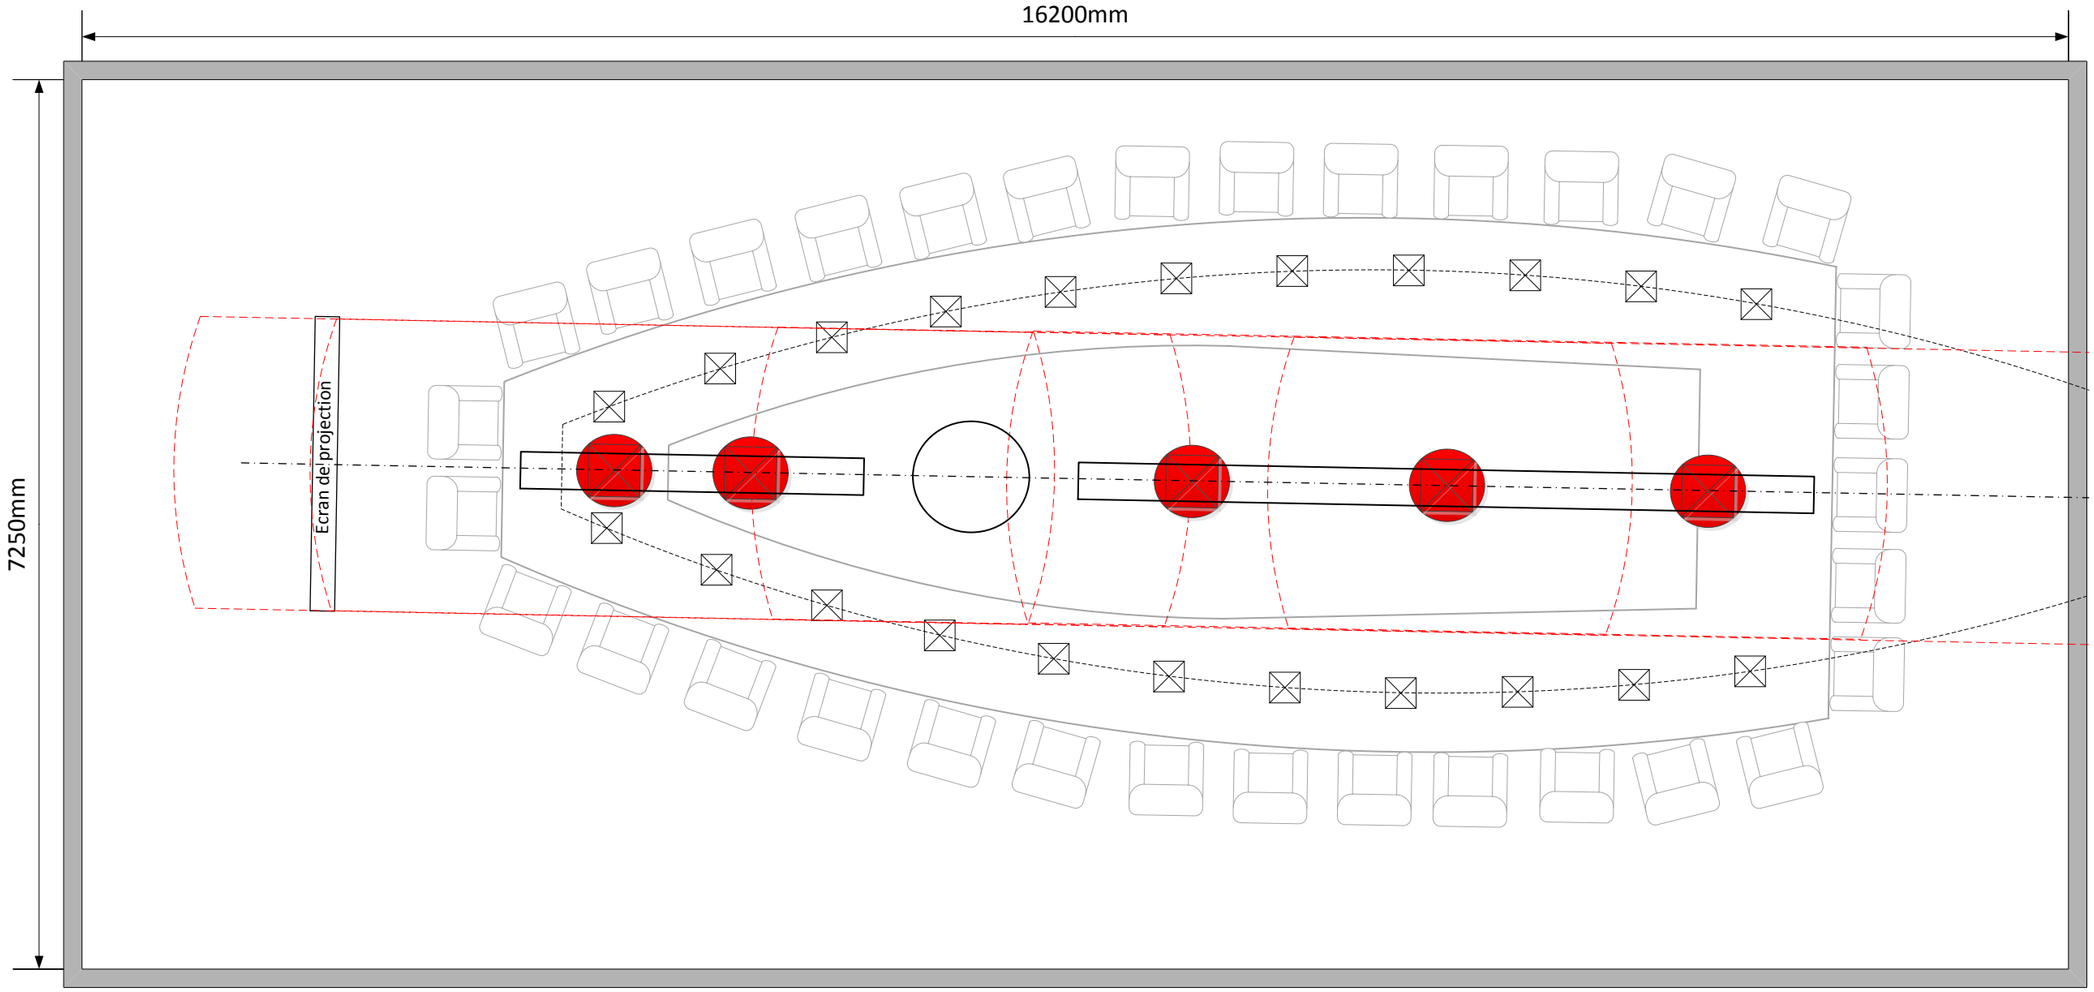

Hauteur sous plafond : 268cm

Diffusion sonore existante

Plafonnier encastré existants

Haut Parleurs Existants

VIDEOSONIC
Image, Son & Technique
Za les portes de l'Oise
Batîment B2 – rue Henri
Becquerel
60230 CHAMBLY
Tel : 01 75 01 60 40
Fax : 01 75 01 60 41
@ : contact@videosonic.fr

FNCA - Boetie

Diffusion sonore actuelle

Billot M	DIMENSION			RÉV
12/05/2017	ECHELLE 1:50		FEUILLE 1 / 4	

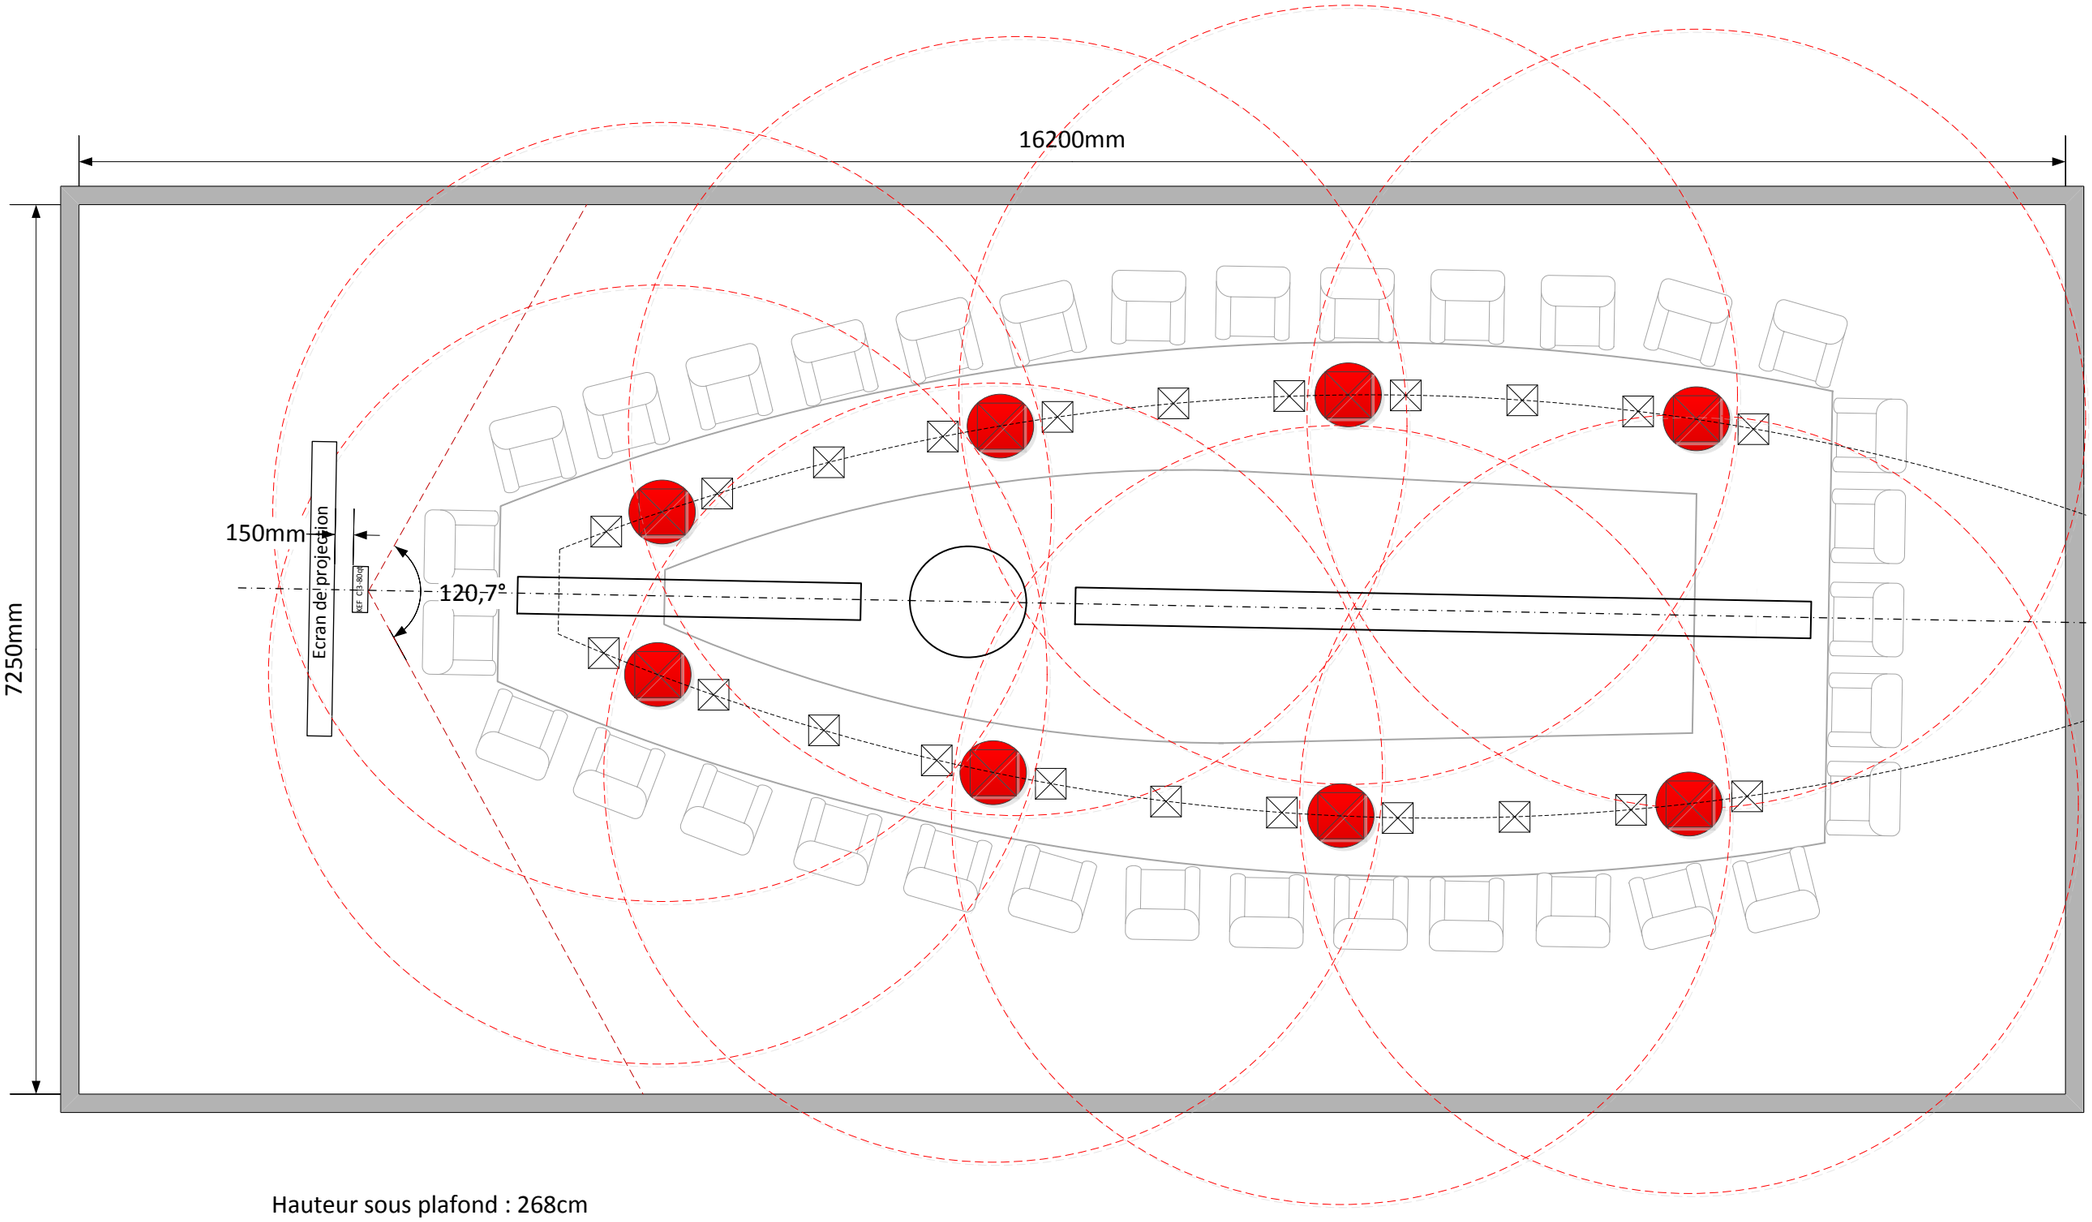

Hauteur sous plafond : 268cm

Diffusion su son entre 500Hz et 4kHz à hauteur d'oreilles (1.20m par rapport au sol)

Plafonnier encastré existants

Haut Parleur Yamaha VXC4W

Haut Parleur KEF Ci3-80qt

VIDEOSONIC
Image, Son & Technique
Za les portes de l'Oise
Batîment B2 – rue Henri Becquerel
60230 CHAMBLY
Tel : 01 75 01 60 40
Fax : 01 75 01 60 41
@ : contact@videosonic.fr

FNCA - Boetie	
Projet : Plan de diffusion sonore	
Billot M	DIMENSION / RÉV
12/05/2017	ECHELLE 1:50 / FEUILLE 2 / 4

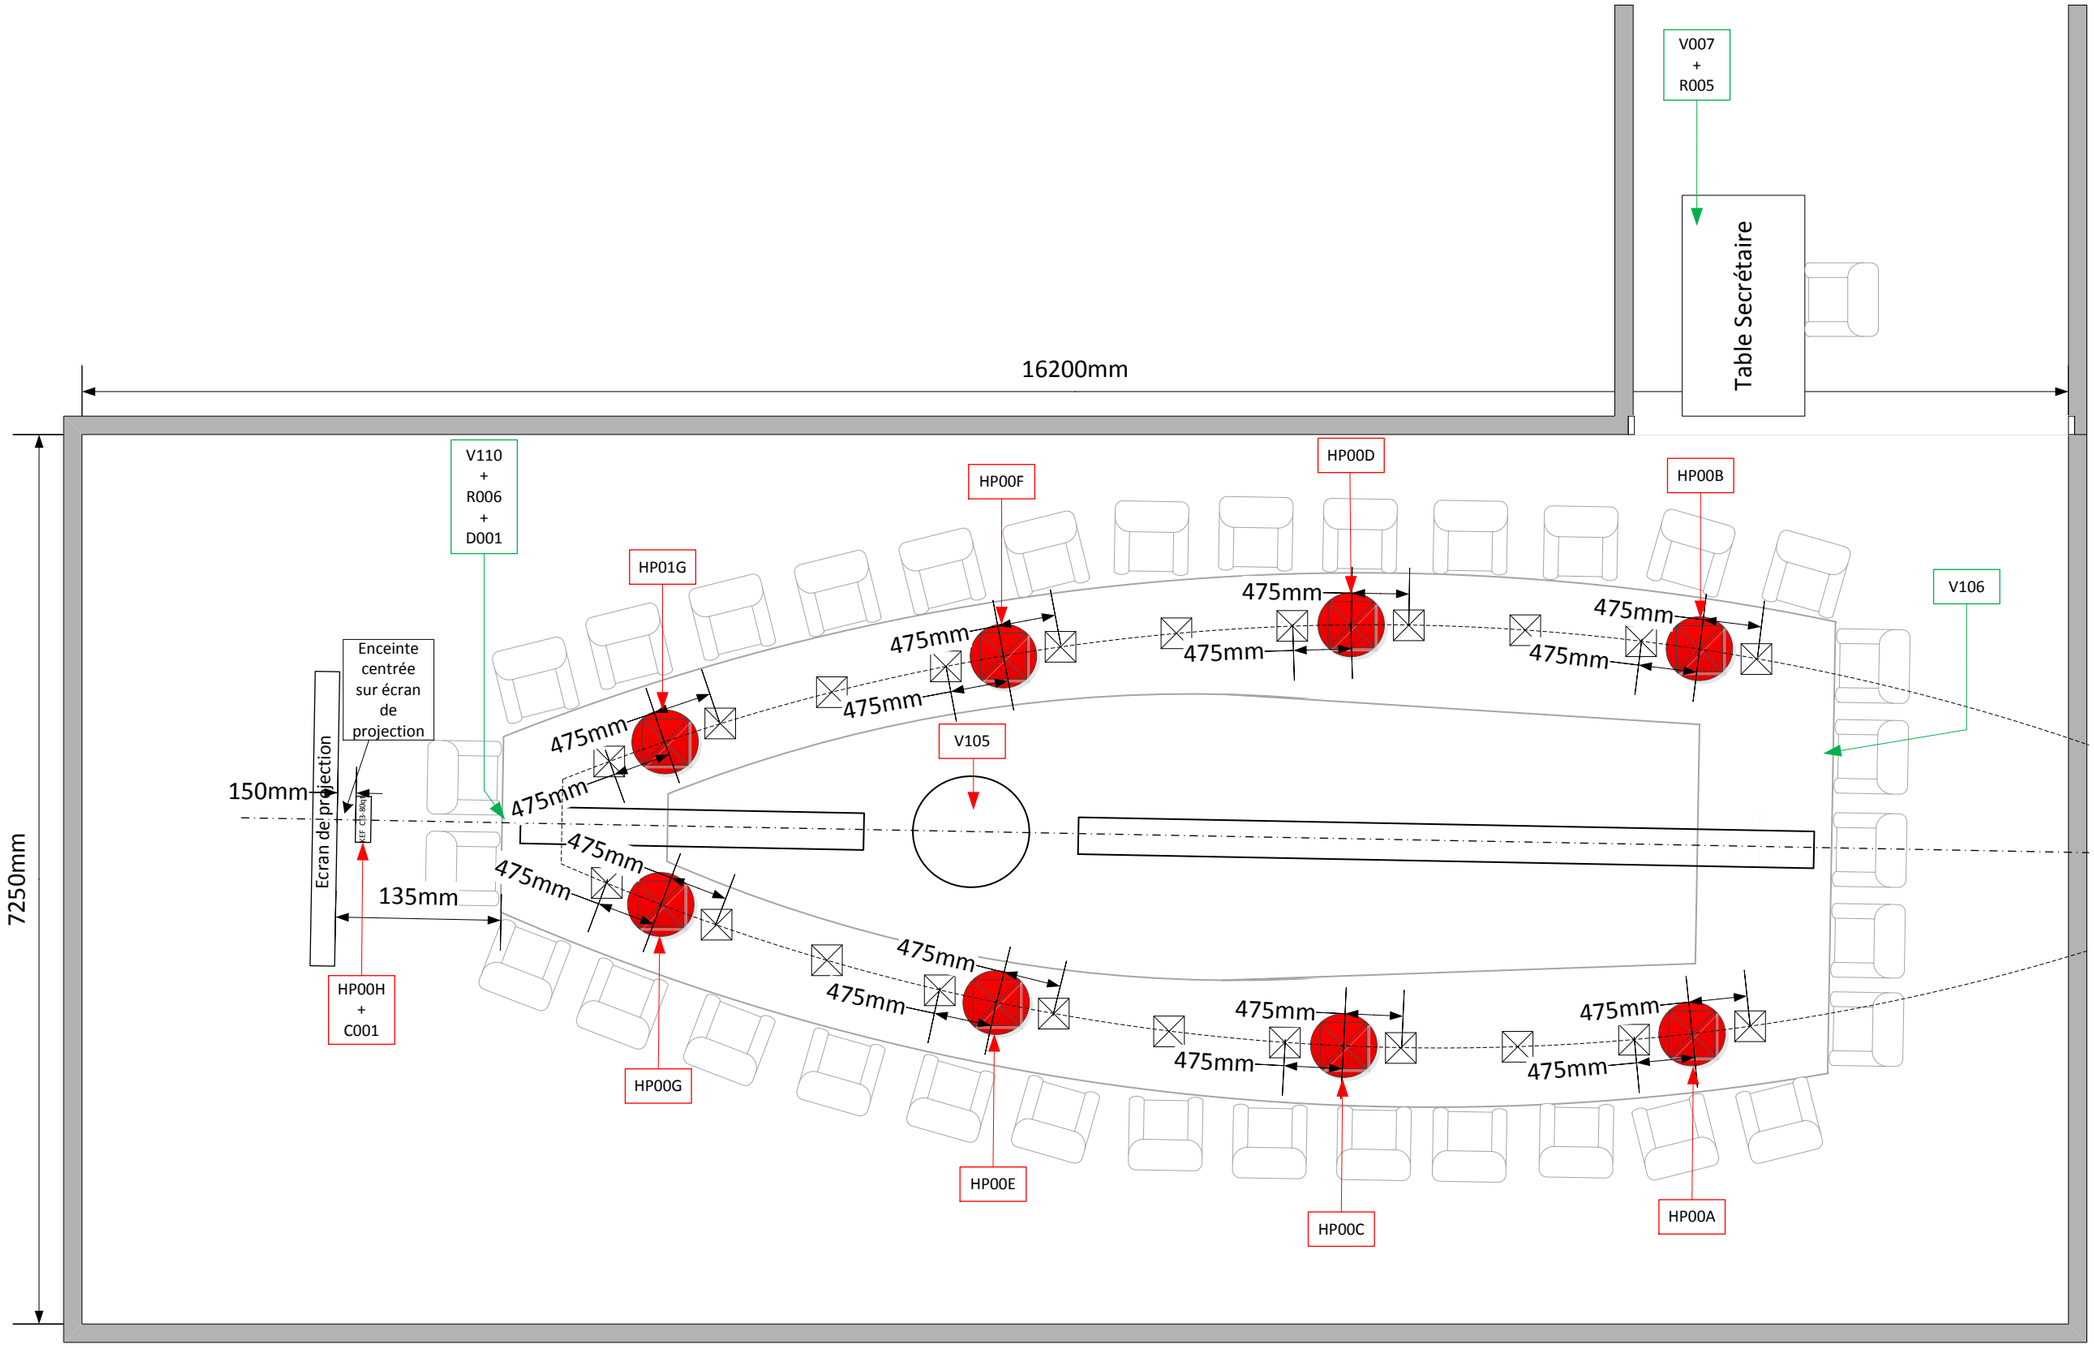

N°Cable — Arrivée câble Plafond

N°Cable — Arrivée câble dans table

Hauteur sous plafond : 268cm

Plafonnier encastré existants

Haut Parleur Yamaha VXC4W -> **Diamètre de perçage : 186mm**

Haut Parleur KEF Ci3-80qt -> **Perçage : 354x112mm**

VIDEOSONIC
Image, Son & Technique
Za les portes de l'Oise
Batîment B2 – rue Henri Becquerel
60230 CHAMBLY
Tel : 01 75 01 60 40
Fax : 01 75 01 60 41
@ : contact@videosonic.fr

FNCA - Boetie

Projet : Plan d'implantation AV + Câblage

Billot M	DIMENSION			RÉV
12/05/2017	ECHELLE	1:50	FEUILLE	3 / 4