Salle Boetie

Synoptiques Audio Video & Contrôle

Za les portes de l'Oise
Batîment B2 – rue Henri Becquerel
60230 CHAMBLY
Tel : 01 75 01 60 40
Fax : 01 75 01 60 41
t.fourmentraux@videosonic.fr

FOURMENTRAUX Thierry

25/11/2024

BOETIE

FNCA

DIMENSION		PLAN DE SALLE	RÉV
			1
ECHELLE 1:1			FEUILLE 1 / 6

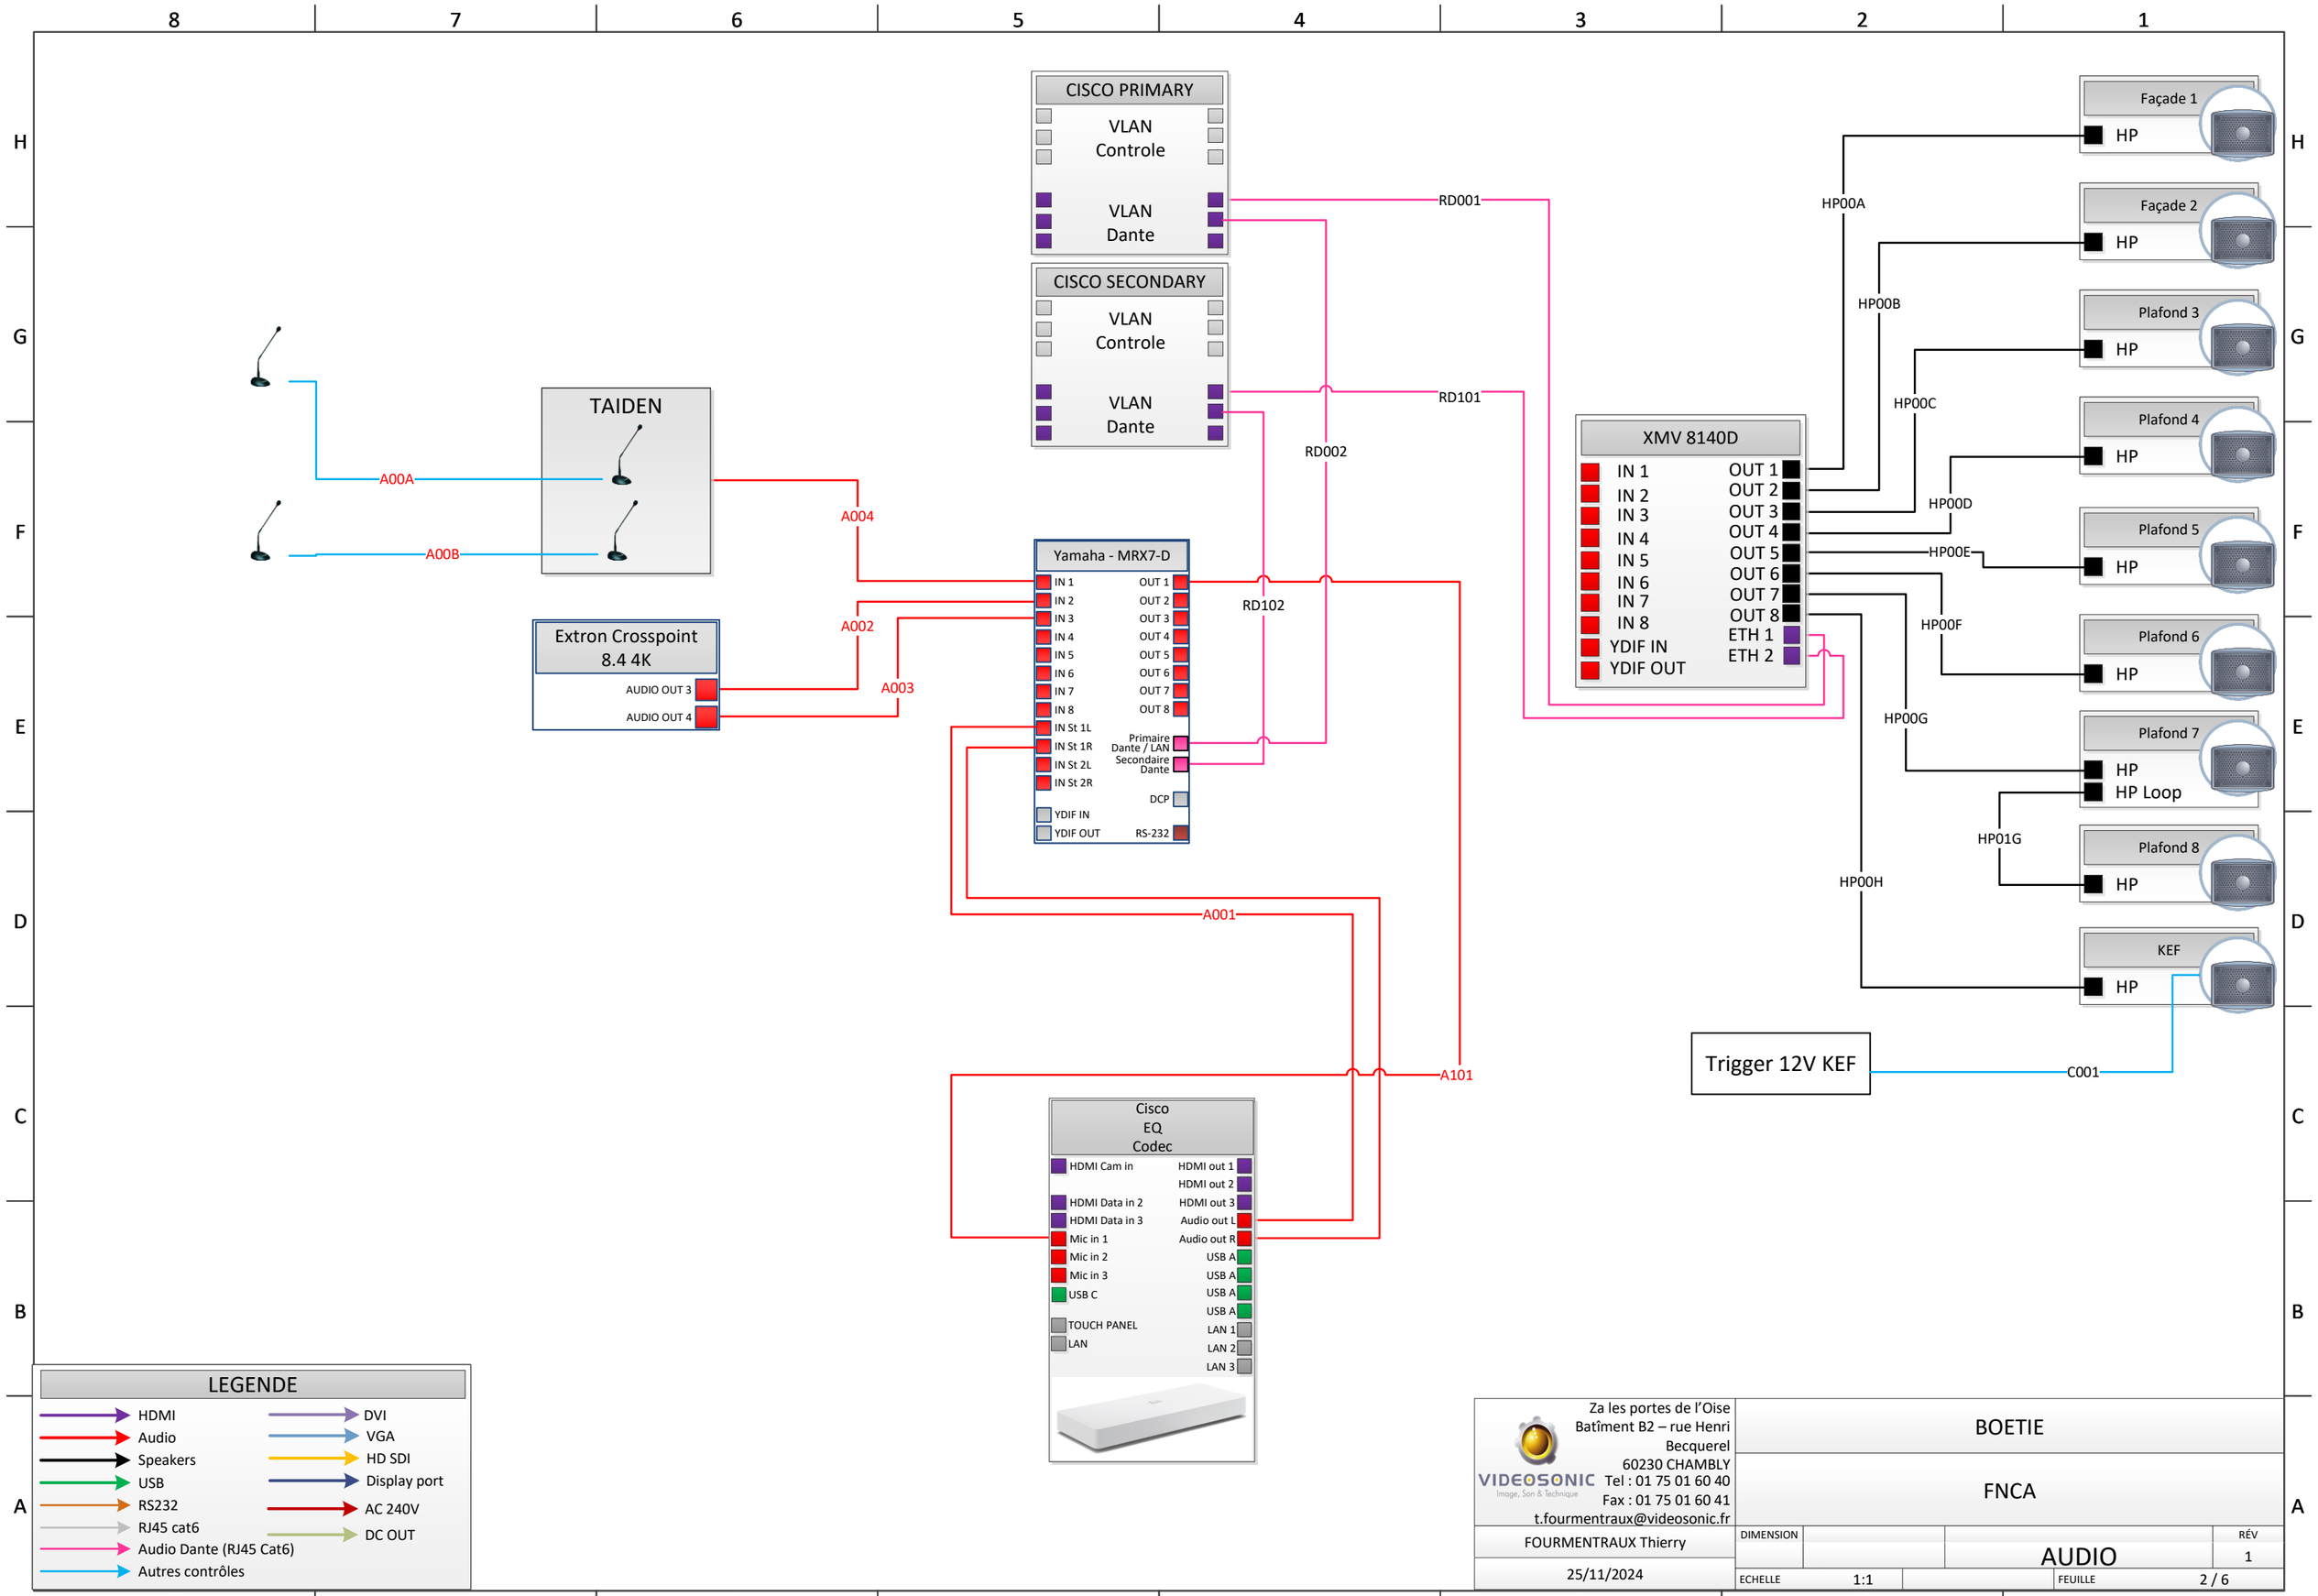
CISCO PRIMARY
VLAN Controle
VLAN Dante
CISCO SECONDARY
VLAN Controle
VLAN Dante
TAIDEN
A00A
A00B
Extron Crosspoint 8.4 4K
AUDIO OUT 3
AUDIO OUT 4
A004
A002
A003
Yamaha - MRX7-D
IN 1
IN 2
IN 3
IN 4
IN 5
IN 6
IN 7
IN 8
IN St 1L
IN St 1R
IN St 2L
IN St 2R
YDIF IN
YDIF OUT
OUT 1
OUT 2
OUT 3
OUT 4
OUT 5
OUT 6
OUT 7
OUT 8
Primaire Dante / LAN
Secondaire Dante
DCP
RS-232
RD001
RD002
RD101
RD102
A001
A101
Cisco EQ Codec
HDMI Cam in
HDMI Data in 2
HDMI Data in 3
Mic in 1
Mic in 2
Mic in 3
USB C
TOUCH PANEL
LAN
HDMI out 1
HDMI out 2
HDMI out 3
Audio out L
Audio out R
USB A
USB A
USB A
USB A
LAN 1
LAN 2
LAN 3
XMV 8140D
IN 1
IN 2
IN 3
IN 4
IN 5
IN 6
IN 7
IN 8
YDIF IN
YDIF OUT
OUT 1
OUT 2
OUT 3
OUT 4
OUT 5
OUT 6
OUT 7
OUT 8
ETH 1
ETH 2
HP00A
HP00B
HP00C
HP00D
HP00E
HP00F
HP00G
HP01G
HP00H
Façade 1
HP
Façade 2
HP
Plafond 3
HP
Plafond 4
HP
Plafond 5
HP
Plafond 6
HP
Plafond 7
HP
HP Loop
Plafond 8
HP
KEF
HP
Trigger 12V KEF
C001
LEGENDE
HDMI
Audio
Speakers
USB
RS232
RJ45 cat6
Audio Dante (RJ45 Cat6)
Autres contrôles
DVI
VGA
HD SDI
Display port
AC 240V
DC OUT
VIDEOSONIC
Image, Son & Technique
Za les portes de l'Oise
Batîment B2 – rue Henri Becquerel
60230 CHAMBLY
Tel : 01 75 01 60 40
Fax : 01 75 01 60 41
t.fourmentraux@videosonic.fr
FOURMENTRAUX Thierry
25/11/2024
BOETIE
FNCA
DIMENSION
AUDIO
RÉV
1
ECHELLE
1:1
FEUILLE
2 / 6

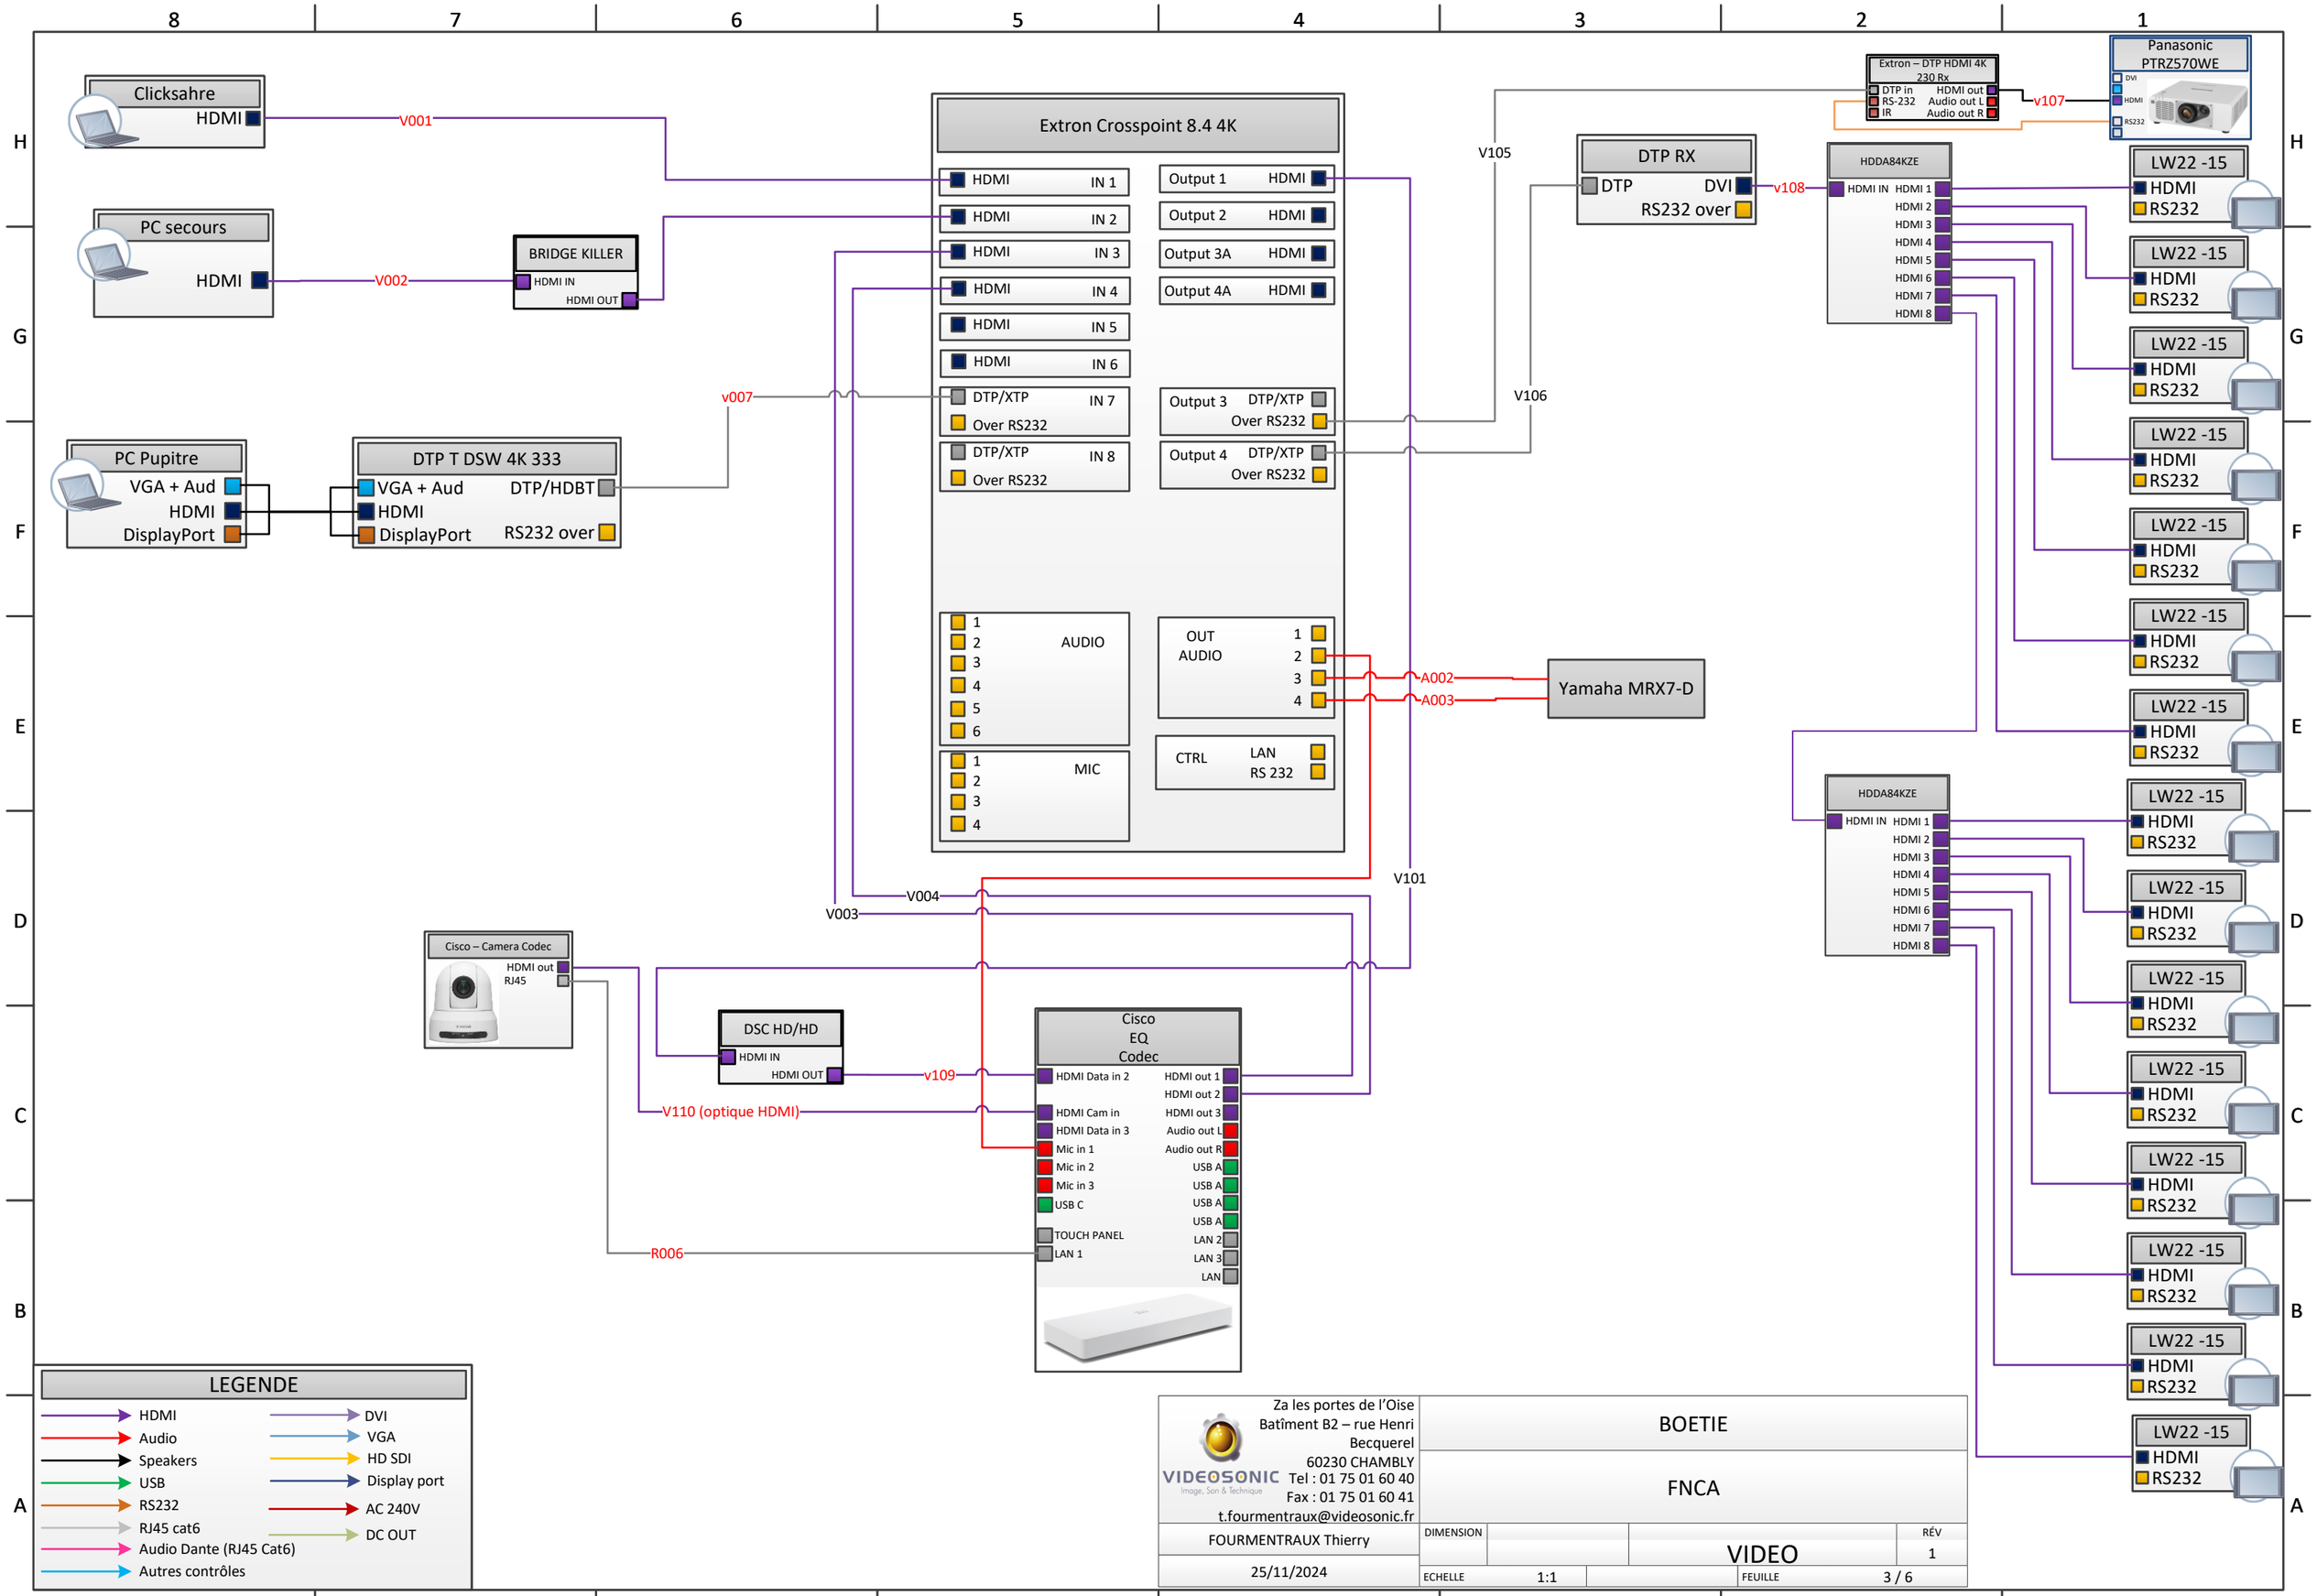
Clicksahre
HDMI
V001
PC secours
HDMI
V002
BRIDGE KILLER
HDMI IN
HDMI OUT
PC Pupitre
VGA + Aud
HDMI
DisplayPort
DTP T DSW 4K 333
VGA + Aud
HDMI
DisplayPort
DTP/HDBT
RS232 over
v007
Extron Crosspoint 8.4 4K
HDMI IN 1
HDMI IN 2
HDMI IN 3
HDMI IN 4
HDMI IN 5
HDMI IN 6
DTP/XTP IN 7
Over RS232
DTP/XTP IN 8
Over RS232
Output 1 HDMI
Output 2 HDMI
Output 3A HDMI
Output 4A HDMI
Output 3 DTP/XTP
Over RS232
Output 4 DTP/XTP
Over RS232
AUDIO
OUT AUDIO
MIC
CTRL
LAN
RS 232
V105
V106
V101
A002
A003
Yamaha MRX7-D
V004
V003
Cisco – Camera Codec
HDMI out
RJ45
DSC HD/HD
HDMI IN
HDMI OUT
v109
V110 (optique HDMI)
R006
Cisco
EQ
Codec
HDMI Data in 2
HDMI Cam in
HDMI Data in 3
Mic in 1
Mic in 2
Mic in 3
USB C
TOUCH PANEL
LAN 1
HDMI out 1
HDMI out 2
HDMI out 3
Audio out L
Audio out R
USB A
LAN 2
LAN 3
LAN
DTP RX
DTP
DVI
RS232 over
v108
Extron – DTP HDMI 4K 230 Rx
DTP in
RS-232
IR
HDMI out
Audio out L
Audio out R
v107
Panasonic
PTRZ570WE
HDDA84KZE
HDMI IN
HDMI 1
HDMI 2
HDMI 3
HDMI 4
HDMI 5
HDMI 6
HDMI 7
HDMI 8
LW22 -15
HDMI
RS232
LEGENDE
HDMI
Audio
Speakers
USB
RS232
RJ45 cat6
Audio Dante (RJ45 Cat6)
Autres contrôles
DVI
VGA
HD SDI
Display port
AC 240V
DC OUT
Za les portes de l'Oise
Batîment B2 – rue Henri
Becquerel
60230 CHAMBLY
Tel : 01 75 01 60 40
Fax : 01 75 01 60 41
t.fourmentraux@videosonic.fr
VIDEOSONIC
Image, Son & Technique
FOURMENTRAUX Thierry
25/11/2024
BOETIE
FNCA
DIMENSION
RÉV
1
VIDEO
ECHELLE
1:1
FEUILLE
3 / 6

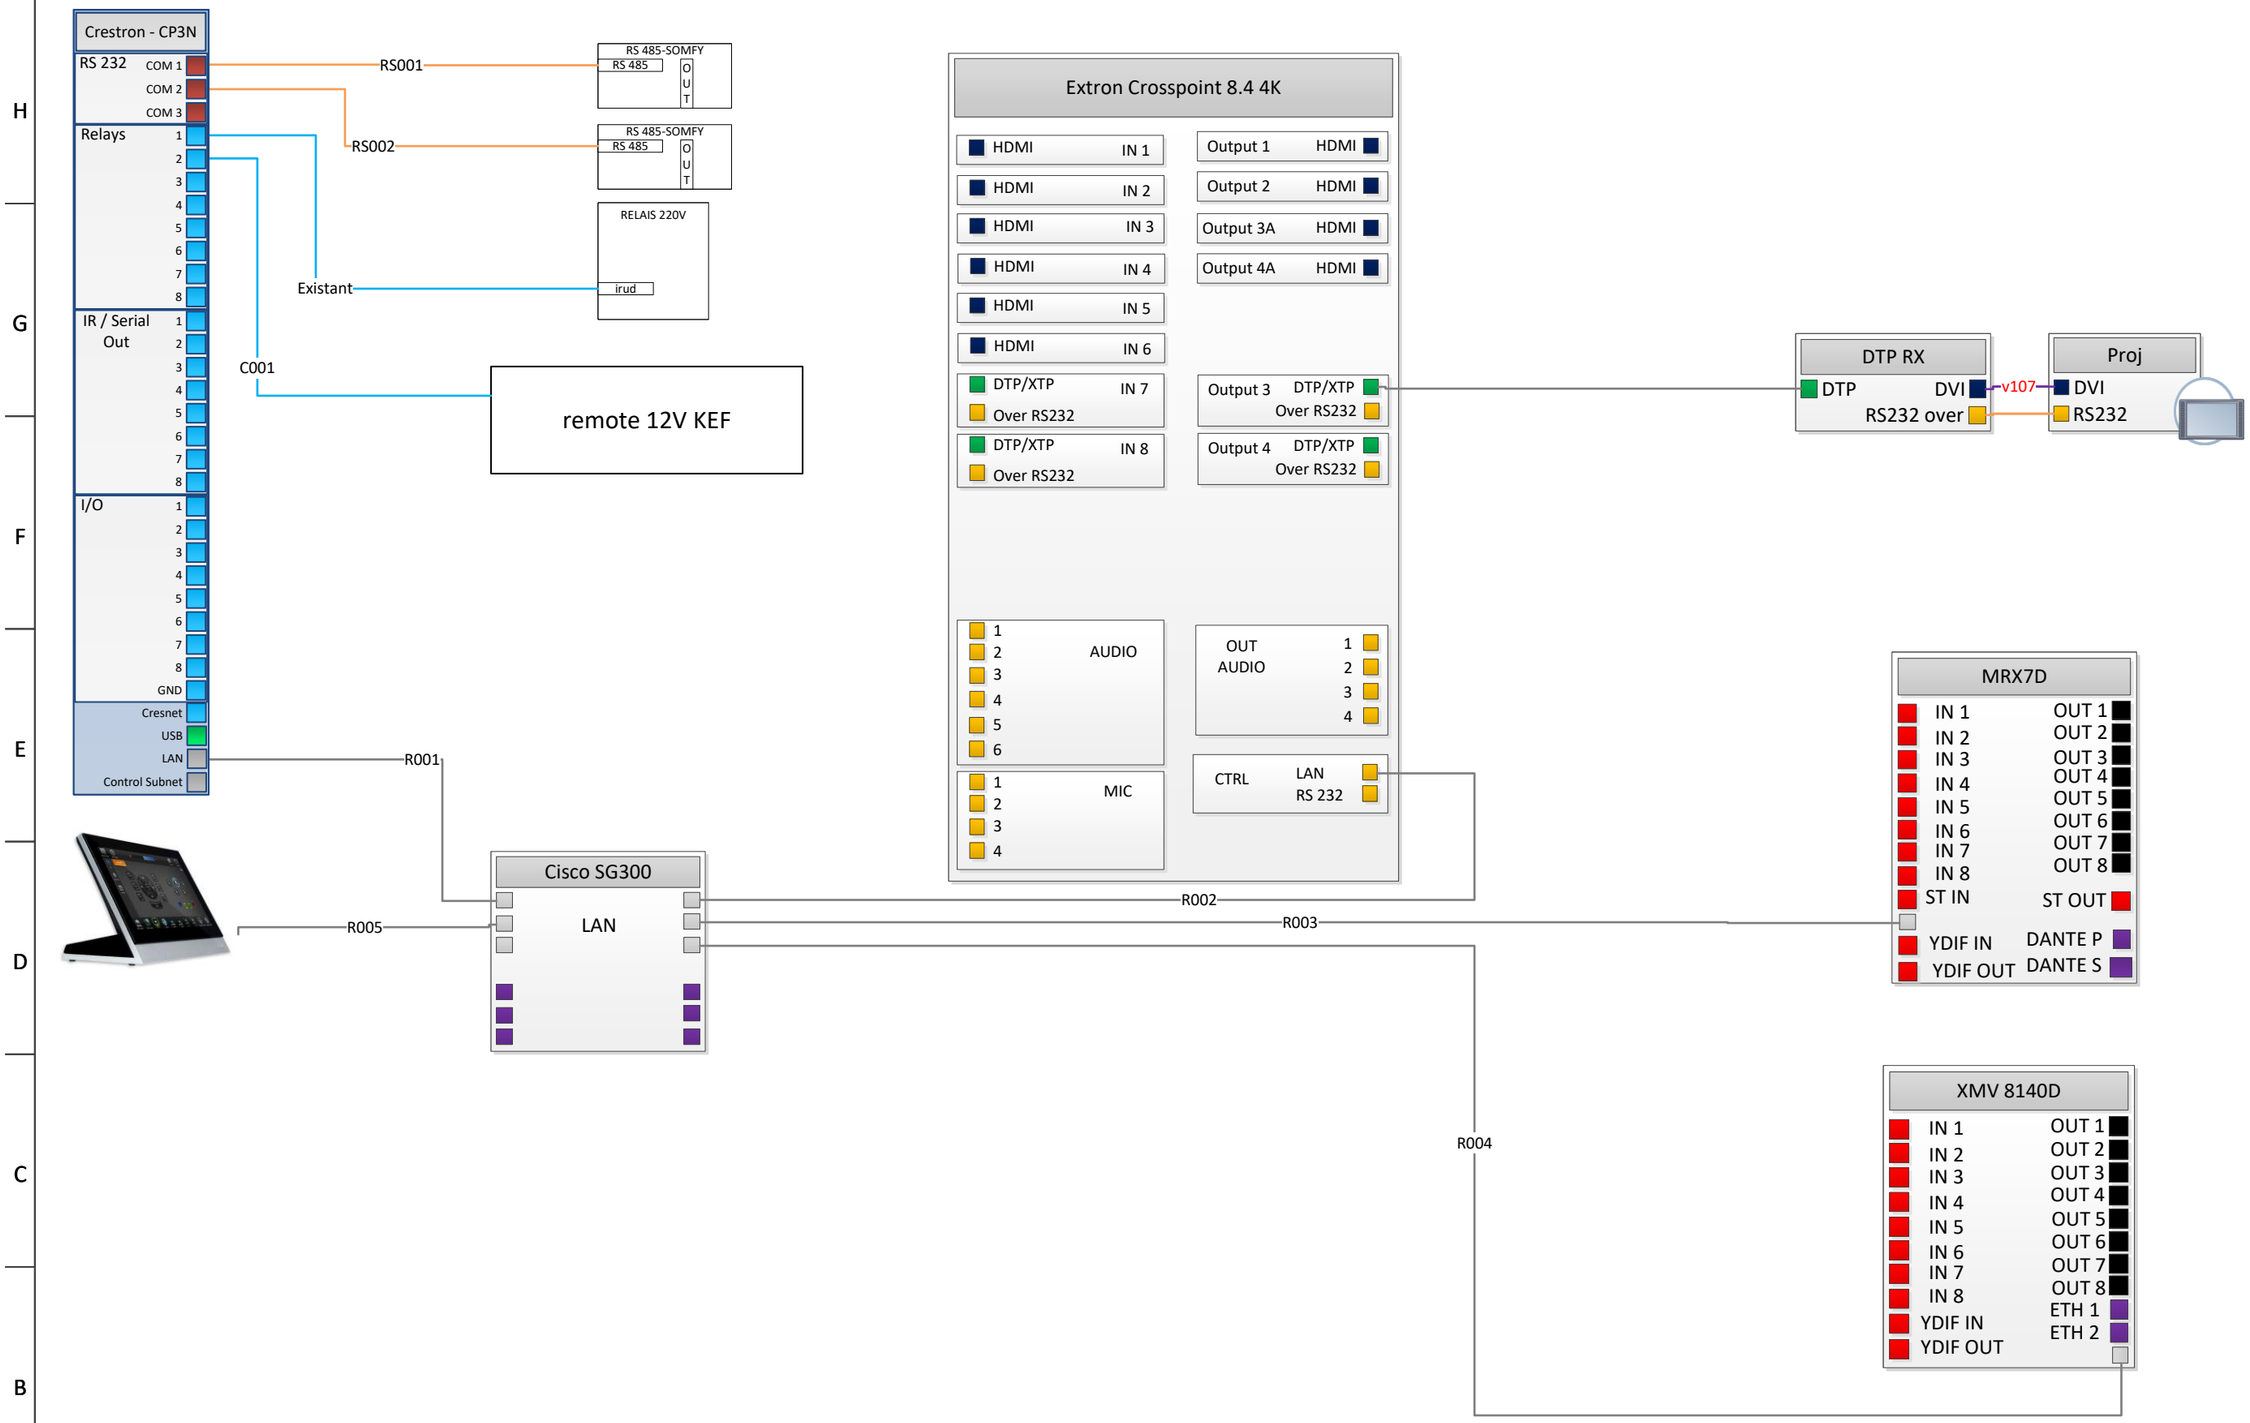

VIDEOSONIC
Image, Son & Technique
Za les portes de l'Oise
Batîment B2 – rue Henri Becquerel
60230 CHAMBLY
Tel : 01 75 01 60 40
Fax : 01 75 01 60 41
t.fourmentraux@videosonic.fr
FOURMENTRAUX Thierry

25/11/2024

BOETIE

FNCA

CONTRÔLE

DIMENSION		RÉV
		1
ECHELLE 1:1		FEUILLE 4 / 6

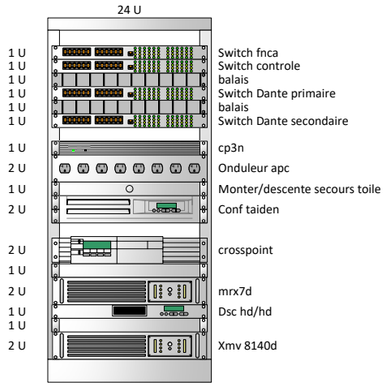

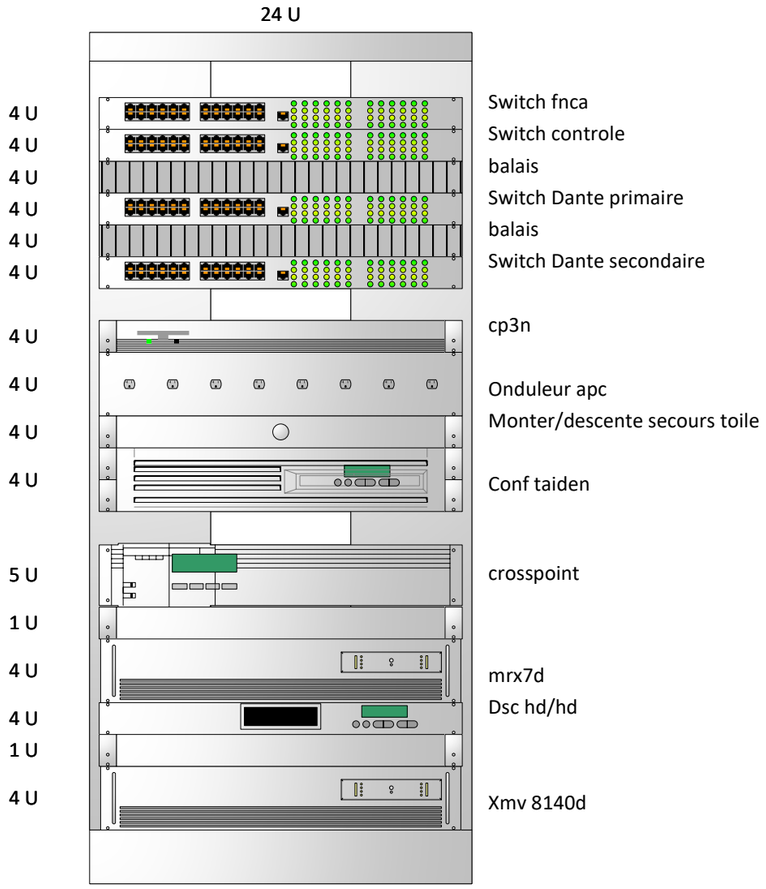

VIDEOSONIC
Image, Son & Technique
Za les portes de l'Oise
Batîment B2 – rue Henri Becquerel
60230 CHAMBLY
Tel : 01 75 01 60 40
Fax : 01 75 01 60 41
t.fourmentraux@videosonic.fr
FOURMENTRAUX Thierry

25/11/2024

BOETIE

FNCA

DIMENSION		PLAN DE BAIE	RÉV
			1
ECHELLE 1:1			FEUILLE 5 / 6

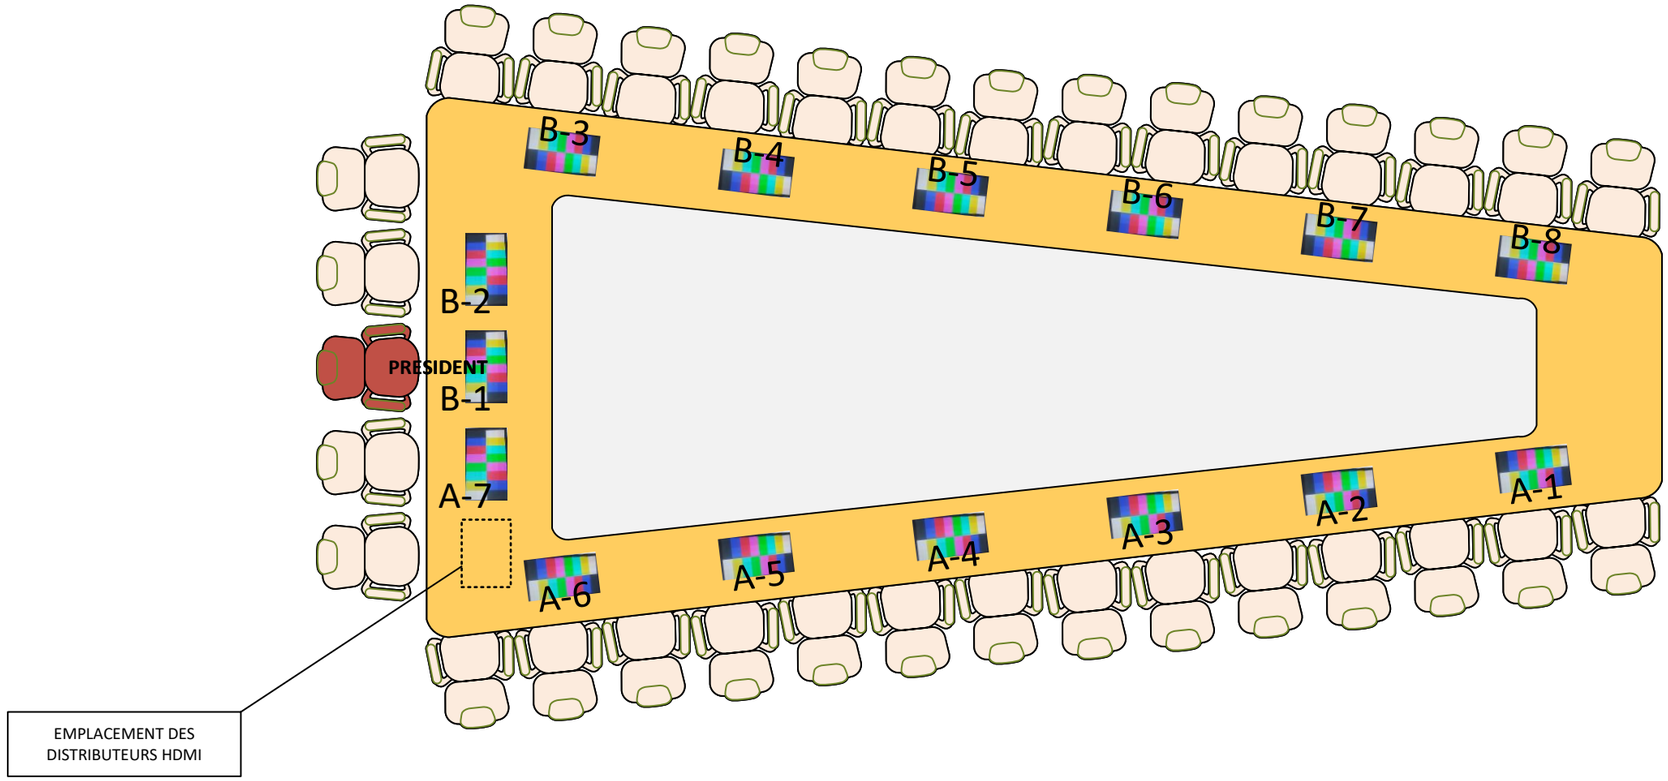

VIDEOSONIC
Image, Son & Technique
Za les portes de l'Oise
Batîment B2 – rue Henri Becquerel
60230 CHAMBLY
Tel : 01 75 01 60 40
Fax : 01 75 01 60 41
t.fourmentraux@videosonic.fr

FOURMENTRAUX Thierry

25/11/2024

DIMENSION		PLAN DE SALLE	RÉV 1
ECHELLE 1:50		FEUILLE 6 / 6	