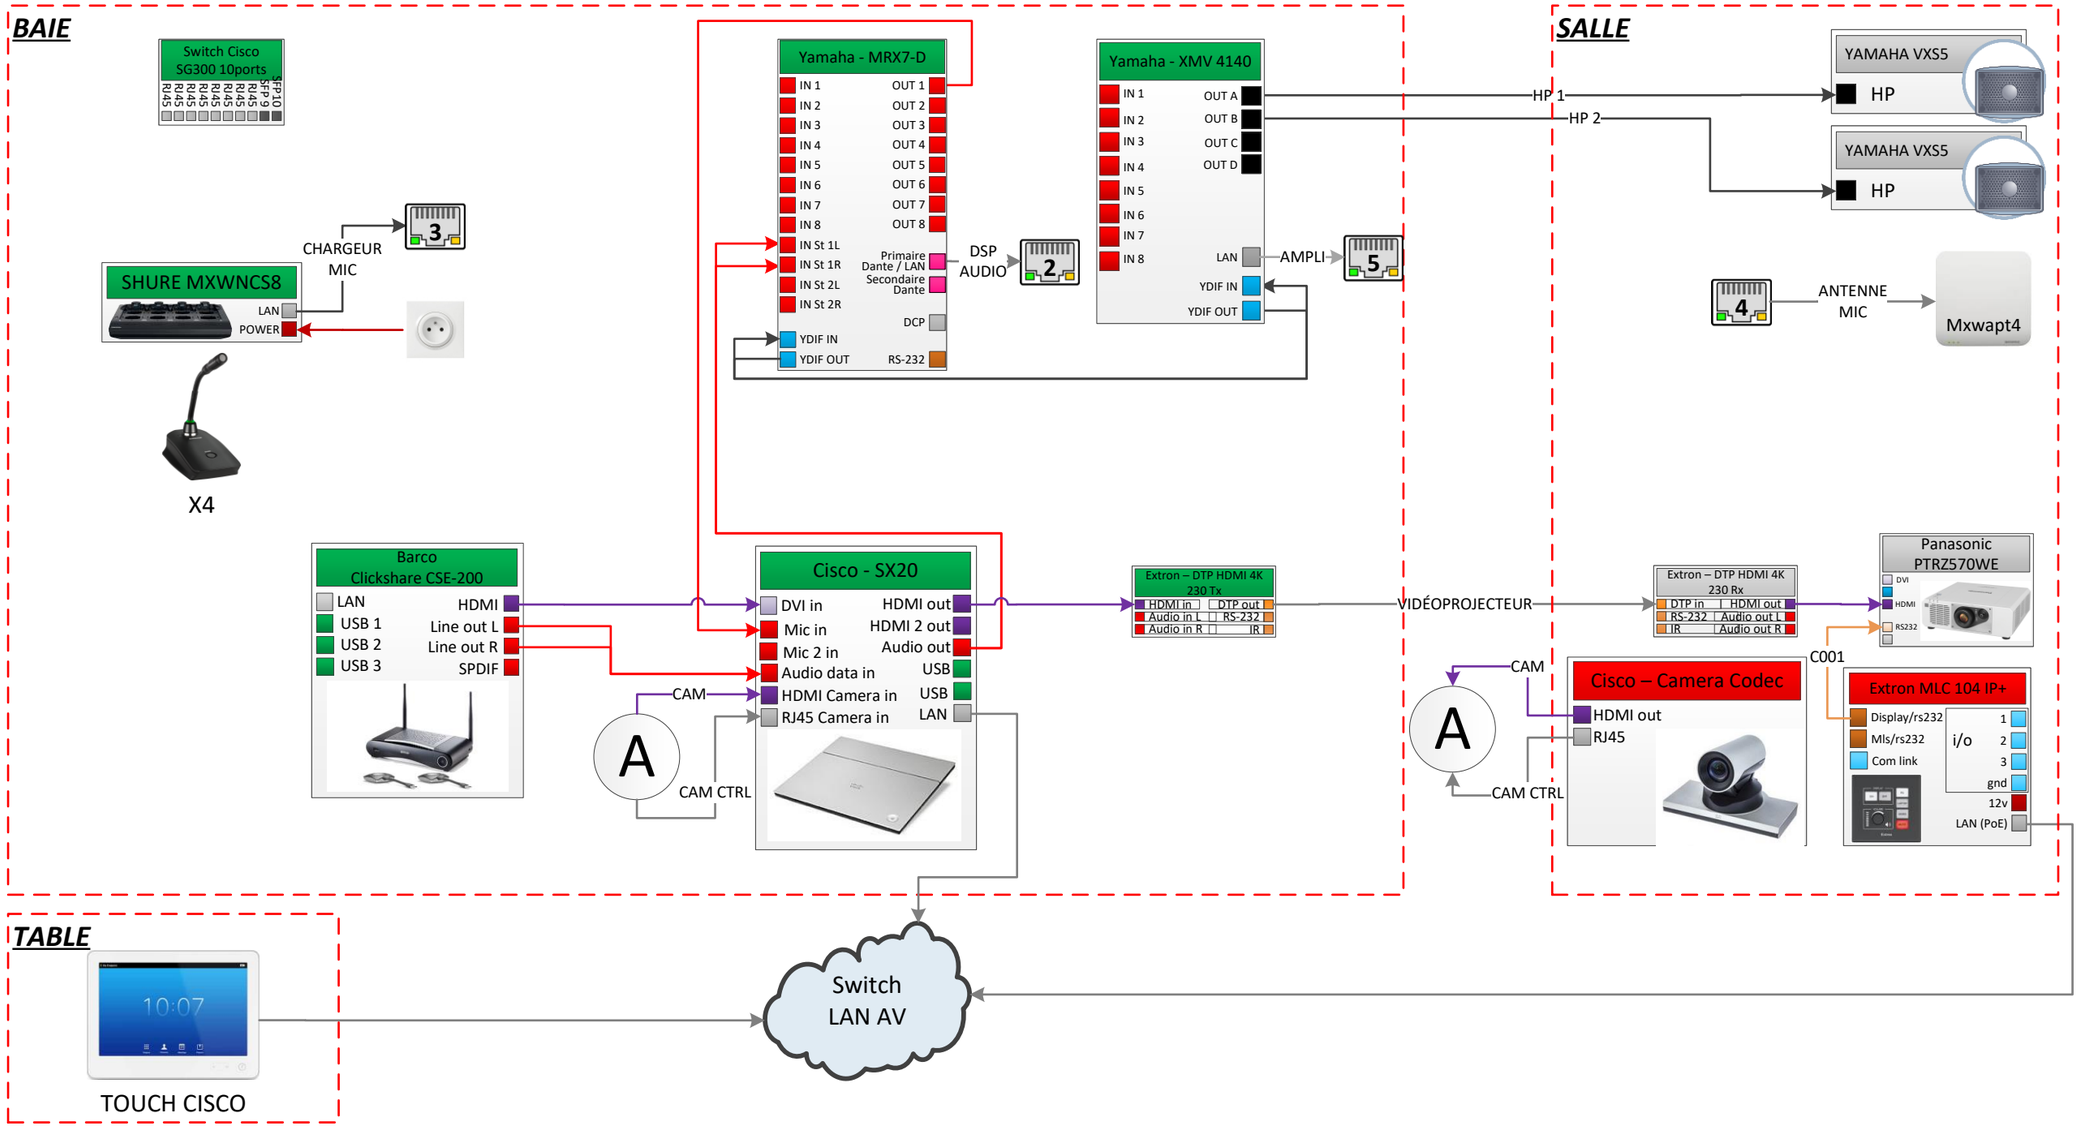

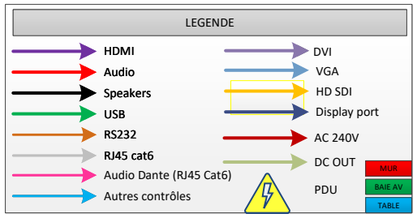

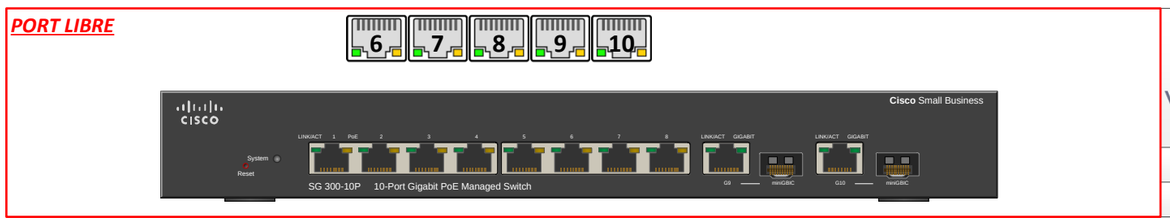

VIDEOSONIC
Image, Son & Technique
Za les portes de l'Oise
Batîment B2 – rue Henri Becquerel
60230 CHAMBLY
Tel : 01 75 01 60 40
Fax : 01 75 01 60 41
t.fourmentraux@videosonic.fr

FOURMENTRAUX Thierry

27/02/2025

Salle ANJOU

GIFECAM 48 Rue de la Boétie
75008 PARIS

DIMENSION			RÉV
A3		SYNOPTIQUE AVC	1
ECHELLE 1:1		FEUILLE 1 / 2	

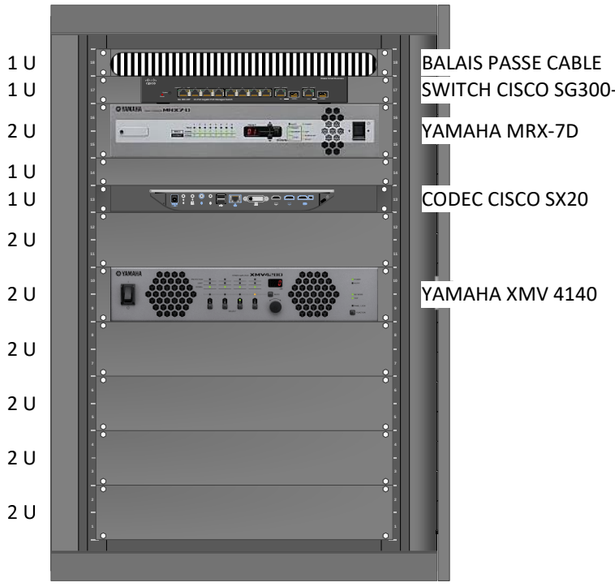

Za les portes de l'Oise
Batîment B2 – rue Henri Becquerel
60230 CHAMBLY
Tel : 01 75 01 60 40
Fax : 01 75 01 60 41
t.fourmentraux@videosonic.fr

Salle ANJOU

GIFECAM 48 Rue de la Boétie
75008 PARIS

FOURMENTRAUX Thierry	DIMENSION A3	PLAN DE BAIE	RÉV 1
27/02/2025	ECHELLE 1:10		FEUILLE 2 / 2