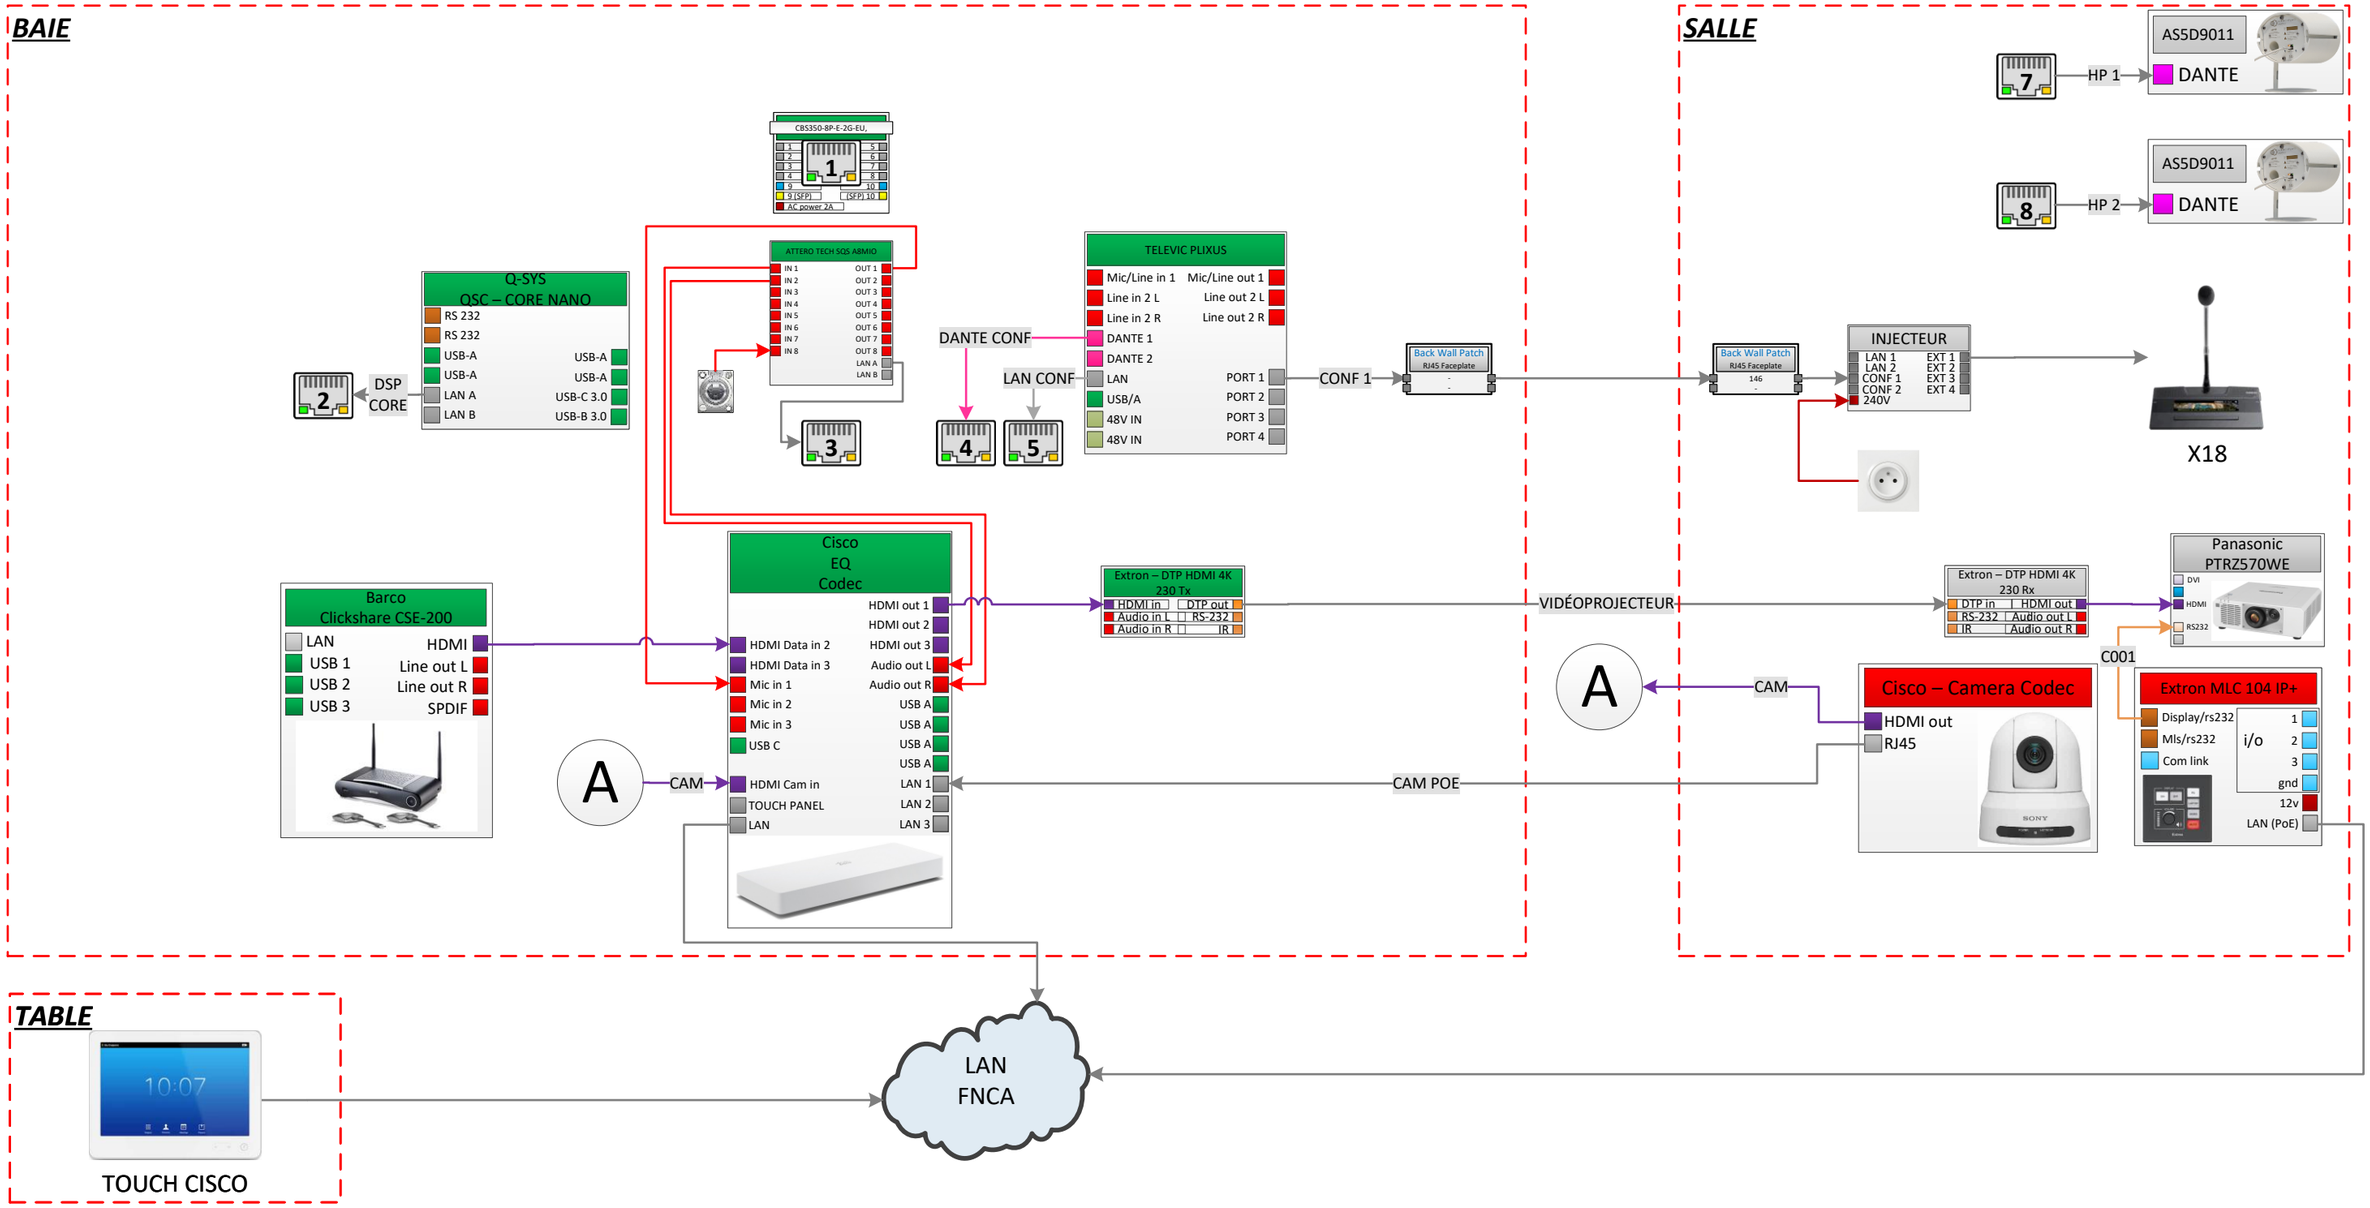

LEGENDE	
HDMI	DVI
Audio	VGA
Speakers	HD SDI
USB	Display port
RS232	AC 240V
RJ45 cat6	DC OUT
Audio Dante (RJ45 Cat6)	PDU
Autres contrôles	MUR / BAIE AV / TABLE

PORT LIBRE

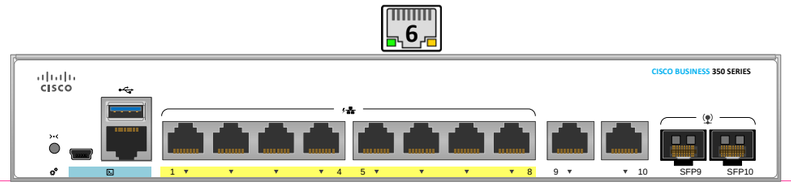

VIDEOSONIC
Image, Son & Technique
Za les portes de l'Oise
Batîment B2 – rue Henri Becquerel
60230 CHAMBLY
Tel : 01 75 01 60 40
Fax : 01 75 01 60 41
t.fourmentraux@videosonic.fr
FOURMENTRAUX Thierry

13/03/2025

Salle Alsace

GIFECAM 48 Rue de la Boétie
75008 PARIS

DIMENSION	RÉV
A3	1

ECHELLE	1:1	FEUILLE	1 / 2

BAIE AV 22U
4122

1 U	BALAIS PASSE CABLE
1 U	SWITCH CBS350-8P-E-2G-EU,
1 U	
1 U	CORE NANO+CLICKSHARE CSE200
1 U	CONF TELEVIC PLIXUS AE-R
1 U	ATTEROTECH A8MIO+ ALIM+ DTP TX 230 HDMI
1 U	ALIM CISCO CODEC EQ
1 U	CISCO CODEC EQ
1 U	IN AUX
4 U	
4 U	
4 U	

VIDEOSONIC
Image, Son & Technique
Za les portes de l'Oise
Batîment B2 – rue Henri Becquerel
60230 CHAMBLY
Tel : 01 75 01 60 40
Fax : 01 75 01 60 41
t.fourmentraux@videosonic.fr
FOURMENTRAUX Thierry

13/03/2025

Salle Alsace

GIFECAM 48 Rue de la Boétie
75008 PARIS

DIMENSION			RÉV
A3		PLAN DE BAIE	1
ECHELLE 1:10		FEUILLE 2 / 2	