FNCA CHEGUT

Synoptiques Audio Video & Contrôle

Za les portes de l'Oise
Batîment B2 – rue Henri Becquerel
60230 CHAMBLY
Tel : 01 75 01 60 40
Fax : 01 75 01 60 41
@ : contact@videosonic.fr

FNCA CHEGUT 2015	
Videosonic	
DIMENSION	RÉV
Page Garde	1
02/02/2026	
ECHELLE 1:1	FEUILLE 1 / 8

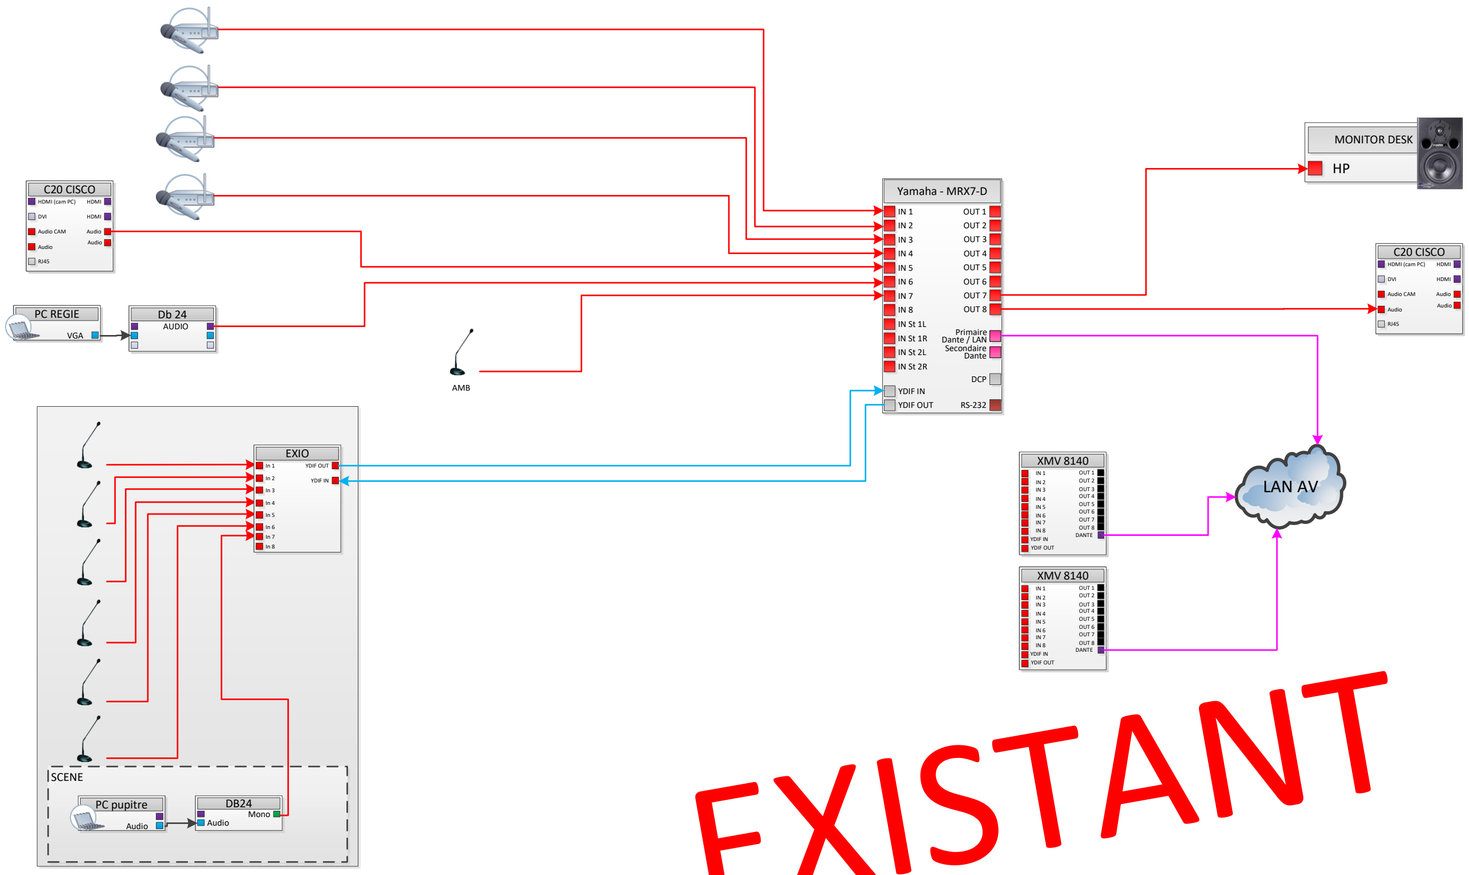

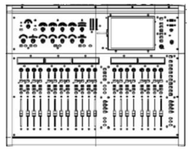

1 HF 1
2 HF 2
3
4
5 VISIO
6
7
8
9 AMBIANCE
10 PC SALLE
11 PC SALLE
12 CONF
13 CD
14 CD
15 GRILLE
16 GRILLE

AUX 1 FACADE
AUX 2 FACADE
AUX 3 PLAFOND
AUX 4 PLAFOND
MASTER VISIO

User avancé IPAD 1234
Admin: 5775

EXISTANT

LEGENDE

- HDMI
- Audio
- Speakers
- USB
- RS232
- RJ45 cat6
- Audio Dante (RJ45 Cat6)
- Autres contrôles
- DVI
- VGA
- HD SDI
- Display port
- AC 240V
- DC OUT

VIDEOSONIC
Image, Son & Technique

Za les portes de l'Oise
Batîment B2 – rue Henri Becquerel
60230 CHAMBLY

Tel : 01 75 01 60 40
Fax : 01 75 01 60 41
@ : contact@videosonic.fr

FNCA CHEGUT

Videosonic

audio CHEGUT

DIMENSION			RÉV 1
02/02/2026	ECHELLE 1:1		FEUILLE 2 / 8

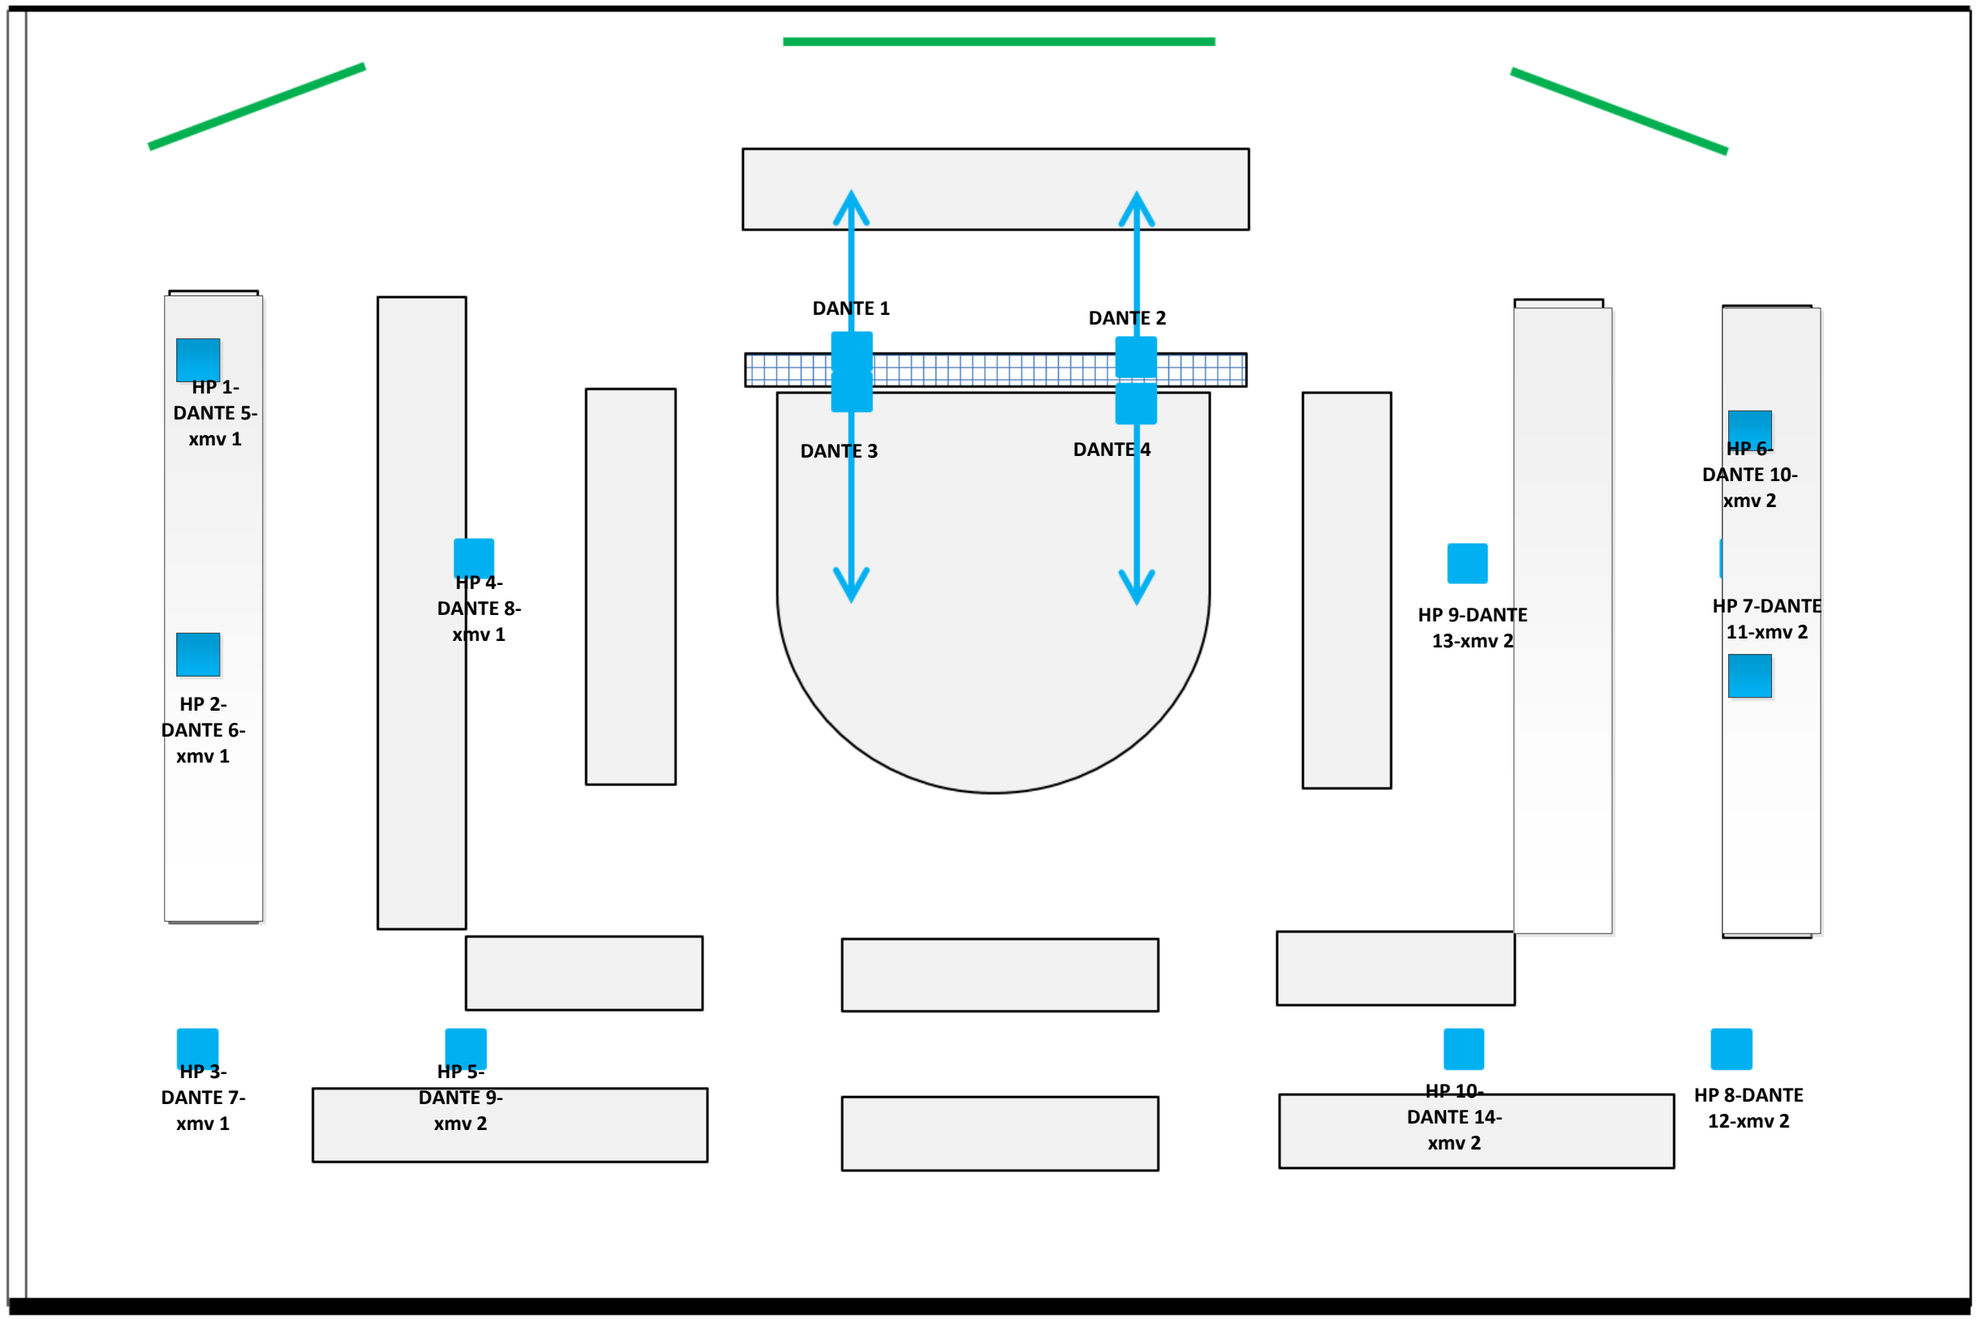

MRX 7D: 192.168.0.2 ID 1
EXI8: 192.168.0.1 ID 2
XMV1: 192.168.0.48 ID 30
XMV2: 192.168.0.49 ID 31

VIDEOSONIC
Image, Son & Technique
Za les portes de l'Oise
Batîment B2 – rue Henri Becquerel
60230 CHAMBLY
Tel : 01 75 01 60 40
Fax : 01 75 01 60 41
@ : contact@videosonic.fr

FNCA CHEGUT

Videosonic

DIMENSION			RÉV
		synoptique masse	1
ECHELLE 1:1		FEUILLE 3 / 8	

02/02/2026

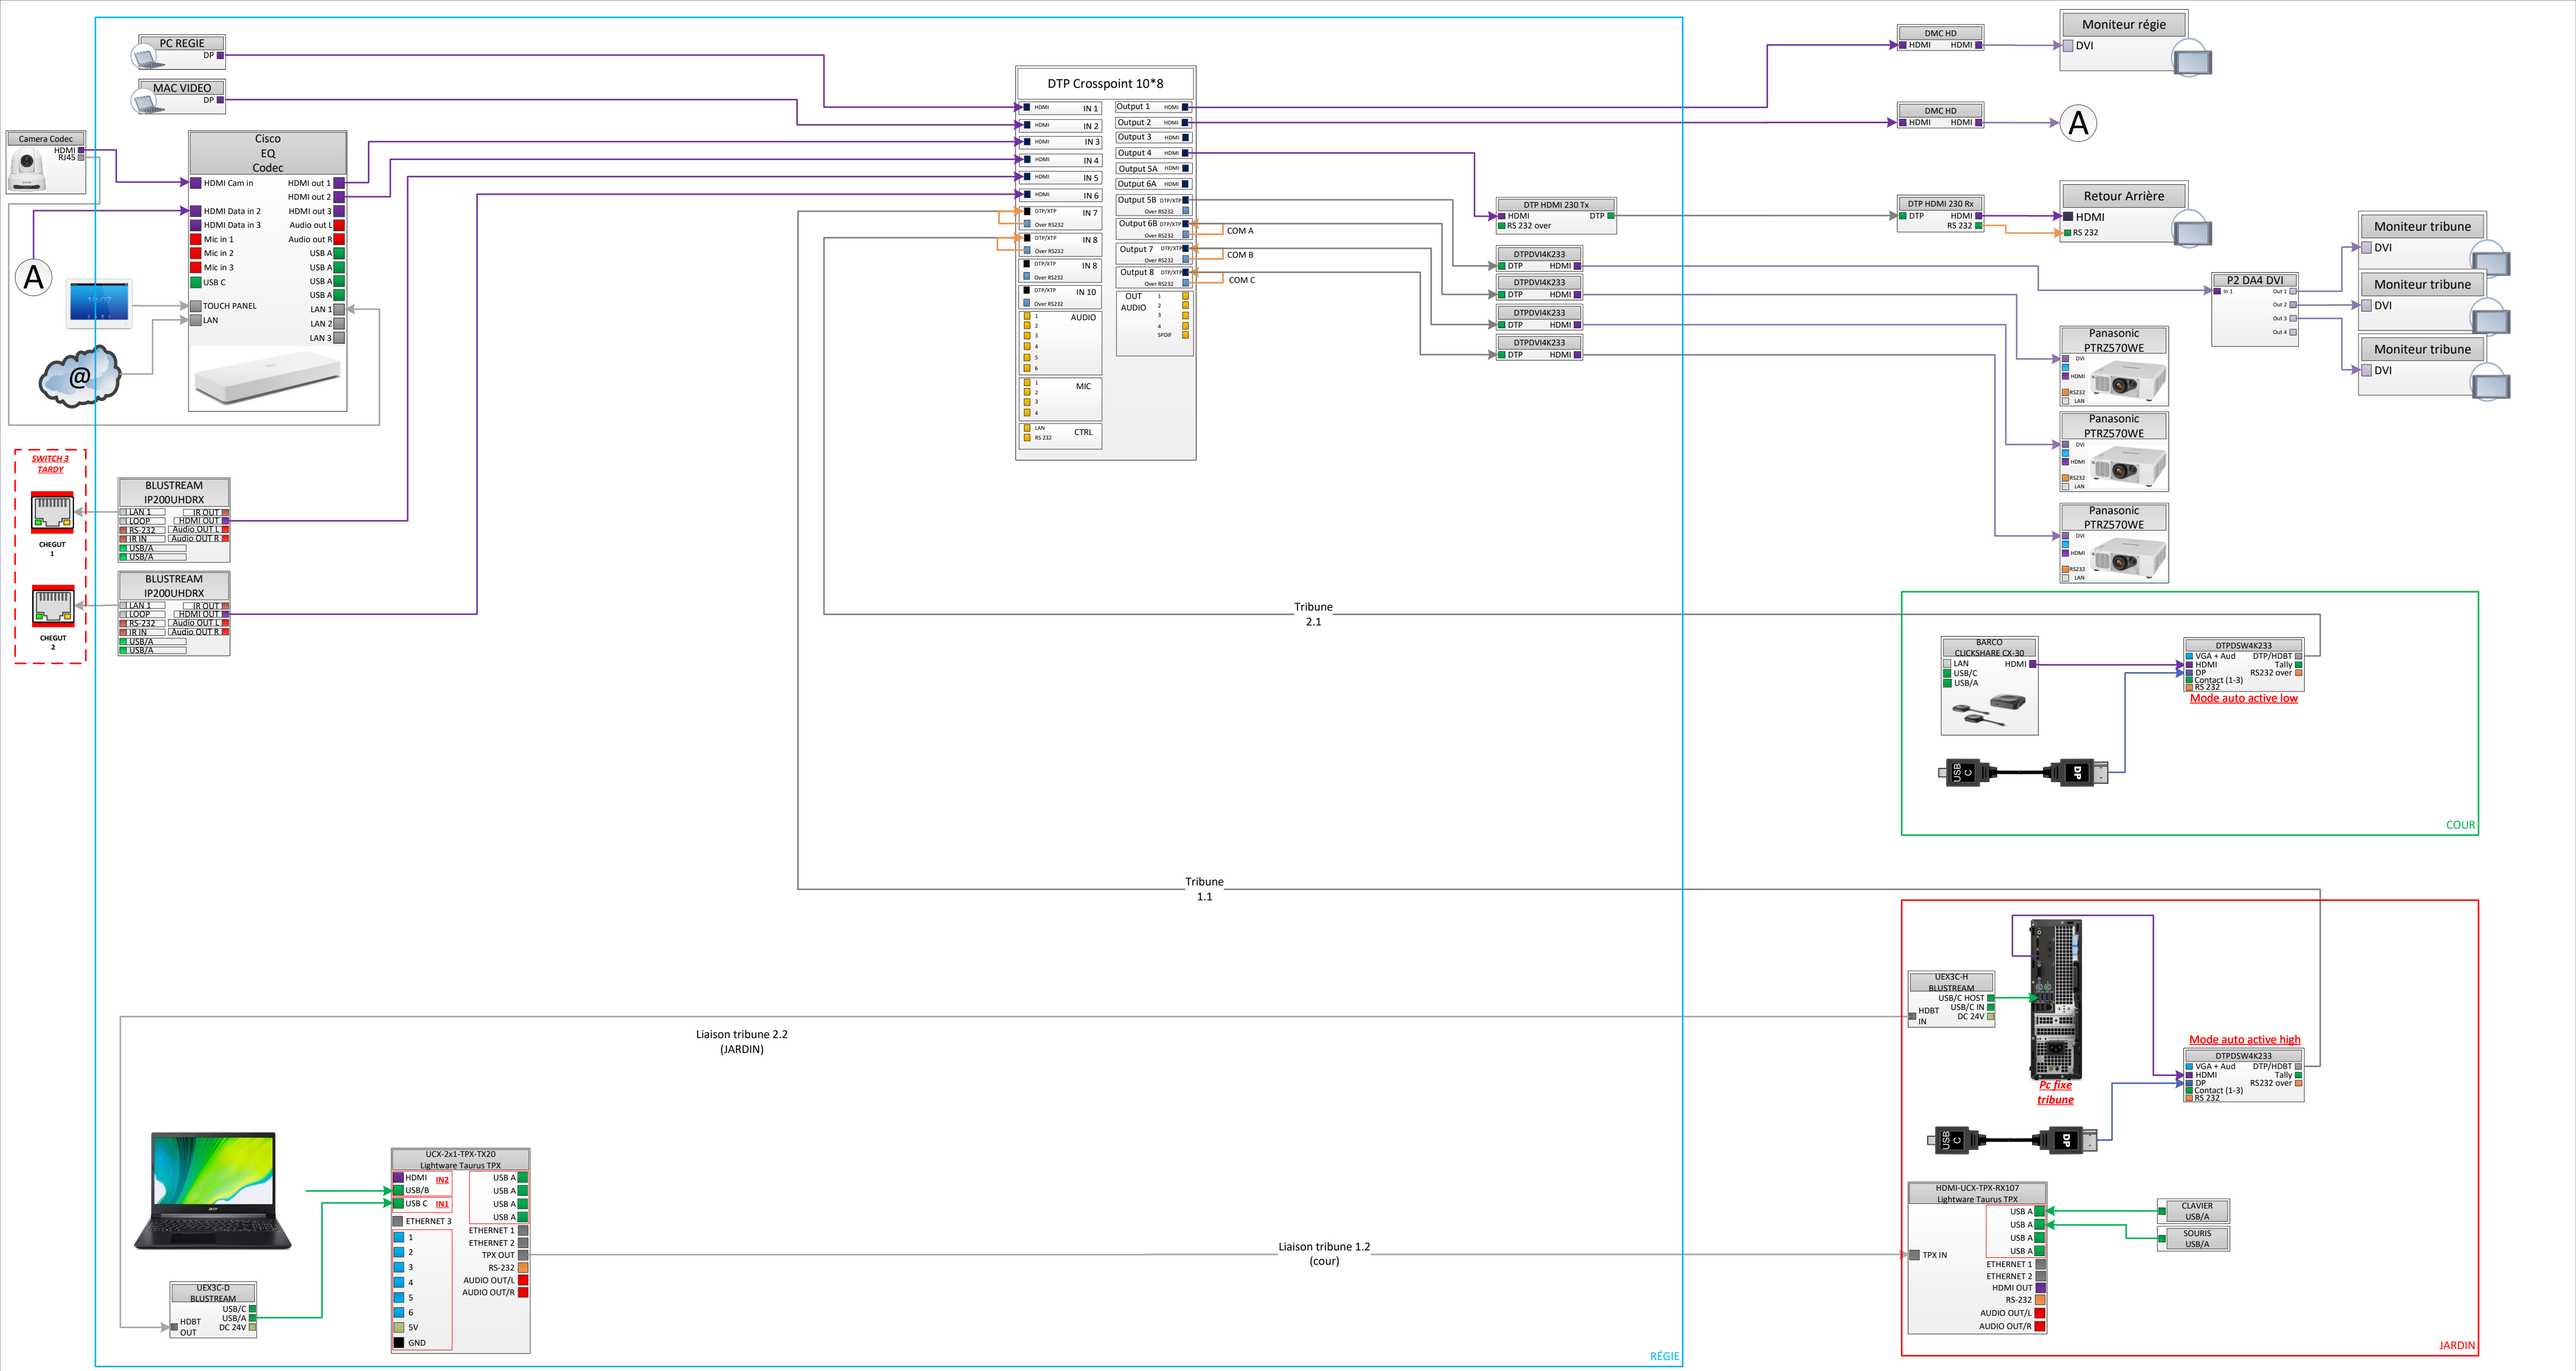

LEGENDE

- HDMI
- Audio
- Speakers
- USB
- RS232
- RJ45 cat6
- Audio Dante (RJ45 Cat6)
- Autres contrôles
- DVI
- VGA
- HD SDI
- Display port
- AC 240V
- DC OUT

VIDEOSONIC
Image, Son & Technique

Za les portes de l'Oise
Batiment B2 – rue Henri Becquerel
60230 CHAMBLY
Tel : 01 75 01 60 40
Fax : 01 75 01 60 41
@ : contact@videosonic.fr

FNCA CHEGUT

Videosonic

DIMENSION		VIDEO	RÉV 1
02/02/2026	ECHELLE 1:1		FEUILLE 4 / 8

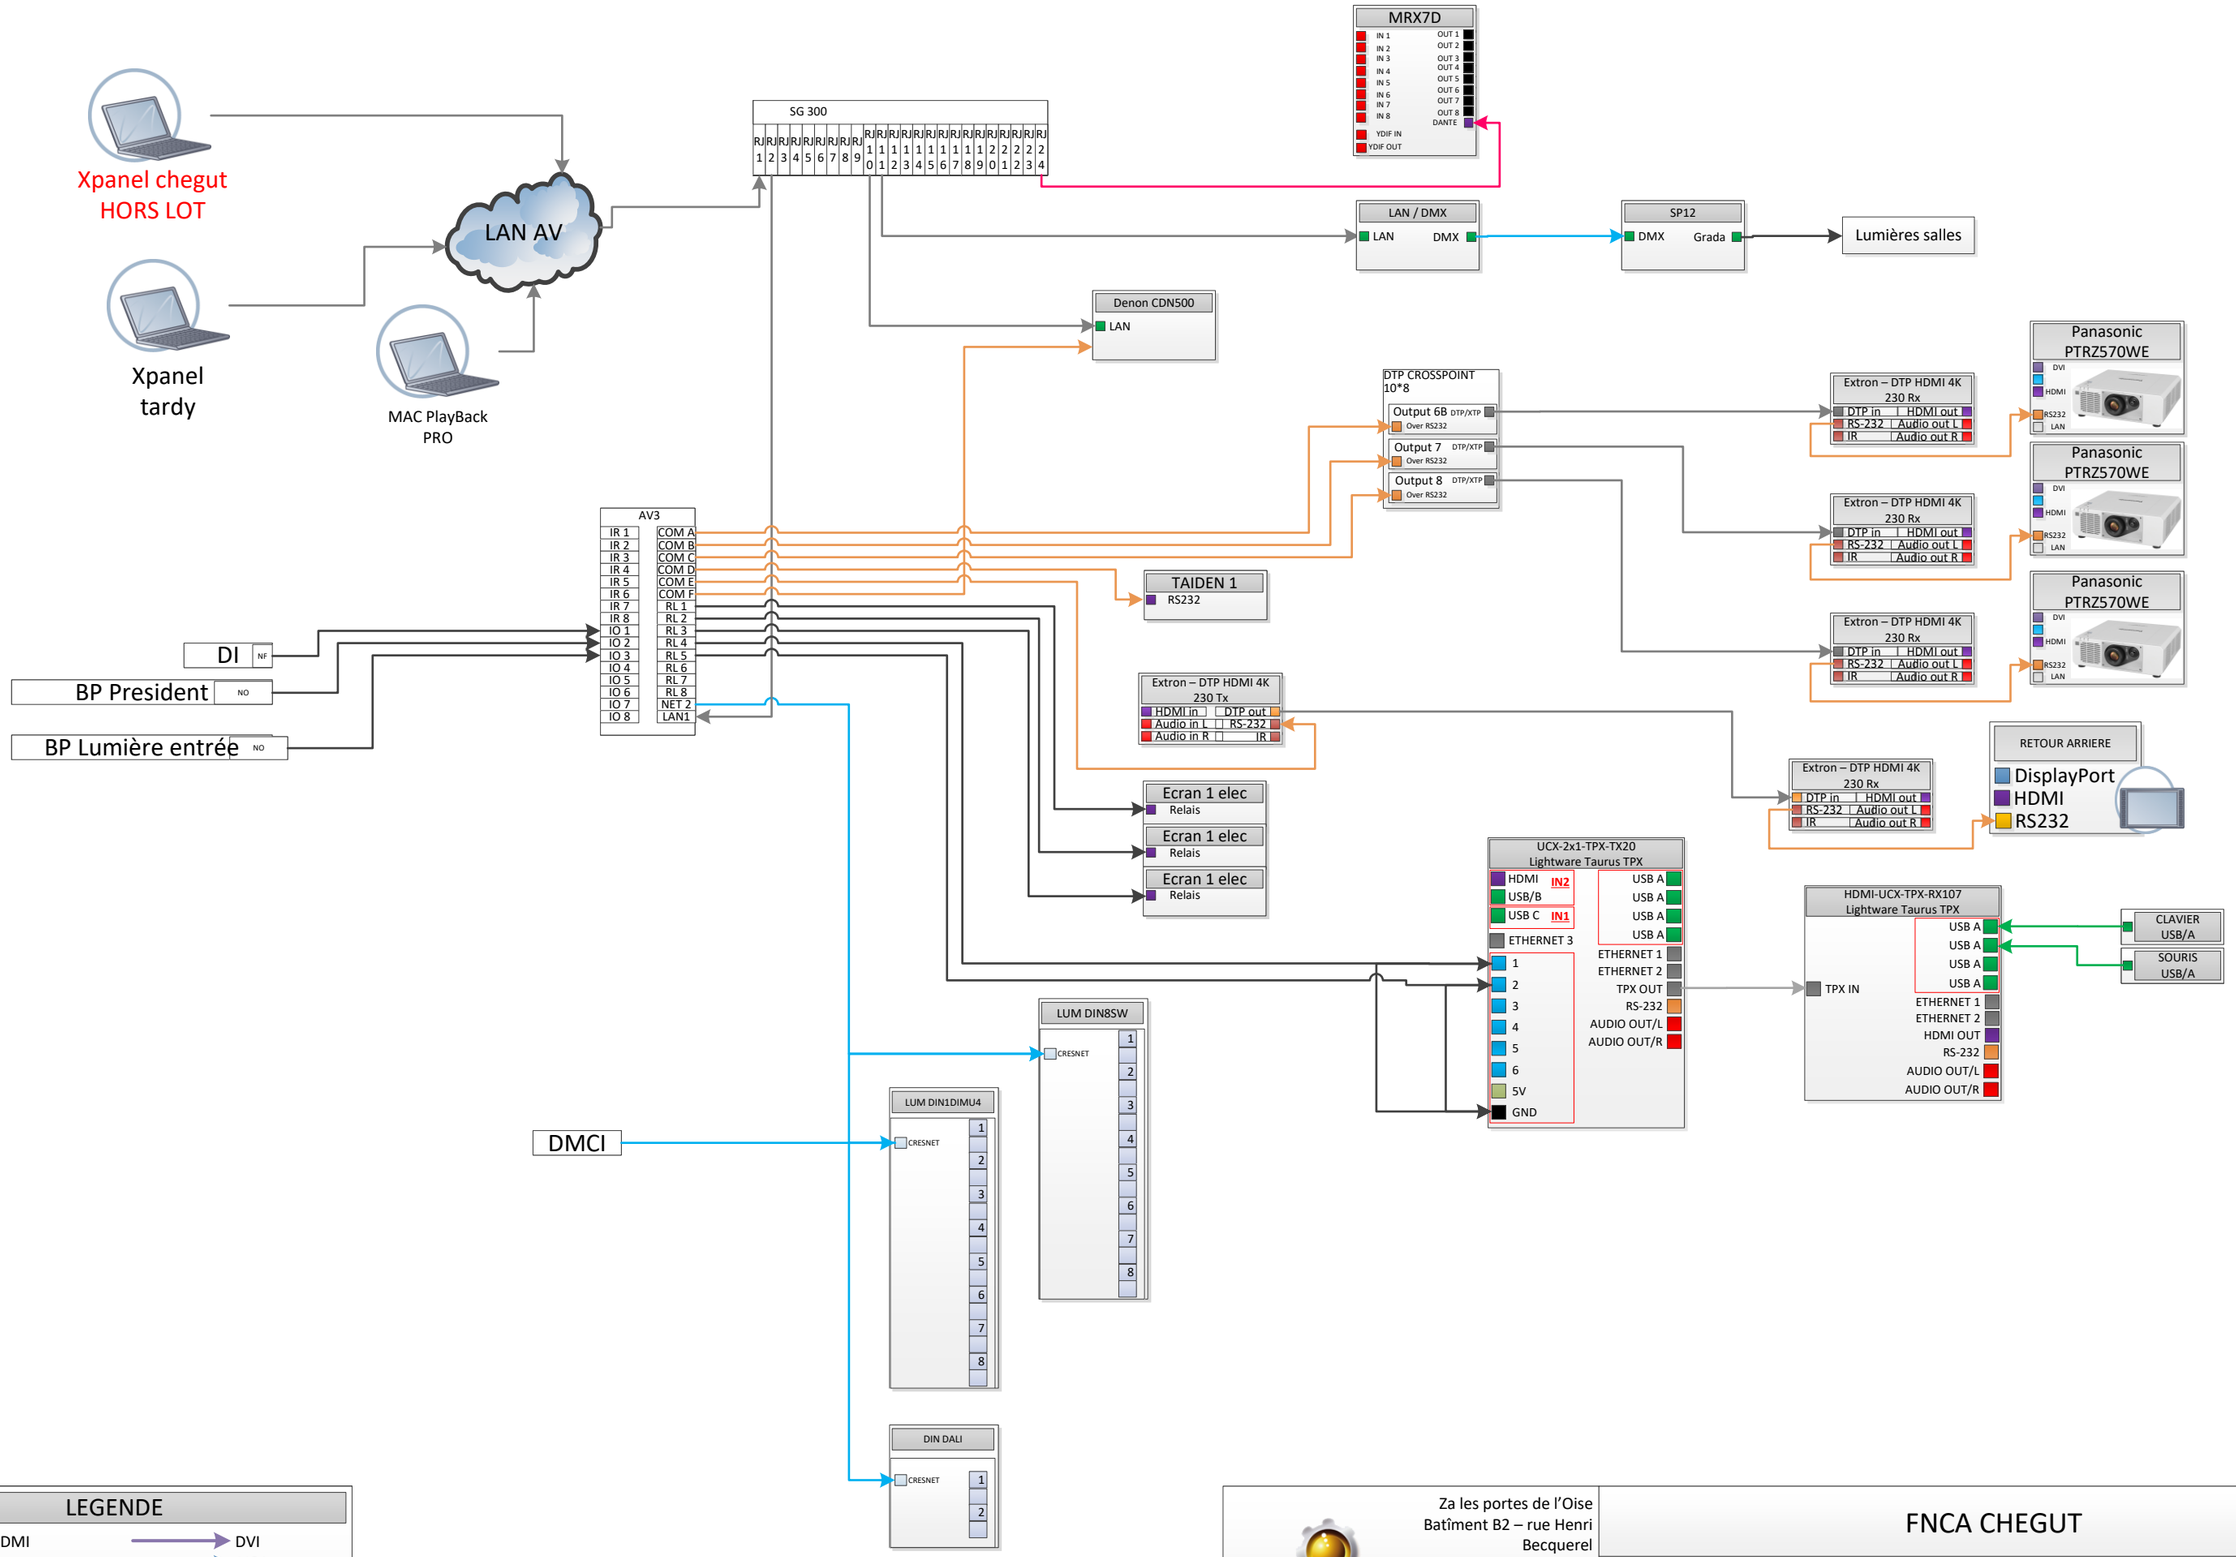

LEGENDE

- HDMI
- Audio
- Speakers
- USB
- RS232
- RJ45 cat6
- Audio Dante (RJ45 Cat6)
- Autres contrôles
- DVI
- VGA
- HD SDI
- Display port
- AC 240V
- DC OUT

VIDEOSONIC
Image, Son & Technique

Za les portes de l'Oise
Batîment B2 – rue Henri
Becquerel
60230 CHAMBLY

Tel : 01 75 01 60 40
Fax : 01 75 01 60 41
@ : contact@videosonic.fr

FNCA CHEGUT

Videosonic

DIMENSION			RÉV
		contrôle	1
02/02/2026	ECHELLE 1:1		FEUILLE 5 / 8

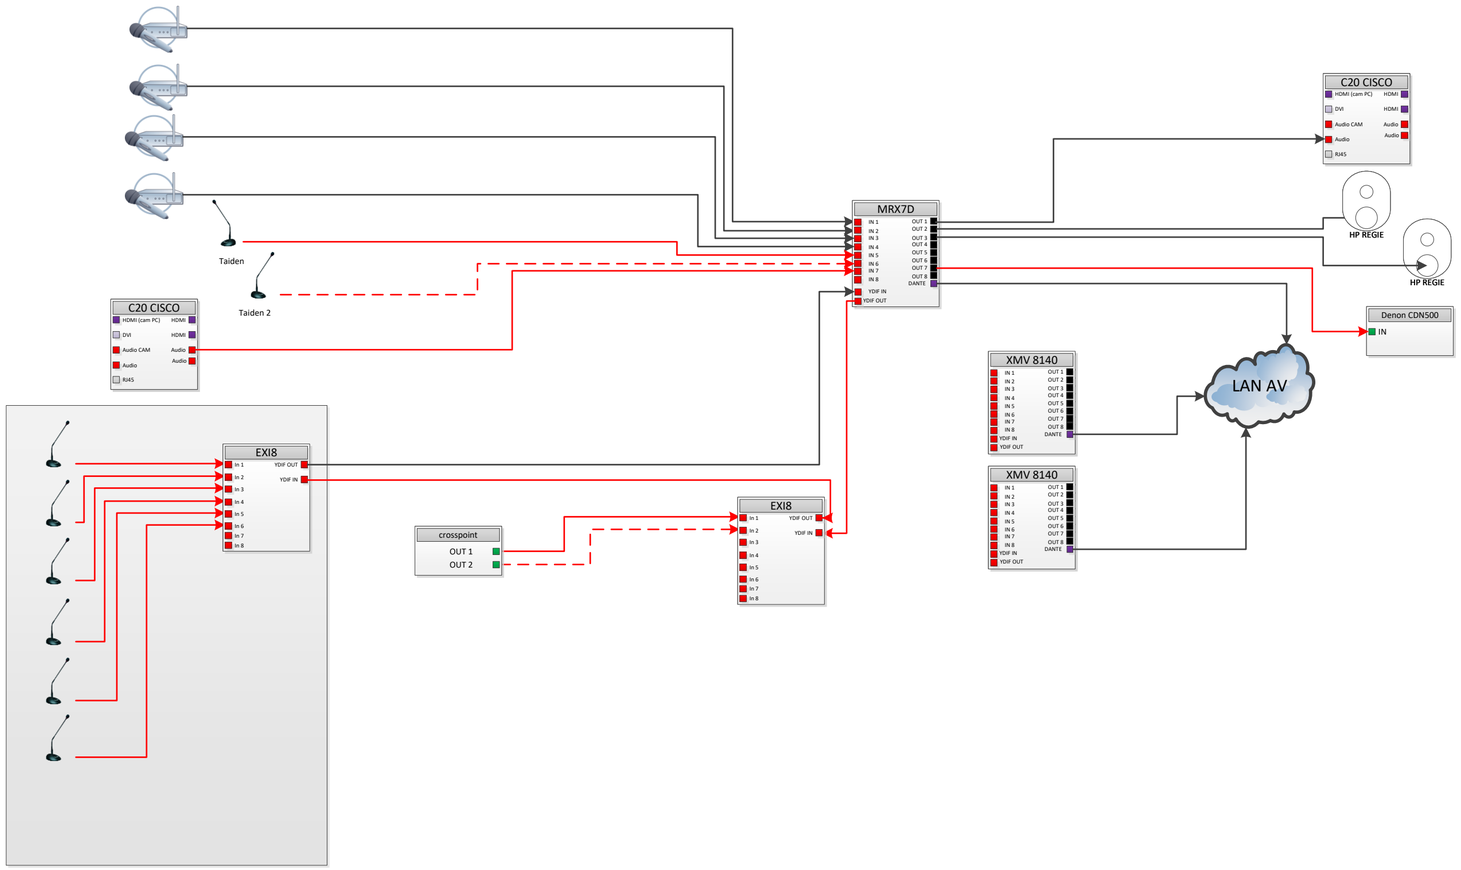

DANTE

1 Tribune Jardin
2 Tribune Cour
3 Facade Jardin
4Facade Cour
5 HP COUR 1
6 HP COUR 2
7HP COUR 3
8HP COUR 4
9 HP COUR 5
10 HP JARDIN 1
11HP JARDIN 2
12 HP JARDIN 3
13 HP JARDIN 4
14 HP JARDIN 5
15
16
User avancé IPAD 1234
Admin: 5775

Projet

Légende

existant

Modifs/ajouts

Option

VIDEOSONIC
Image, Son & Technique

Za les portes de l'Oise
Batiment B2 – rue Henri Becquerel
60230 CHAMBLY

Tel : 01 75 01 60 40
Fax : 01 75 01 60 41
@ : contact@videosonic.fr

FNCA CHEGUT

Videosonic

DIMENSION		Audio projet	RÉV 1
ECHELLE 1:1		FEUILLE 6 / 8	

02/02/2026

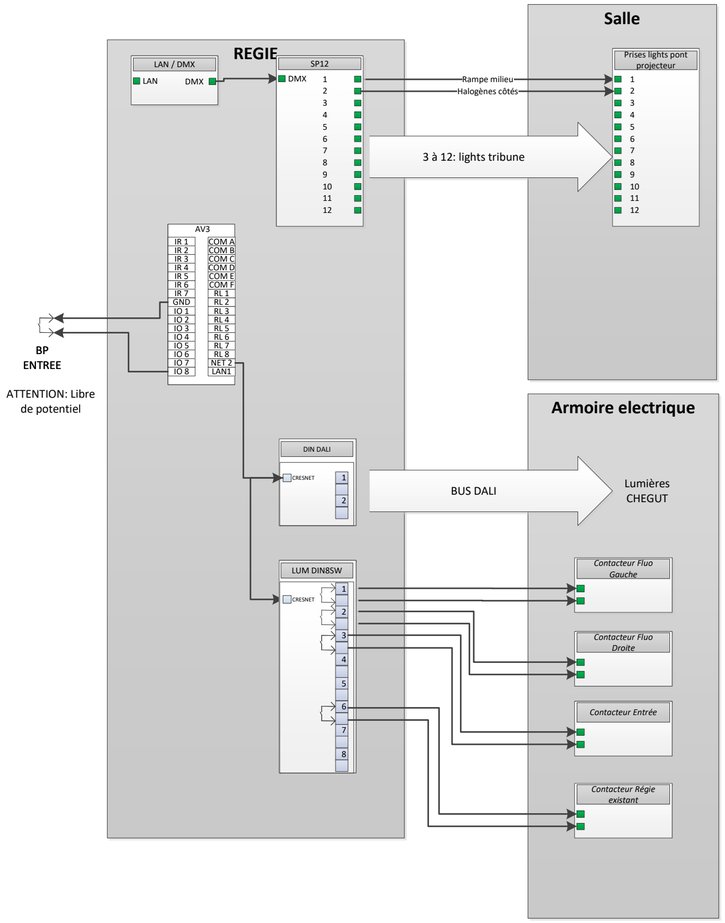

VIDEOSONIC
Image, Son & Technique

Za les portes de l'Oise
Batîment B2 – rue Henri
Becquerel
60230 CHAMBLY

Tel : 01 75 01 60 40
Fax : 01 75 01 60 41
@ : contact@videosonic.fr

FNCA CHEGUT

Videosonic

DIMENSION		lumières	RÉV
			1

02/02/2026

ECHELLE	1:1	FEUILLE	7 / 8

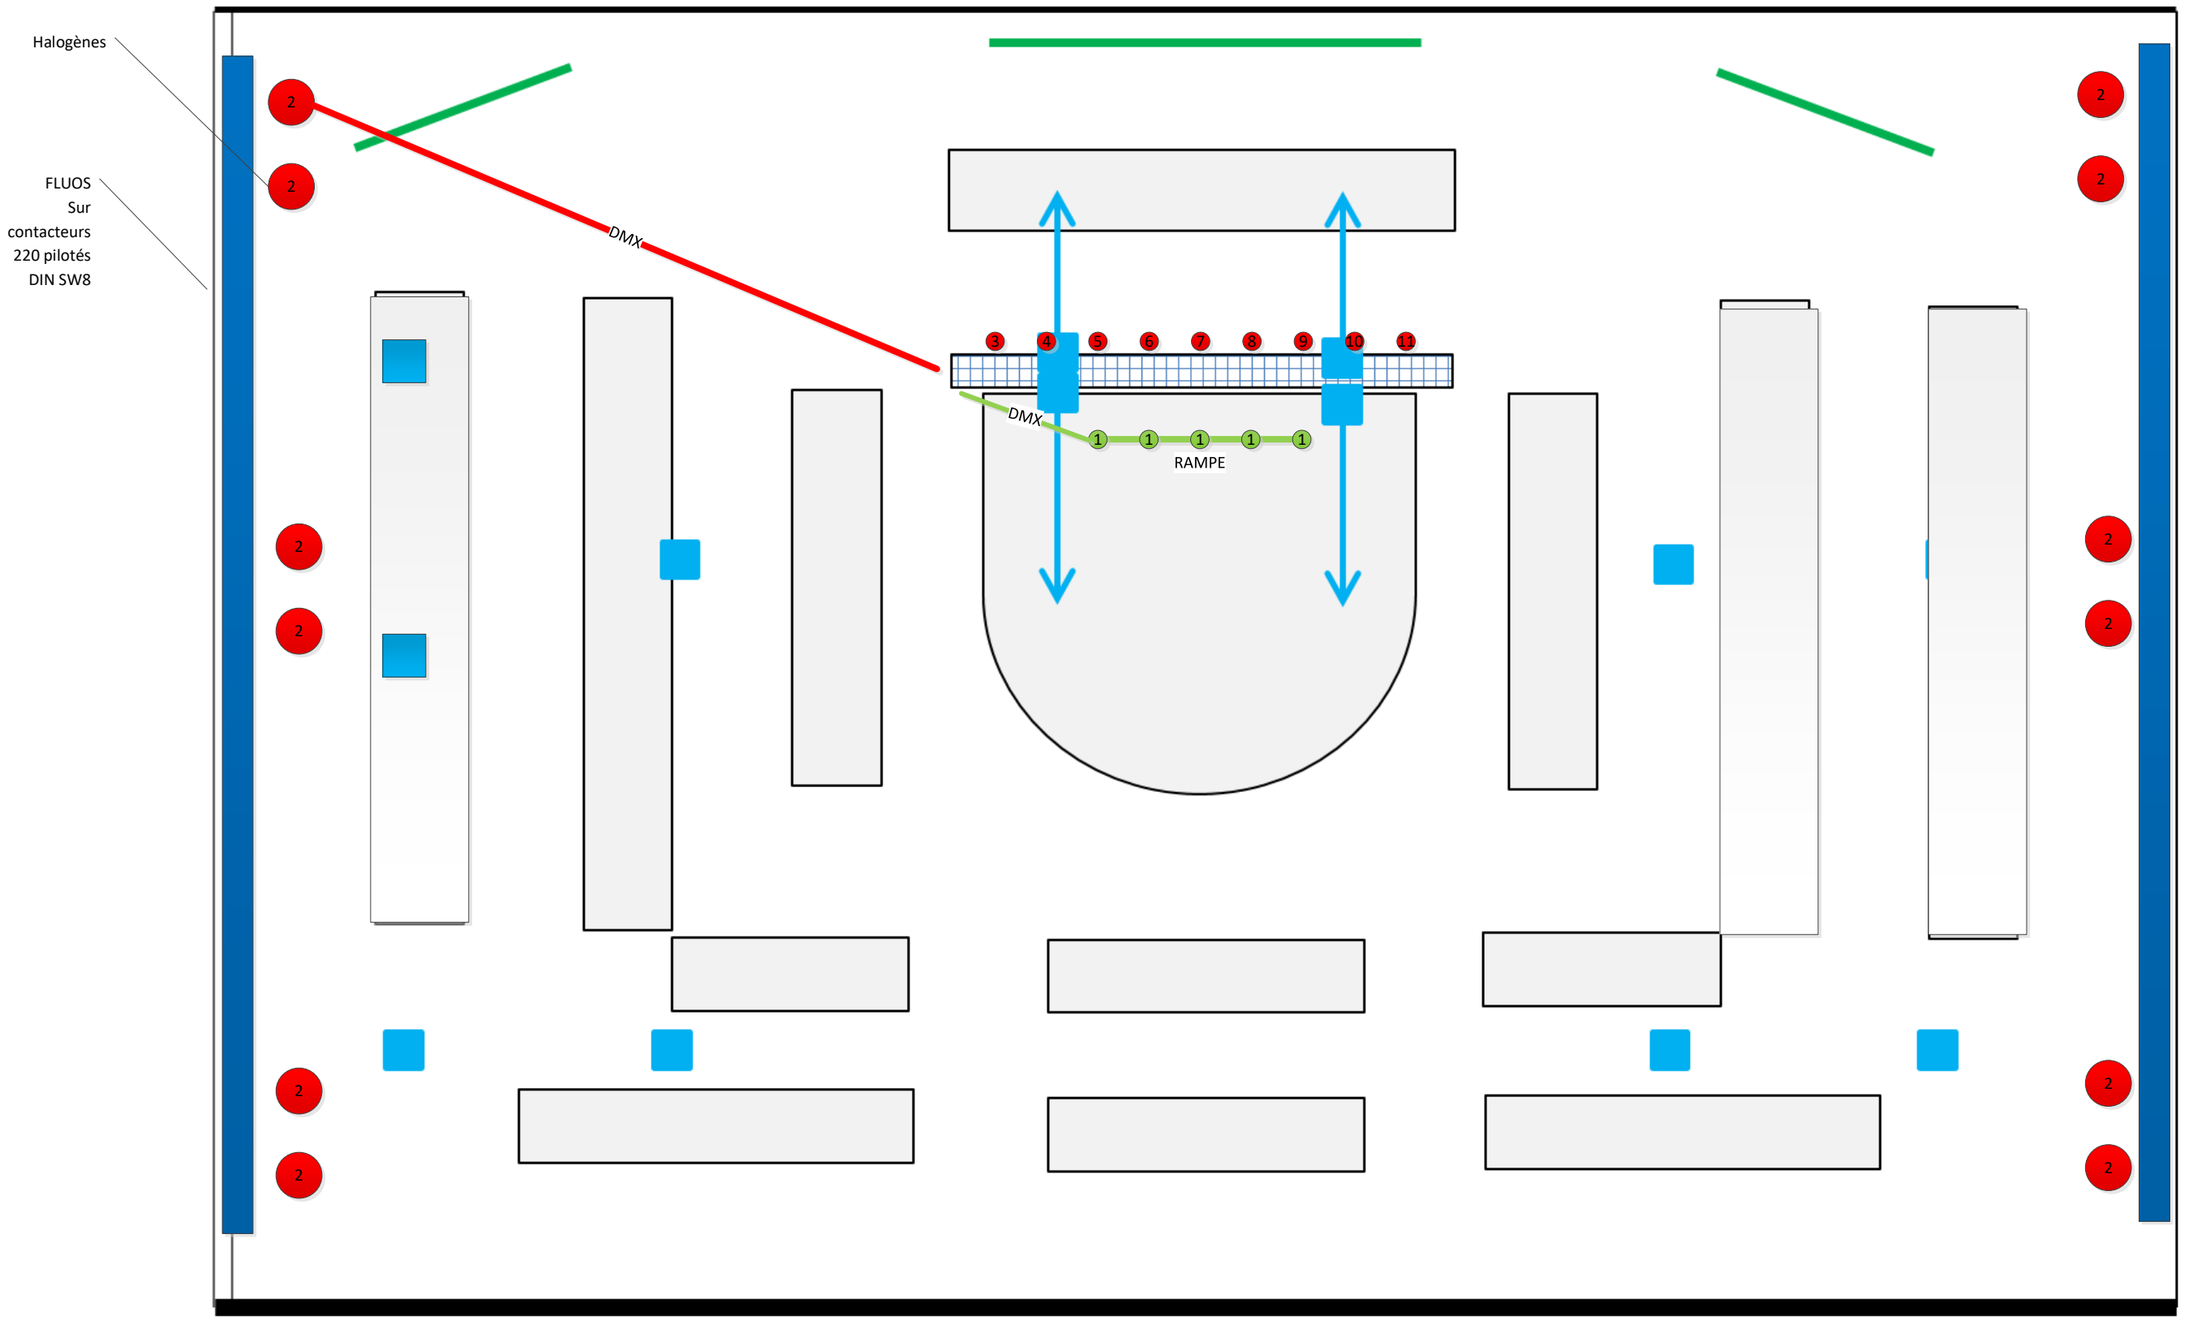

Za les portes de l'Oise
Batîment B2 – rue Henri Becquerel
60230 CHAMBLY
Tel : 01 75 01 60 40
Fax : 01 75 01 60 41
@ : contact@videosonic.fr

VIDEOSONIC
Image, Son & Technique

FNCA CHEGUT

Videosonic

DIMENSION			RÉV
		lumieres masse	1
ECHELLE 1:1		FEUILLE 8 / 8	

02/02/2026