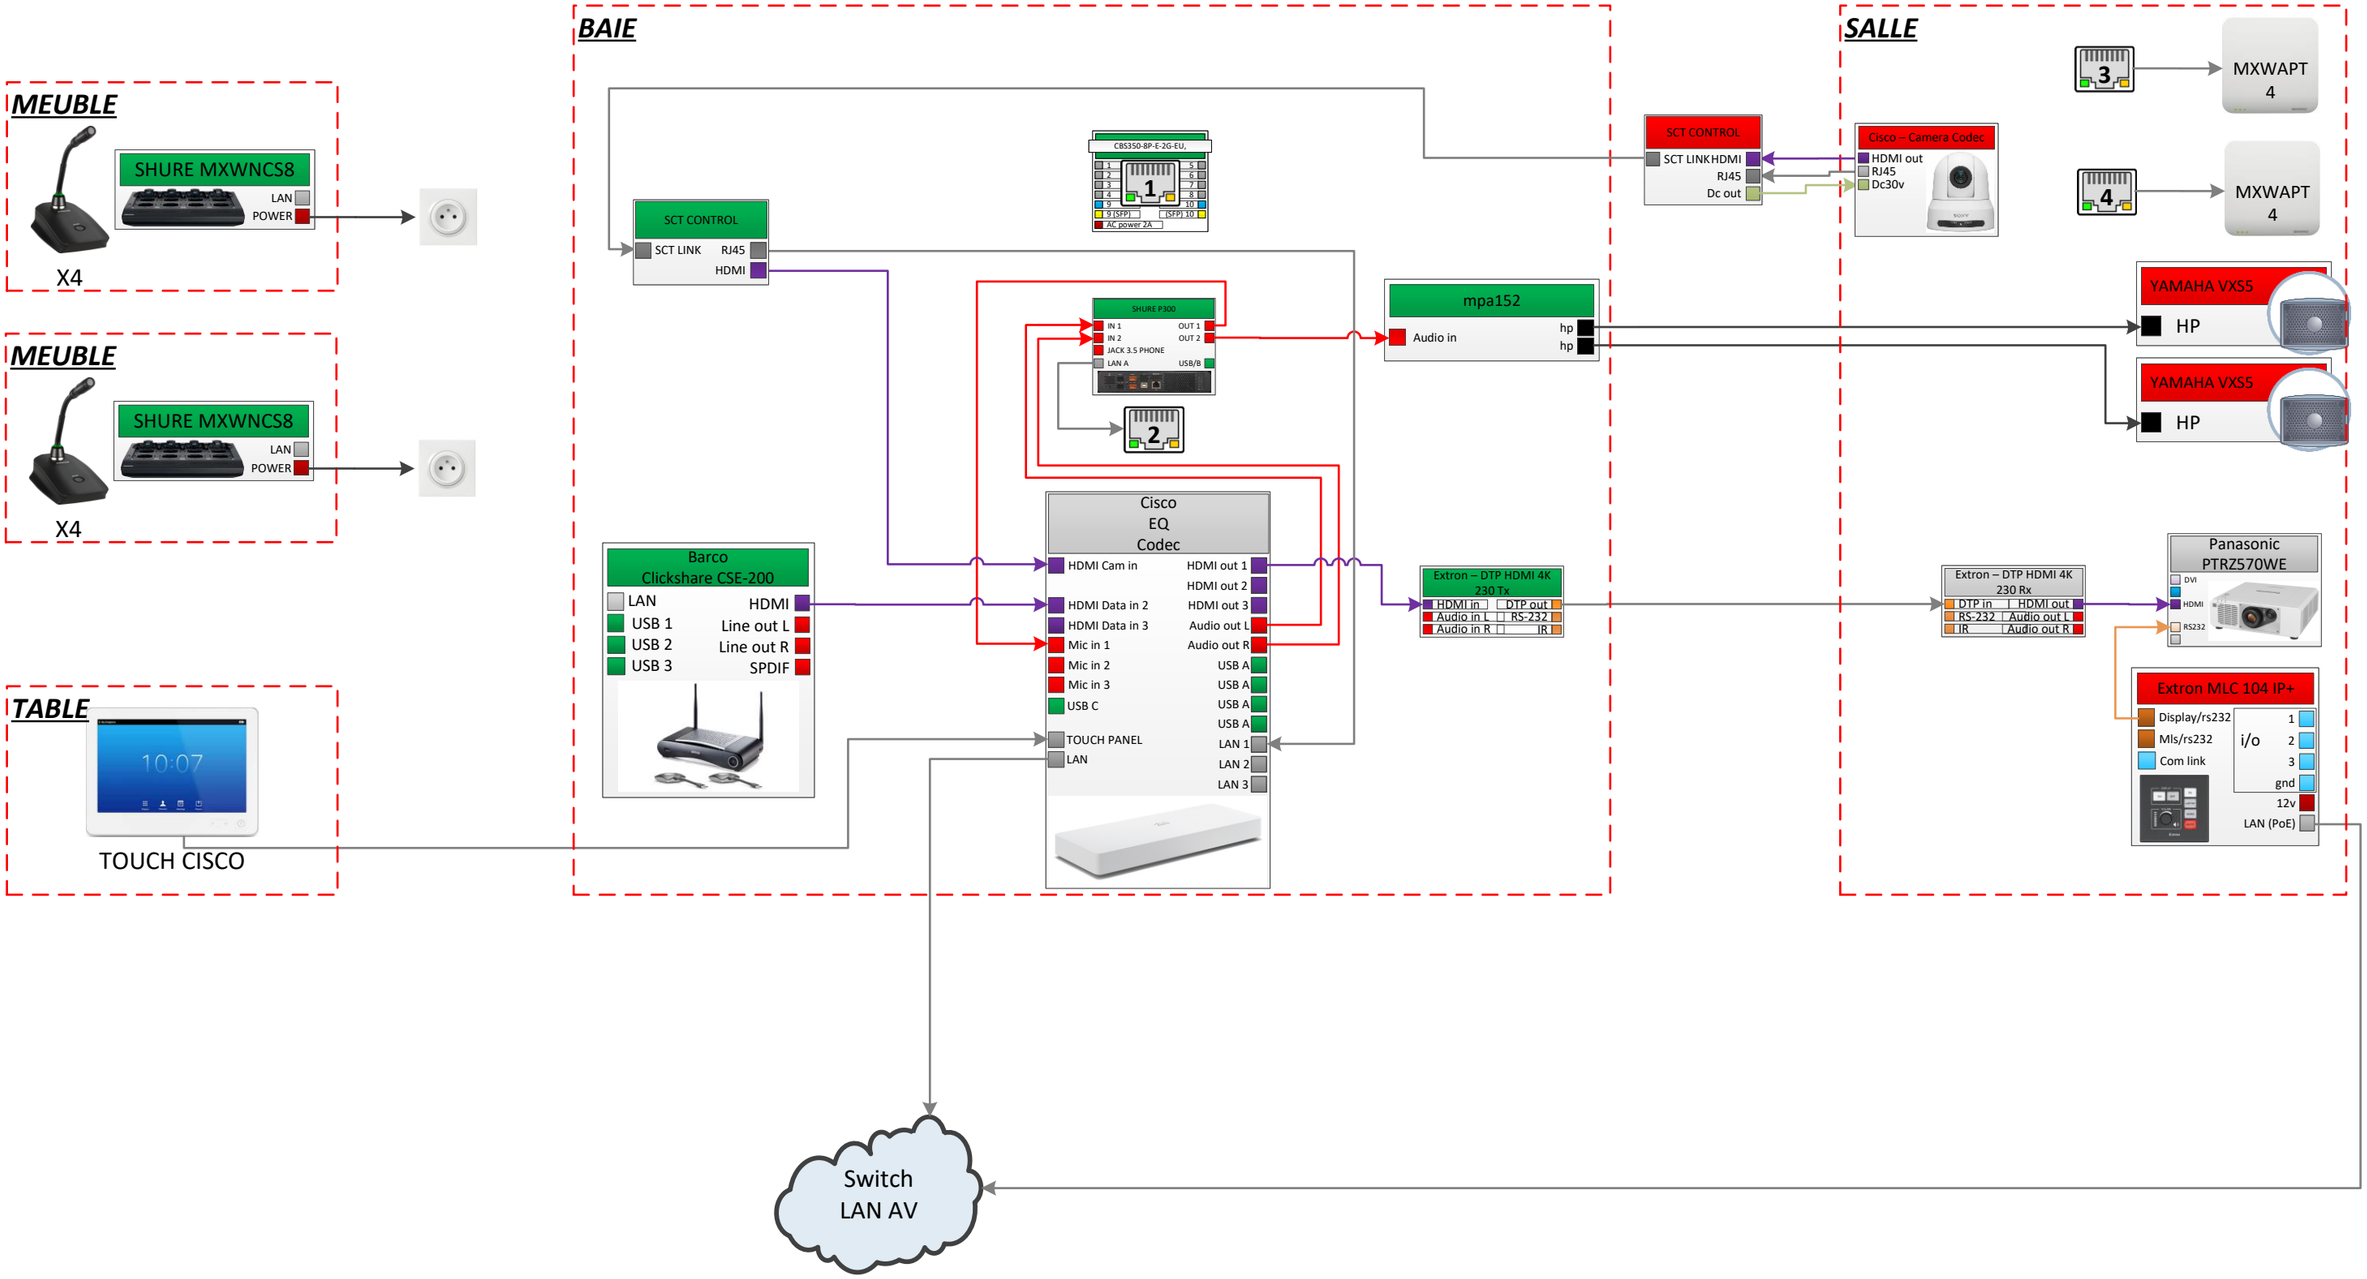

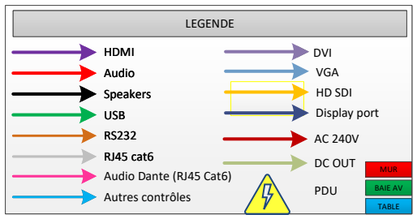

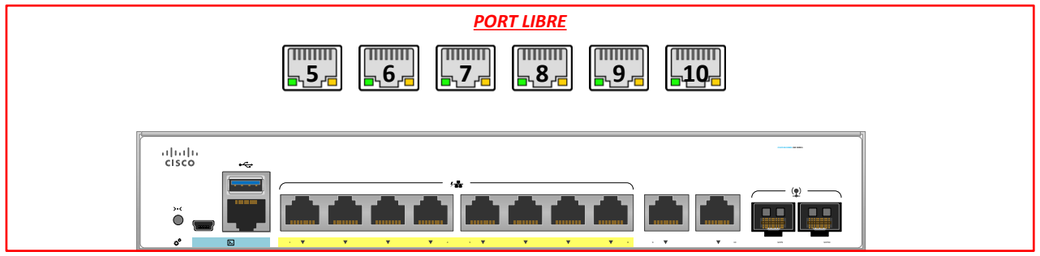

VIDEOSONIC
Image, Son & Technique
Za les portes de l'Oise
Batîment B2 – rue Henri Becquerel
60230 CHAMBLY
Tel : 01 75 01 60 40
Fax : 01 75 01 60 41
t.fourmentraux@videosonic.fr

FOURMENTRAUX Thierry

24/06/2025

Salle Bourbonnais

GIFECAM 48 Rue de la Boétie
75008 PARIS

DIMENSION	RÉV
A3	1

ECHELLE	1:1	FEUILLE	1 / 2

1 U	SWITCH CBS350-8P-E-2G-EU,
1 U	BALAIS PASSE CABLE
1 U	DTP TX 230 HDMI + ALIM + MPA152 + ALIM
1 U	CLICKSHARE CSE200 + SHURE P300
1 U	CODEC CISCO SX20
1 U	SOUND CONTROL RC4-HE

VIDEOSONIC
Image, Son & Technique
Za les portes de l'Oise
Batîment B2 – rue Henri Becquerel
60230 CHAMBLY
Tel : 01 75 01 60 40
Fax : 01 75 01 60 41
t.fourmentraux@videosonic.fr
FOURMENTRAUX Thierry

24/06/2025

Salle Bourbonnais

GIFECAM 48 Rue de la Boétie
75008 PARIS

DIMENSION	RÉV
A3	1

PLAN DE BAIE

ECHELLE 1:10 FEUILLE 2 / 2