AON

R+9 A

Synoptiques d’exécution salles collaboratives 18+10p

VIDEOSONIC
Image, Son & Technique

Za les portes de l’Oise
Batîment B2 – rue Henri Becquerel
60230 CHAMBLY
Tel : 01 75 01 60 40
Fax : 01 75 01 60 41
@ : contact@videosonic.fr

Salles collaboratives 18+10places - R+9 A

AON
31 - 35 rue de la Fédération - 75015 PARIS

BILLOT M	DIMENSION	Page de Garde	RÉV 1
13/09/2019	ECHELLE 1:1		FEUILLE 1 / 4

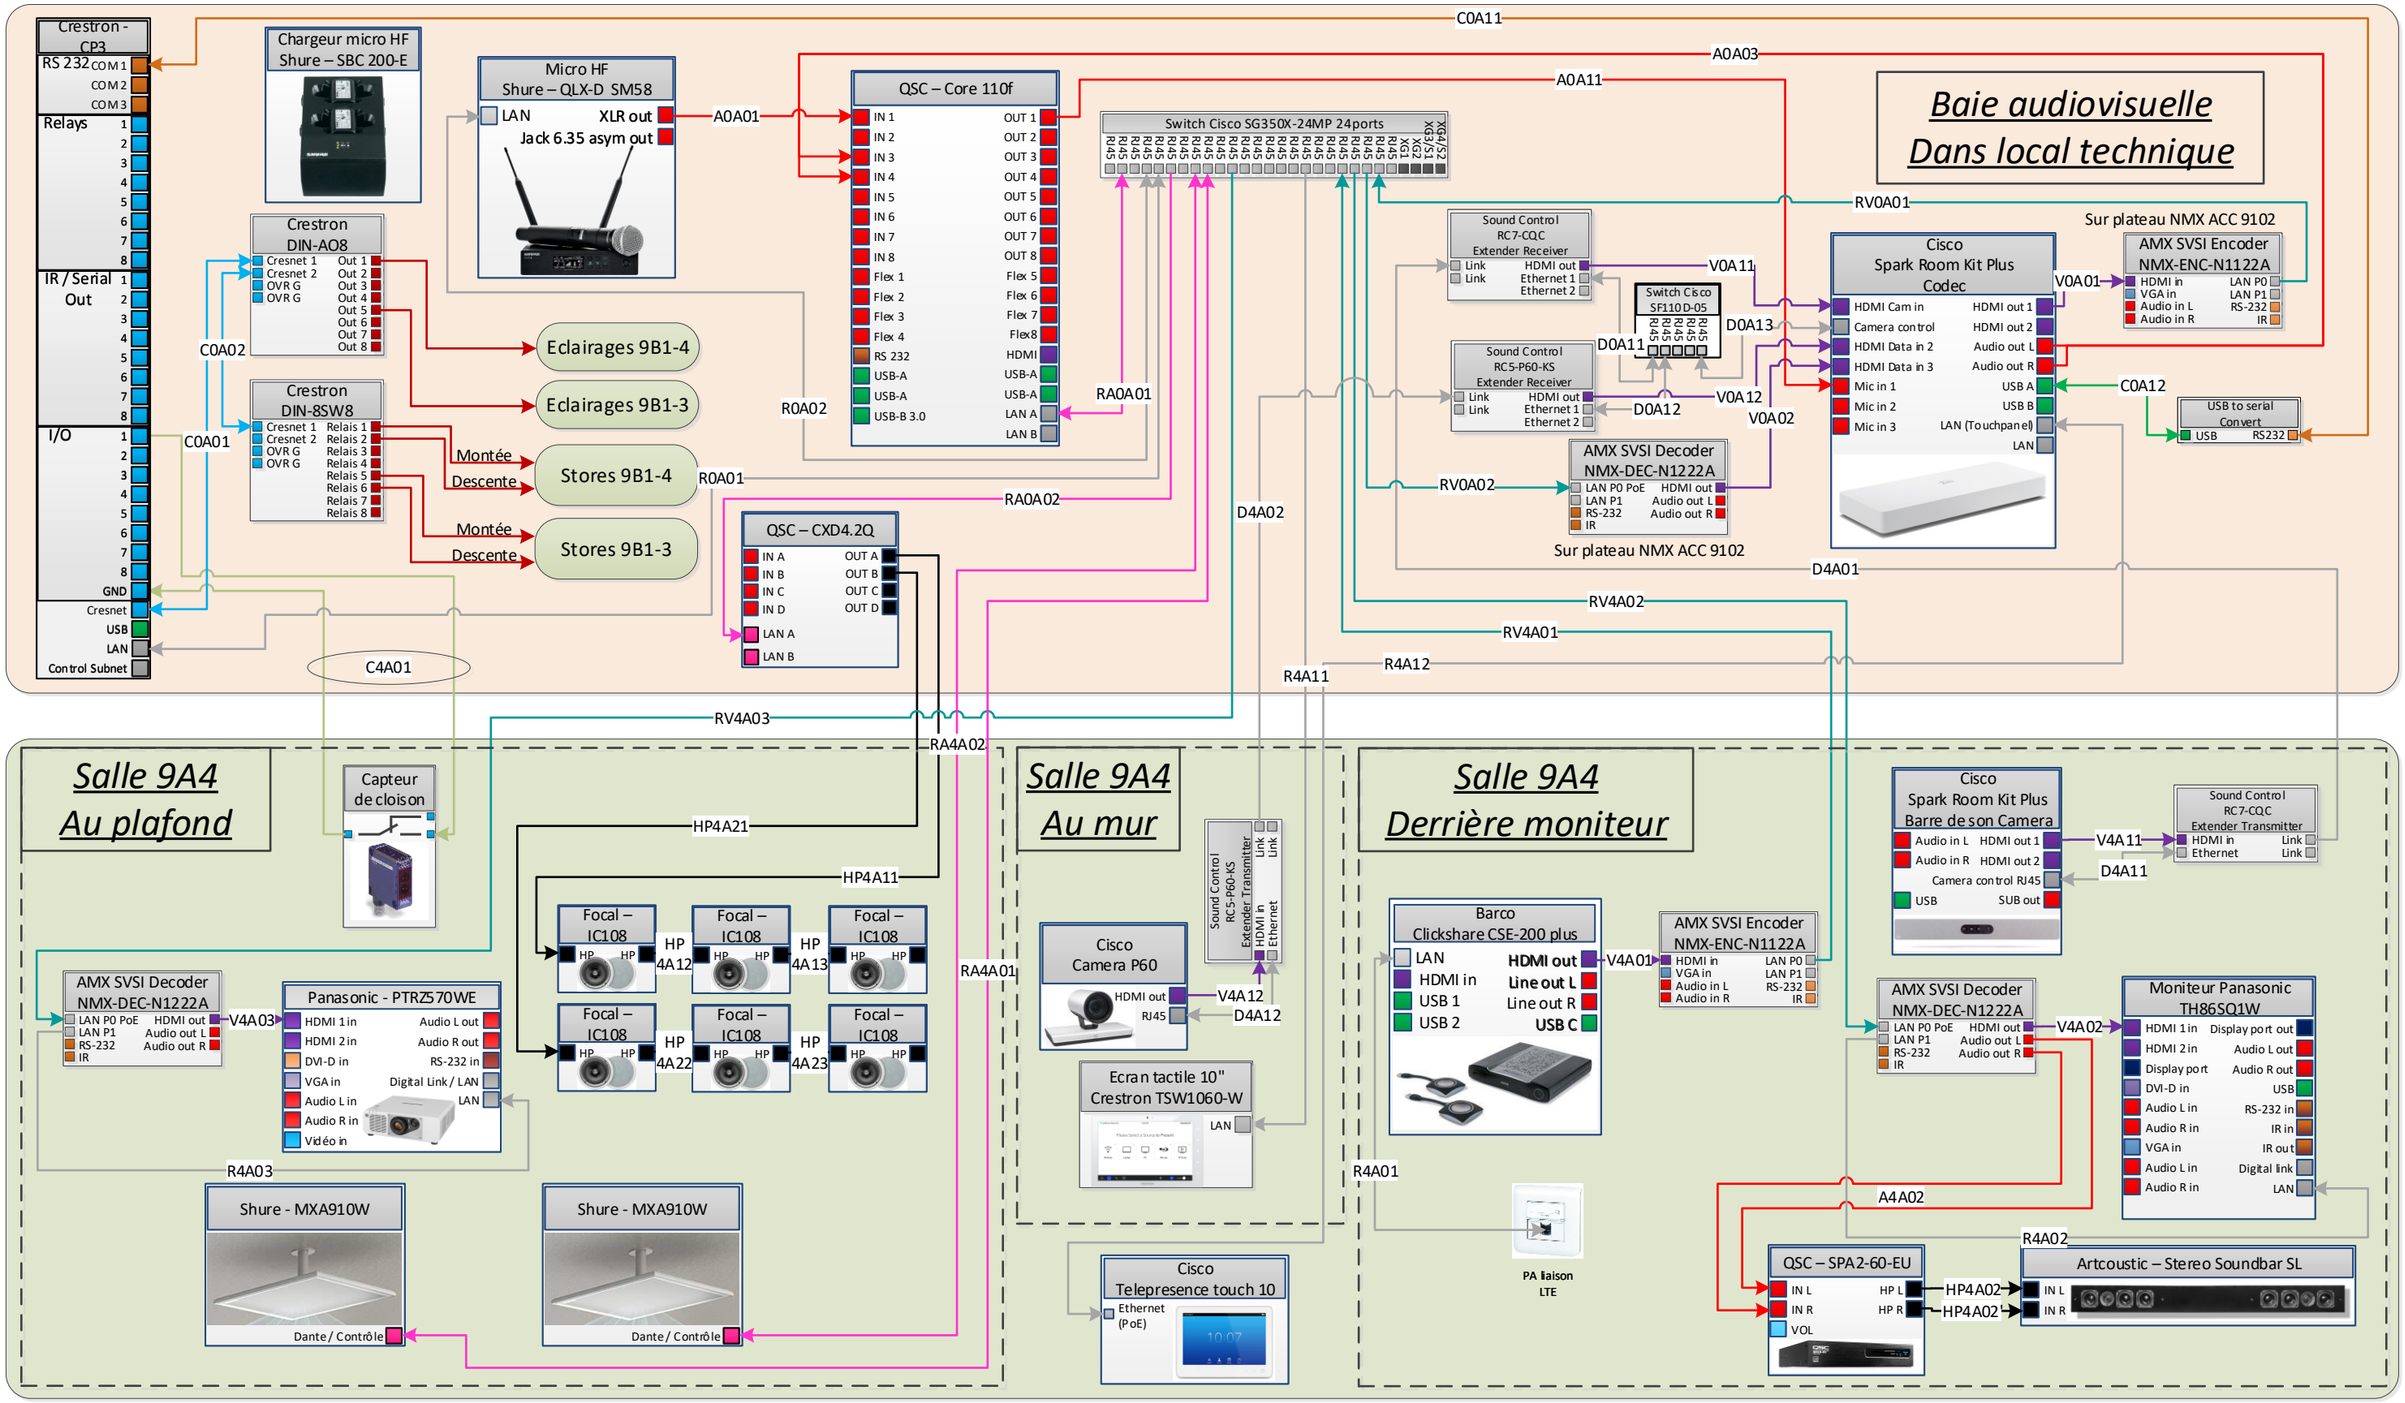

LEGENDE

- HDMI
- Audio
- Speakers
- USB
- RS232
- RJ45 cat6
- Audio Dante (RJ45 Cat6)
- HDBT/DTP/XTP
- DVI
- VGA
- HD SDI
- Display port
- Electricité C Fort
- Electricité C Faible
- Autres contrôles

VIDEOSONIC
Image, Son & Technique

Za les portes de l'Oise
Batiment B2 – rue Henri Becquerel
60230 CHAMBLY
Tel : 01 75 01 60 40
Fax : 01 75 01 60 41
@ : contact@videosonic.fr

BILLOT M

13/09/2019

Salles collaboratives 18+10places - R+9 A

AON

31 - 35 rue de la Fédération - 75015 PARIS

DIMENSION		RÉV
	Synoptique 9A4 (18p)+Baie AV	1
ECHELLE 1:1		FEUILLE 2 / 4

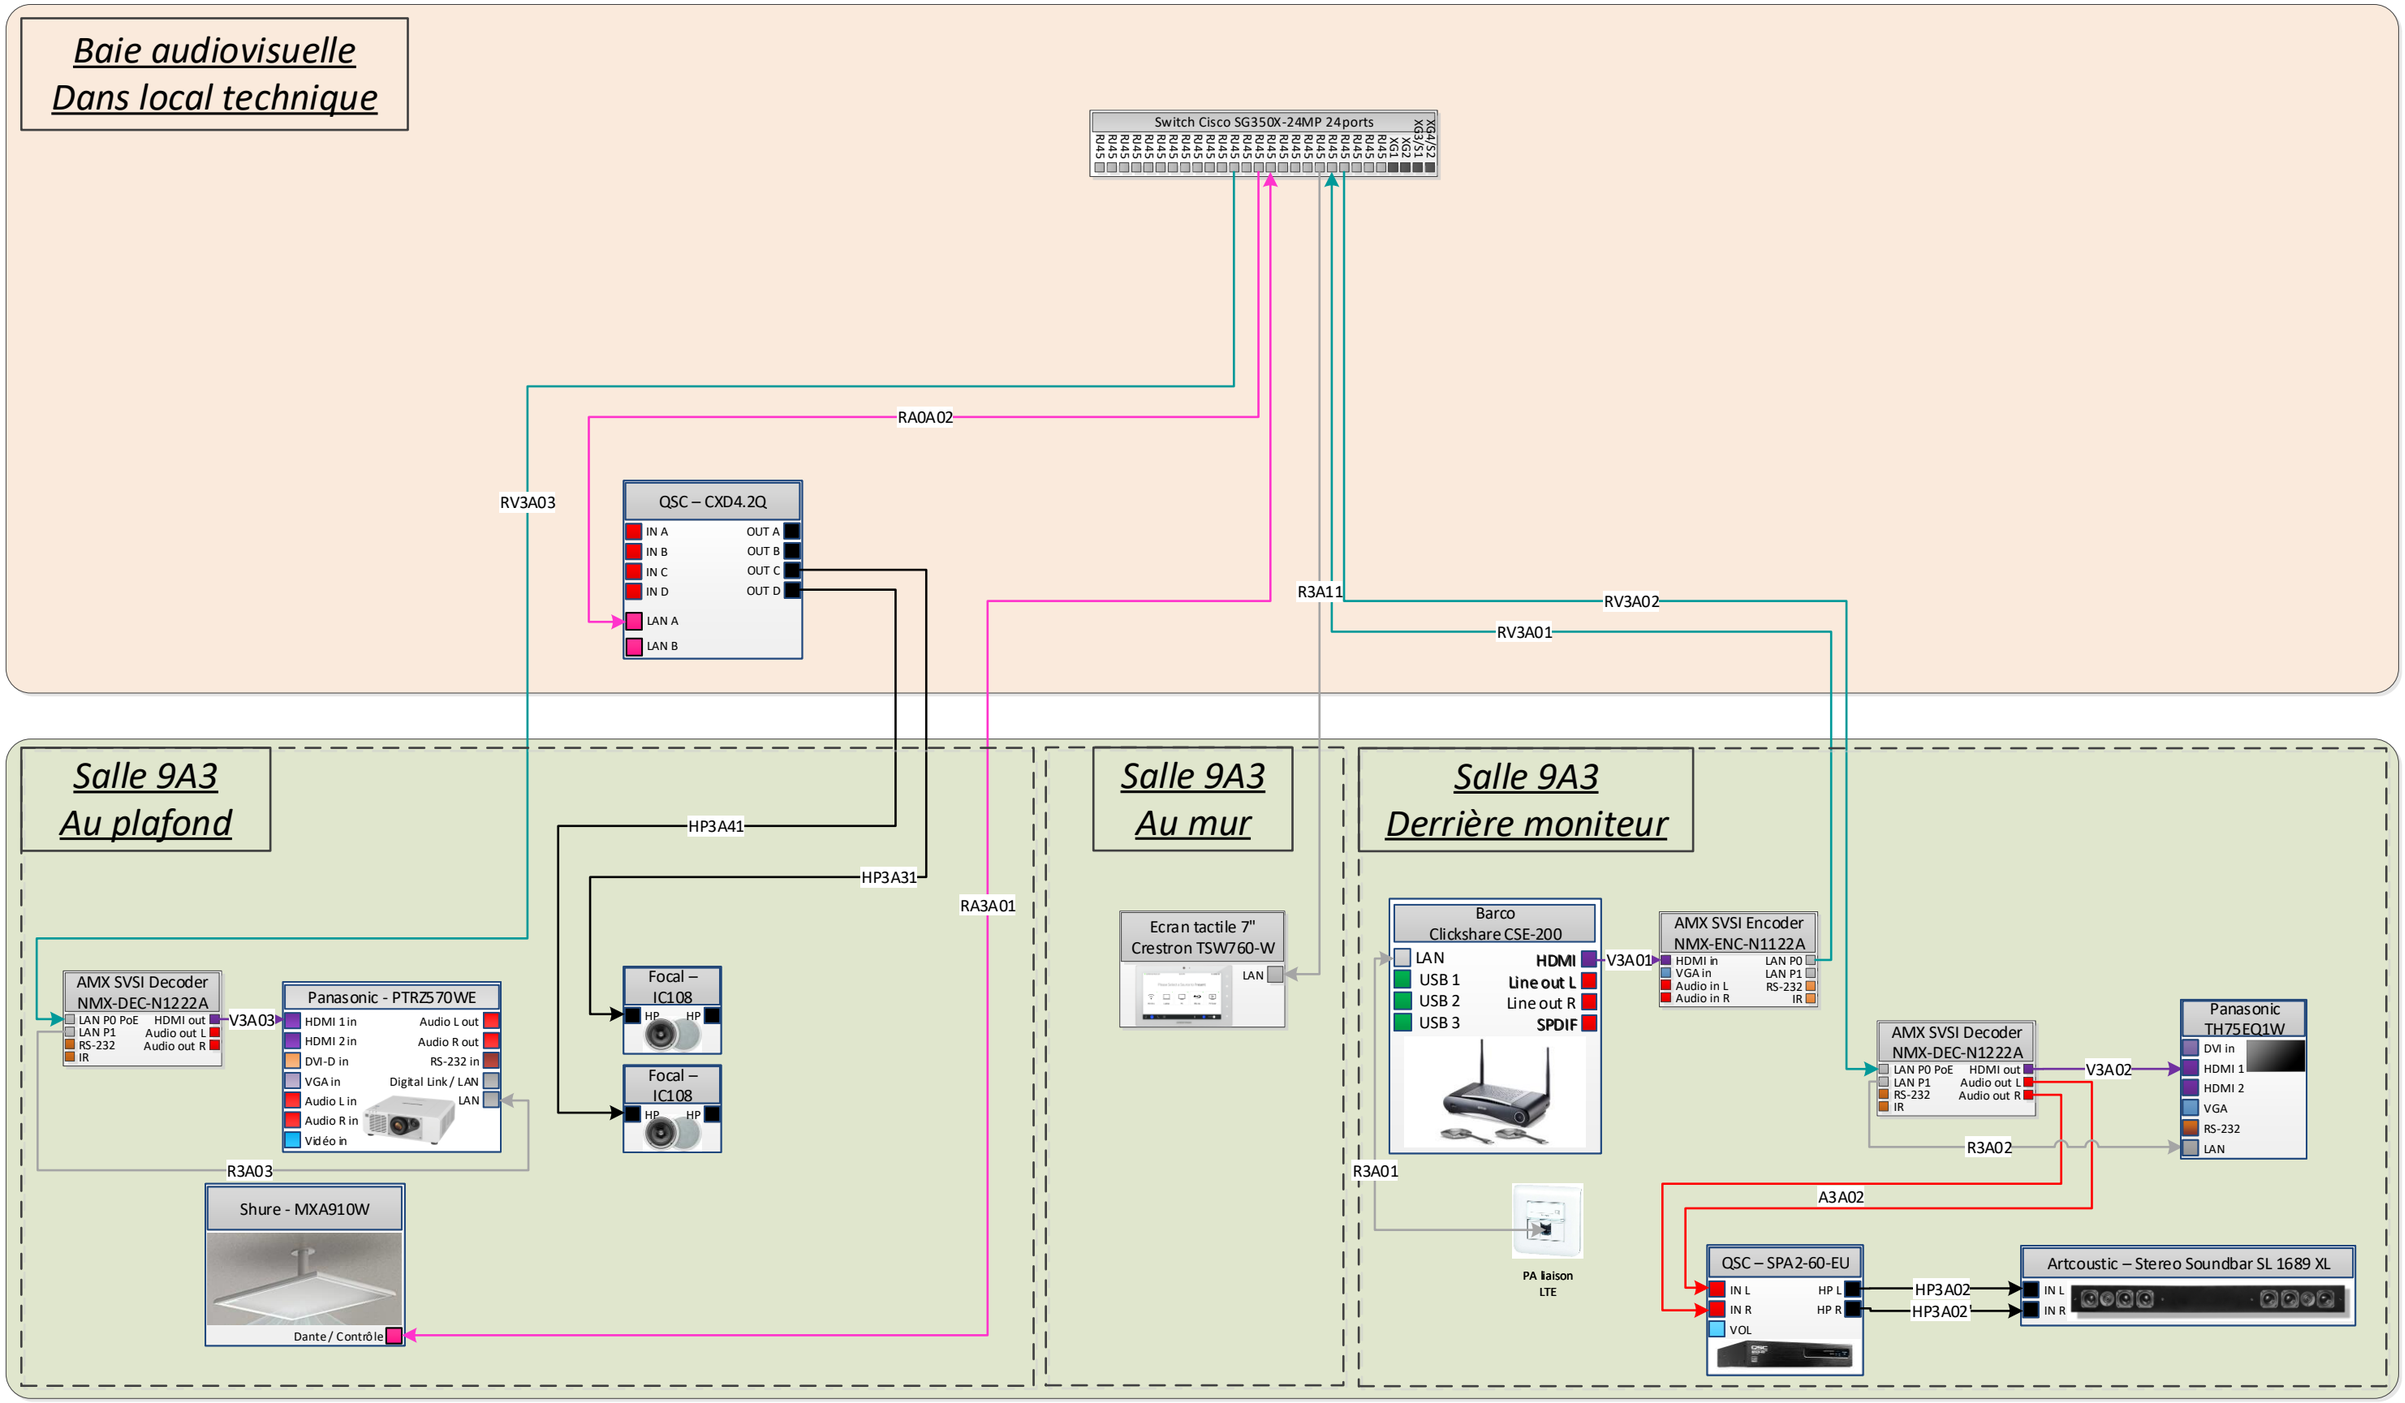

LEGENDE

- HDMI
- Audio
- Speakers
- USB
- RS232
- RJ45 cat6
- Audio Dante (RJ45 Cat6)
- HDBT/DTP/XTP
- DVI
- VGA
- HD SDI
- Display port
- Electricité C Fort
- Electricité C Faible
- Autres contrôles

VIDEOSONIC
Image, Son & Technique

Za les portes de l'Oise
Batîment B2 – rue Henri Becquerel
60230 CHAMBLY

Tel : 01 75 01 60 40
Fax : 01 75 01 60 41
@ : contact@videosonic.fr

BILLOT M

13/09/2019

Salles collaboratives 18+10places - R+9 A

AON

31 - 35 rue de la Fédération - 75015 PARIS

DIMENSION			RÉV
		Synoptique 9A3 (10p)	1
ECHELLE 1:1		FEUILLE 3 / 4	

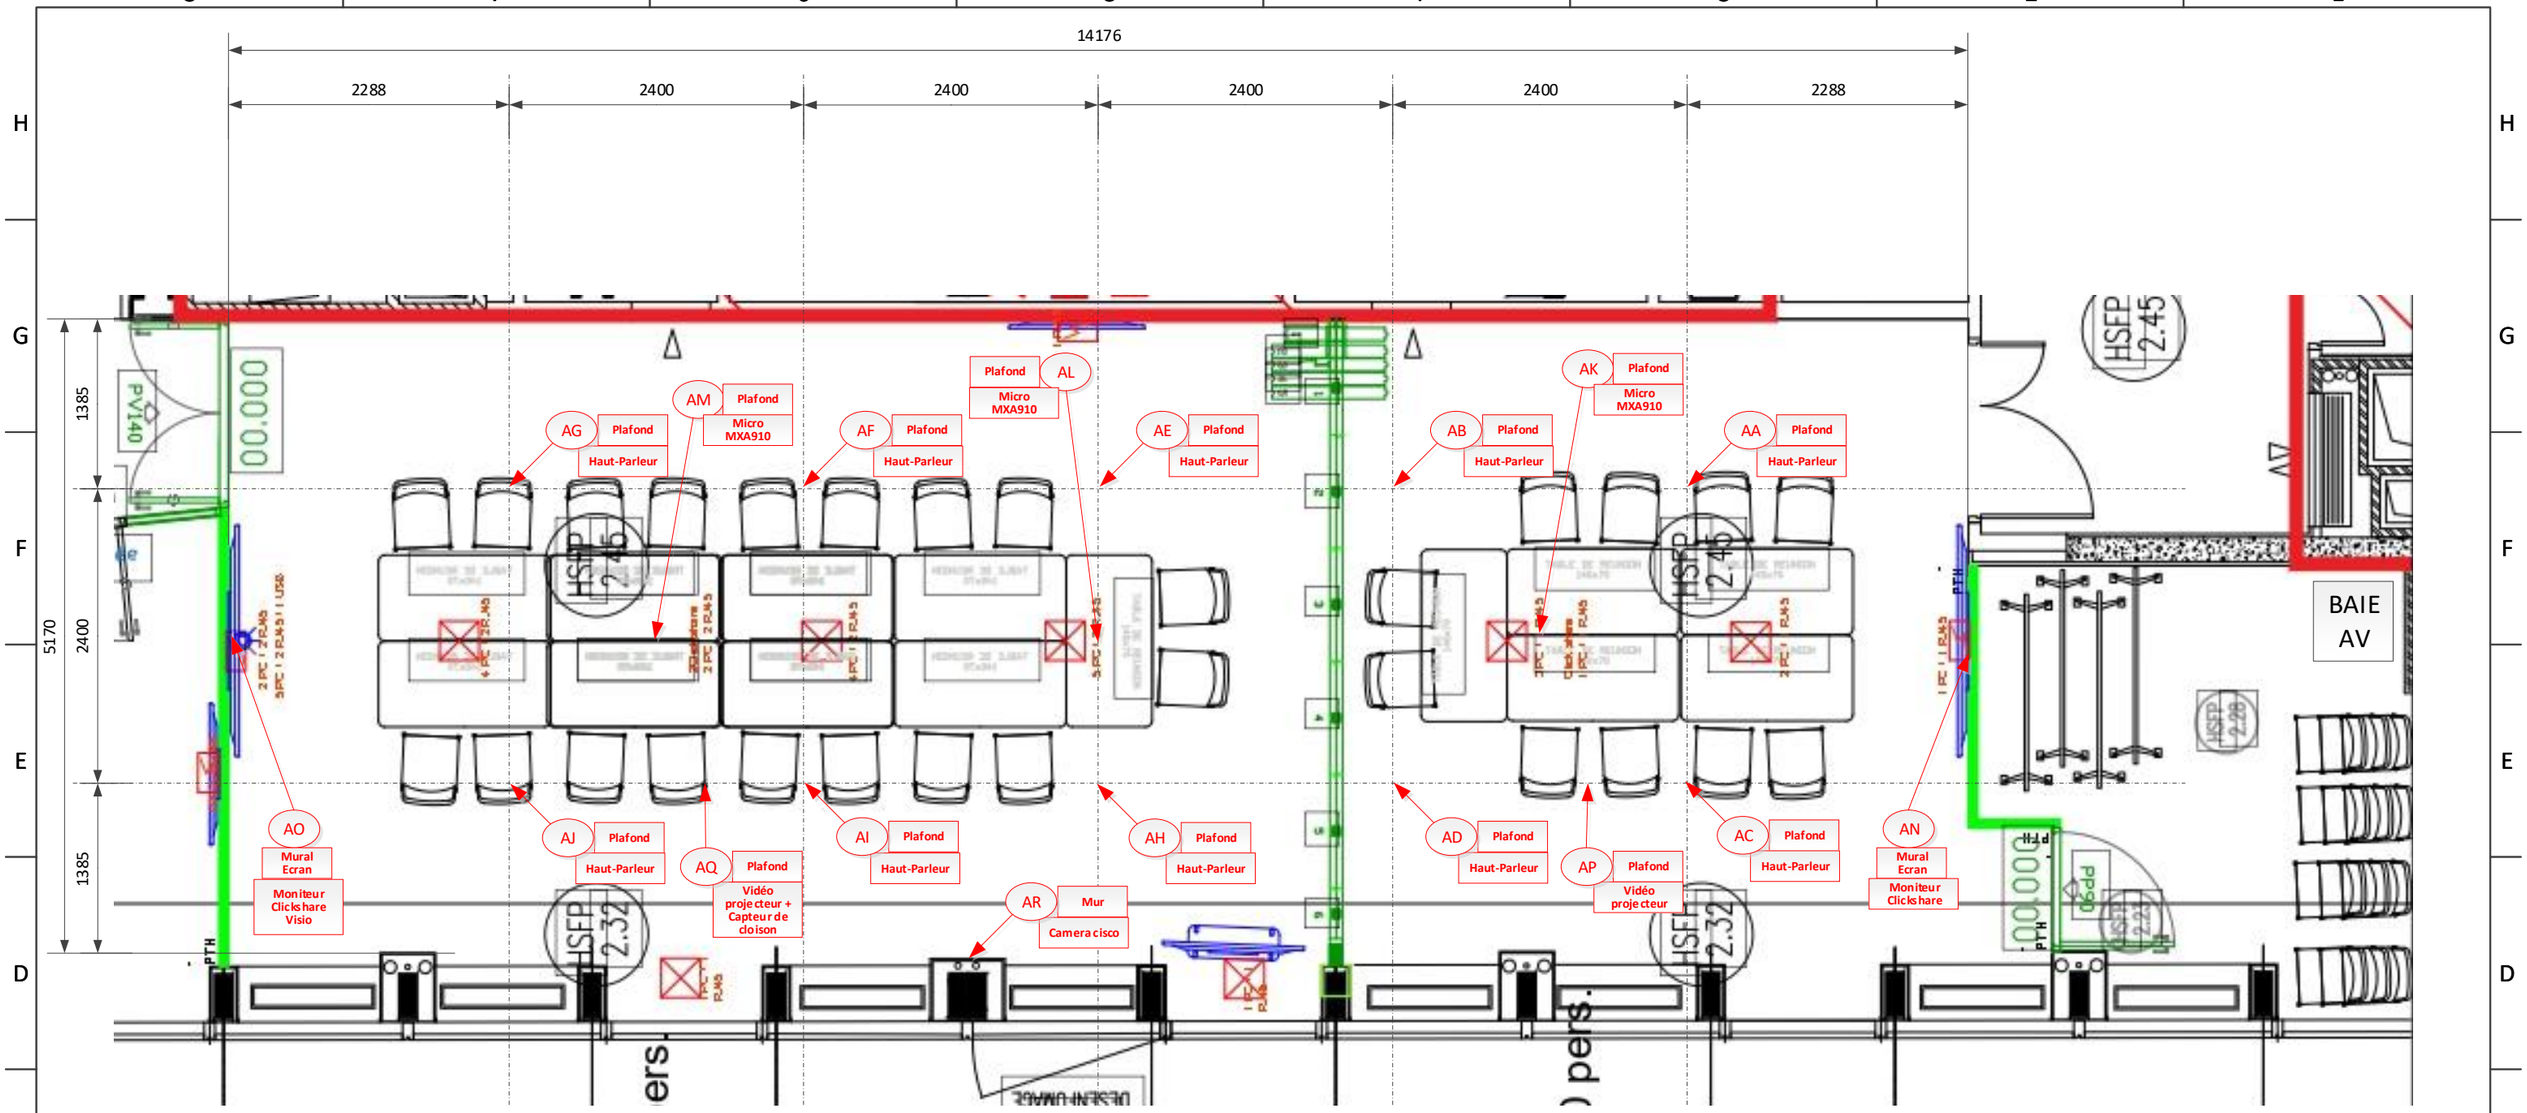

XX LOCALISATION

1m 2m 3m 4m 5m

3000

VIDEOSONIC
Image, Son & Technique
Za les portes de l'Oise
Batîment B2 – rue Henri Becquerel
60230 CHAMBLY
Tel : 01 75 01 60 40
Fax : 01 75 01 60 41
@ : contact@videosonic.fr

BILLOT M

13/09/2019

Salles collaboratives 18+10places - R+9 A

AON

31 - 35 rue de la Fédération - 75015 PARIS

Plan de salle

DIMENSION		RÉV
		1
ECHELLE 1:50	FEUILLE 4 / 4	