AON

R+9 B1

Synoptiques d’exécution salles modulables 14+14p

VIDEOSONIC
Image, Son & Technique

Za les portes de l’Oise
Batîment B2 – rue Henri
Becquerel
60230 CHAMBLY
Tel : 01 75 01 60 40
Fax : 01 75 01 60 41
@ : contact@videosonic.fr

Salles modulables 14+14places - R+9 B1

AON
31 - 35 rue de la Fédération - 75015 PARIS

BILLOT M

06/12/2024

DIMENSION			RÉV
		Page de Garde	1
ECHELLE 1:1			FEUILLE 1 / 4

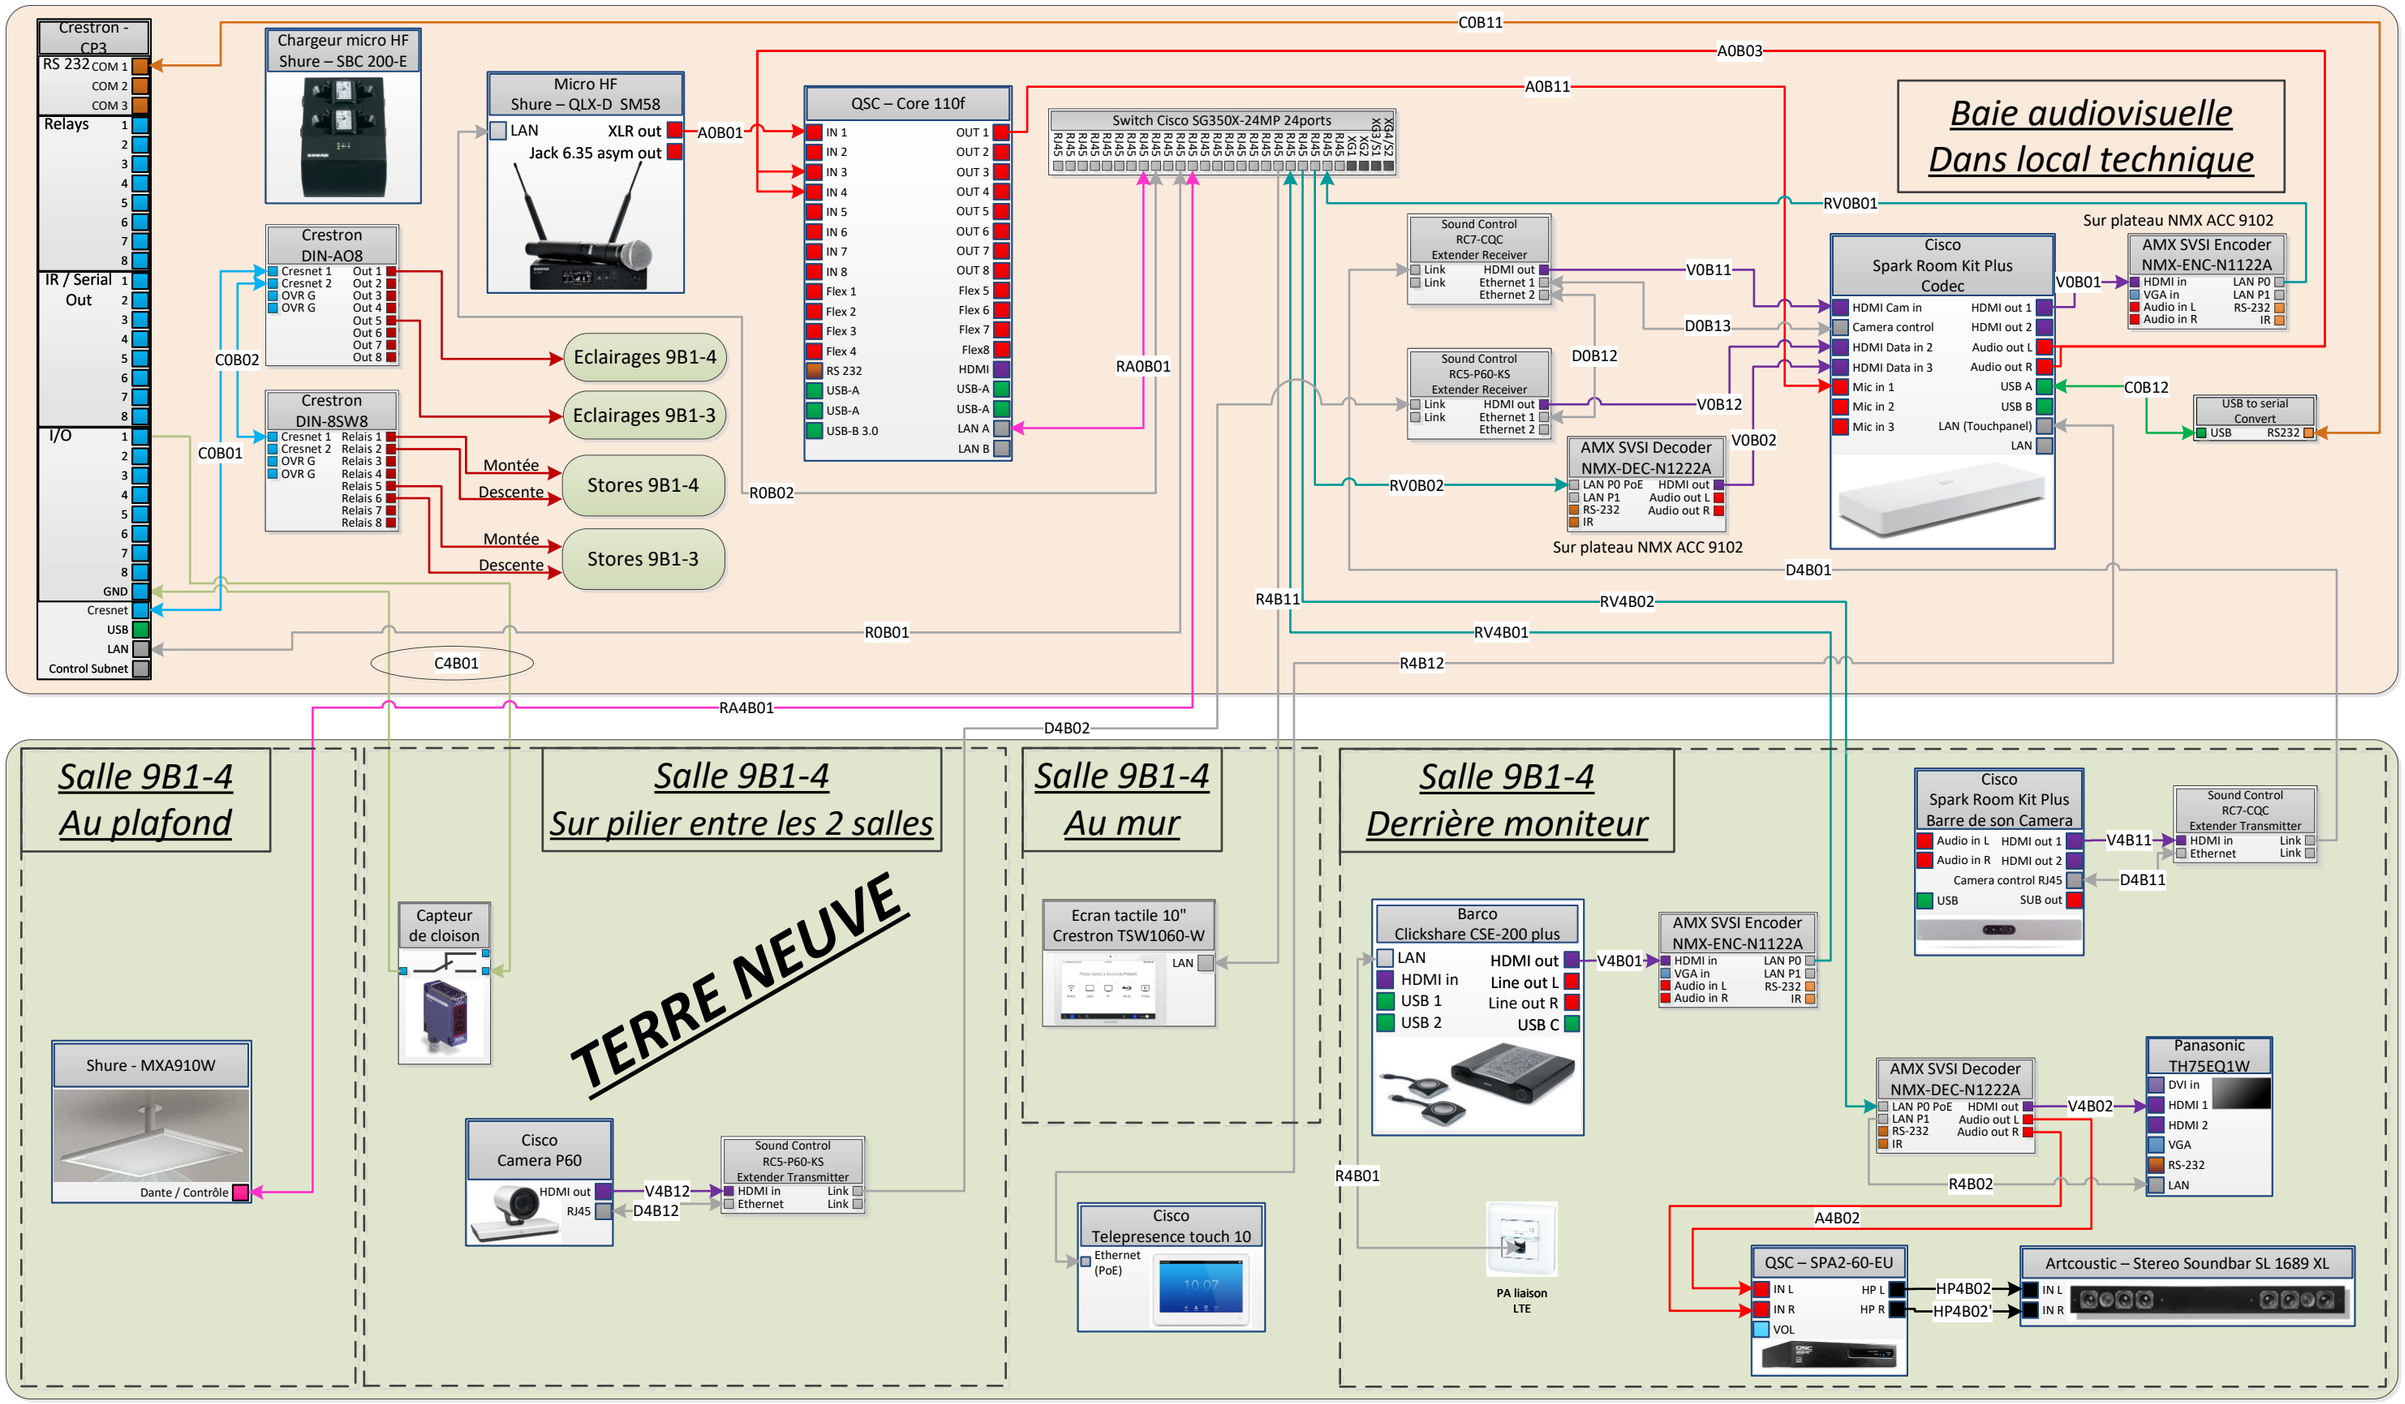

LEGENDE

- HDMI
- Audio
- Speakers
- USB
- RS232
- RJ45 cat6
- Audio Dante (RJ45 Cat6)
- HDBT/DTP/XTP
- DVI
- VGA
- HD SDI
- Display port
- Electricité C Fort
- Electricité C Faible
- Autres contrôles

VIDEOSONIC
Image, Son & Technique

Za les portes de l'Oise
Batîment B2 – rue Henri Becquerel
60230 CHAMBLY
Tel : 01 75 01 60 40
Fax : 01 75 01 60 41
@ : contact@videosonic.fr

BILLOT M

06/12/2024

Salles modulables 14+14places - R+9 B1

AON

31 - 35 rue de la Fédération - 75015 PARIS

DIMENSION			RÉV
		SYNOPTIQUE 9B1-4 TERRE NEUVE + BAIE	1
ECHELLE	1:1	FEUILLE	2 / 4

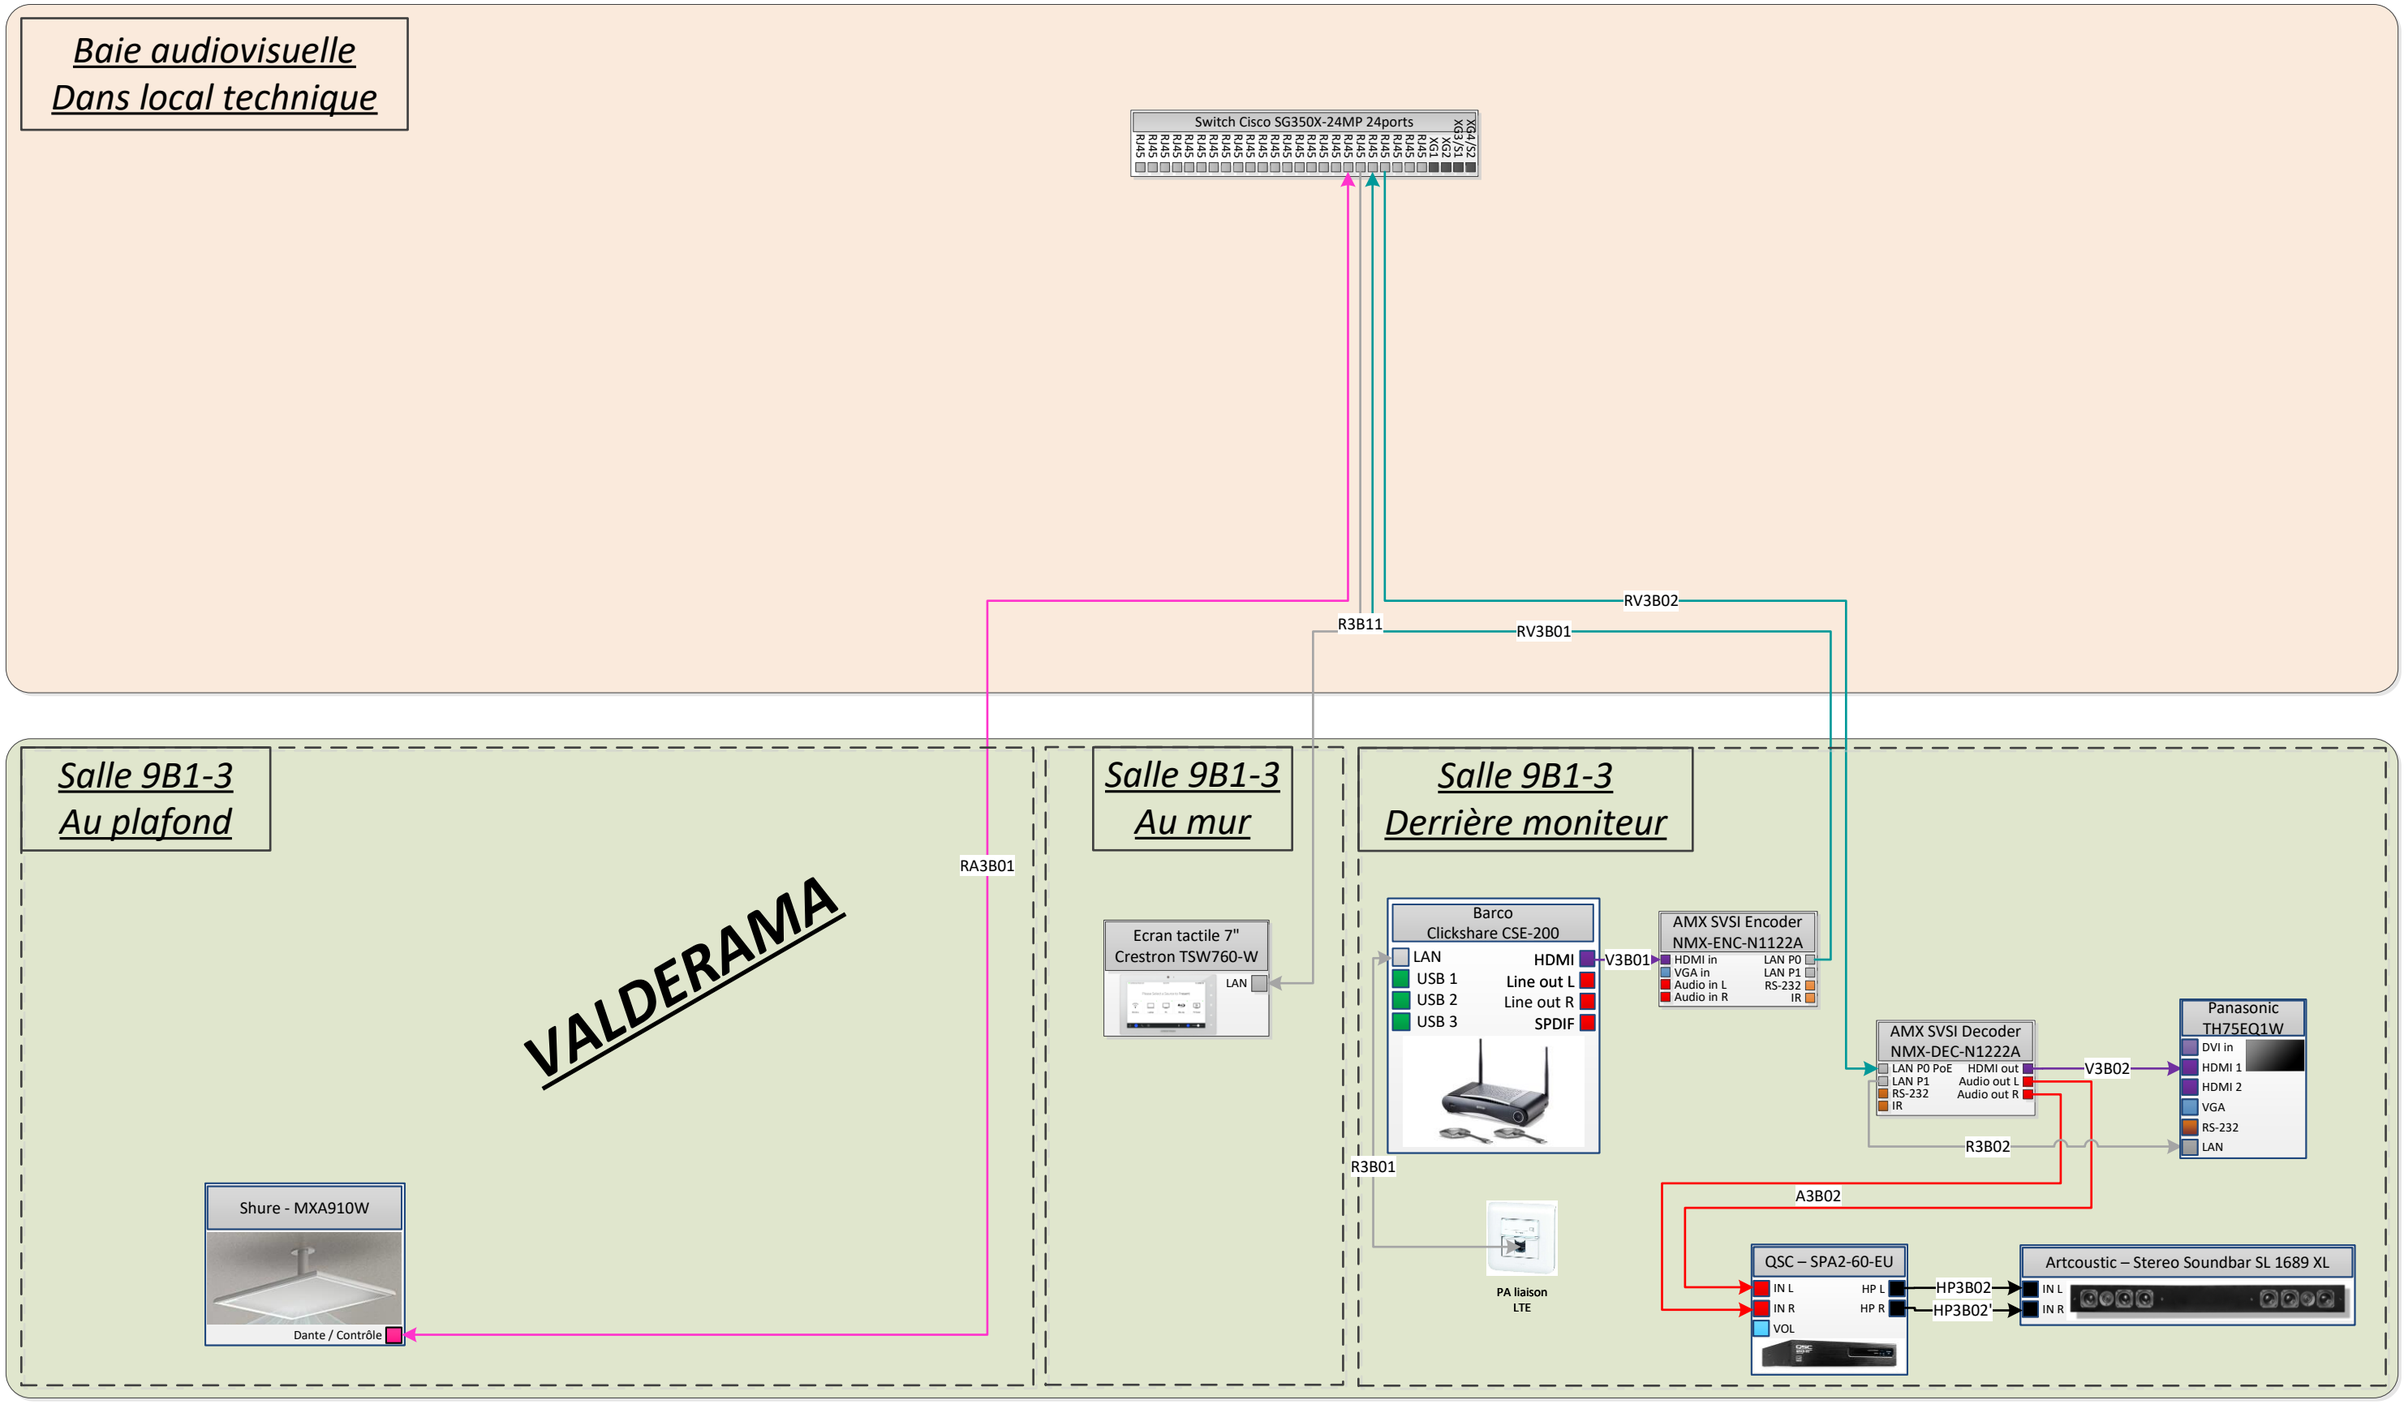

LEGENDE

- HDMI
- Audio
- Speakers
- USB
- RS232
- RJ45 cat6
- Audio Dante (RJ45 Cat6)
- HDBT/DTP/XTP
- DVI
- VGA
- HD SDI
- Display port
- Electricité C Fort
- Electricité C Faible
- Autres contrôles

VIDEOSONIC
Image, Son & Technique

Za les portes de l'Oise
Batîment B2 – rue Henri Becquerel
60230 CHAMBLY

Tel : 01 75 01 60 40
Fax : 01 75 01 60 41
@ : contact@videosonic.fr

BILLOT M

06/12/2024

Salles modulables 14+14places - R+9 B1

AON

31 - 35 rue de la Fédération - 75015 PARIS

DIMENSION			RÉV
		Synoptique 9B1-3 VALDERAMA	1
ECHELLE	1:1	FEUILLE	3 / 4

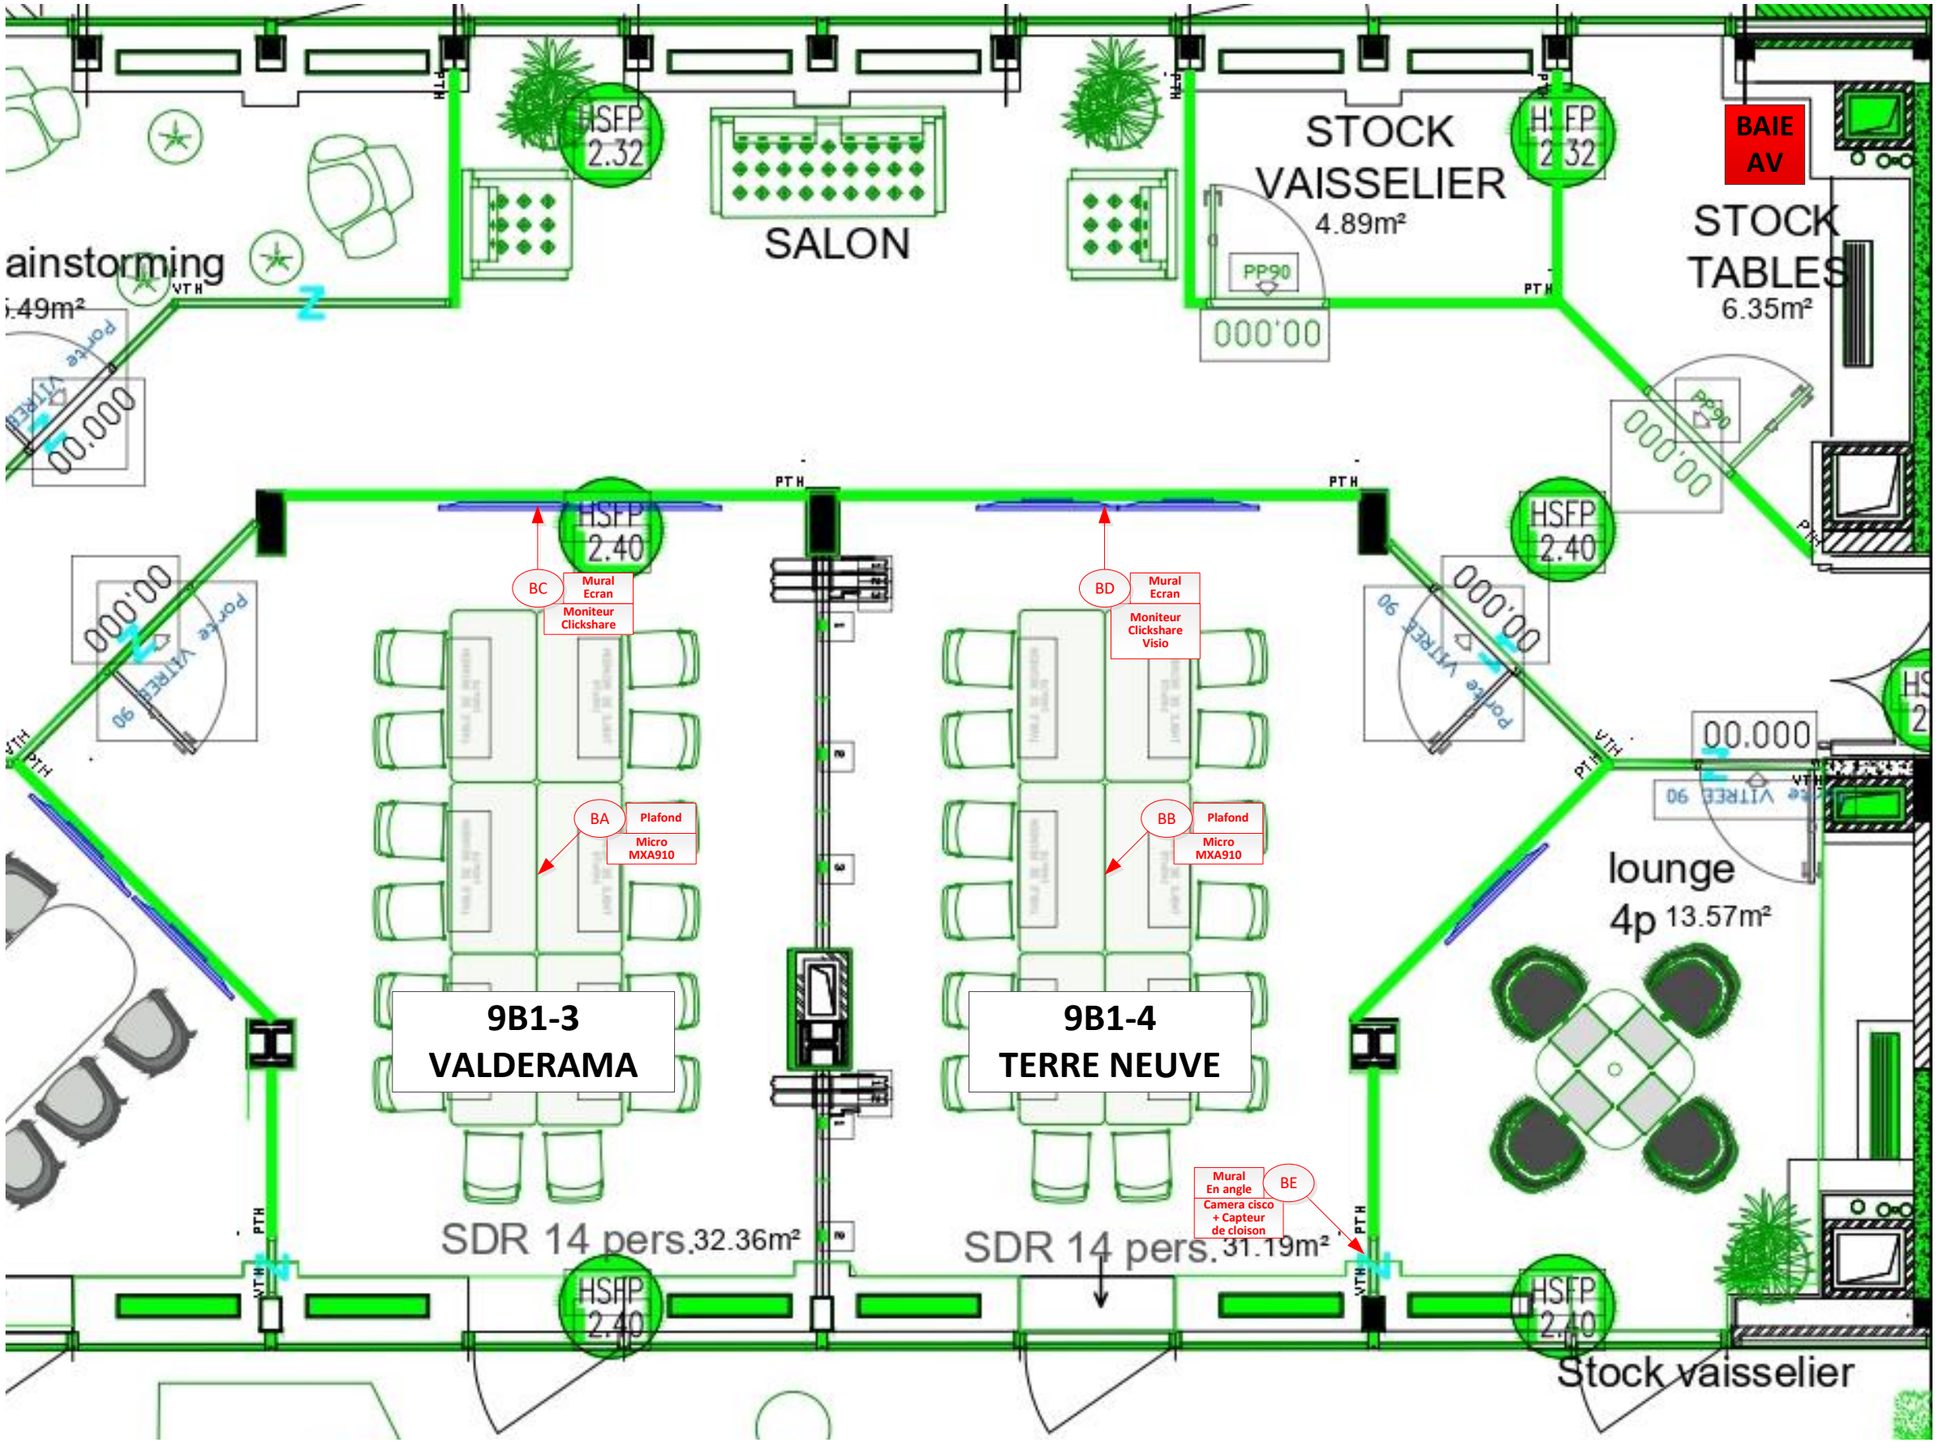

XX LOCALISATION

1m 2m 3m 4m 5m

3000,00

VIDEOSONIC
Image, Son & Technique

Za les portes de l'Oise
Batîment B2 – rue Henri
Becquerel
60230 CHAMBLY
Tel : 01 75 01 60 40
Fax : 01 75 01 60 41
@ : contact@videosonic.fr

Salles modulables 14+14places - R+9 B1

AON
31 - 35 rue de la Fédération - 75015 PARIS

BILLOT M	DIMENSION	Plan de salle	RÉV 1
06/12/2024	ECHELLE 1:50		FEUILLE 4 / 4