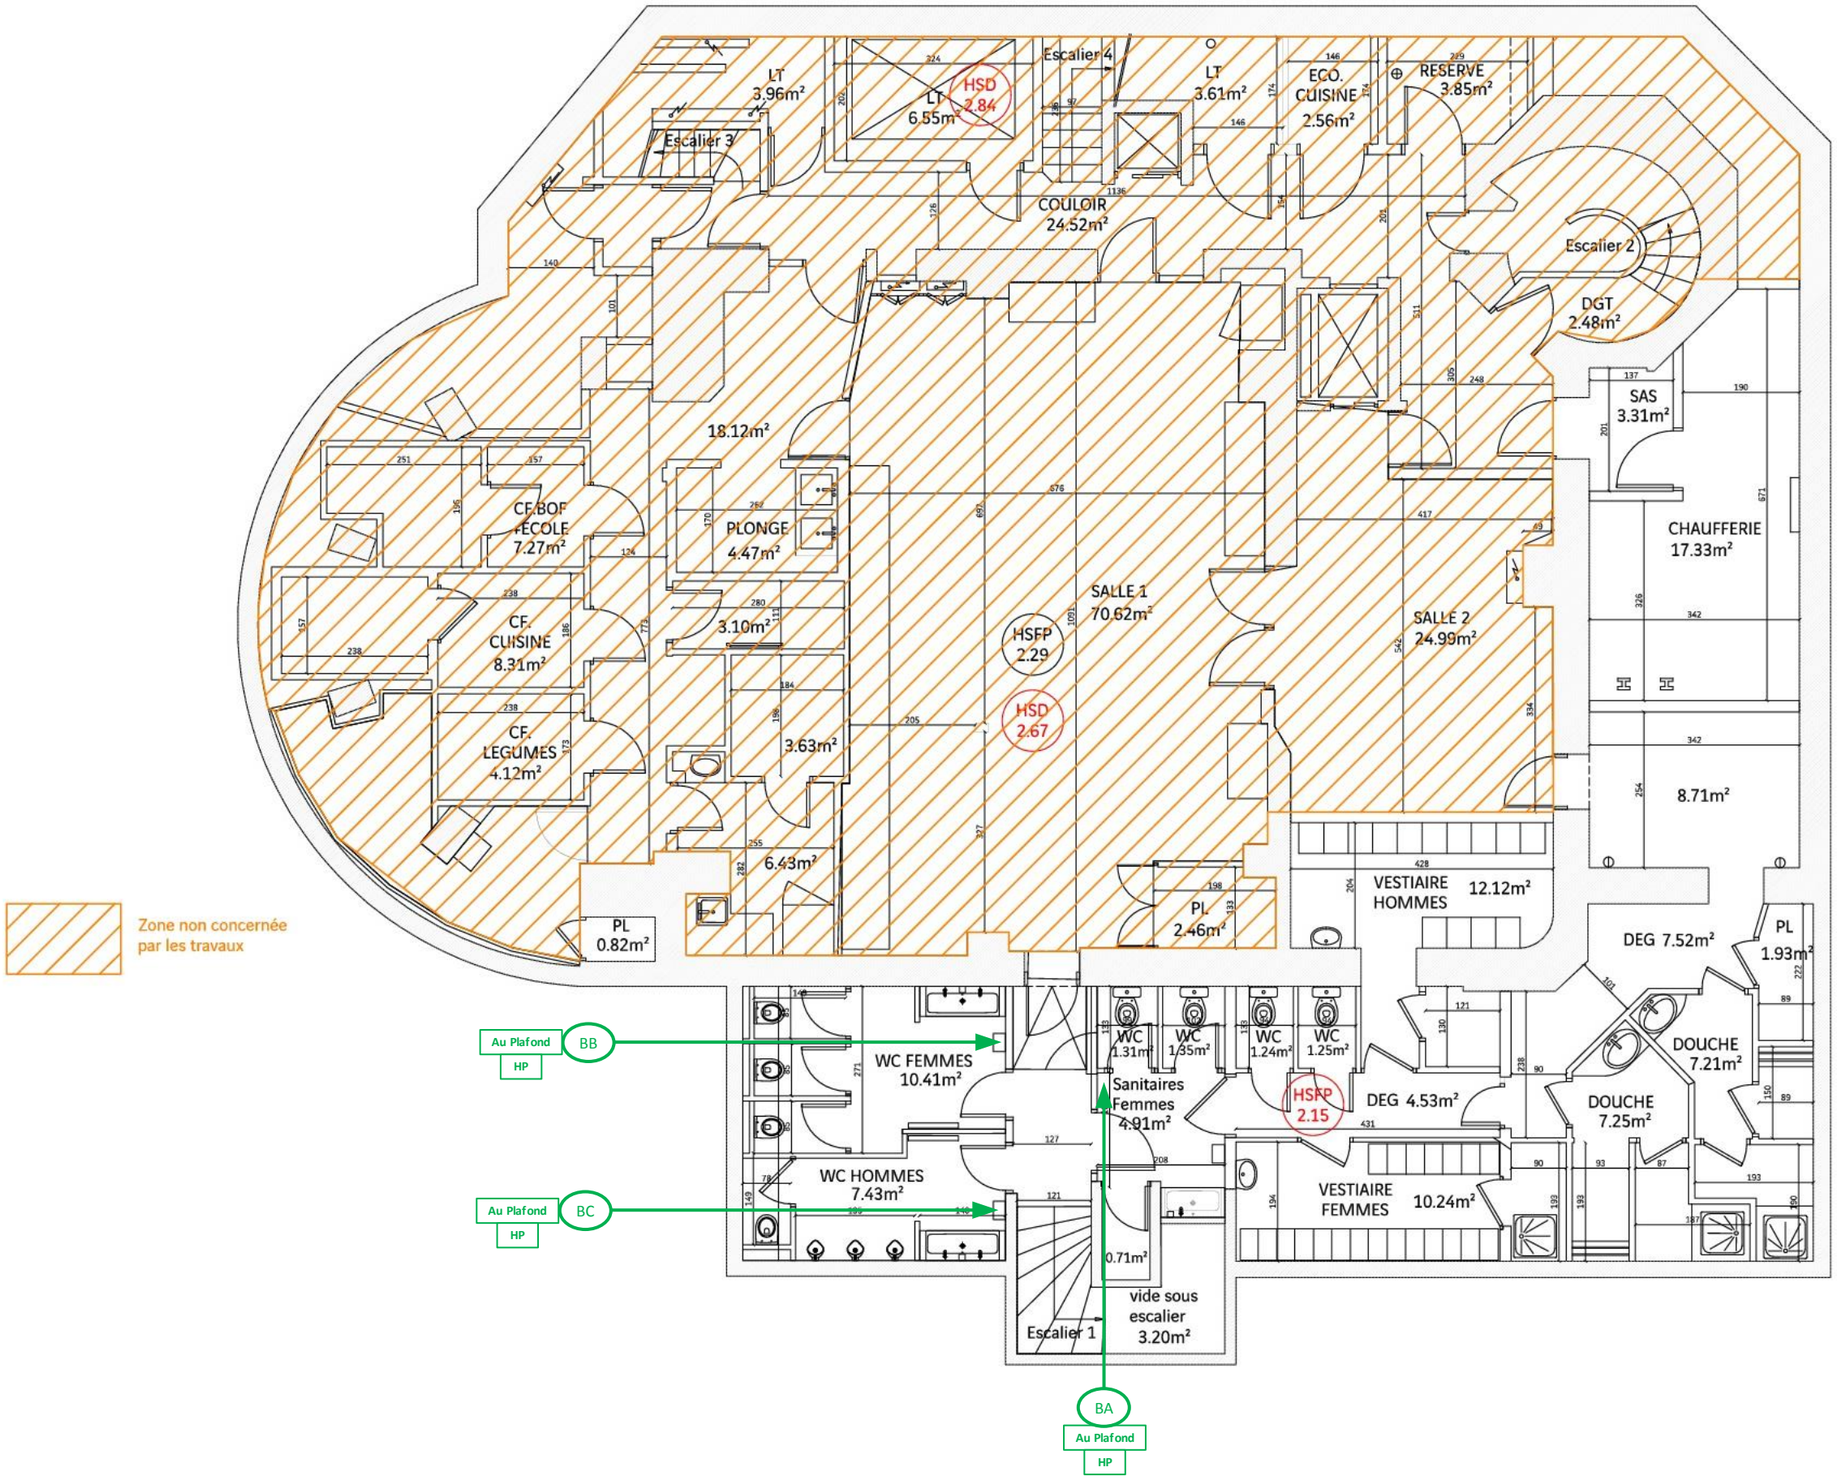

(u) L'USINE L'USINE 102C rue Amelot 75011 Paris Représentée par Madame Céline Peudenier	C.B.I. Etablissement de Camponon Bernard Construction 85 Avenue Victor Hugo CS-30041 92563 Rueil-Malmaison Cedex	Pavillon Elysée 10, Avenue des champs Elysées 75008 Paris		Date: 16.02.2018	Echelle: 1/100
	Dessiné par: MF	04a PLAN PROJET	R-1	Phase: PROJET	Ind: e

Propriété intellectuelle : Ce document, propriété de l'agence,dont la copie est protégée, ne peut être communiqué à une personne étrangère au projet sans autorisation écrite

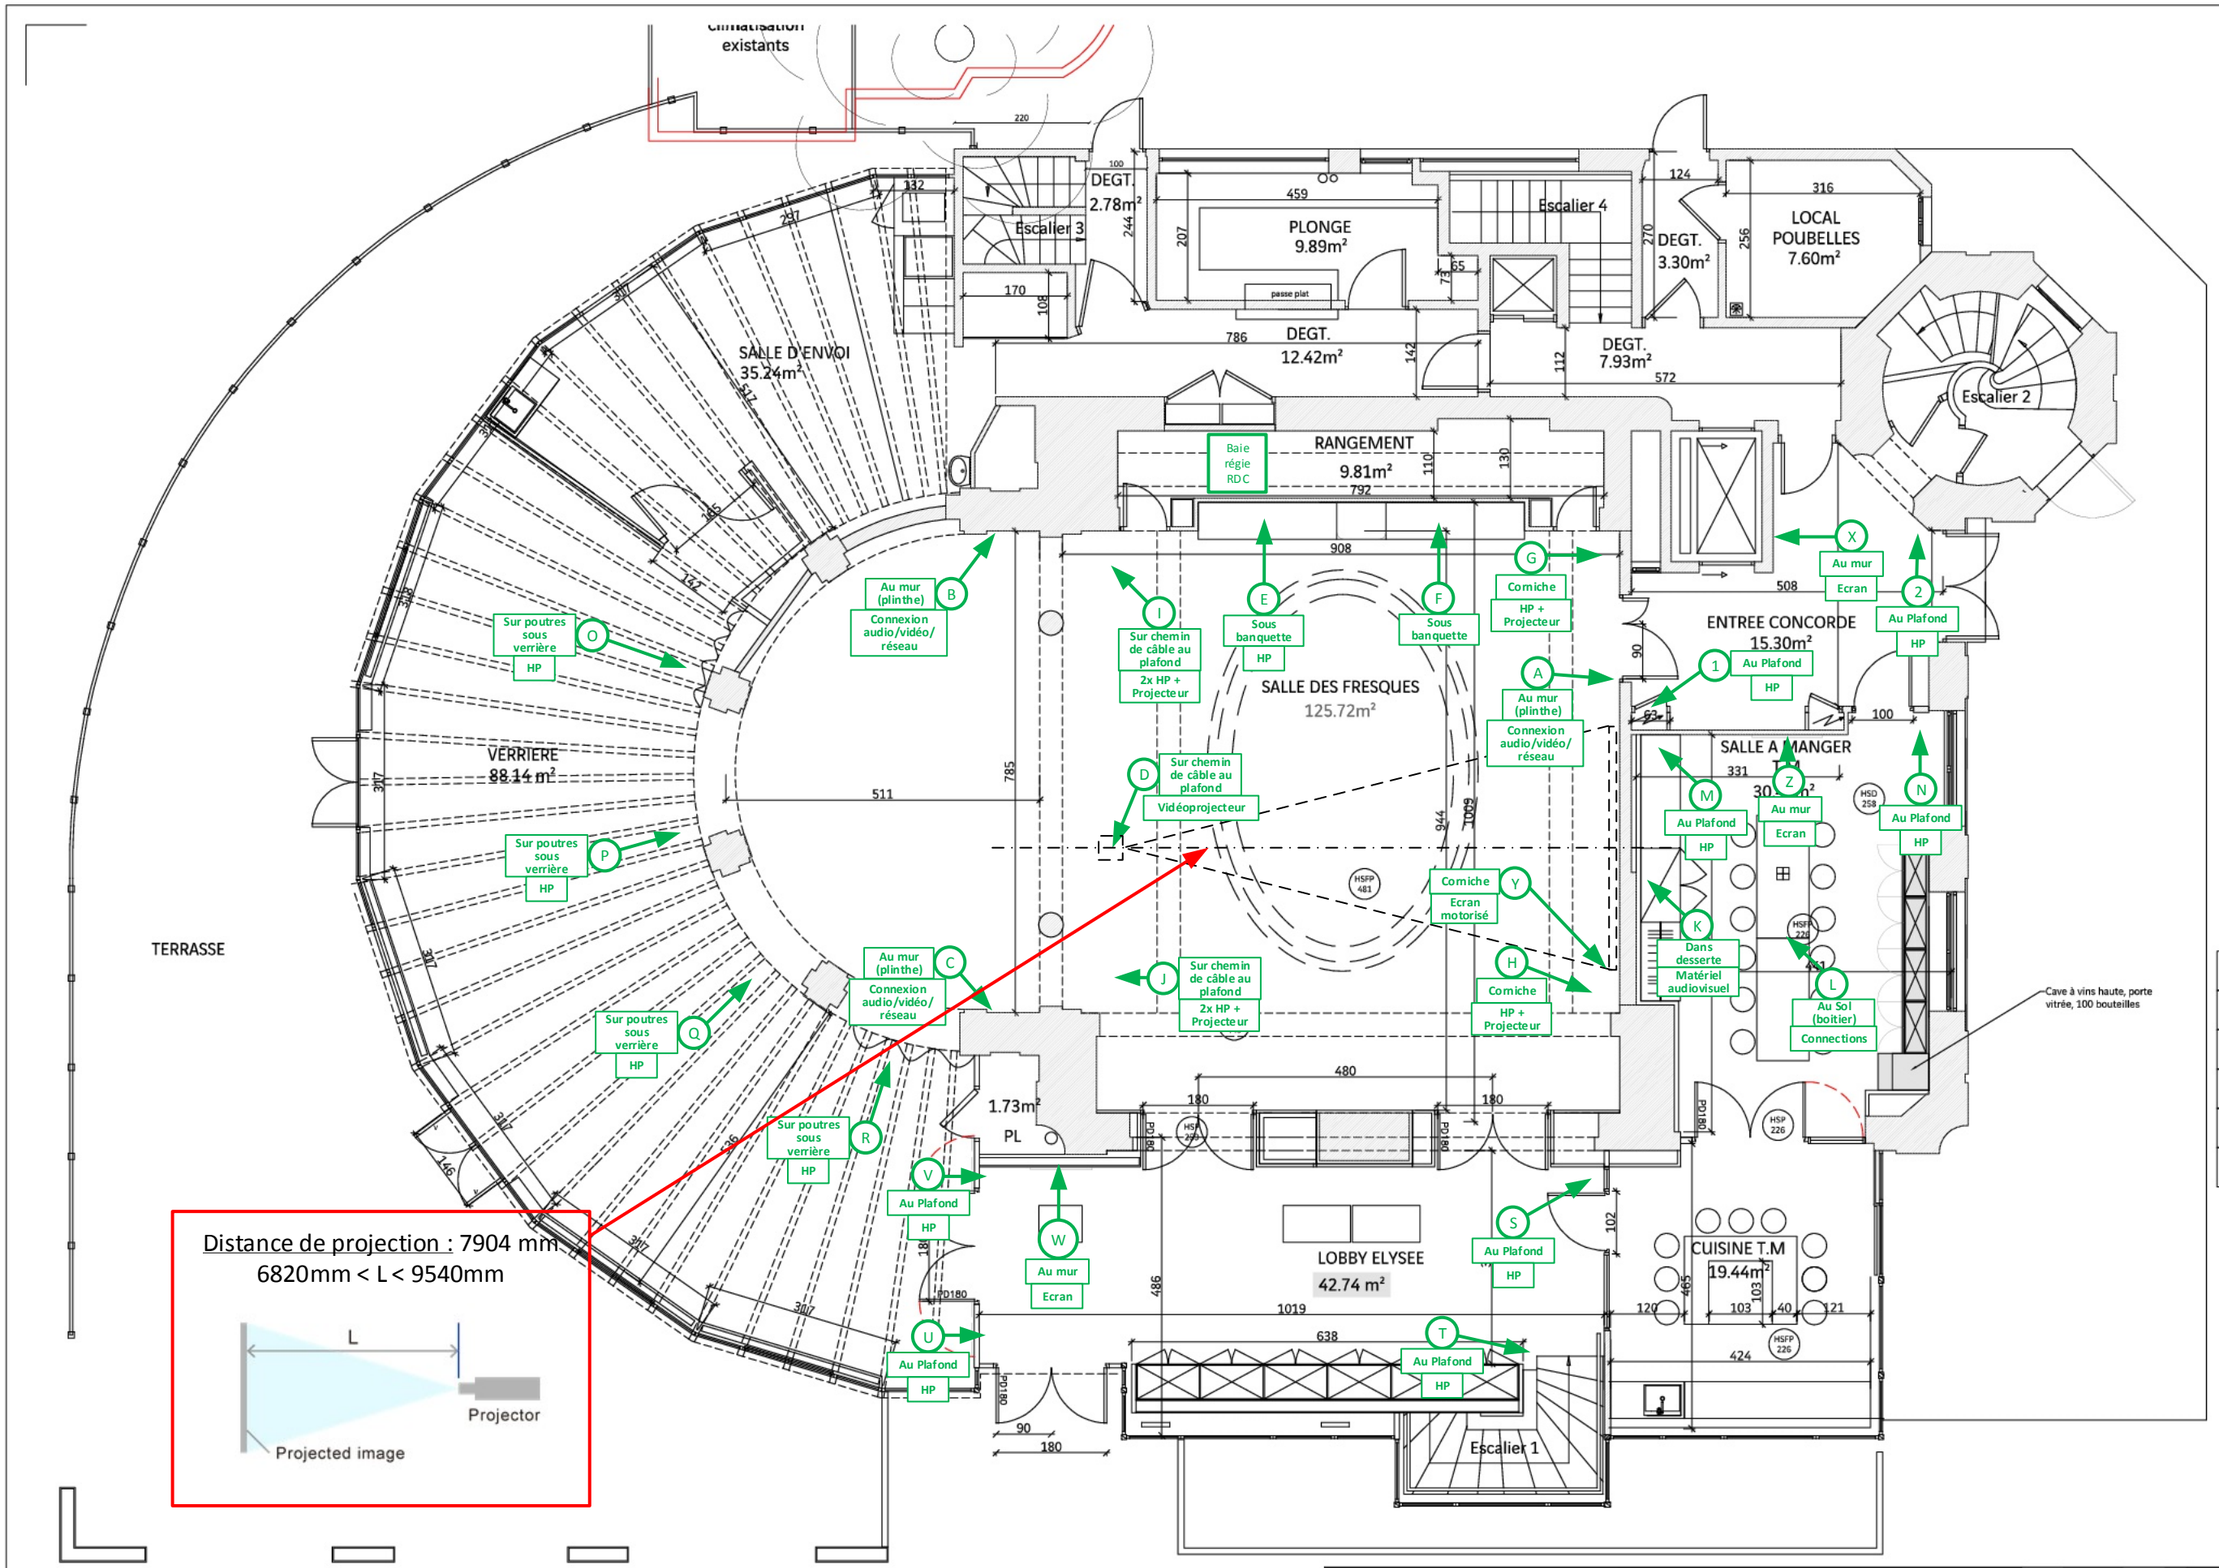

SALLE DES FRESQUE	125.72 m²
SAM + CUISINE T.M	49.88 m²
LOBBY	58.04 m²
VERRIERE	88.14 m²
BACK OFFICE	88.97 m²
TOTAL m²	410.75 m²

L'USINE
102C rue Amelot
75013 Paris
Représentée par Madame Céline Peudenier

C.B.I.
Etablissement de Campenon Bernard Construction
85 Avenue Victor Hugo
CS-30041
92563 Rueil-Malmaison Cedex

Pavillon Elysée
10 Avenue des champs elysées
75008 Paris

Date: 26.03.2018

Echelle: 1/100

Dessiné par: MF

04b PLAN PROJET

RDC

Phase: PROJET

Ind: F

Propriété intellectuelle :Ce document, propriété de l'agence,dont la copie est protégée, ne peut être communiqué à une personne étrangère au projet sans autorisation écrite

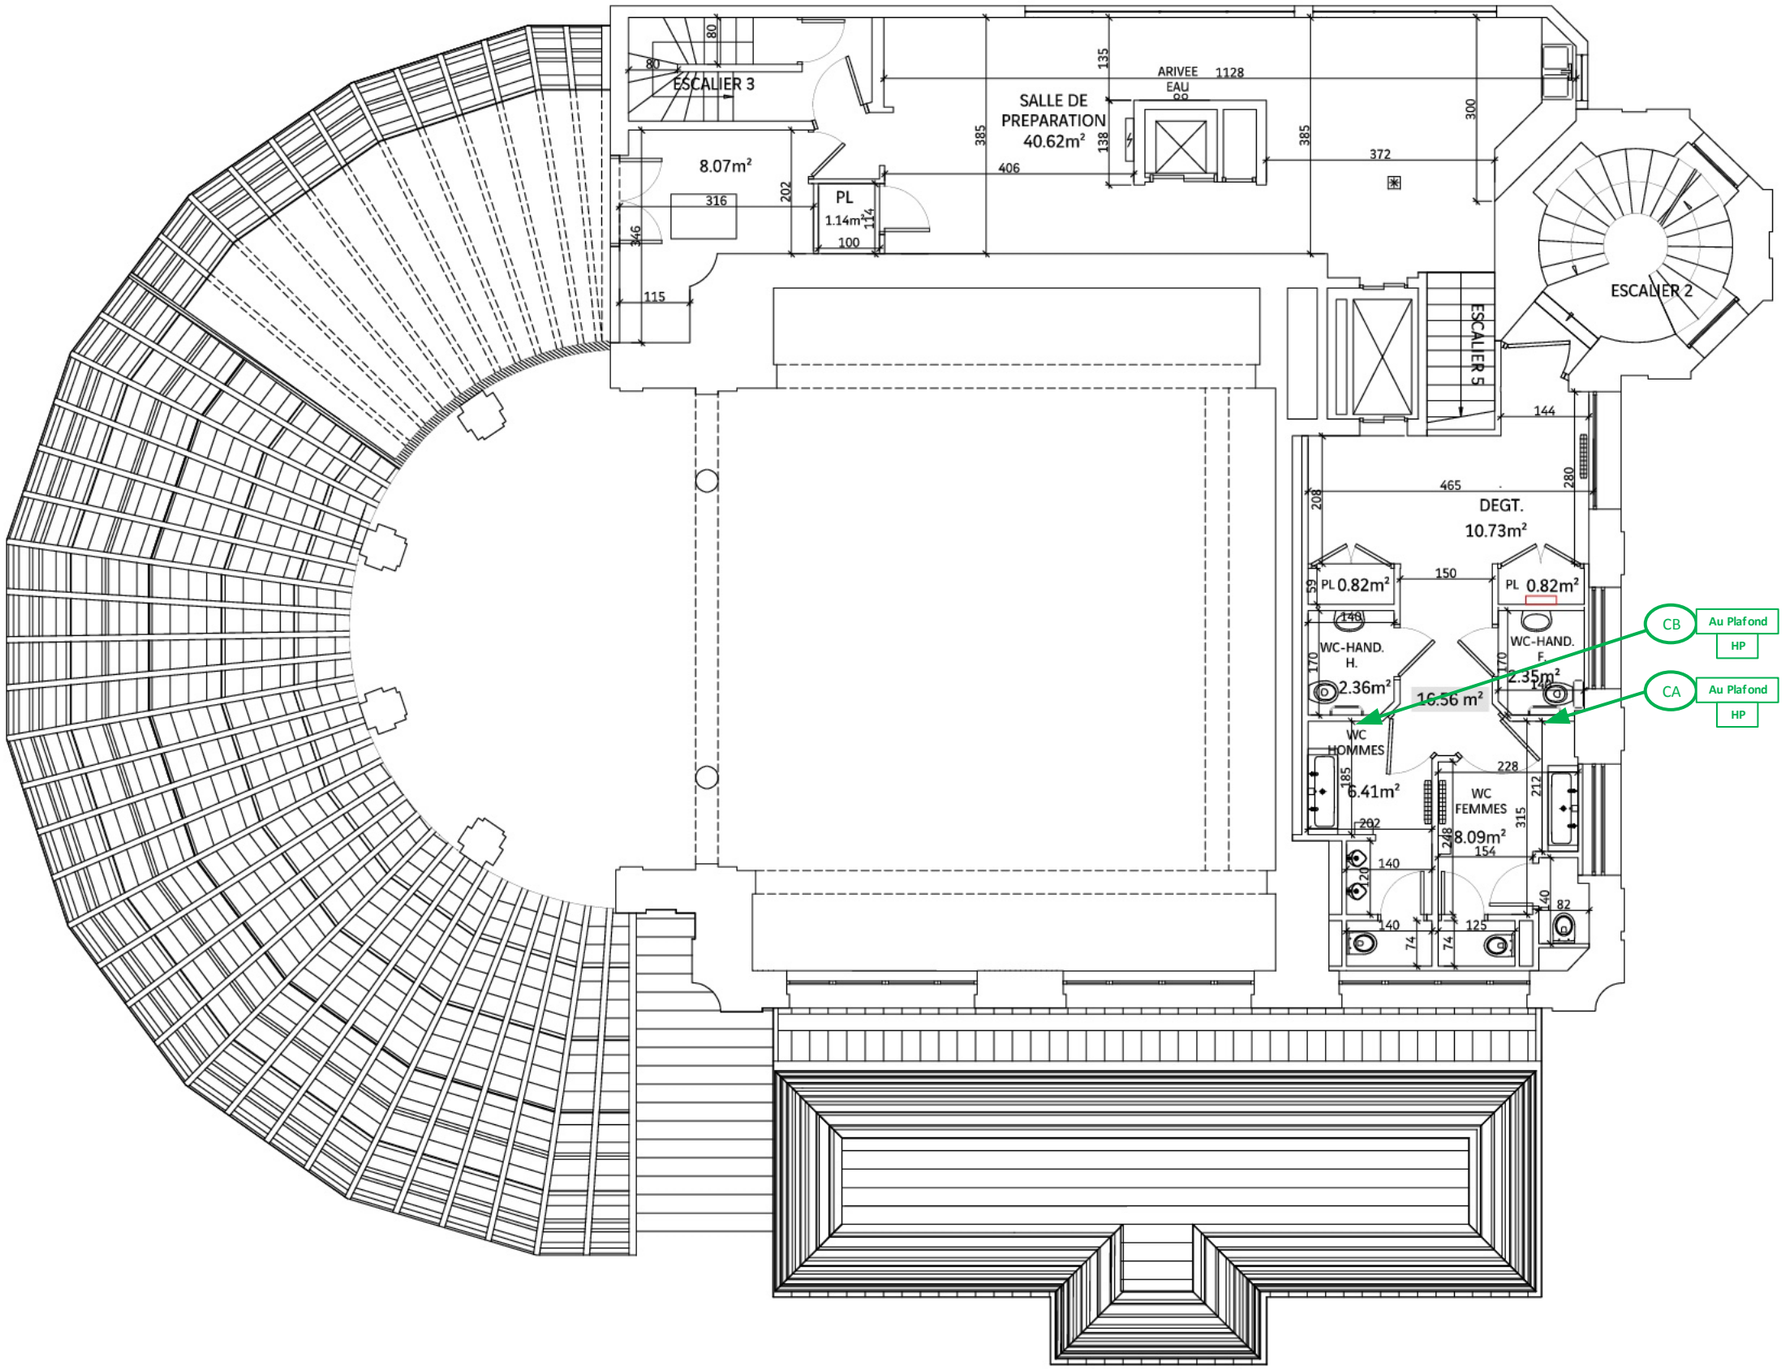

(u) L'USINE Direction des Projets Immobiliers 13 quai Gailleton B.P. 2216 69214 Lyon Cedex 02	C.B.I. Etablissement de Campenon Bernard Construction 85 Avenue Victor Hugo CS-30041 92563 Rueil-Malmaison Cedex	Pavillon Elysée 10, Avenue des Champs Elysées 75008 Paris		Date: 26.03.2018	Echelle: 1/100
	Dessiné par: MF	04c PLAN PROJET	R+05	Phase: PROJET	Ind: F

Propriété intellectuelle : Ce document, propriété de l'agence,dont la copie est protégée, ne peut être communiqué à une personne étrangère au projet sans autorisation écrite

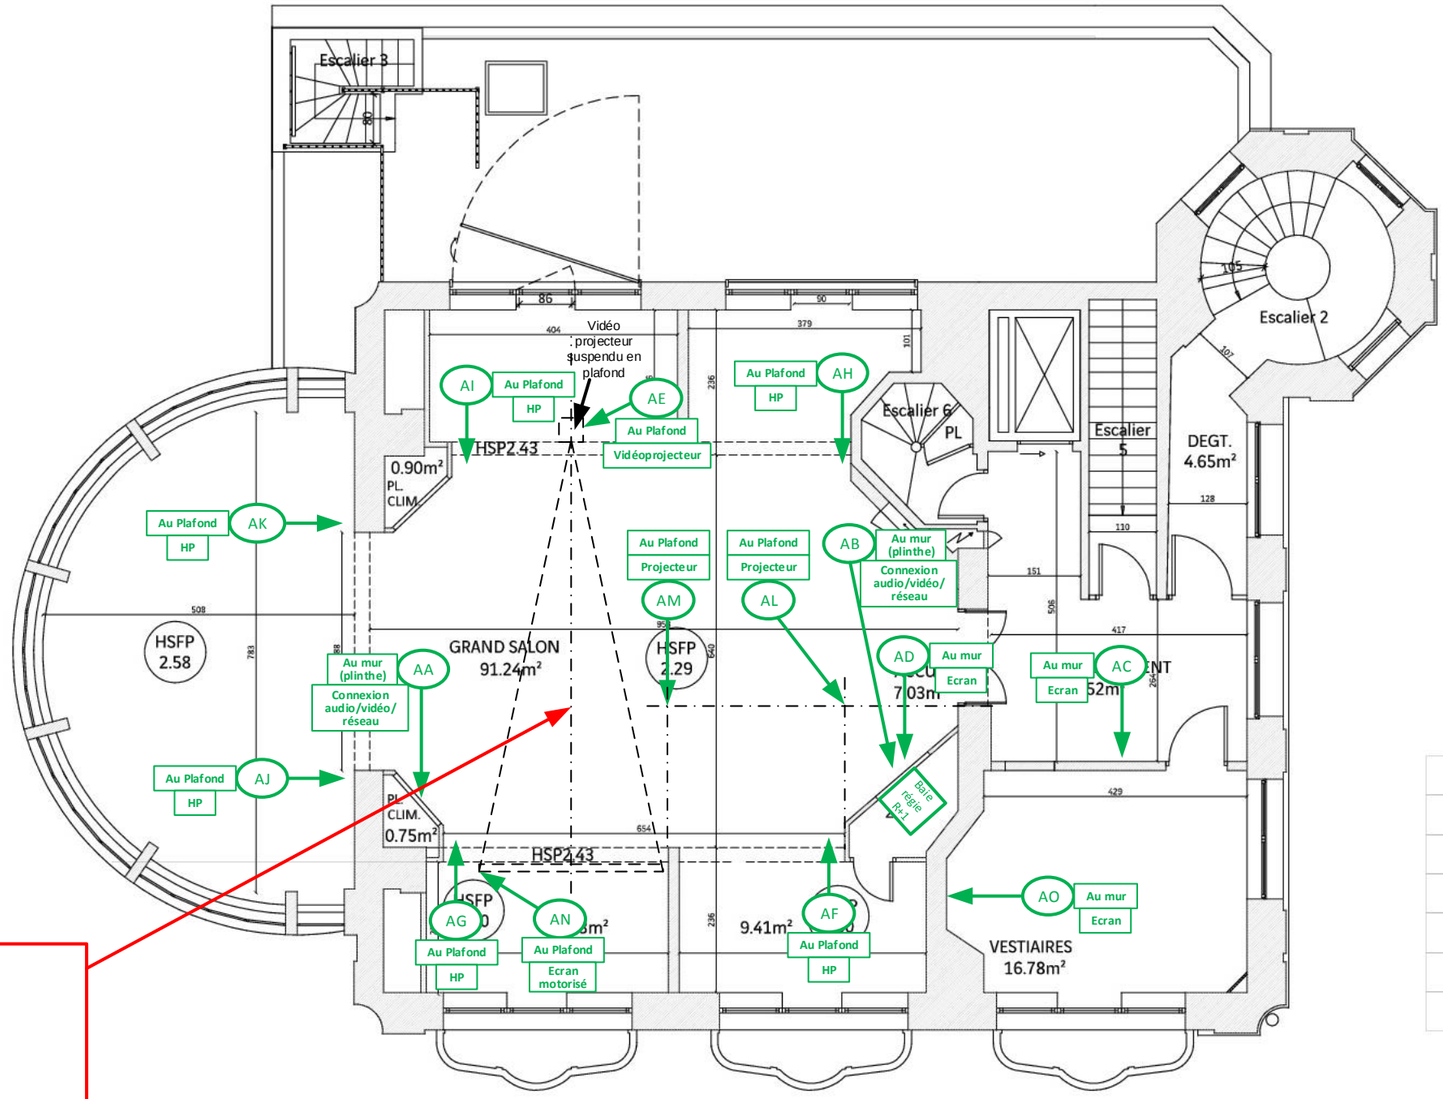

SERVICE BUFFET	26.82 m²
ACCUEIL	7.03 m²
GRAND SALON	91.24 m²
VESTIAIRES	16.78 m²
DEGAGEMENT	14.75 m²
DEGAGEMENT + PLACARD	8.28 m²
TOTAL m²	164.90 m²

Distance de projection
3842mm < L < 7725mm

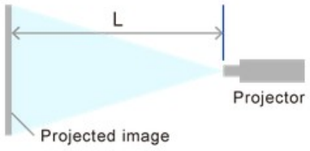

(u) L'USINE L'USINE 102C rue Amelot 75011 Paris Représentée par Madame Céline Peudenier	C.B.I. Etablissement de Camponon Bernard Construction 85 Avenue Victor Hugo CS-30041 92563 Rueil-Malmaison Cedex	Pavillon Elysée 10, Avenue des champs Elysées 75008 Paris		Date: 26.03.2018	Echelle: 1/100
	Dessiné par: MF	04d PLAN PROJET	R+1	Phase: PROJET	Ind: F

Propriété intellectuelle : Ce document, propriété de l'agence,dont la copie est protégée, ne peut être communiqué à une personne étrangère au projet sans autorisation écrite