Safran Aircraft Engines

Salle modulable-BÂTIMENT-D

Synoptiques, Plan de baie AV et positionnement

CFO/CFA

VIDEOSONIC
Image, Son & Technique
Za les portes de l'Oise
Batiment B2
rue Henri Becquerel
60230 CHAMBLY
Tel : 01 75 01 60 40
Fax : 01 75 01 60 41
t.fourmentraux@videosonic.fr

Safran Aircraft Engines - Salle Modulable - Synoptiques et plans d'execution VERSION CISCO.vsdm

SAFRAN AIRCRAFT ENGINES
SNECMA 1 RUE HENRI DESBRUÈRES ÉVRY-COURCOURONNES

Thierry FOURMENTRAUX

29 FÉVRIER 2024

DIMENSION	N° CODE	PAGE	RÉV
A3		Page de Garde	19/02/2026
ECHELLE 1:1		FEUILLE 1 / 9	

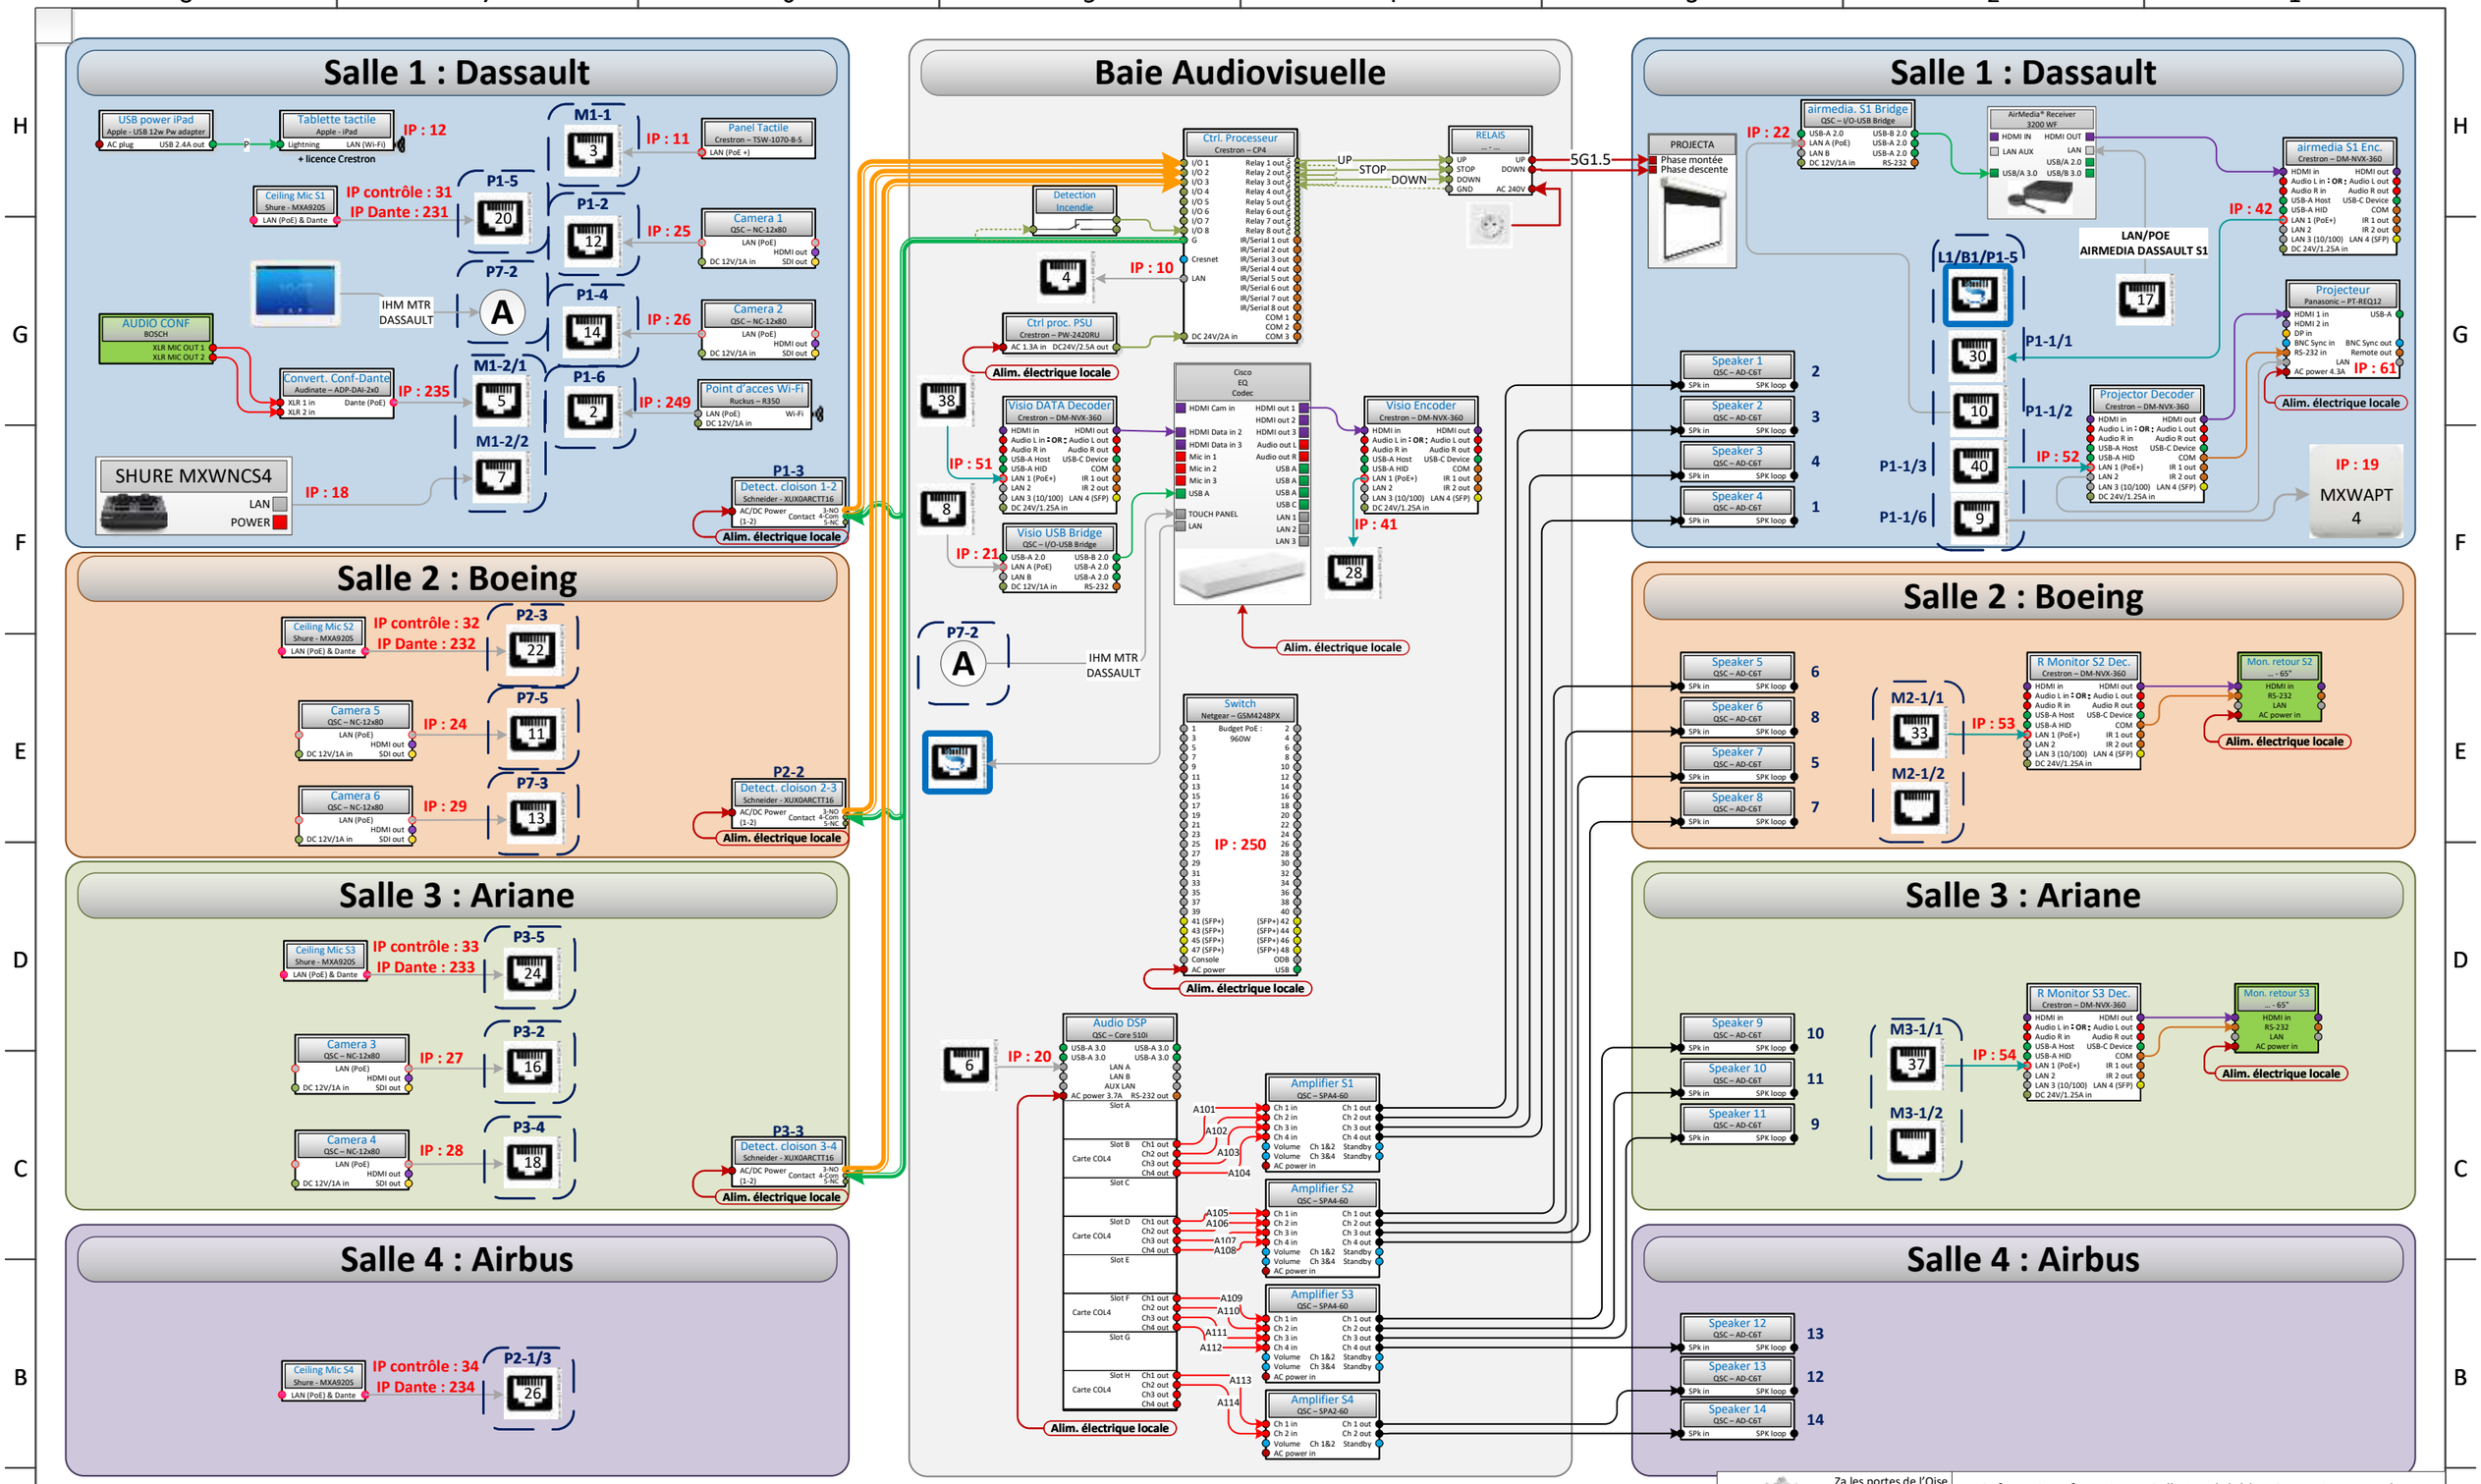

VIDEOSONIC
Za les portes de l'Oise
Batiment B2
rue Henri Becquerel
60230 CHAMBLY
Tel : 01 75 01 60 40
Fax : 01 75 01 60 41
t.fourmentraux@videosonic.fr

Safran Aircraft Engines - Salle Modulable - Synoptiques et plans d'execution VERSION CISCO.vsdm

SAFRAN AIRCRAFT ENGINES
SNECMA 1 RUE HENRI DESBRUÈRES ÉVRY-COURCOURONNES

Thierry FOURMENTRAUX

29 FÉVRIER 2024

DIMENSION	N° CODE	PAGE	RÉV
A3		Synoptique 1/2	19/02/2026
ECHELLE 1:1		FEUILLE 2 / 9	

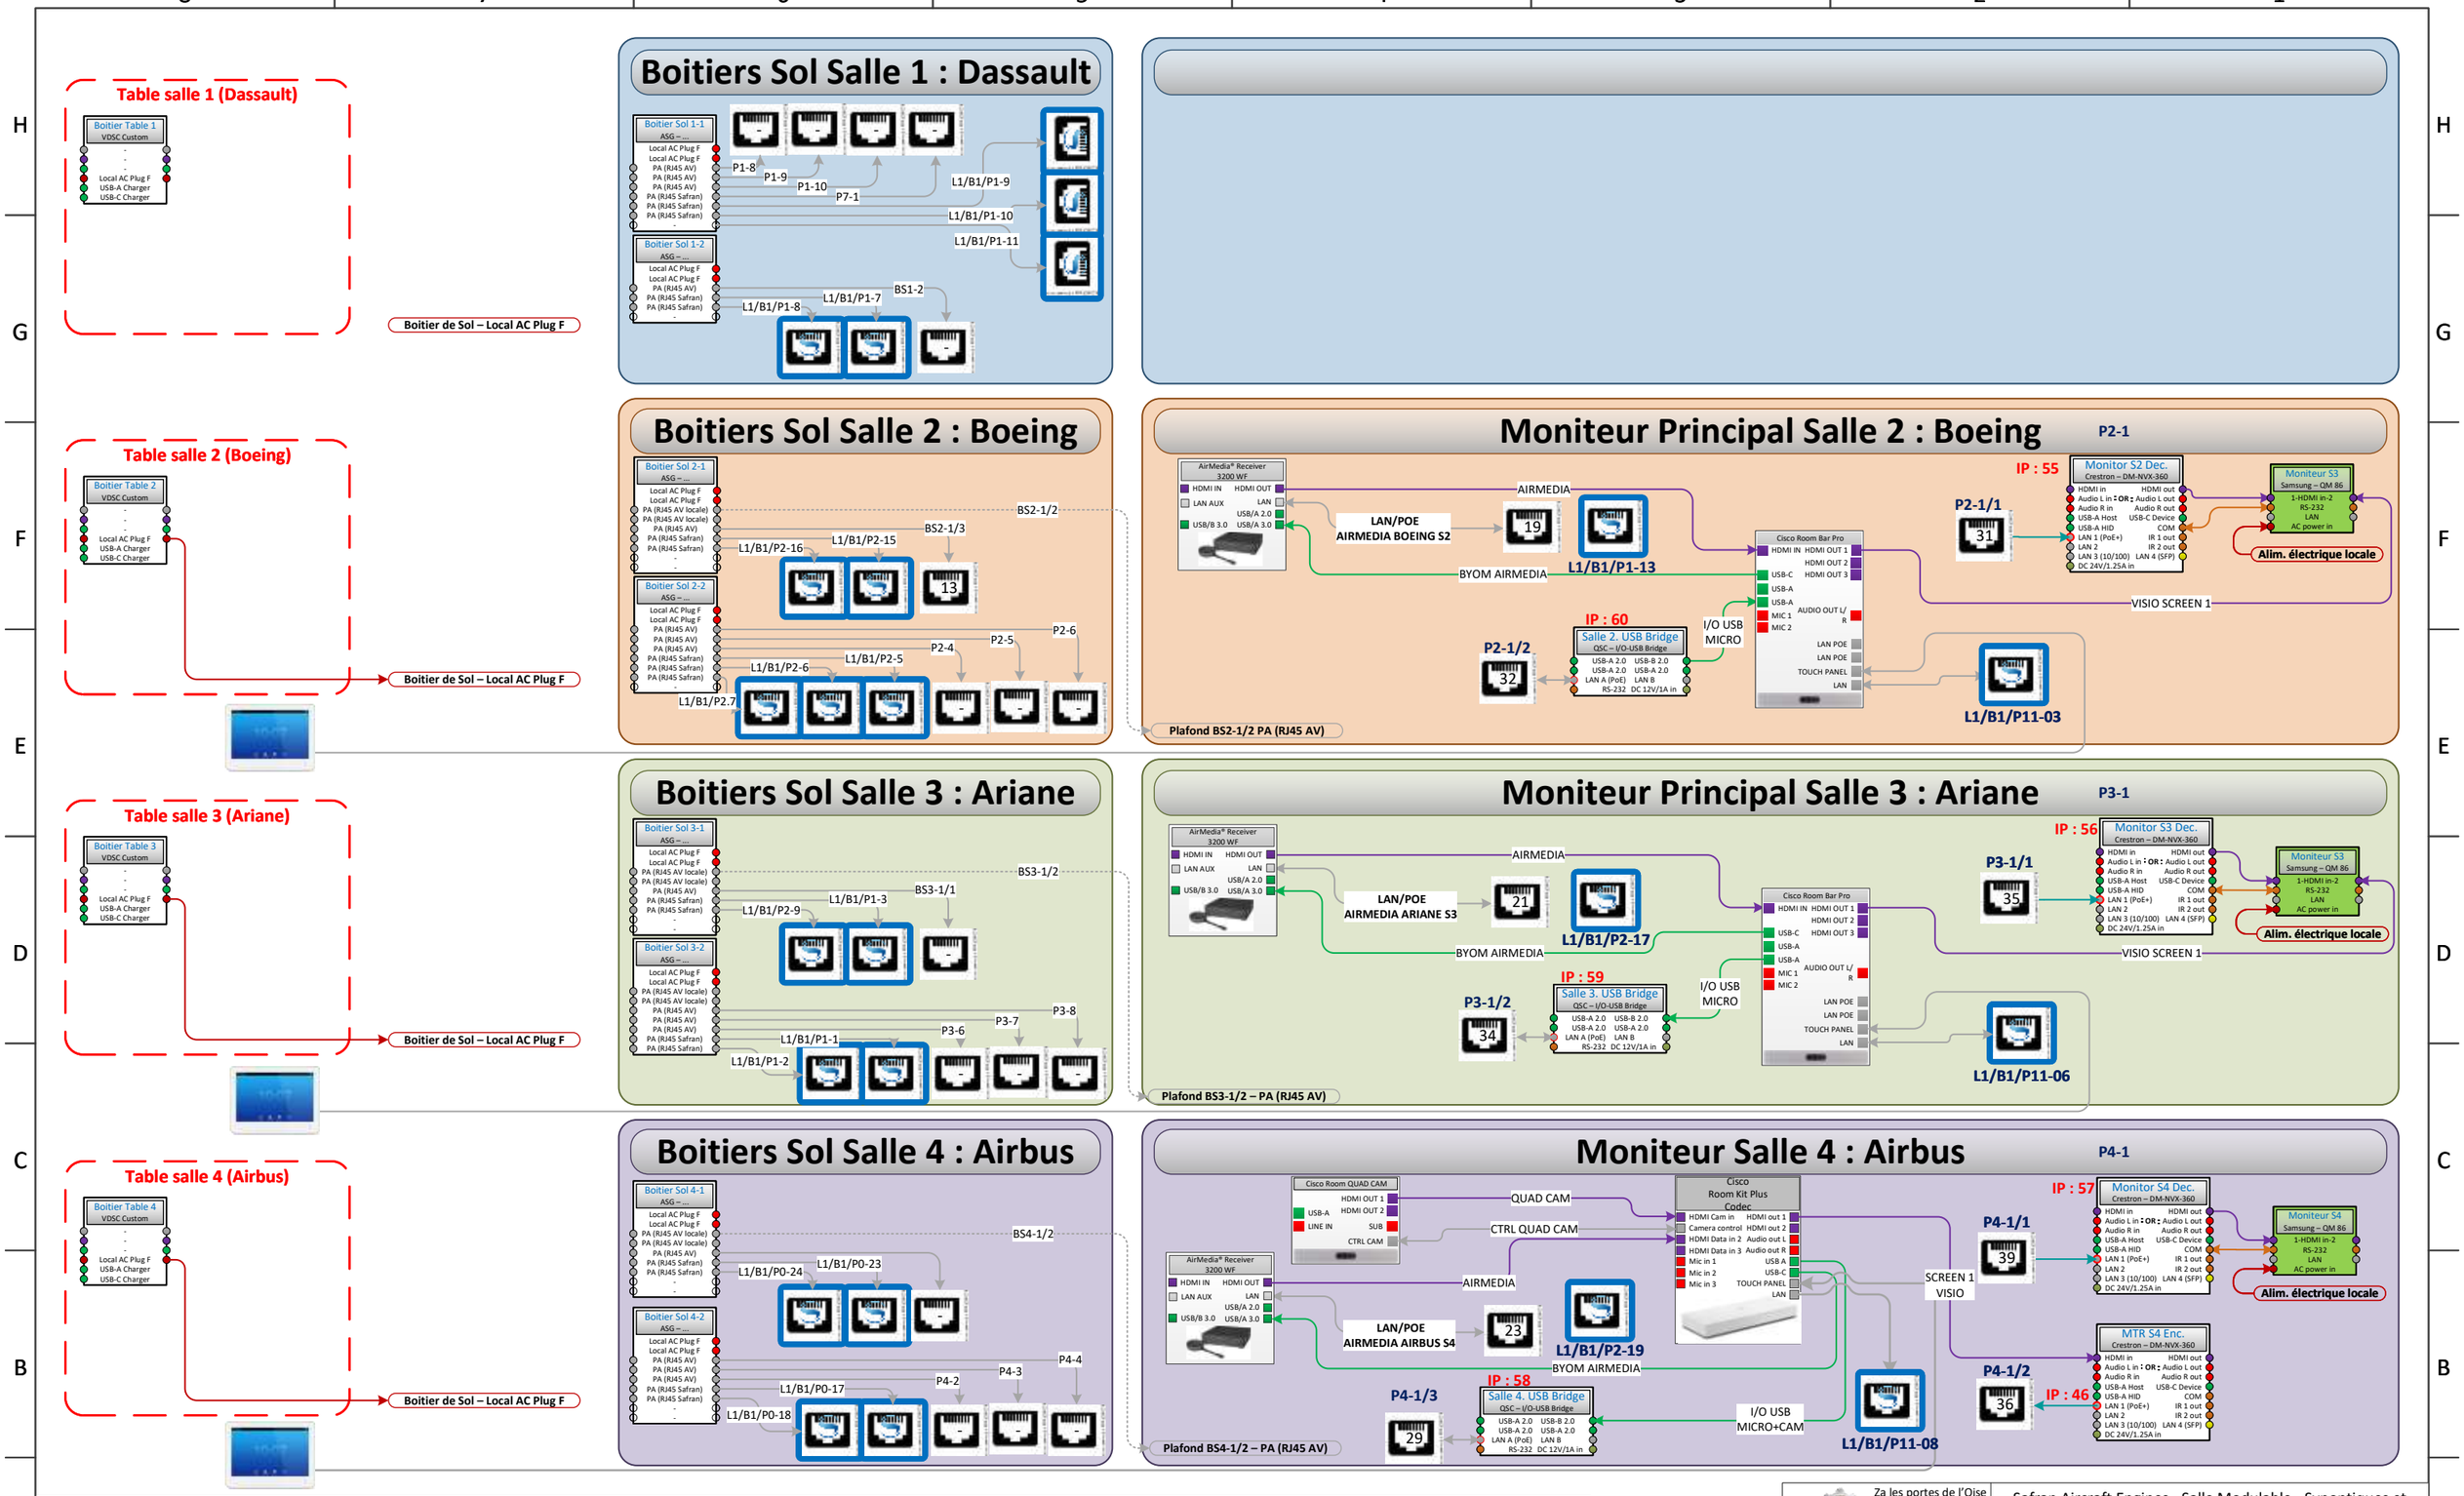

Légende

Code couleur du câblage

- HDMI
- Display Port
- (HD) SDI
- DVI
- VGA
- Vidéo autres
- Audio Analogique
- Audio Numérique
- Haut Parleur
- RJ45 Cat.6 Audio
- RJ45 Cat.6 Vidéo
- RJ45 Cat.6 Réseau
- Fibre Optique
- USB
- RS-232
- Electricité C Fort
- Electricité C Faible
- Contrôle autres

Adressage IP

Base des adresses IP : 192.168.0.xxx

IP : xxx :
Dernier nombre IPv4 de la machine

Matériel

Nom de la machine
Fabriquant - Modèle
Connector Connector

Matériel fourni

Matériel non fourni par Videosonic

Numérotation de câblage

A	Audio	N	Réseau (Network)
AN	Réseau audio (Audio Network)	P	Puissance
C	Contrôle	S	Haut-Parleurs (Speakers)
T	Conférence (Taiden)	V	Video
I	Informatique	VN	Réseau Vidéo (Video Network)

VIDEOSONIC
Image, Son & Technique
Za les portes de l'Oise
Batiment B2
rue Henri Becquerel
60230 CHAMBLY
Tel : 01 75 01 60 40
Fax : 01 75 01 60 41
t.fourmentraux@videosonic.fr
Thierry FOURMENTRAUX

29 FÉVRIER 2024

Safran Aircraft Engines - Salle Modulable - Synoptiques et plans d'execution VERSION CISCO.vsdm

SAFRAN AIRCRAFT ENGINES
SNECMA 1 RUE HENRI DESBRUÈRES ÉVRY-COURCOURONNES

DIMENSION	N° CODE	PAGE	RÉV
A3		Synoptique 2/2	19/02/2026
ECHELLE 1:1		FEUILLE 3 / 9	

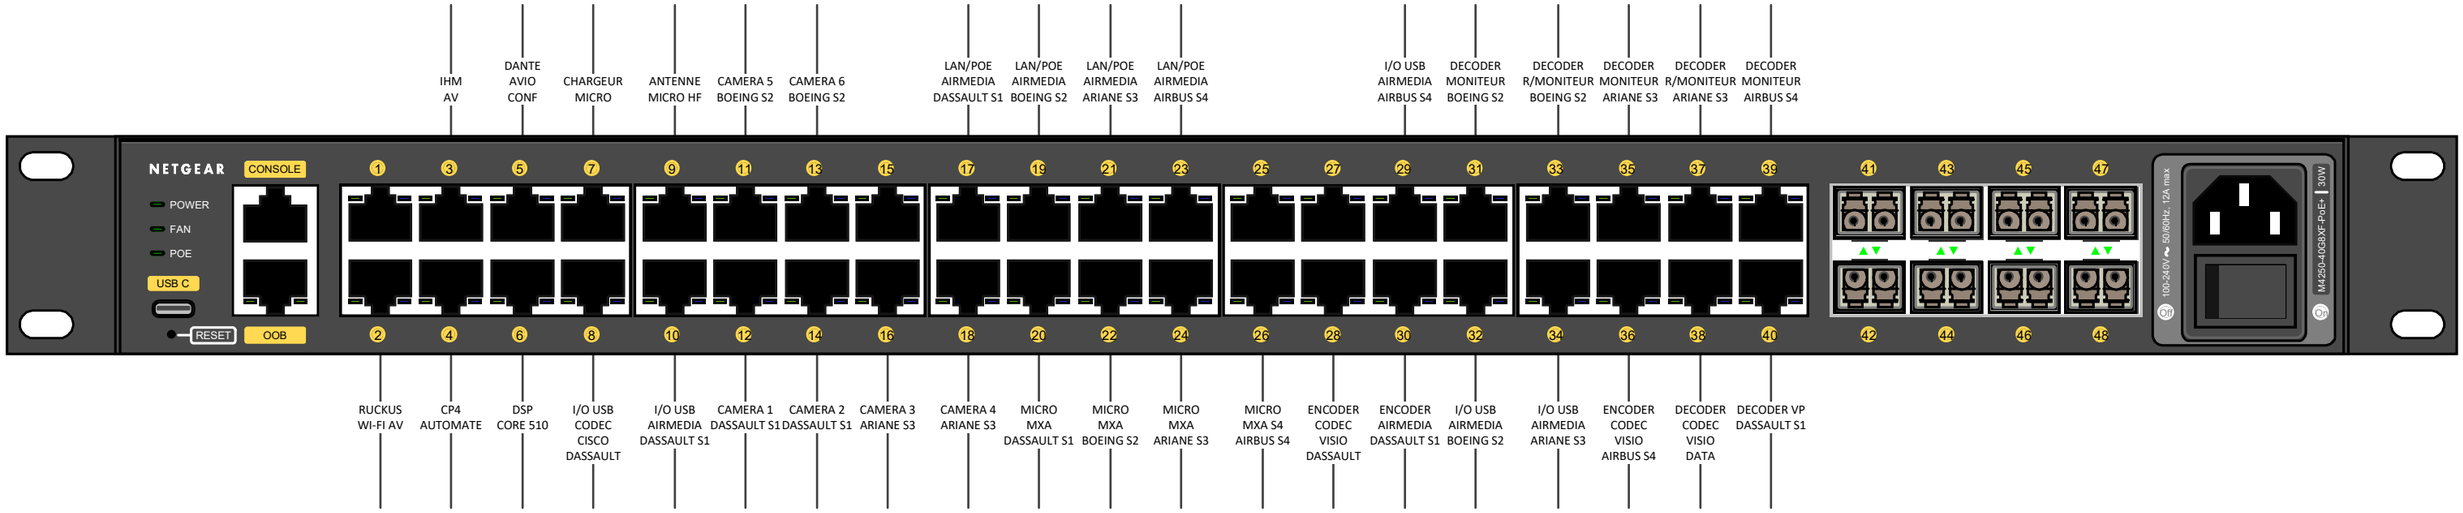

Équipement	Quanti	Norme PoE	Puissance unitaire (V	Puissance totale (V
DM-NVX-360	10	PoE+ 802.3at Type 2	25,5	255
QSC-I/O USB-BRIDGE	5	PoE Type 1, Classe 3	12,95	64,75
QSC-NC-12x80	6	PoE Type 1, Classe 3	12,95	77,7
SHURE MXA920W	4	IEEE 802.3at Type 1	10,1	40,4
SHURE MXWAPT4	1	IEEE 802.3at Type 0	6,5	6,5
CRESTRON TSW-1070-B-S	1	IEEE 802.3at Type 2	15	15
DANTE AVIO	1	IEEE 802.3at Type 0	4	4
RUCHUS R350	1		12,62	12,62
AIRMEDIA AM-3200-WF	4	IEEE 802.3af Class 4	14	56
CP4 AUTOMATE	1			0
CORE510 DSP	1			0
CHARGEUR MICRO HF SHURE	1			0
total port switch/amphi	36			0
Budget PoE brut (W)	531,97			
Budget PoE recommandé (+30%) (W)	691,561			
BUDGET SWITCH 960W (30W/PORT)				

VIDEOSONIC
Image, Son & Technique
Za les portes de l'Oise
Batîment B2
rue Henri Becquerel
60230 CHAMBLY
Tel : 01 75 01 60 40
Fax : 01 75 01 60 41
t.fourmentraux@videosonic.fr

Safran Aircraft Engines - Salle Modulable - Synoptiques et plans d'execution VERSION CISCO.vsdm

SAFRAN AIRCRAFT ENGINES
SNECMA 1 RUE HENRI DESBRUÈRES ÉVRY-COURCOURONNES

Thierry FOURMENTRAUX	DIMENSION A3	N° CODE	PAGE SWITCH AV	RÉV 19/02/2026
13 FÉVRIER 2026	ECHELLE 1:1		FEUILLE 4 / 9	

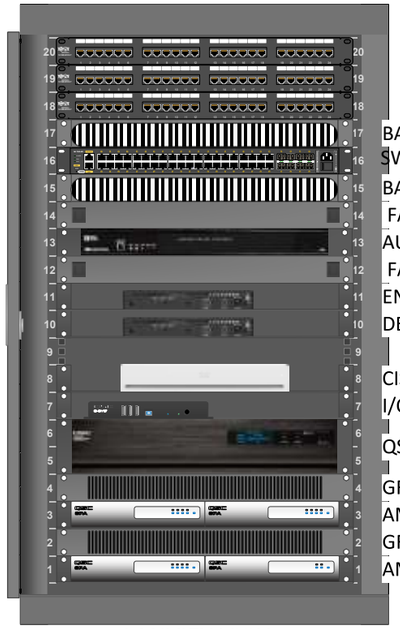

	PATCH 1 RJ45
	PATCH 2 RJ45
	PATCH 3 RJ45
1 U	BALAIS PASSE CABLE
	SWITCH AV M4250-40G8XF-PoE+
1 U	BALAIS PASSE CABLE
1 U	FACE CLIPS
1 U	AUTOMATE CRESTRON CP4
1 U	FACE CLIPS
1 U	ENCODER MTR
1 U	DECODER MTR
1 U	CISCO CODEC EQ
1 U	I/O USB MTR
2 U	QSC Q-SYS CORE 510i
1 U	GRILLE
1 U	AMPLI S1 + S2
1 U	GRILLE
1 U	AMPLI S3 + S4

LANVIEW 20U

RWP20U45BL + RWMD20UBL

- Total équipements électronique : **31.3 Kg**
- Dissipation thermique maximum totale de la baie :
- **5469.56** BTU/h
- Puissance consommée maximum de la baie :
- **1619** W

VIDEOSONIC
Image, Son & Technique
Za les portes de l'Oise
Batîment B2
rue Henri Becquerel
60230 CHAMBLY
Tel : 01 75 01 60 40
Fax : 01 75 01 60 41
t.fourmentraux@videosonic.fr

Safran Aircraft Engines - Salle Modulable - Synoptiques et plans d'execution VERSION CISCO.vsdm

SAFRAN AIRCRAFT ENGINES

SNECMA 1 RUE HENRI DESBRUÈRES ÉVRY-COURCOURONNES

Thierry FOURMENTRAUX	DIMENSION	N° CODE	PAGE	RÉV
	A3		Plan de baie	19/02/2026
29 FÉVRIER 2024	ECHELLE 1:10		FEUILLE	5 / 9

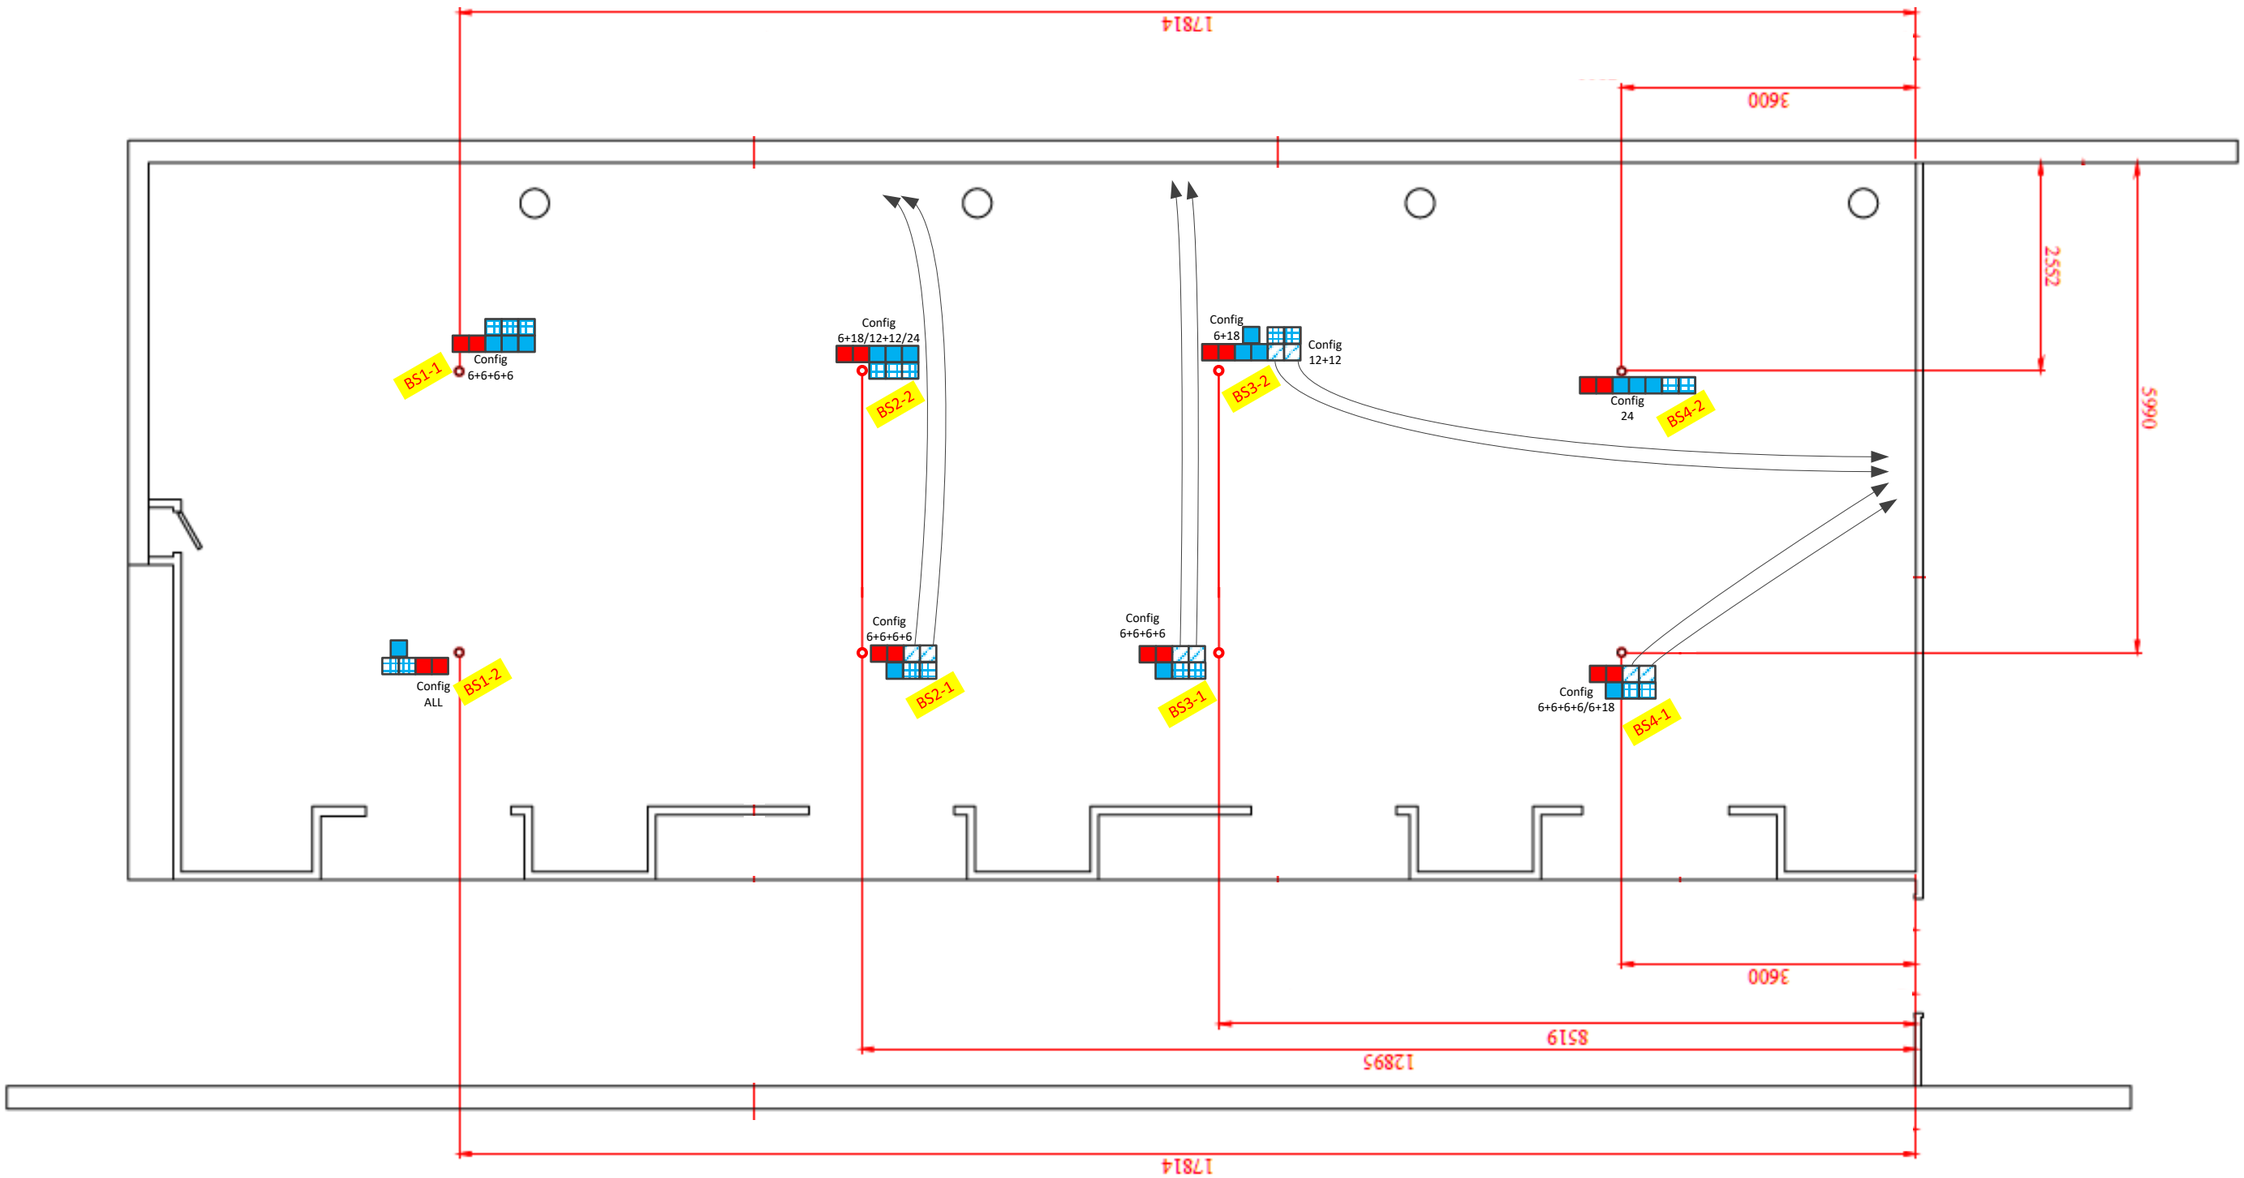

LEGENDE

Couleurs : Type

- Prise de courant 16A 2P+T
- Prise RJ45 - Cat.6A
- Haut parleur
- Ecran de projection (4G1.5)

Formes : emplacement

- Dans le plafond
- Au mur
- Au sol

Remplissage : Tenant

- Baie audiovisuelle (Couleur pleine)
- Local (vdsc) (Couleur hachurée)
- Baie Safran (Couleur quadrillée)

VIDEOSONIC
Image, Son & Technique
Za les portes de l'Oise
Batîment B2
rue Henri Becquerel
60230 CHAMBLY
Tel : 01 75 01 60 40
Fax : 01 75 01 60 41
t.fourmentraux@videosonic.fr

Safran Aircraft Engines - Salle Modulable - Synoptiques et plans d'execution VERSION CISCO.vsdm

SAFRAN AIRCRAFT ENGINES

SNECMA 1 RUE HENRI DESBRUÈRES ÉVRY-COURCOURONNES

Thierry FOURMENTRAUX

29 FÉVRIER 2024

DIMENSION	N° CODE	PAGE	RÉV
A3		Plan câbles - Boitiers de sol	19/02/2026
ECHELLE 1:75		FEUILLE 6 / 9	

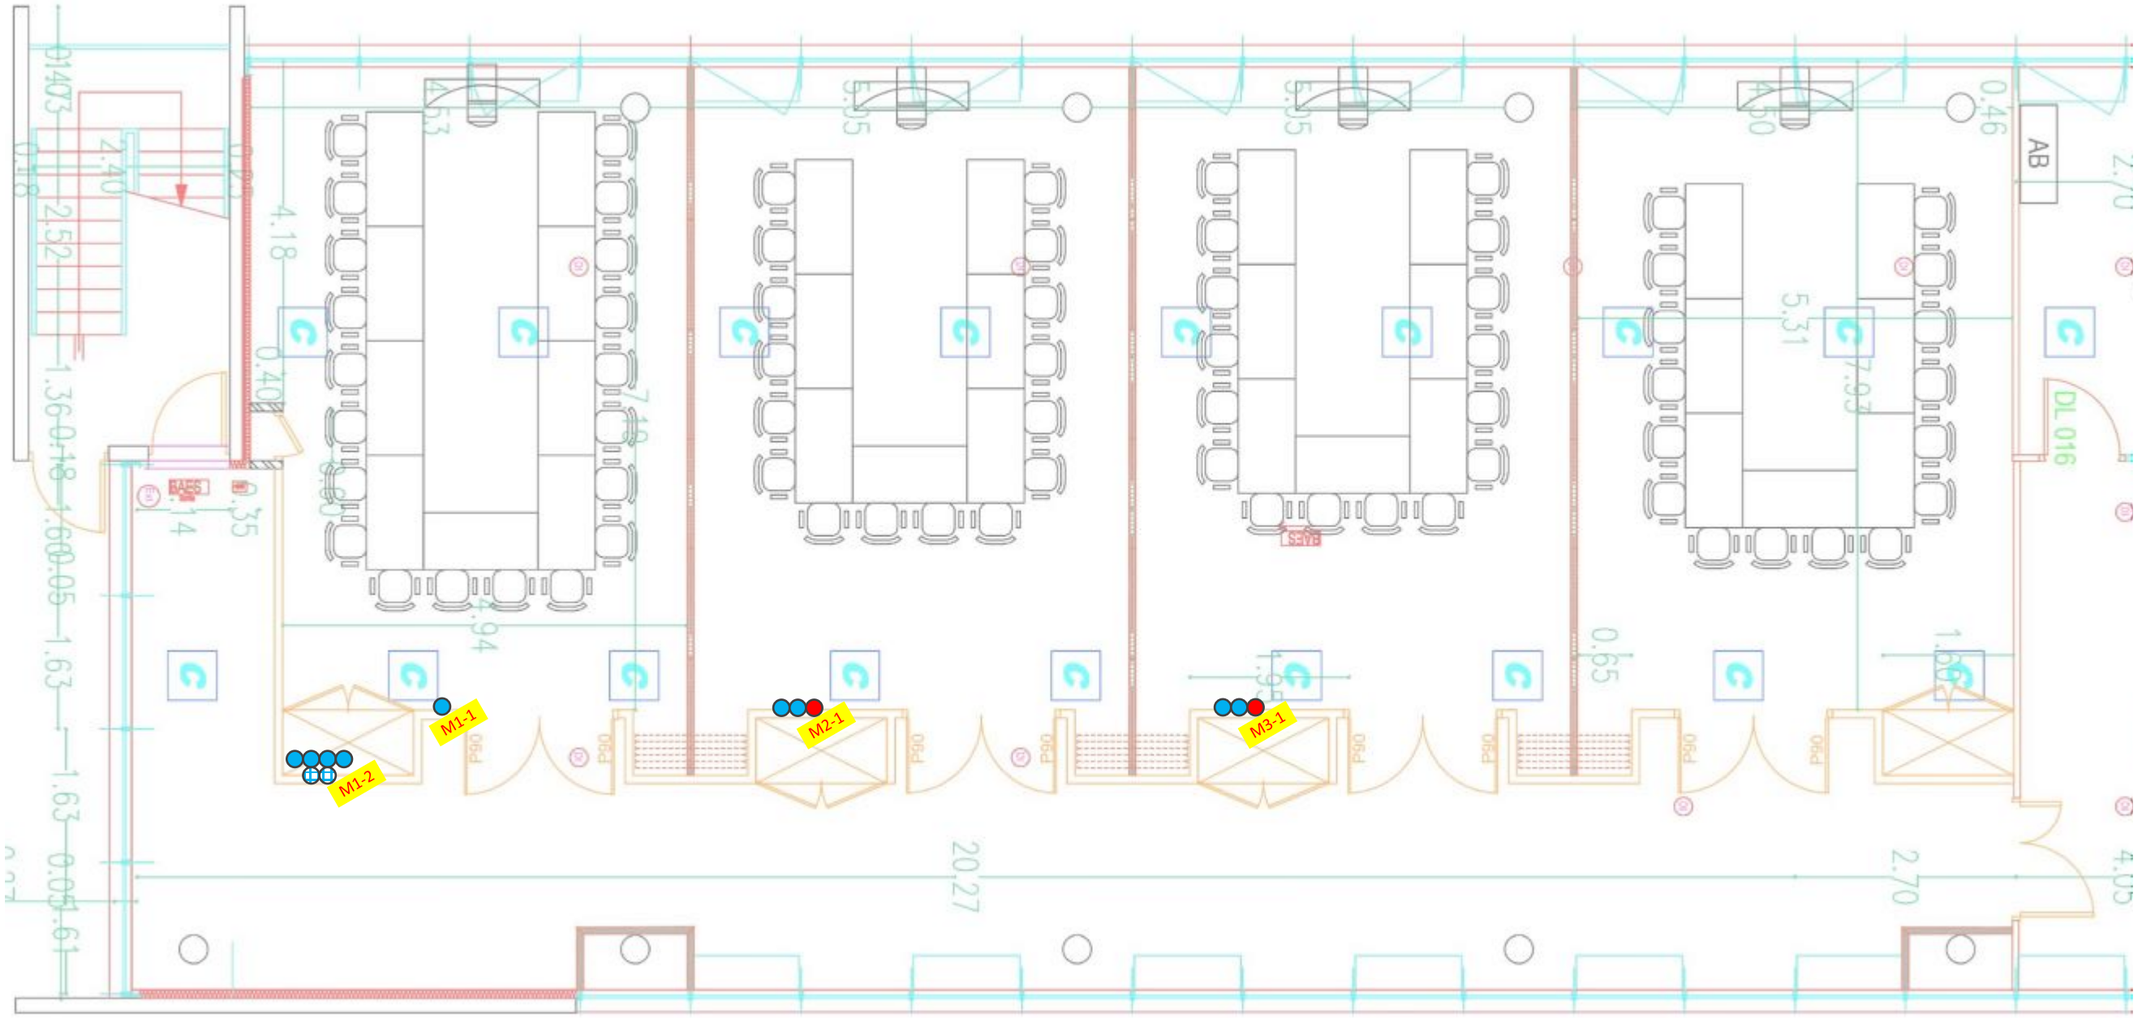

LEGENDE

Couleurs : Type

- Prise de courant 16A 2P+T
- Prise RJ45 - Cat.6A
- Haut parleur
- Ecran de projection (4G1.5)

Formes : emplacement

- Dans le plafond
- Au mur
- Au sol

Remplissage : Tenant

- Baie audiovisuelle (Couleur pleine)
- Local (vdsc) (Couleur hachurée)
- Baie Safran (Couleur quadrillée)

VIDEOSONIC
Image, Son & Technique
Za les portes de l'Oise
Batîment B2
rue Henri Becquerel
60230 CHAMBLY
Tel : 01 75 01 60 40
Fax : 01 75 01 60 41
t.fourmentraux@videosonic.fr

Safran Aircraft Engines - Salle Modulable - Synoptiques et plans d'execution VERSION CISCO.vsdm

SAFRAN AIRCRAFT ENGINES
SNECMA 1 RUE HENRI DESBRUÈRES ÉVRY-COURCOURONNES

Thierry FOURMENTRAUX

29 FÉVRIER 2024

DIMENSION	N° CODE	PAGE	RÉV
A3		Plan câbles - Mural	19/02/2026
ECHELLE 1:75		FEUILLE 7 / 9	

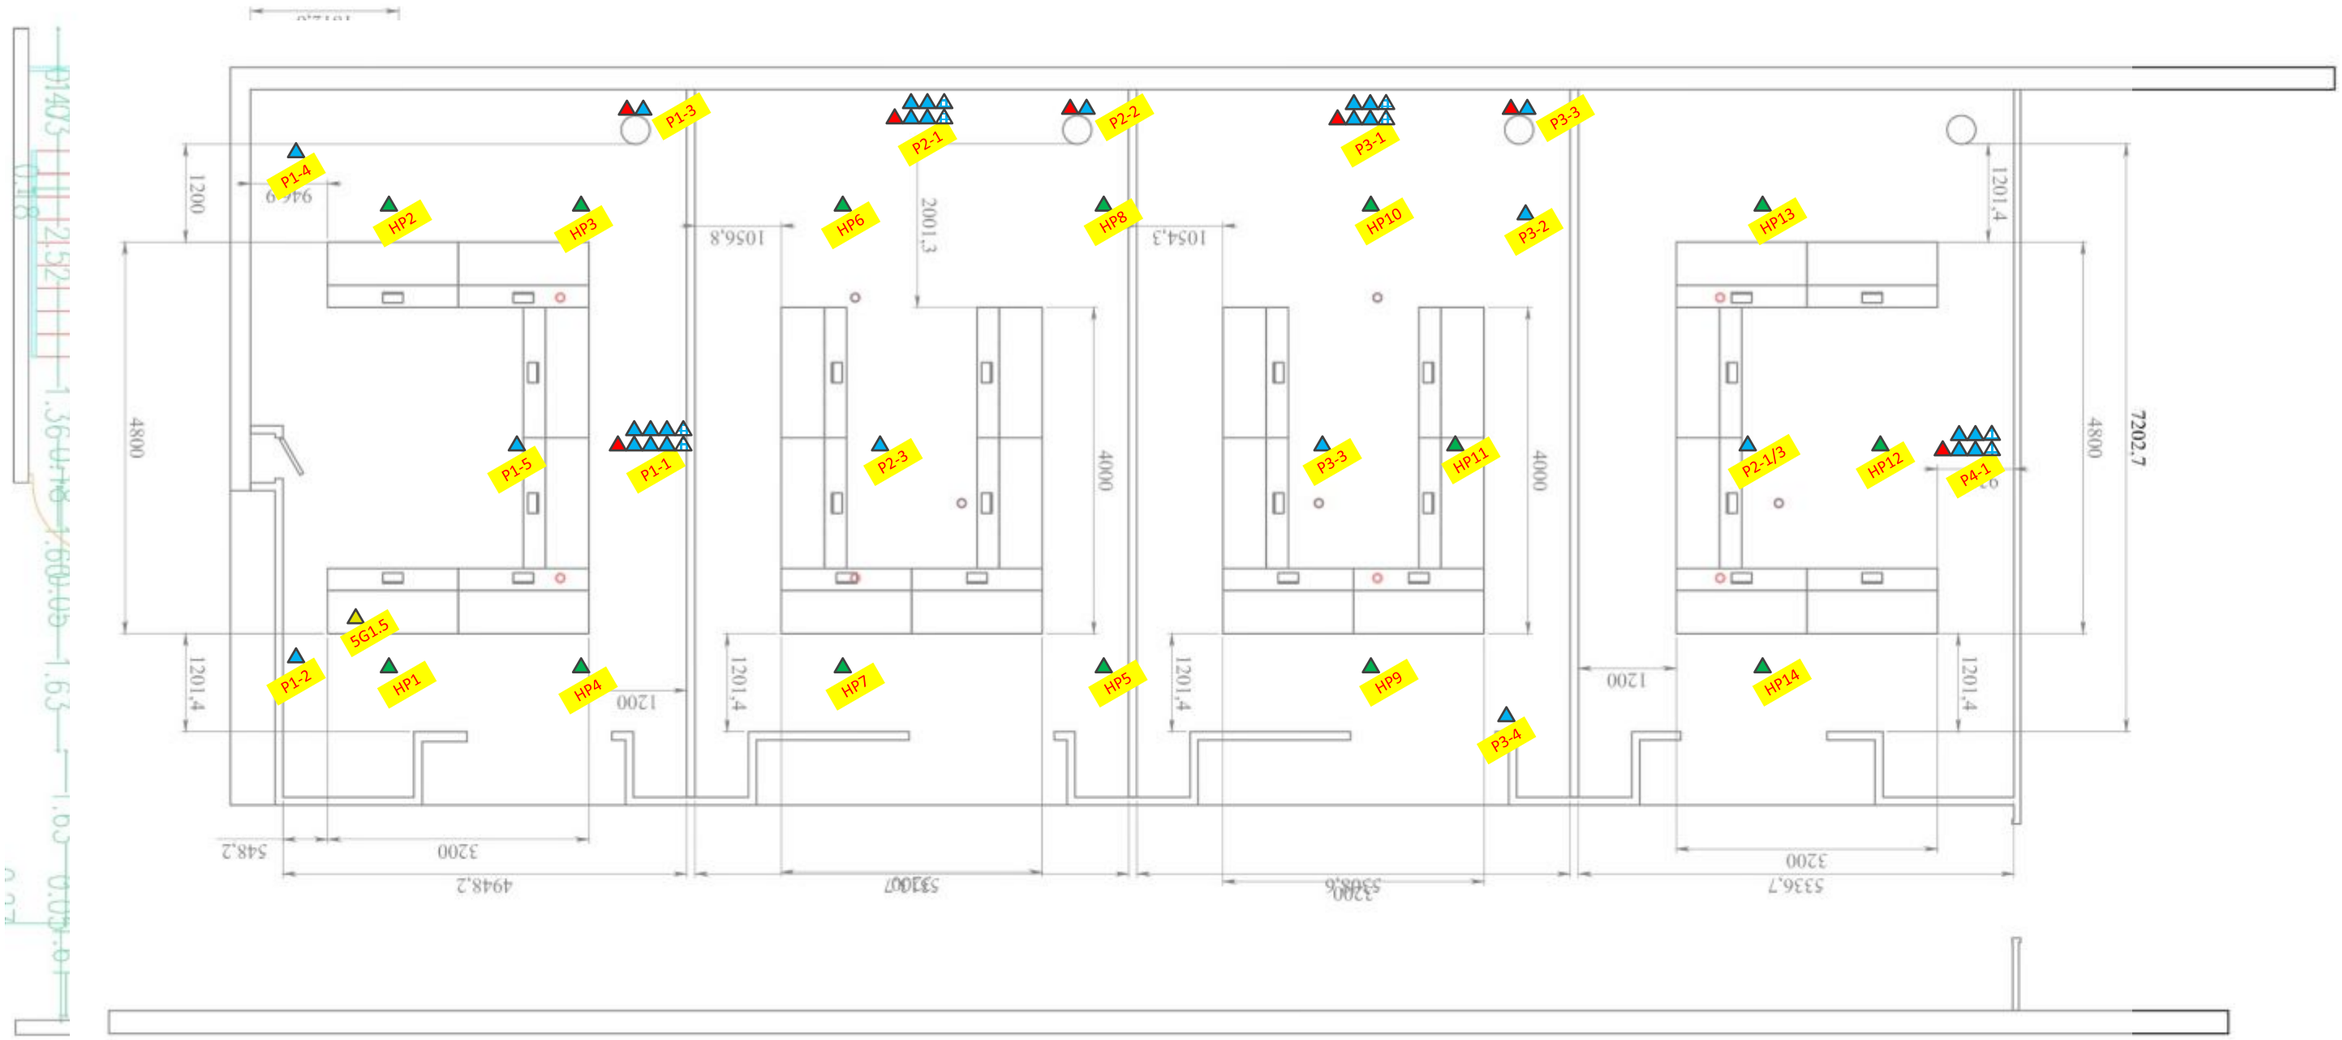

LEGENDE

Couleurs : Type

- Prise de courant 16A 2P+T
- Prise RJ45 - Cat.6A
- Haut parleur
- Ecran de projection (4G1.5)

Formes : emplacement

- Dans le plafond
- Au mur
- Au sol

Remplissage : Tenant

- Baie audiovisuelle (Couleur pleine)
- Local (vdsc) (Couleur hachurée)
- Baie Safran (Couleur quadrillée)

VIDEOSONIC
Image, Son & Technique
Za les portes de l'Oise
Batîment B2
rue Henri Becquerel
60230 CHAMBLY
Tel : 01 75 01 60 40
Fax : 01 75 01 60 41
t.fourmentraux@videosonic.fr

Safran Aircraft Engines - Salle Modulable - Synoptiques et plans d'execution VERSION CISCO.vsdm

SAFRAN AIRCRAFT ENGINES
SNECMA 1 RUE HENRI DESBRUÈRES ÉVRY-COURCOURONNES

Thierry FOURMENTRAUX

29 FÉVRIER 2024

DIMENSION	N° CODE	PAGE	RÉV
A3		Plan câbles - Plafond	19/02/2026
ECHELLE 1:75		FEUILLE 8 / 9	

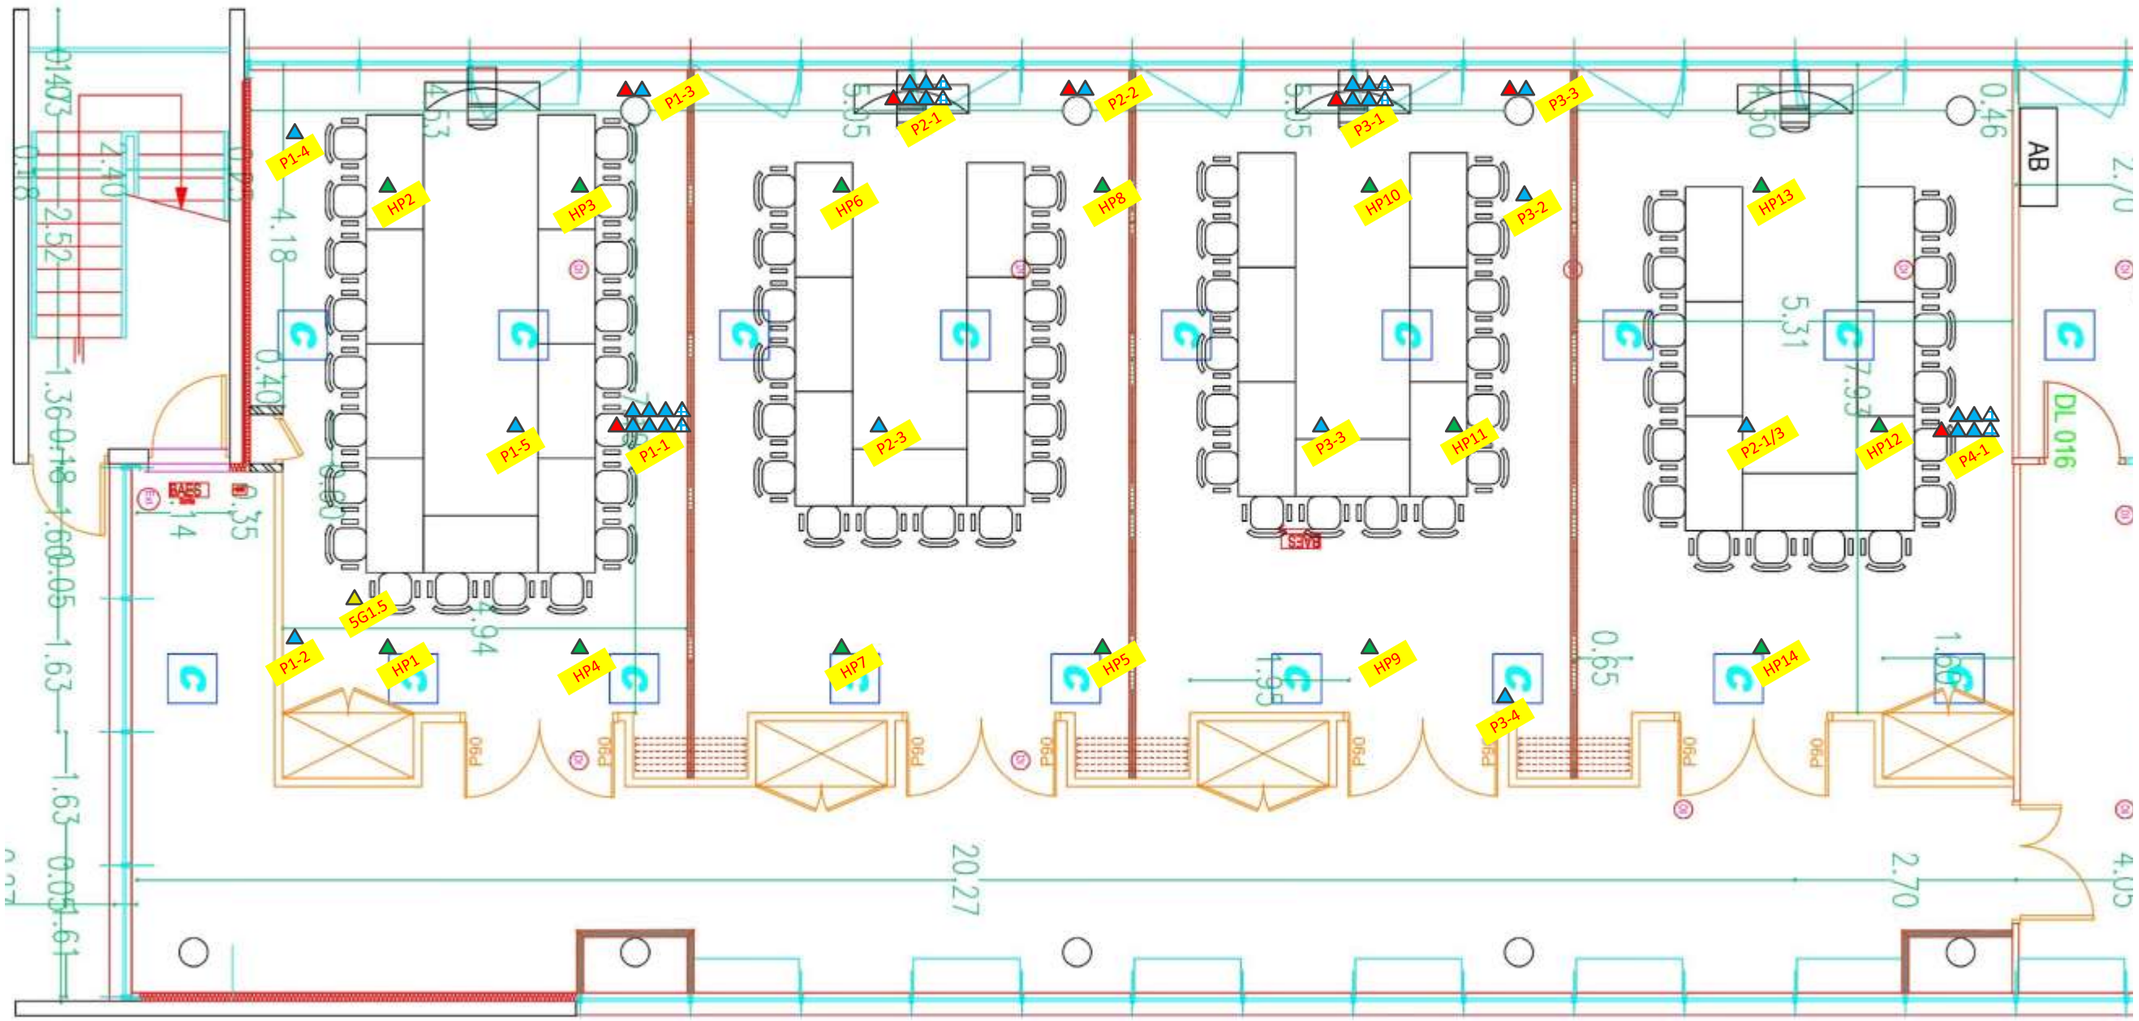

LEGENDE

Couleurs : Type

- Prise de courant 16A 2P+T
- Prise RJ45 - Cat.6A
- Haut parleur
- Ecran de projection (4G1.5)

Formes : emplacement

- Dans le plafond
- Au mur
- Au sol

Remplissage : Tenant

- Vers Baie AV (Couleur hachurée)

VIDEOSONIC
Image, Son & Technique
Za les portes de l'Oise
Batîment B2
rue Henri Becquerel
60230 CHAMBLY
Tel : 01 75 01 60 40
Fax : 01 75 01 60 41
t.fourmentraux@videosonic.fr

Safran Aircraft Engines - Salle Modulable - Synoptiques et plans d'execution VERSION CISCO.vsdm

SAFRAN AIRCRAFT ENGINES
SNECMA 1 RUE HENRI DESBRUÈRES ÉVRY-COURCOURONNES

Thierry FOURMENTRAUX

29 FÉVRIER 2024

DIMENSION	N° CODE	PAGE	RÉV
A3		Plan salle	19/02/2026
ECHELLE 1:75		FEUILLE 9 / 9	