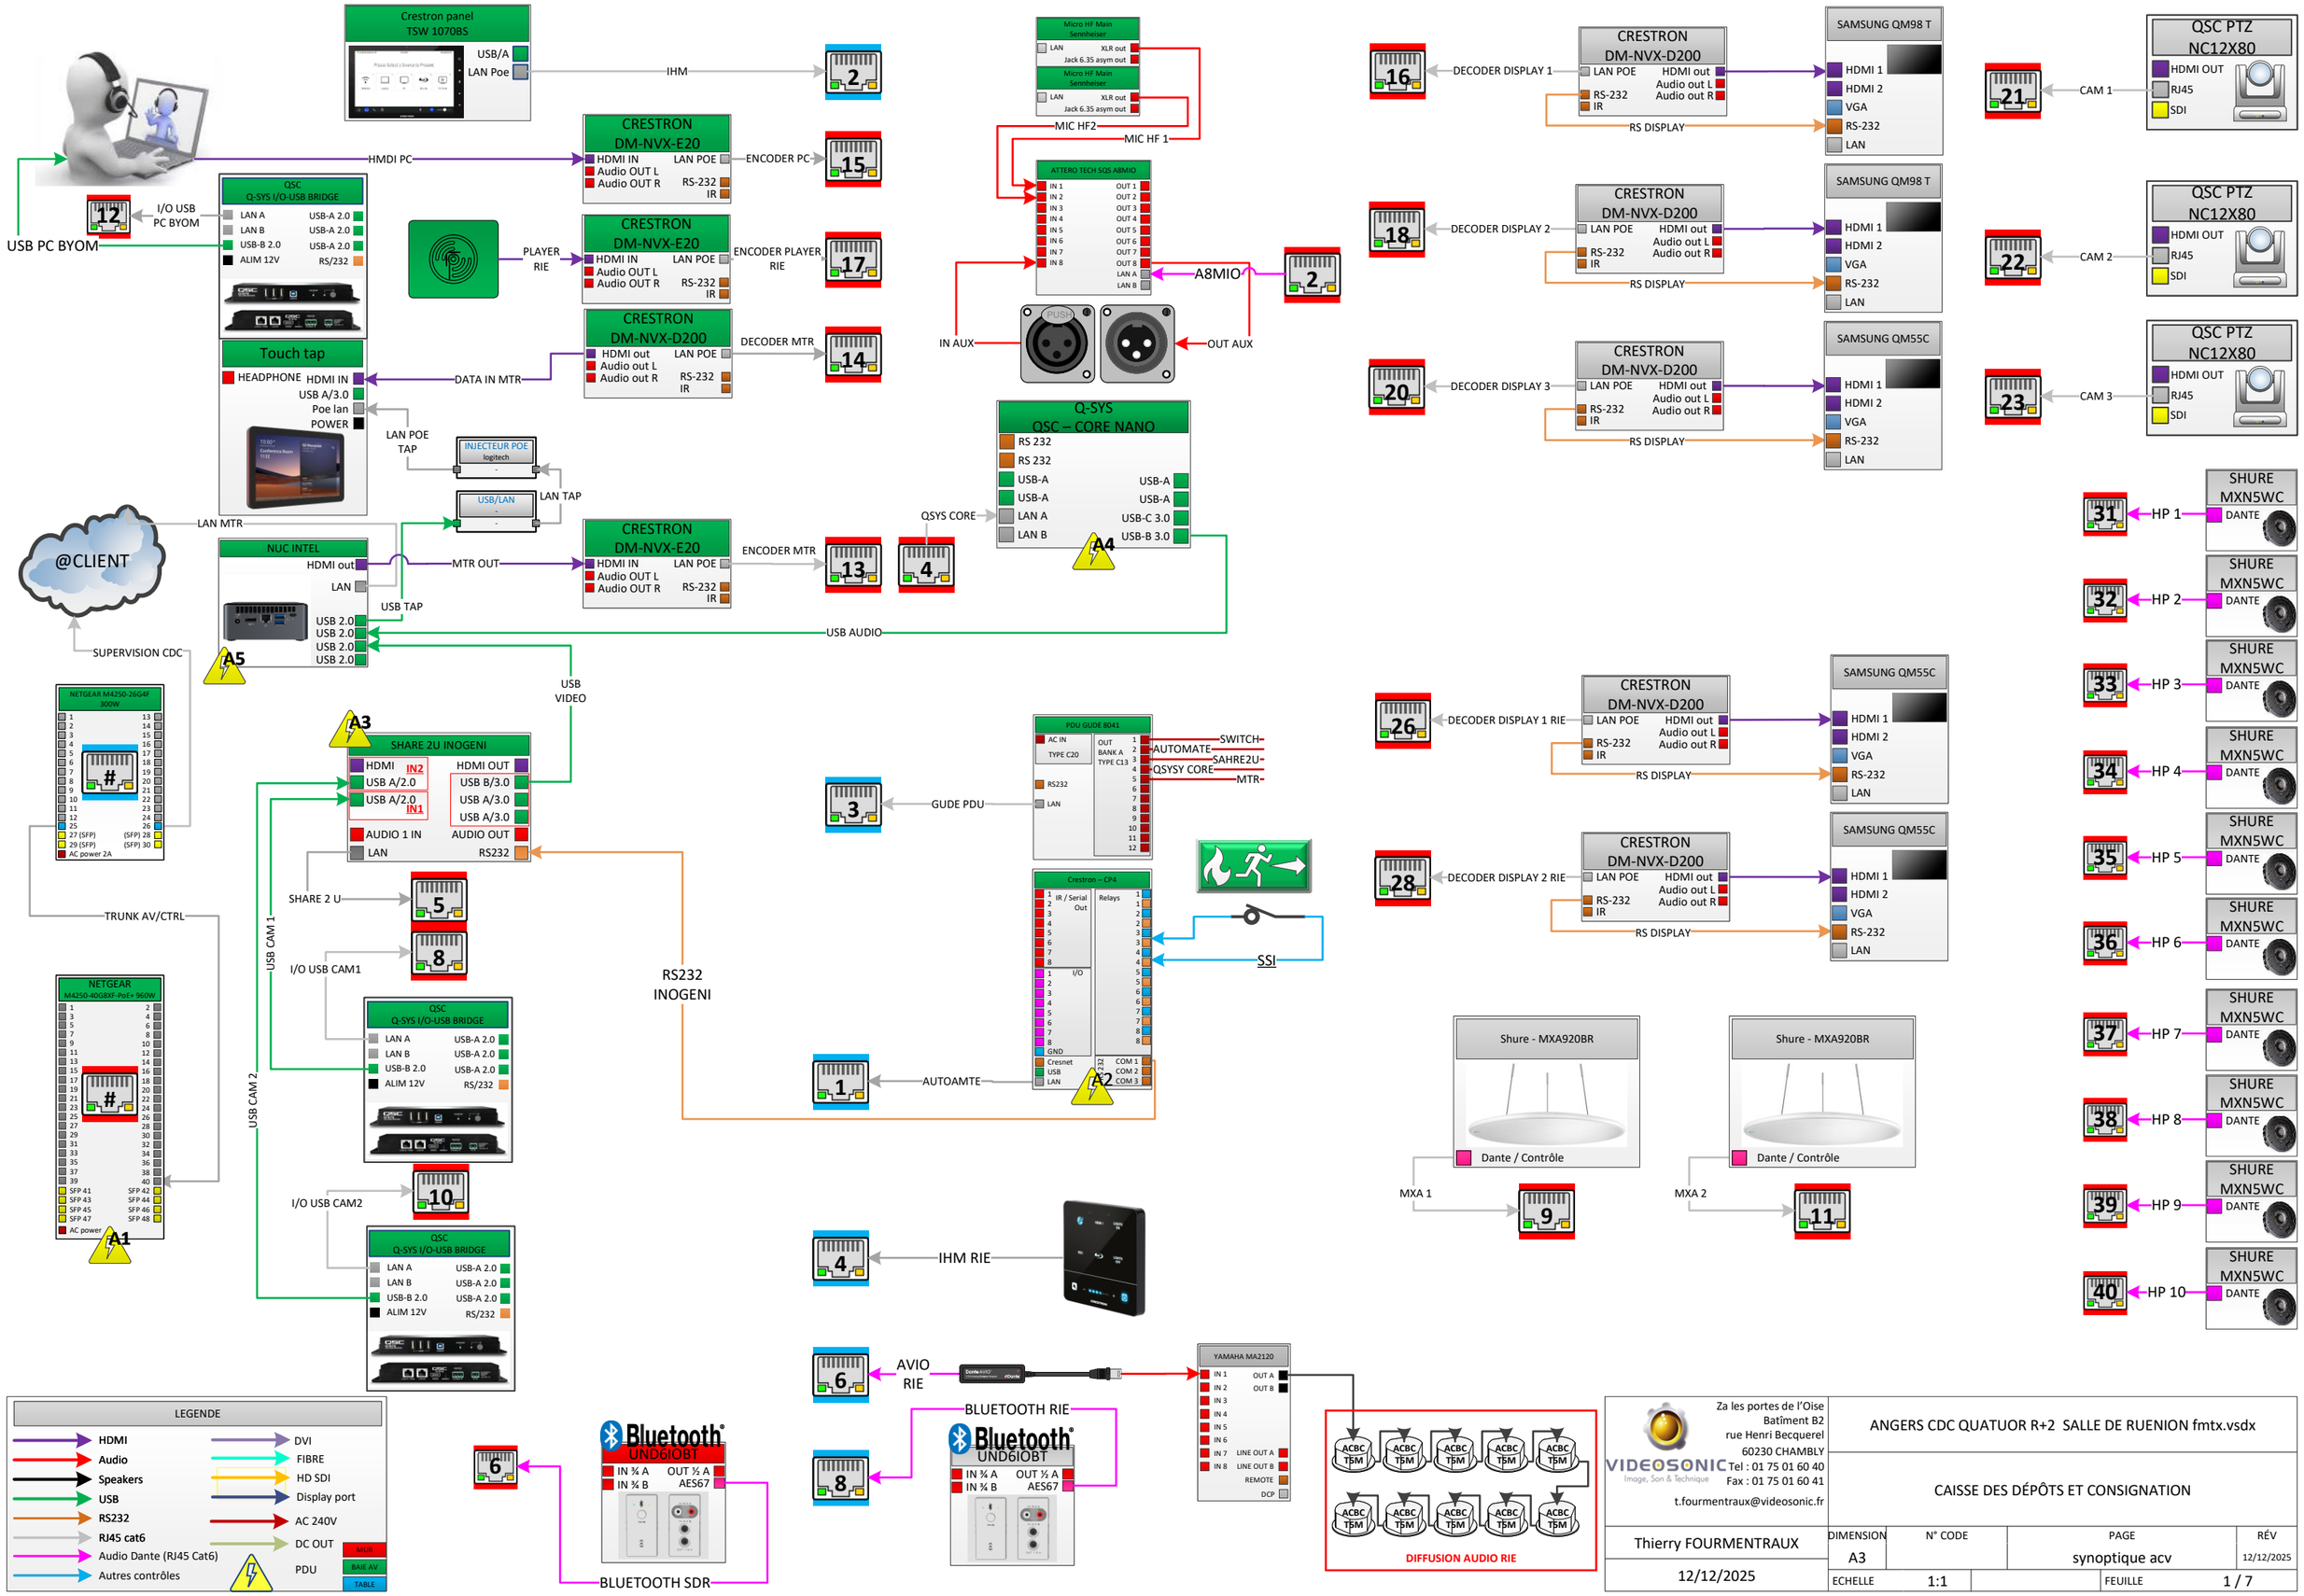
Crestron panel
TSW 1070BS
USB/A
LAN Poe
IHM
2
HMDI PC
CRESTRON
DM-NVX-E20
HDMI IN
Audio OUT L
Audio OUT R
LAN POE
RS-232
IR
ENCODER PC
15
USB PC BYOM
12
I/O USB
PC BYOM
QSC
Q-SYS I/O-USB BRIDGE
LAN A
LAN B
USB-B 2.0
ALIM 12V
USB-A 2.0
RS/232
PLAYER
RIE
CRESTRON
DM-NVX-E20
ENCODER PLAYER
RIE
17
CRESTRON
DM-NVX-D200
HDMI out
Audio out L
Audio out R
DECODER MTR
14
Touch tap
HEADPHONE
HDMI IN
USB A/3.0
Poe lan
POWER
DATA IN MTR
LAN POE
TAP
INJECTEUR POE
logitech
USB/LAN
LAN TAP
LAN MTR
@CLIENT
NUC INTEL
HDMI out
LAN
USB TAP
USB 2.0
A5
MTR OUT
CRESTRON
DM-NVX-E20
ENCODER MTR
13
4
QSYS CORE
Q-SYS
QSC – CORE NANO
RS 232
USB-A
LAN A
LAN B
USB-C 3.0
USB-B 3.0
A4
USB AUDIO
SUPERVISION CDC
NETGEAR M4250-26G4F 300W
AC power 2A
A3
SHARE 2U INOGENI
HDMI
USB A/2.0
IN2
IN1
AUDIO 1 IN
LAN
HDMI OUT
USB B/3.0
USB A/3.0
AUDIO OUT
RS232
USB
VIDEO
SHARE 2 U
5
8
I/O USB CAM1
TRUNK AV/CTRL
USB CAM 1
USB CAM 2
RS232
INOGENI
NETGEAR M4250-40G8XF-PoE+ 960W
AC power
A1
QSC
Q-SYS I/O-USB BRIDGE
10
I/O USB CAM2
3
GUDE PDU
PDU GUDE 8041
AC IN
TYPE C20
RS232
LAN
OUT
BANK A
TYPE C13
AUTOMATE
SWITCH
SAHRE2U
QSYSY CORE
MTR
Crestron – CP4
IR / Serial
Relays
I/O
Cresnet
USB
LAN
COM 1
COM 2
COM 3
A2
1
AUTOAMTE
SSI
Micro HF Main
Sennheiser
LAN
XLR out
Jack 6.35 asym out
MIC HF2
MIC HF 1
ATTERO TECH SQS A8MIO
IN 1
IN 2
IN 3
IN 4
IN 5
IN 6
IN 7
IN 8
OUT 1
OUT 2
OUT 3
OUT 4
OUT 5
OUT 6
OUT 7
OUT 8
LAN A
LAN B
A8MIO
IN AUX
OUT AUX
PUSH
4
IHM RIE
6
AVIO
RIE
BLUETOOTH RIE
8
Bluetooth
UND6IOBT
IN ¾ A
IN ¾ B
OUT ½ A
AES67
6
BLUETOOTH SDR
YAMAHA MA2120
IN 1
IN 2
IN 3
IN 4
IN 5
IN 6
IN 7
IN 8
OUT A
OUT B
LINE OUT A
LINE OUT B
REMOTE
DCP
ACBC TSM
DIFFUSION AUDIO RIE
16
DECODER DISPLAY 1
CRESTRON
DM-NVX-D200
LAN POE
HDMI out
Audio out L
Audio out R
RS-232
IR
RS DISPLAY
SAMSUNG QM98 T
HDMI 1
HDMI 2
VGA
RS-232
LAN
21
CAM 1
QSC PTZ
NC12X80
HDMI OUT
RJ45
SDI
18
DECODER DISPLAY 2
22
CAM 2
20
DECODER DISPLAY 3
SAMSUNG QM55C
23
CAM 3
26
DECODER DISPLAY 1 RIE
28
DECODER DISPLAY 2 RIE
Shure - MXA920BR
Dante / Contrôle
MXA 1
9
MXA 2
11
SHURE
MXN5WC
DANTE
31
HP 1
32
HP 2
33
HP 3
34
HP 4
35
HP 5
36
HP 6
37
HP 7
38
HP 8
39
HP 9
40
HP 10
LEGENDE
HDMI
Audio
Speakers
USB
RS232
RJ45 cat6
Audio Dante (RJ45 Cat6)
Autres contrôles
DVI
FIBRE
HD SDI
Display port
AC 240V
DC OUT
PDU
MUR
BAIE AV
TABLE
Za les portes de l'Oise
Batiment B2
rue Henri Becquerel
60230 CHAMBLY
Tel : 01 75 01 60 40
Fax : 01 75 01 60 41
t.fourmentraux@videosonic.fr
VIDEOSONIC
Image, Son & Technique
ANGERS CDC QUATUOR R+2 SALLE DE RUENION fmtx.vsdx
CAISSE DES DÉPÔTS ET CONSIGNATION
Thierry FOURMENTRAUX
12/12/2025
DIMENSION
A3
N° CODE
PAGE
synoptique acv
RÉV
12/12/2025
ECHELLE
1:1
FEUILLE
1 / 7

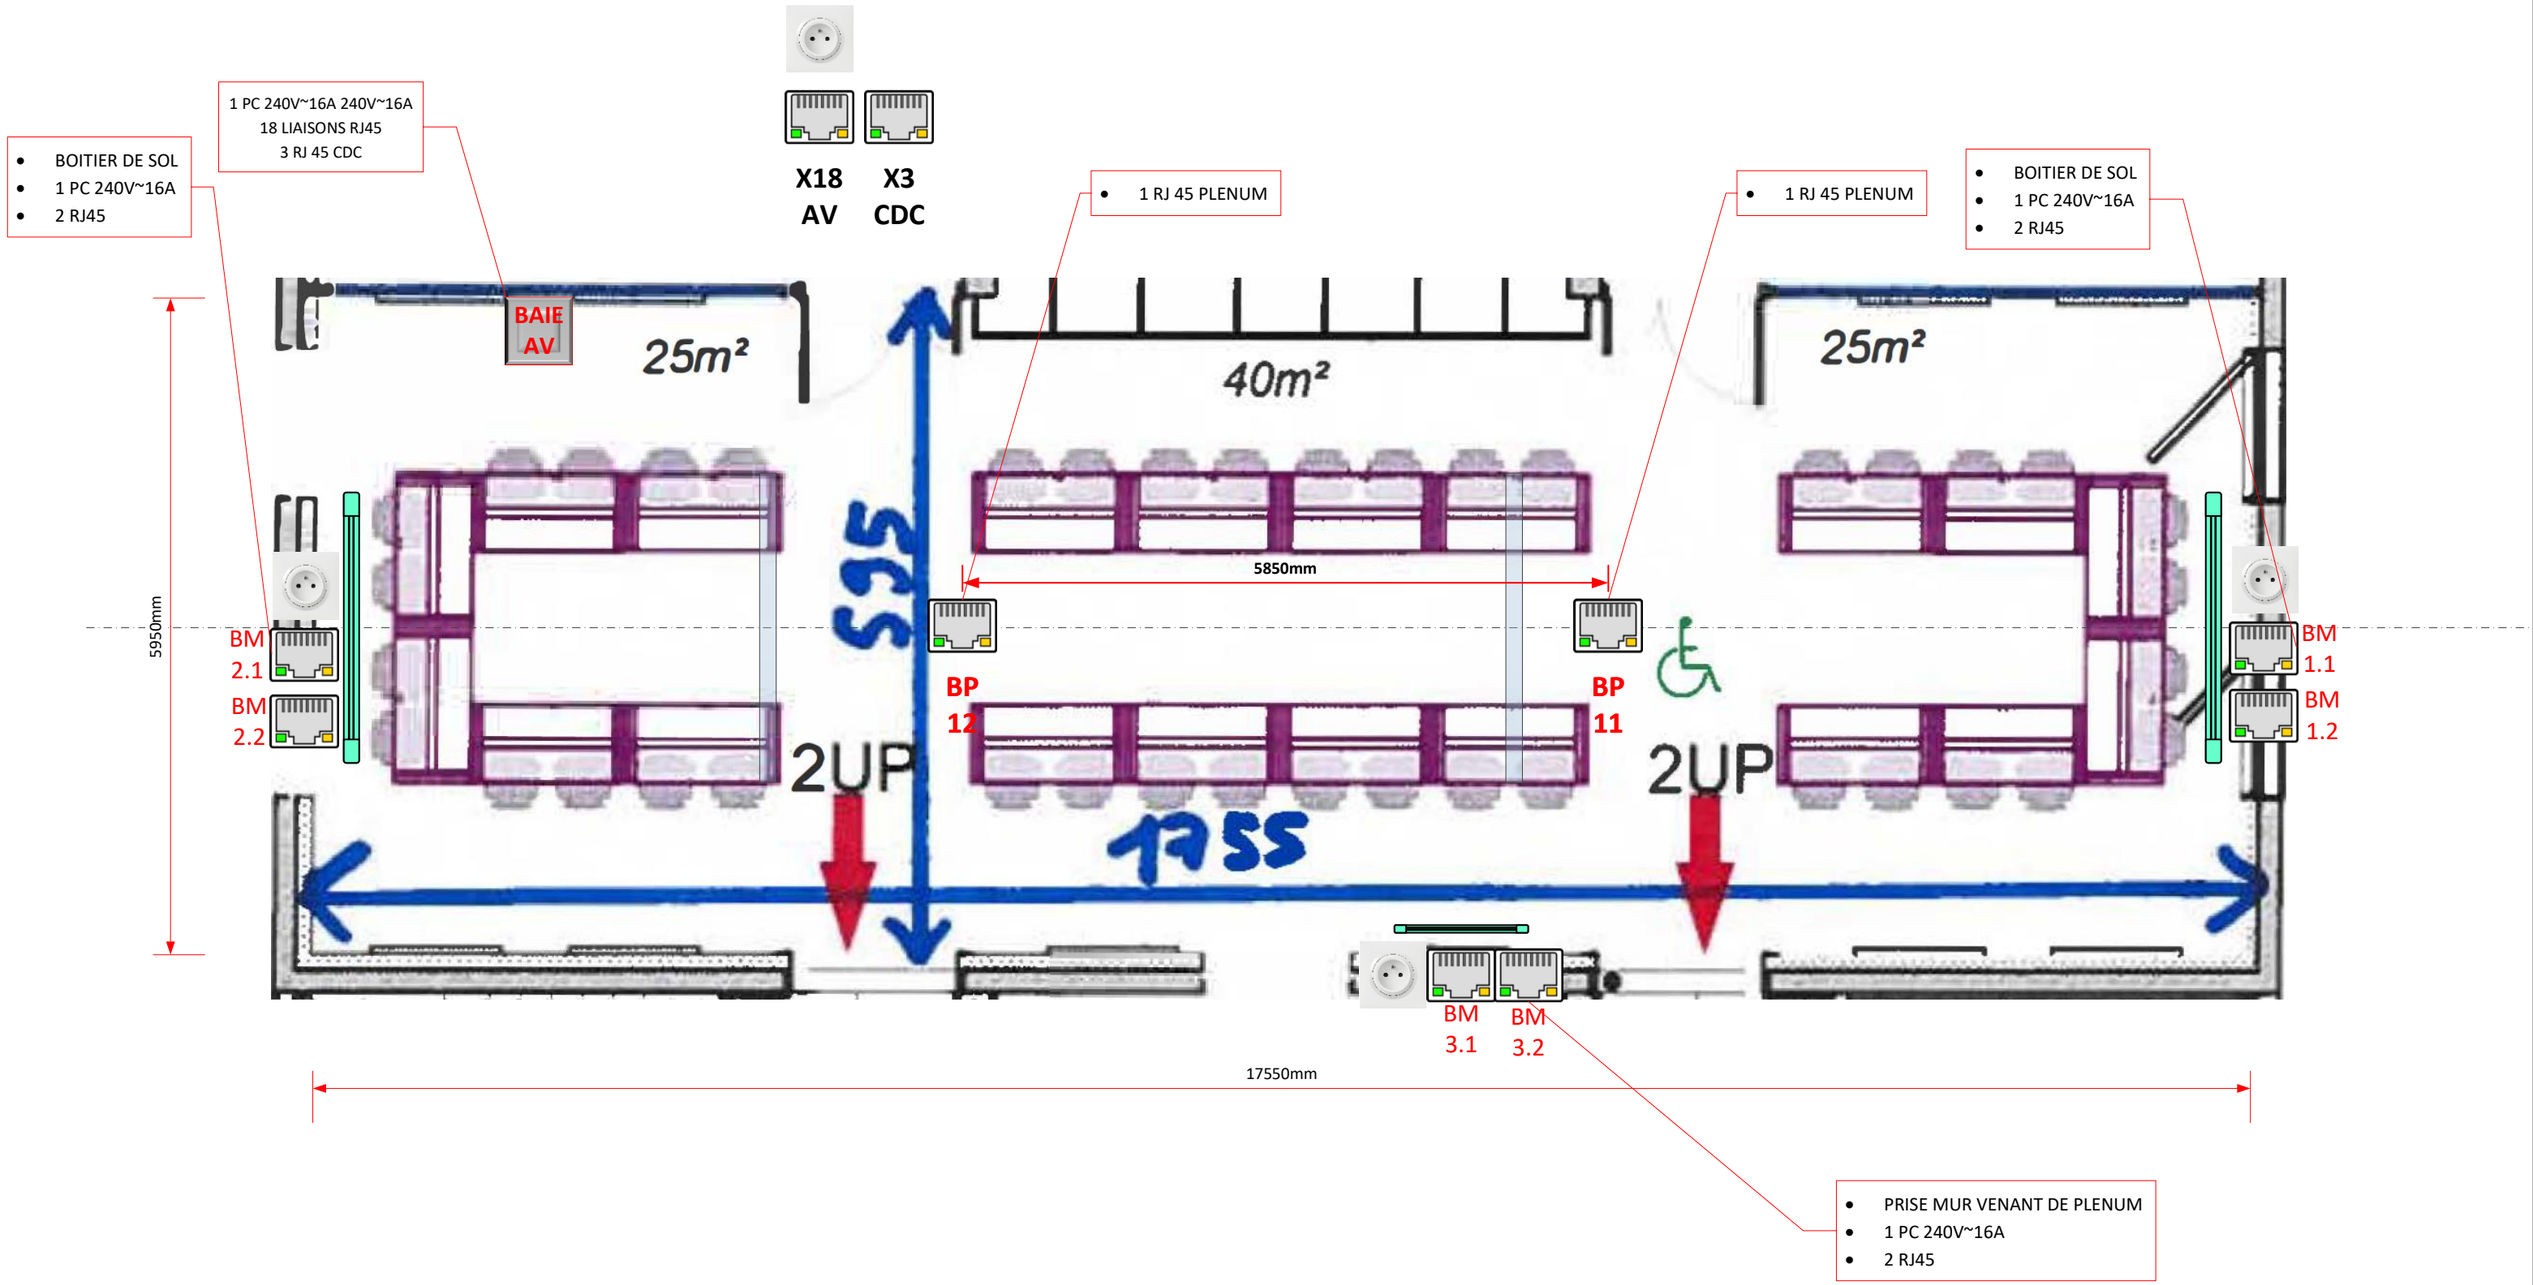

LEGENDE

HDMI	DVI
Audio	FIBRE
Speakers	HD SDI
USB	Display port
RS232	AC 240V
RJ45 cat6	DC OUT
Audio Dante (RJ45 Cat6)	PDU
Autres contrôles	

MUR
BAIE AV
TABLE

VIDEOSONIC
Image, Son & Technique
Za les portes de l'Oise
Batîment B2
rue Henri Becquerel
60230 CHAMBLY
Tel : 01 75 01 60 40
Fax : 01 75 01 60 41
t.fourmentraux@videosonic.fr

ANGERS CDC QUATUOR R+2 SALLE DE RUENION fmtx.vsdx

CAISSE DES DÉPÔTS ET CONSIGNATION

Thierry FOURMENTRAUX	DIMENSION A3	N° CODE 1:55,555 6	PAGE POSITION SALLE	RÉV 12/12/2025
12/12/2025	ECHELLE		FEUILLE 2 / 7	

CDC Quatuor Salle de réunion (voice lift)

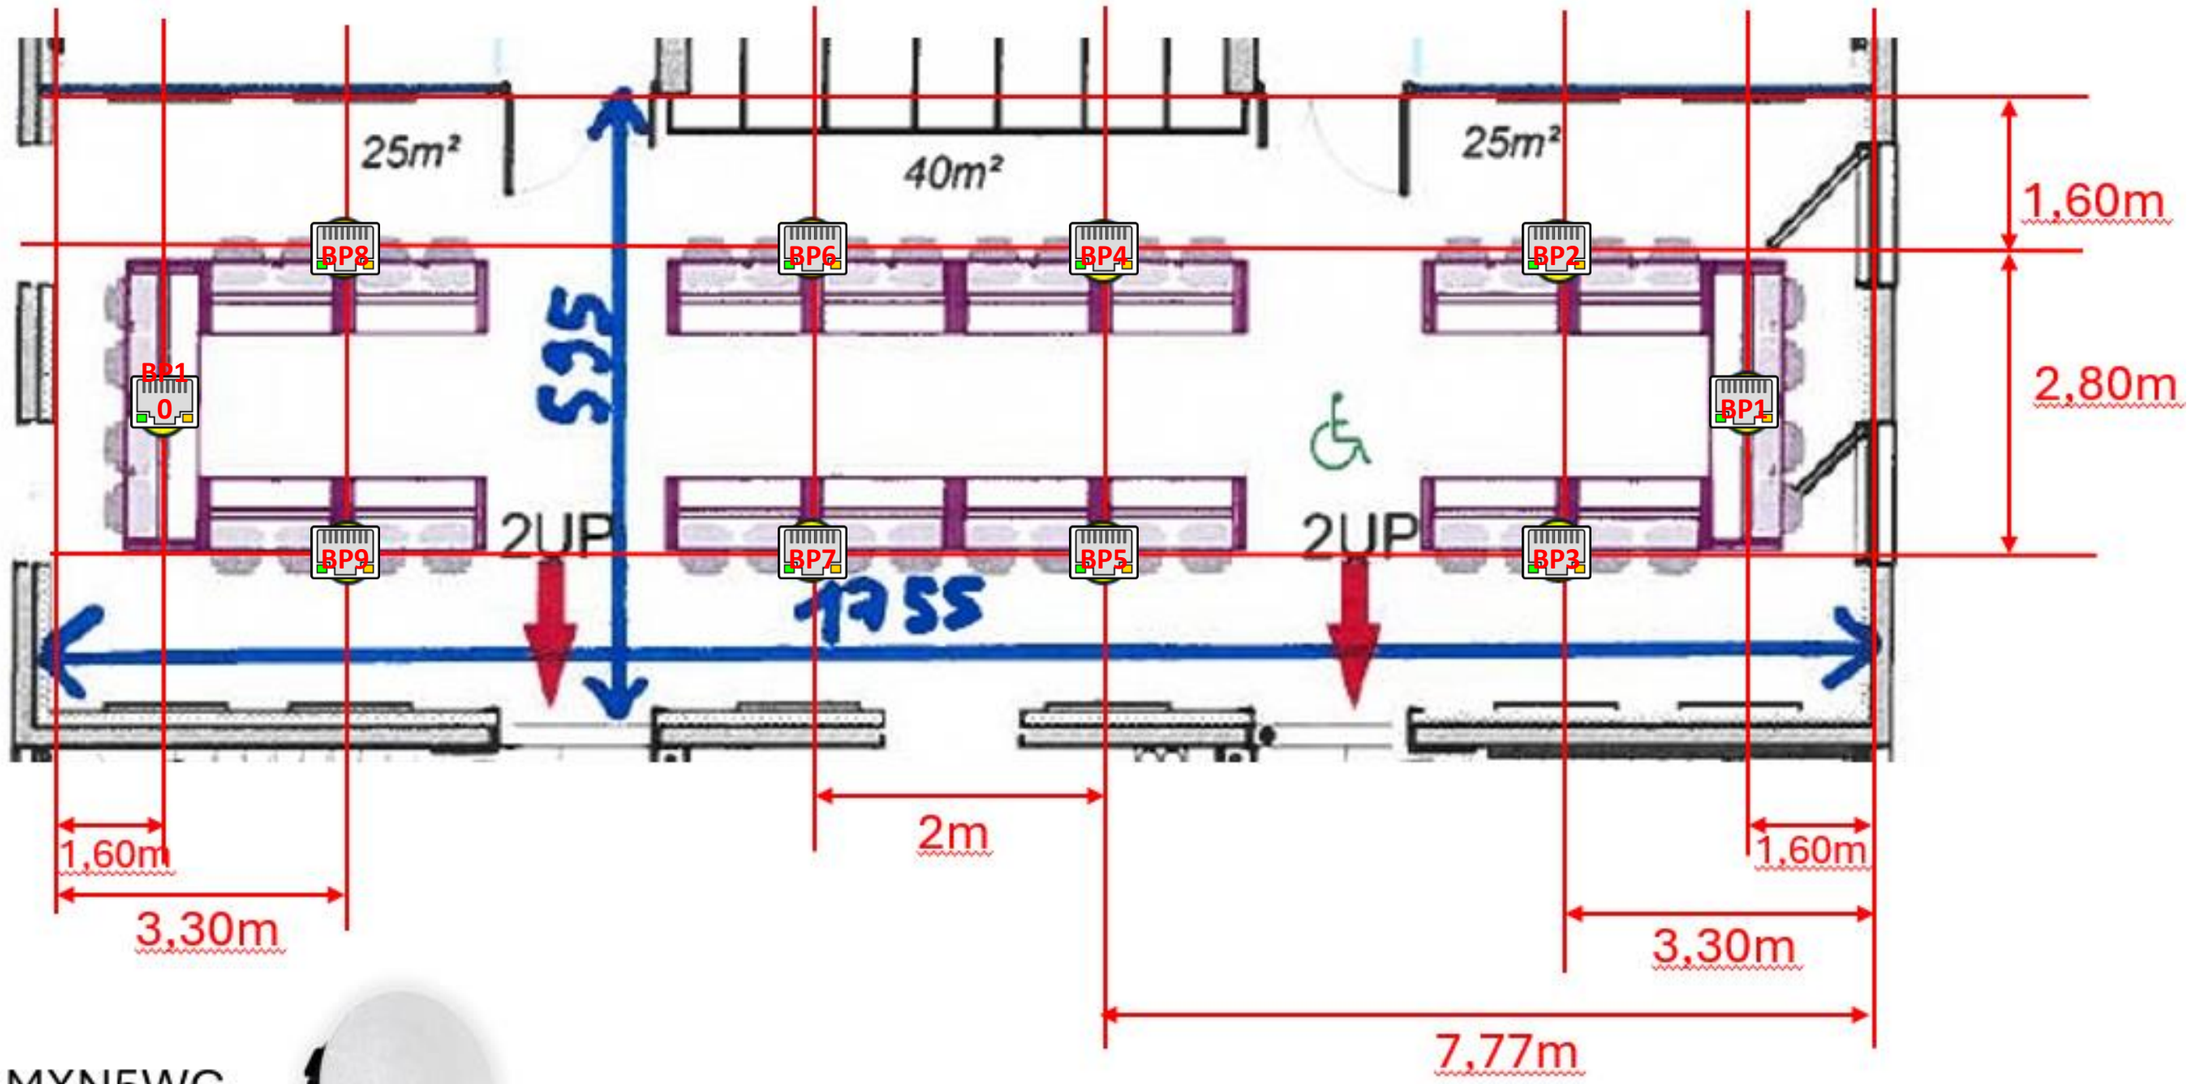

SHURE MXN5WC

LEGENDE	
HDMI	DVI
Audio	VGA
Speakers	HD SDI
USB	Display port
RS232	AC 240V
RJ45 cat6	DC OUT
Audio Dante (RJ45 Cat6)	PDU
Autres contrôles	

MUR
BAIE AV
TABLE

VIDEOSONIC Image, Son & Technique
Za les portes de l'Oise
Batîment B2
rue Henri Becquerel
60230 CHAMBLY
Tel : 01 75 01 60 40
Fax : 01 75 01 60 41
t.fourmentraux@videosonic.fr

ANGERS CDC QUATUOR R+2 SALLE DE RUENION fmtx.vsdx

CAISSE DES DÉPÔTS ET CONSIGNATION

Thierry FOURMENTRAUX	DIMENSION	N° CODE	PAGE	RÉV
	A3		POSITON HP	12/12/2025
12/12/2025	ECHELLE 1:1		FEUILLE 3 / 7	

- PRISE MURALE
- 1 PC
- 2 RJ45

- PRISE PLACARD
- 1 PC
- 3 RJ45
- LIAISON HP EXISTANTE A DÉPLACER ICI

- PRISE MURALE
- 1 PC
- 2 RJ45

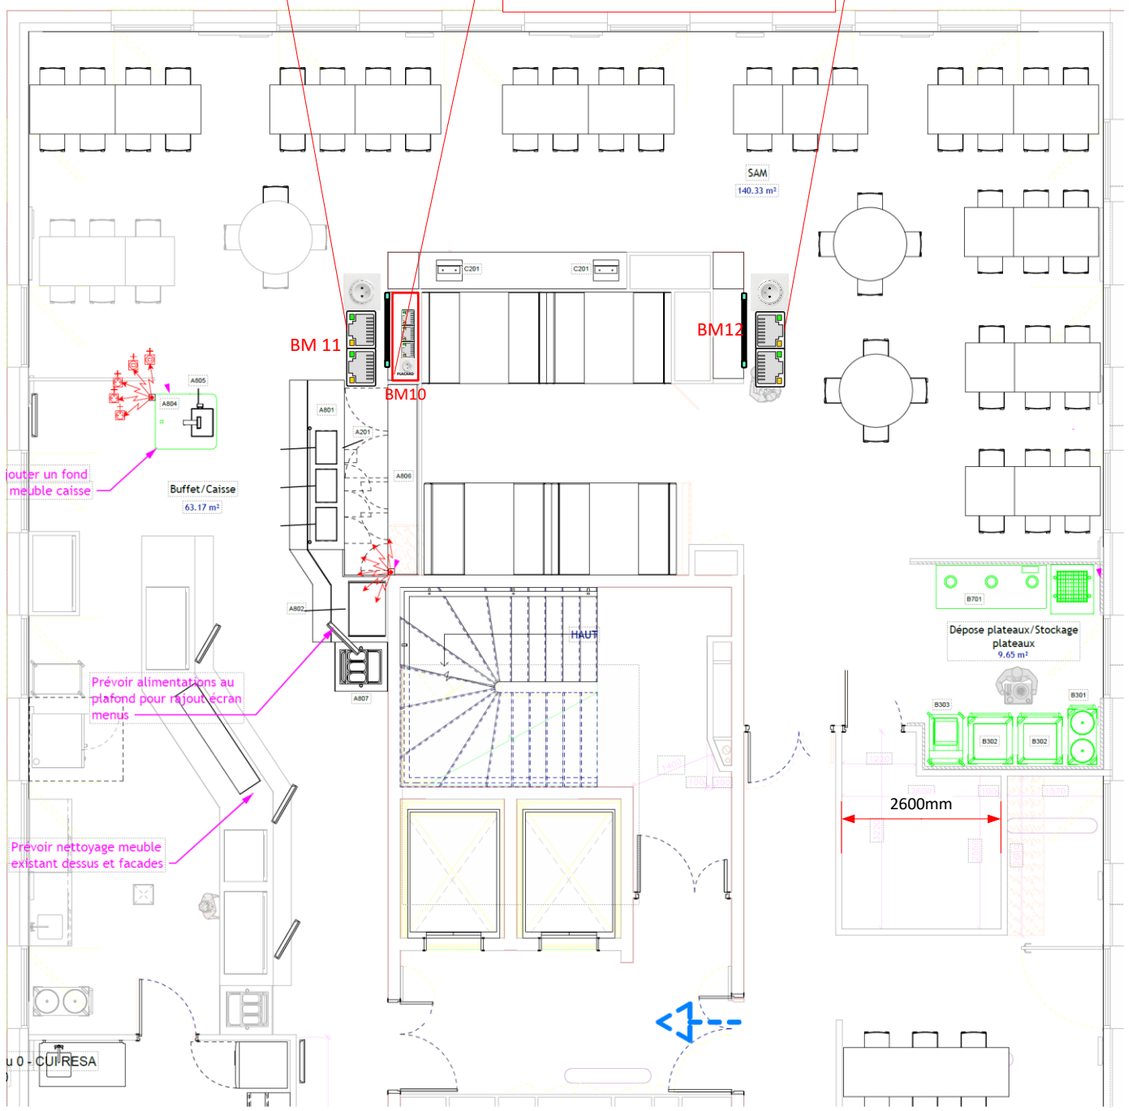

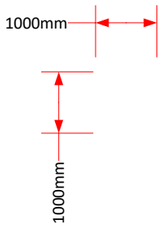

VIDEOSONIC
Image, Son & Technique
Za les portes de l'Oise
Batîment B2
rue Henri Becquerel
60230 CHAMBLY
Tel : 01 75 01 60 40
Fax : 01 75 01 60 41
t.fourmentraux@videosonic.fr

ANGERS CDC QUATUOR R+2 SALLE DE RUENION fmtx.vsdx

CAISSE DES DÉPÔTS ET CONSIGNATION

Thierry FOURMENTRAUX	DIMENSION	N° CODE	PAGE	RÉV
	A3		RIE	12/12/2025
12/12/2025	ECHELLE 1:100		FEUILLE	4 / 7

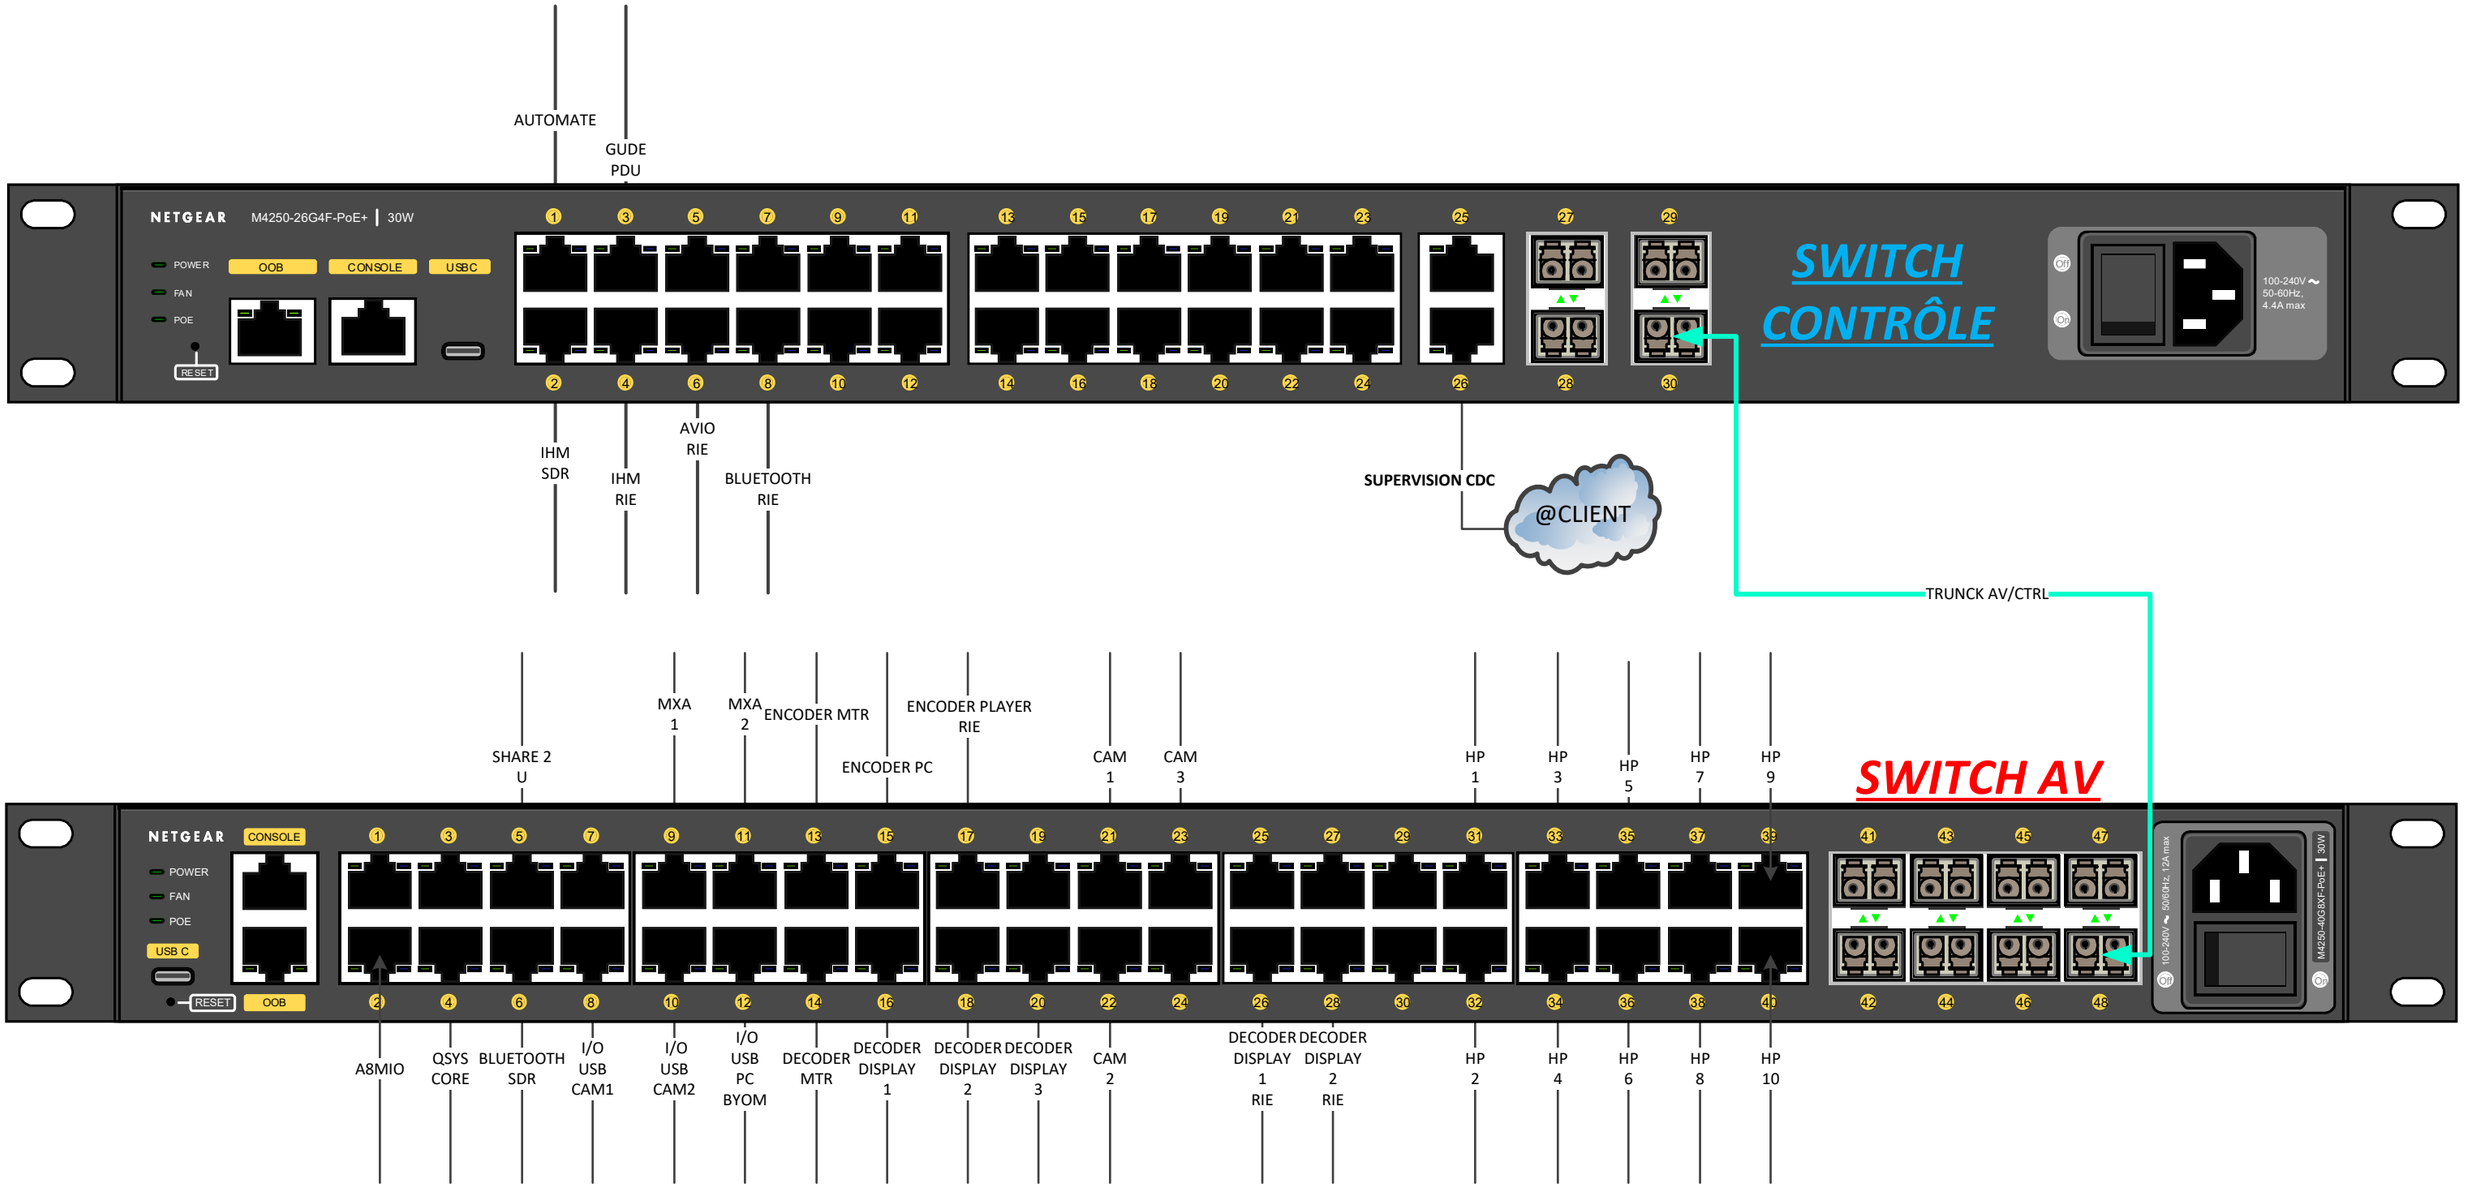

PORT LIBRE

VIDEOSONIC
Image, Son & Technique
Za les portes de l'Oise
Batîment B2
rue Henri Becquerel
60230 CHAMBLY
Tel : 01 75 01 60 40
Fax : 01 75 01 60 41
t.fourmentraux@videosonic.fr

ANGERS CDC QUATUOR R+2 SALLE DE RUENION fmtx.vsdx

CAISSE DES DÉPÔTS ET CONSIGNATION

Thierry FOURMENTRAUX	DIMENSION A3	N° CODE	PAGE Switch	RÉV 12/12/2025
12/12/2025	ECHELLE 1:1		FEUILLE 5 / 7	

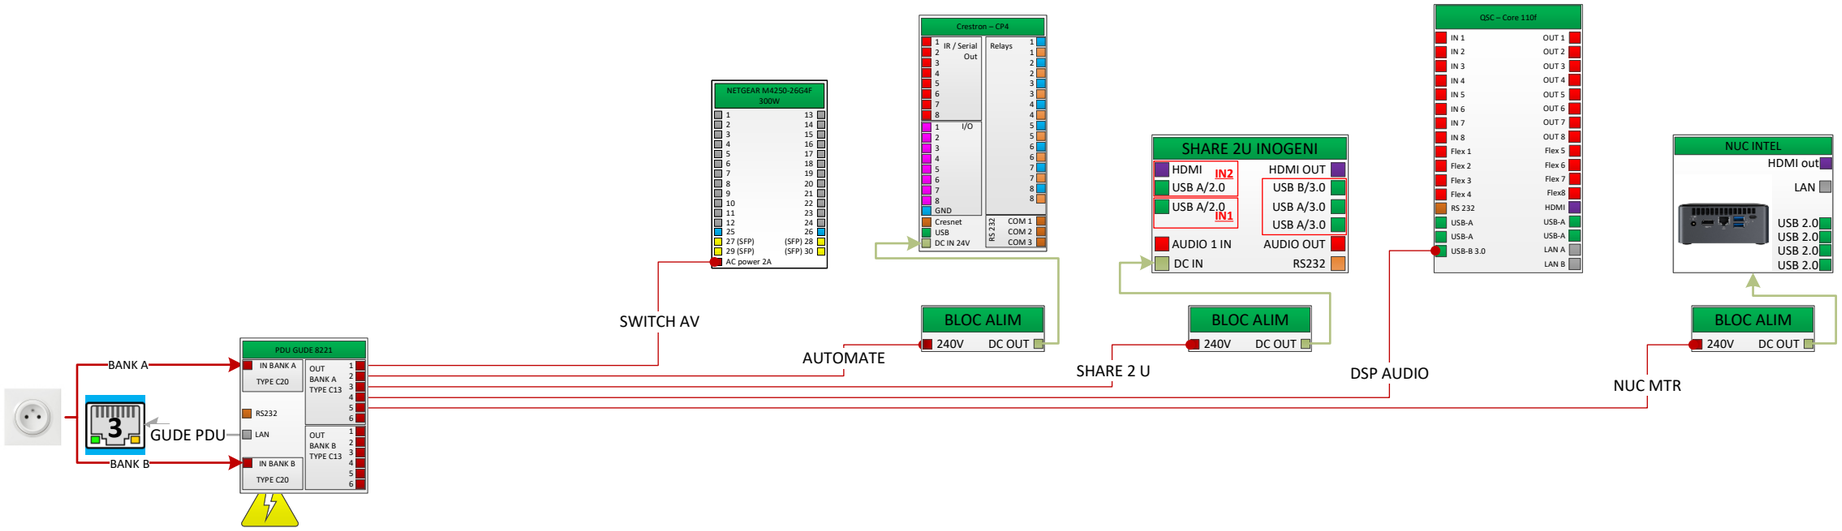

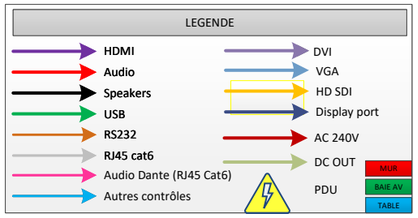

VIDEOSONIC
Image, Son & Technique
Za les portes de l'Oise
Batîment B2
rue Henri Becquerel
60230 CHAMBLY
Tel : 01 75 01 60 40
Fax : 01 75 01 60 41
t.fourmentraux@videosonic.fr

ANGERS CDC QUATUOR R+2 SALLE DE RUENION fmtx.vsdx

CAISSE DES DÉPÔTS ET CONSIGNATION

Thierry FOURMENTRAUX	DIMENSION	N° CODE	PAGE	RÉV
	A3		PDU	12/12/2025
12/12/2025	ECHELLE 1:1		FEUILLE	6 / 7

BAIE AV 21U

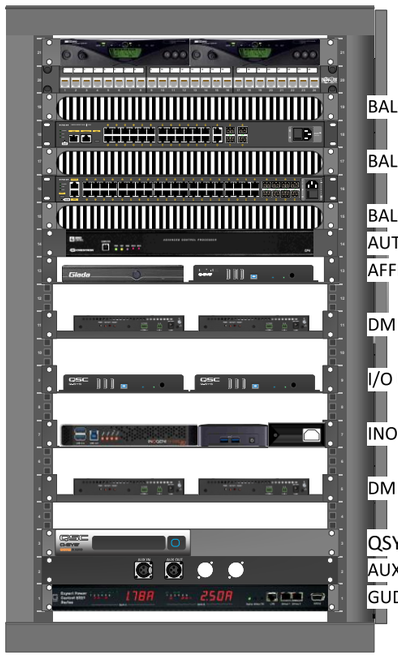

1 U	
1 U	BALAIS PASSE CABLE
	SWITCH CTRL M4250-26G4F-PoE+
1 U	BALAIS PASSE CABLE
	SWITCH AV M4250-40G8XF-PoE+
1 U	BALAIS PASSE CABLE
1 U	AUTOMATE CRESTRON CP4
1 U	AFFICHAGE DYNAMIQUE PLAYER RIE + I/O USB PC BYOM
1 U	DM NVX ENCODER PC + ENCODER PLAYER RIE
1 U	I/O USB BRIDGE CAM 1 ET 2
1 U	INOGENIE SHARE2U + MTR + ALIM
1 U	DM NVX ENCODER MTR + DECODER MTR
1 U	QSYS CORE NANO + ATTEROTECH A8MIO
1 U	AUXILIAIRE IN/OUT
1 U	GUDE PDU 8041

BAIE AV 21U

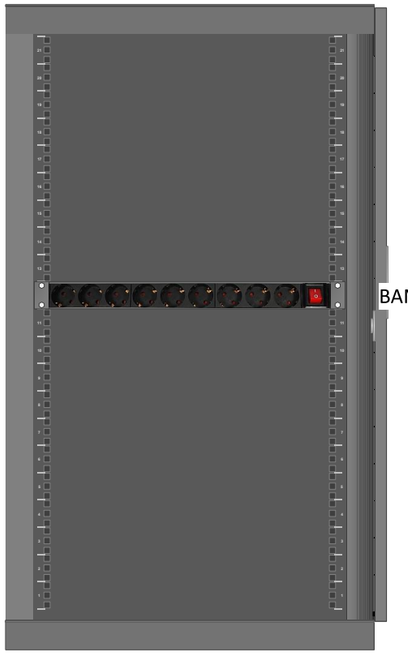

1 U	BANDEAU 9 PRISES

VIDEOSONIC
Image, Son & Technique
Za les portes de l'Oise
Batîment B2
rue Henri Becquerel
60230 CHAMBLY
Tel : 01 75 01 60 40
Fax : 01 75 01 60 41
t.fourmentraux@videosonic.fr

ANGERS CDC QUATUOR R+2 SALLE DE RUENION fmtx.vsdx

CAISSE DES DÉPÔTS ET CONSIGNATION

Thierry FOURMENTRAUX	DIMENSION	N° CODE	PAGE	RÉV
	A3		PLAN DE BAIE	12/12/2025
12/12/2025	ECHELLE 1:10		FEUILLE 7 / 7	