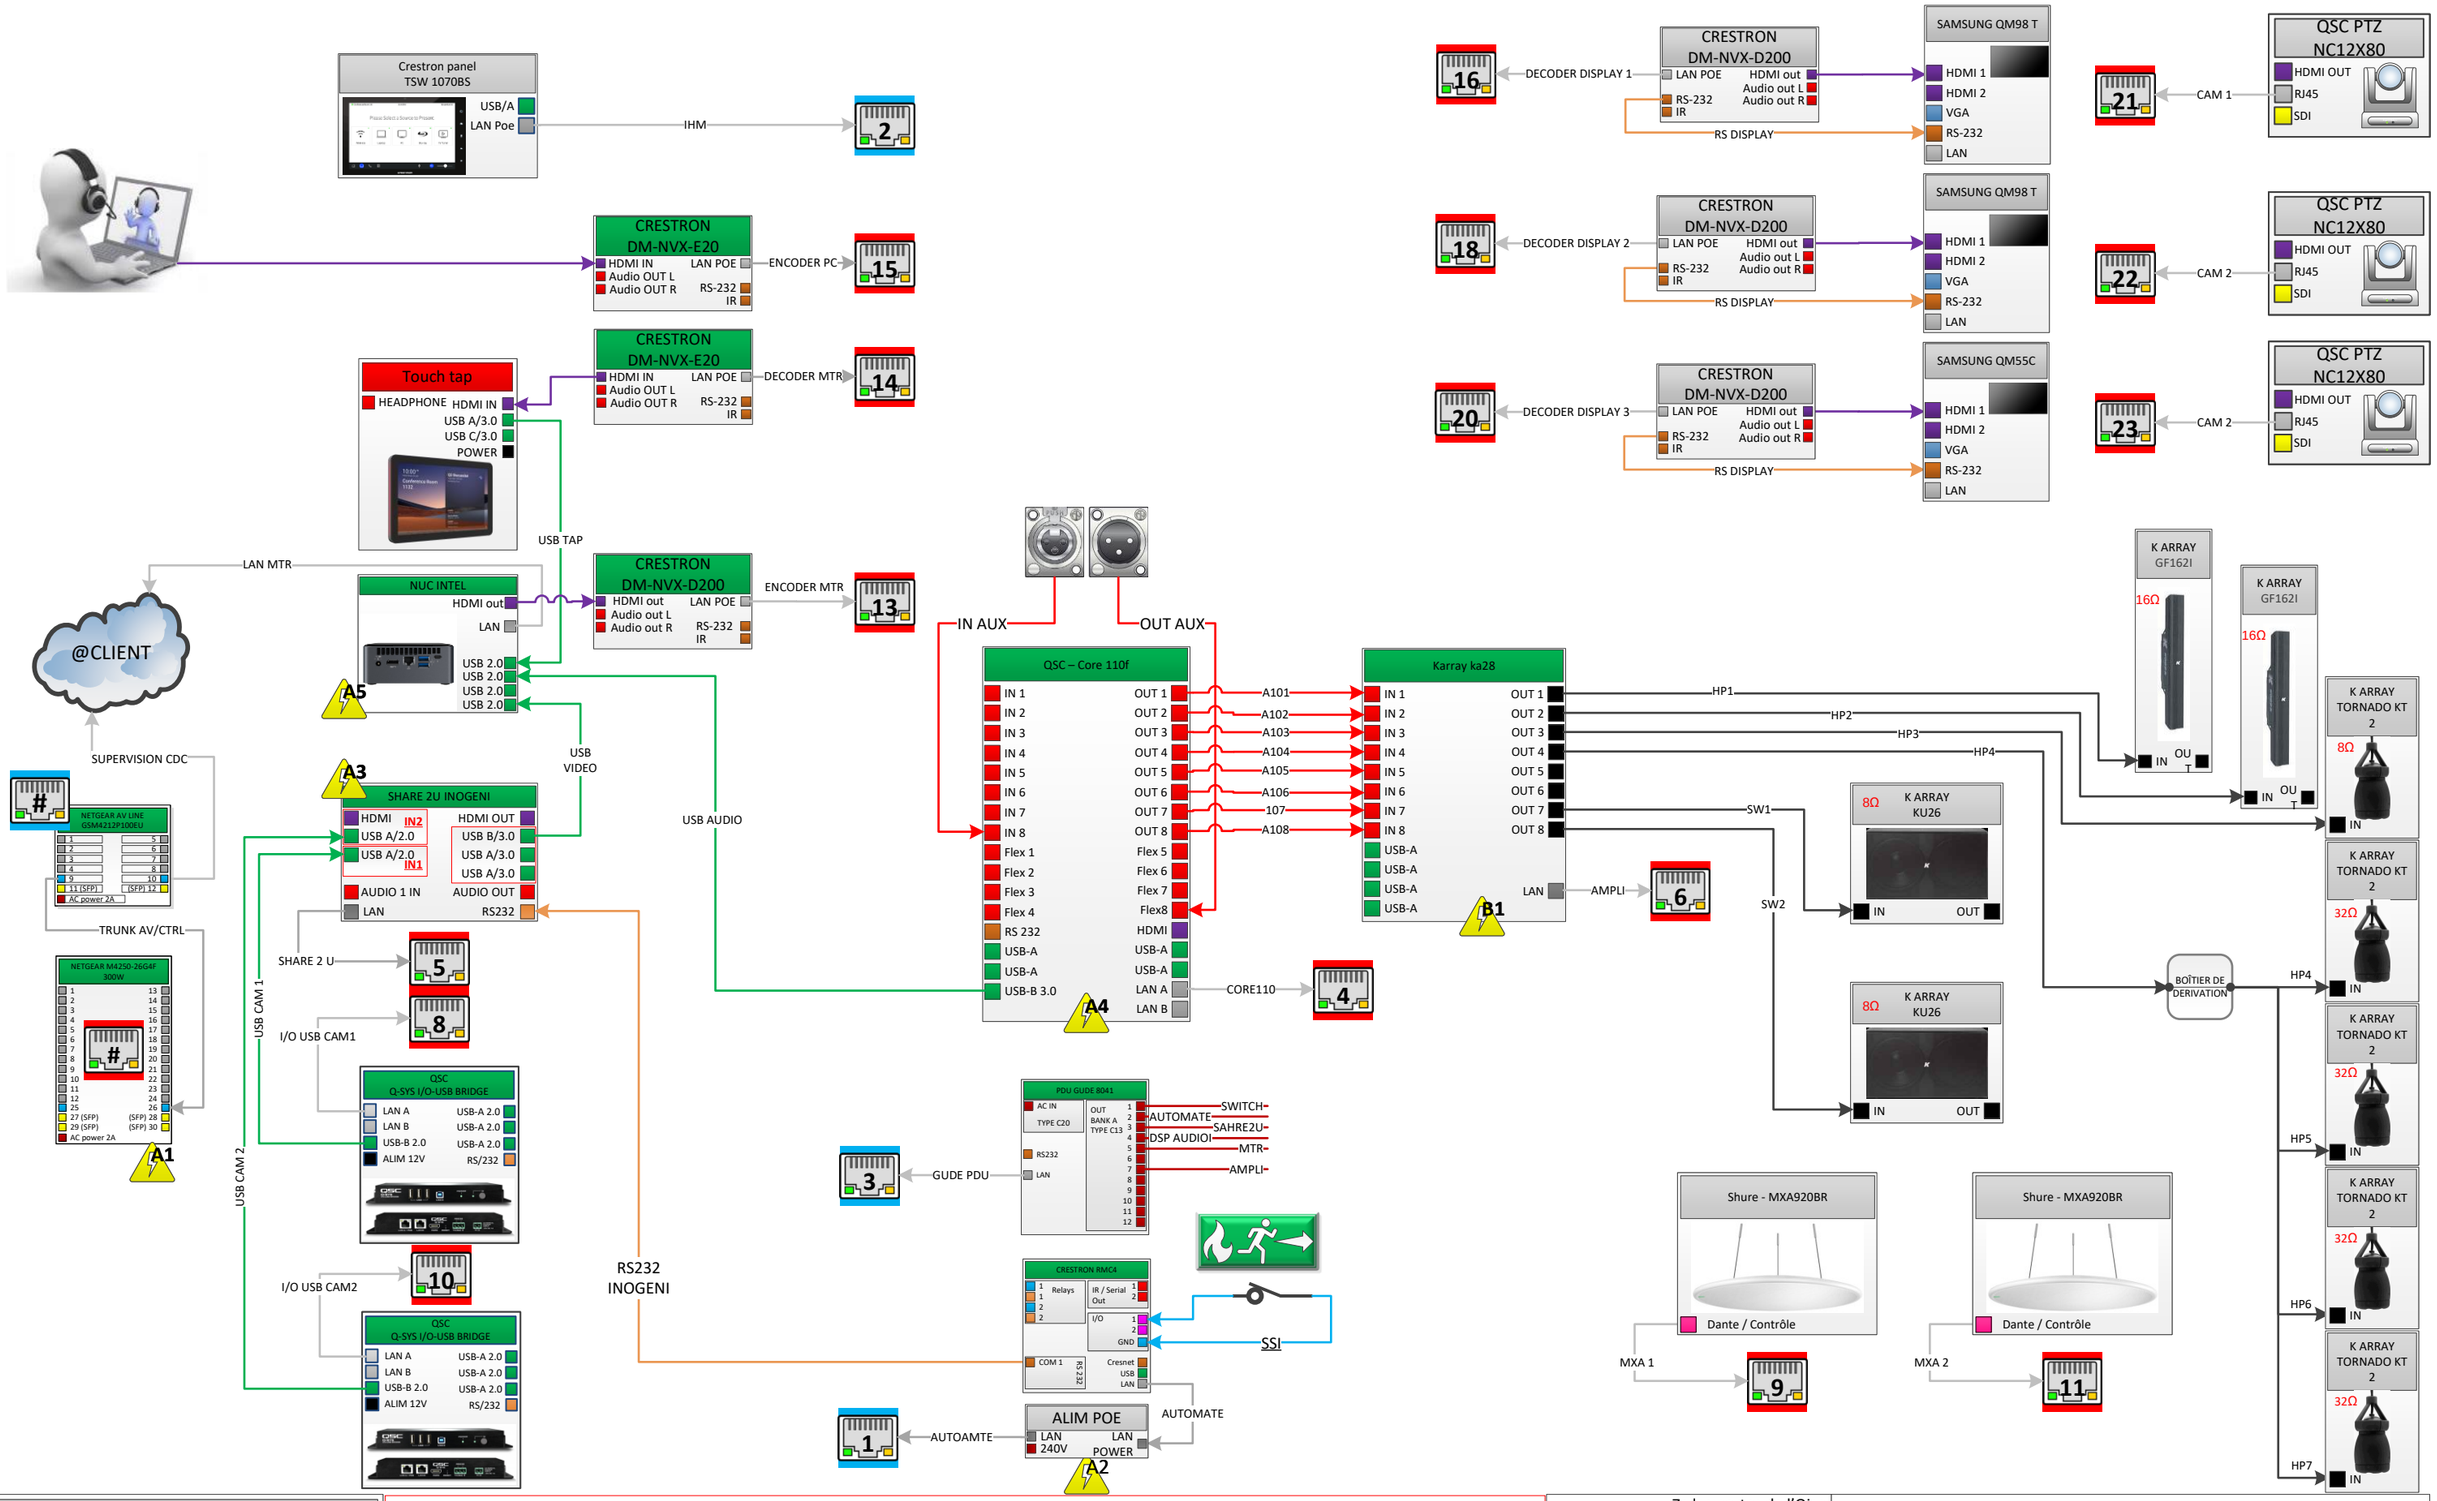

LEGENDE	
HDMI	DVI
Audio	VGA
Speakers	HD SDI
USB	Display port
RS232	AC 240V
RJ45 cat6	DC OUT
Audio Dante (RJ45 Cat6)	PDU
Autres contrôles	MUR / BAIE AV / TABLE

PORT LIBRE

1 2 3 7 12 17 19 24

4 5 6 7 8

VIDEOSONIC
Image, Son & Technique
Za les portes de l'Oise
Batîment B2 – rue Henri Becquerel
60230 CHAMBLY
Tel : 01 75 01 60 40
Fax : 01 75 01 60 41
t.fourmentraux@videosonic.fr
FOURMENTRAUX Thierry

16/05/2025

Caisse des dépôts et consignations

ANGERS CDC R+4 SALLE DE RÉUNION 40 PERSONNES

DIMENSION			RÉV
A3		SYNOPTIQUE AVC	1
ECHELLE 1:1		FEUILLE	1 / 5

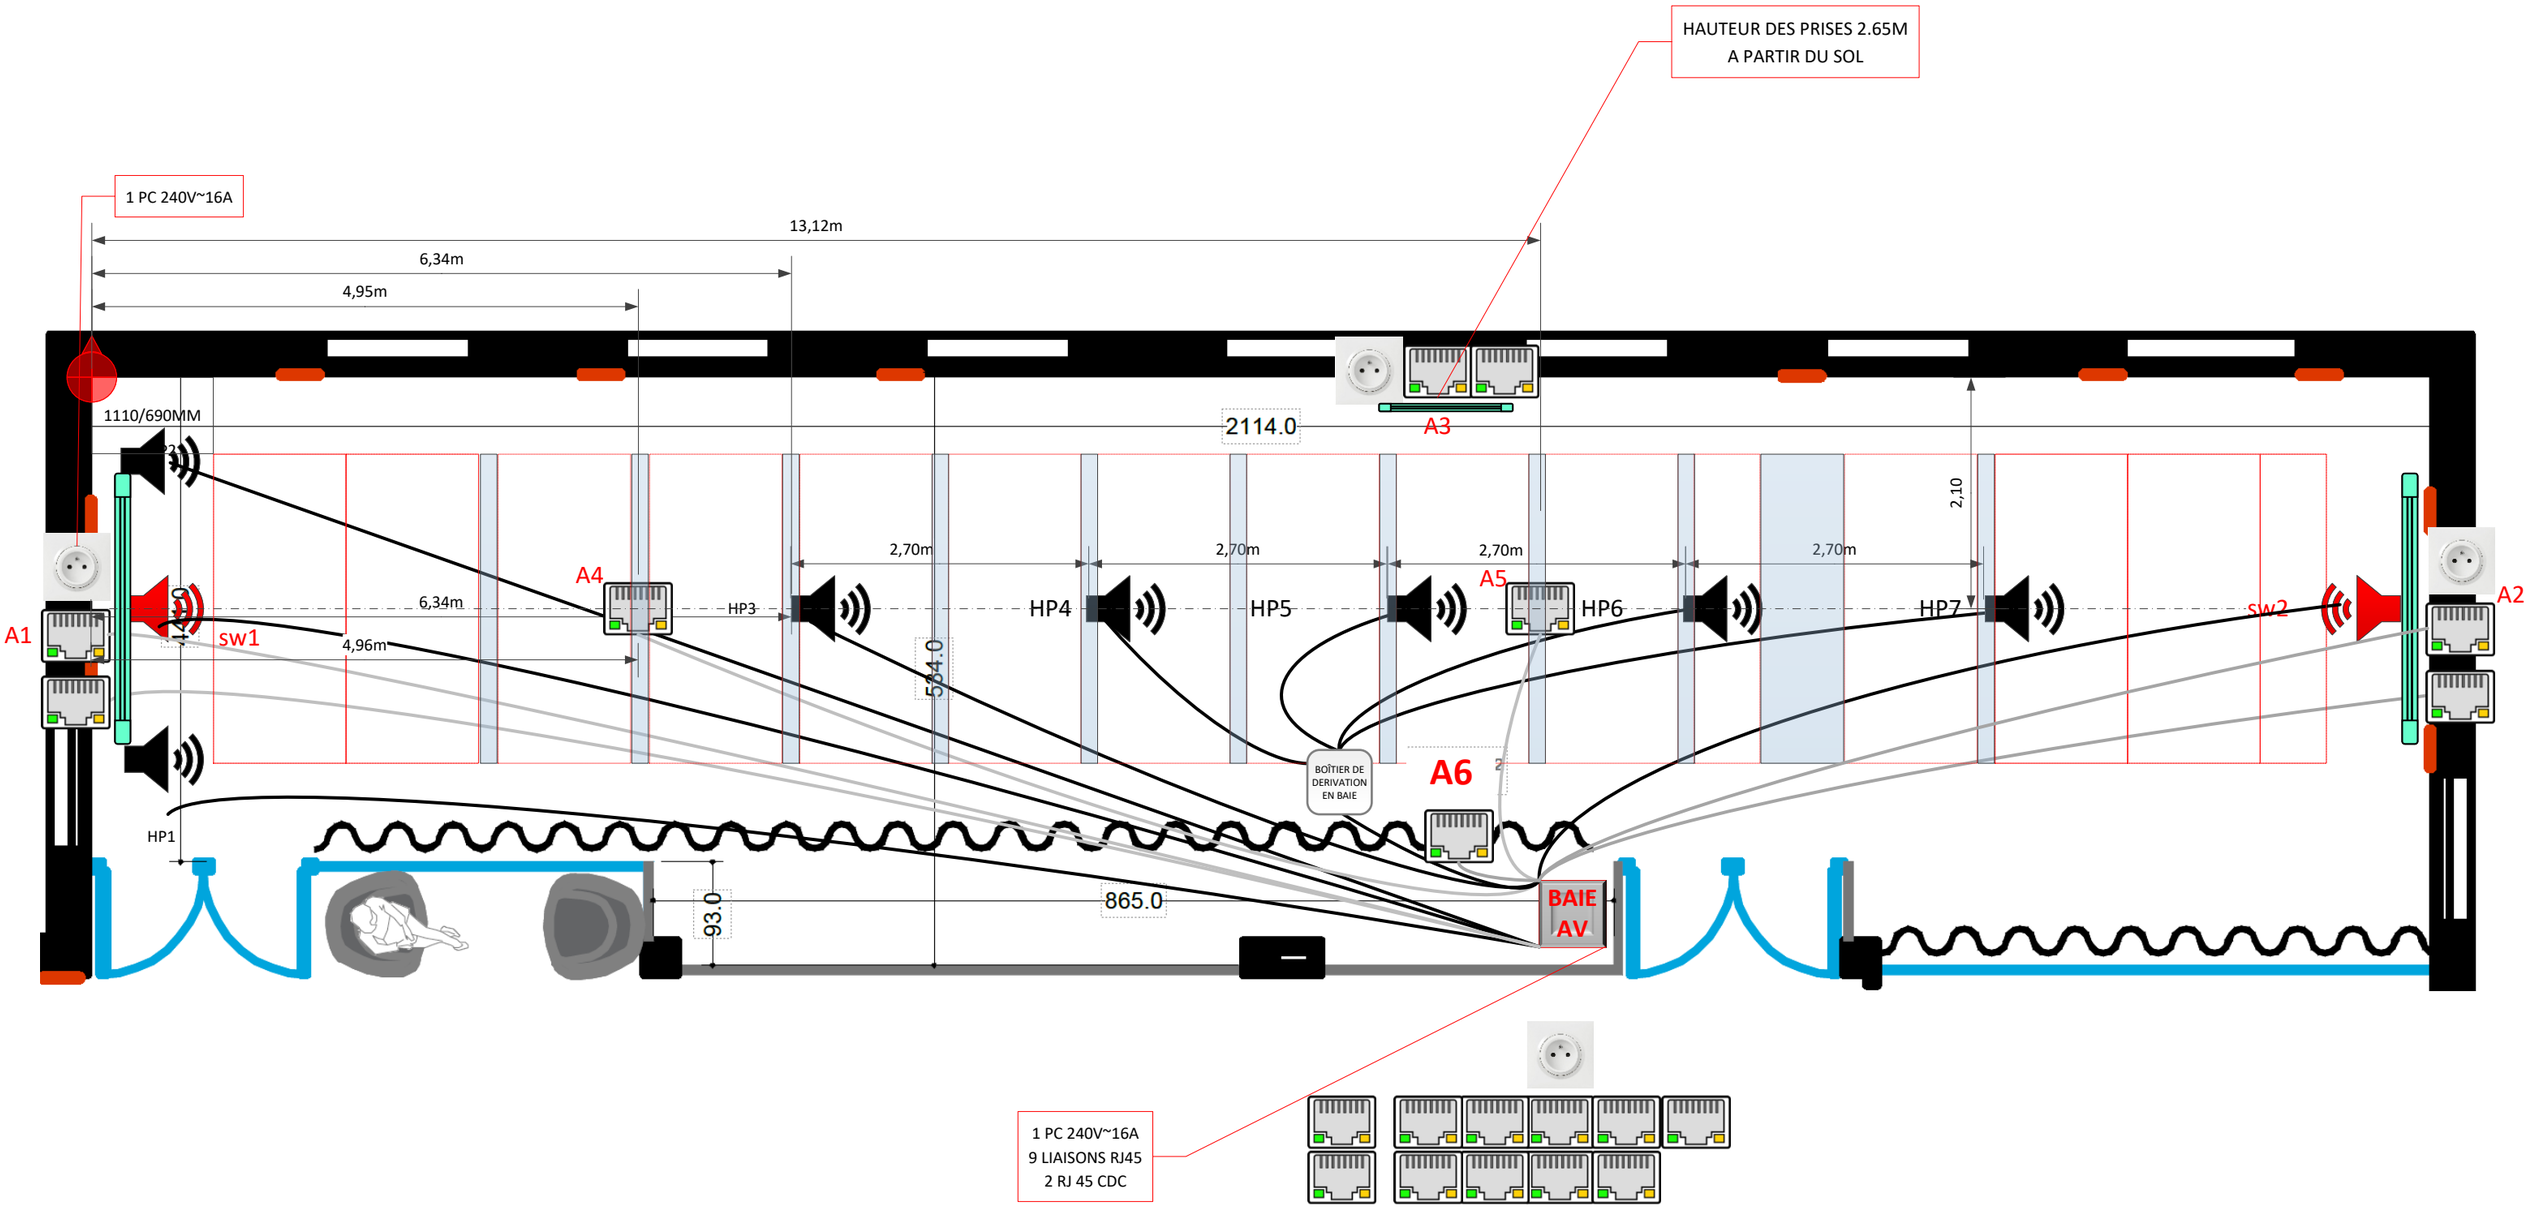

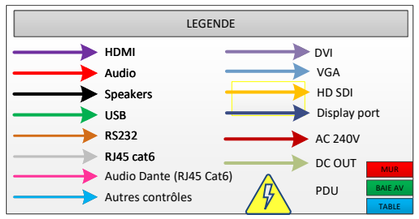

- **SOL/ DALLE BÉTON = 3083MM**
- **SOL/ DALLE ACOUSTIQUE = 2683MM**

VIDEOSONIC
Image, Son & Technique
Za les portes de l'Oise
Batîment B2 – rue Henri Becquerel
60230 CHAMBLY
Tel : 01 75 01 60 40
Fax : 01 75 01 60 41
t.fourmentraux@videosonic.fr
FOURMENTRAUX Thierry

16/05/2025

Caisse des dépôts et consignations

ANGERS CDC R+4 SALLE DE RÉUNION 40 PERSONNES

DIMENSION			RÉV
A3		PLAN	1
ECHELLE	1:55,5556	FEUILLE	2 / 5

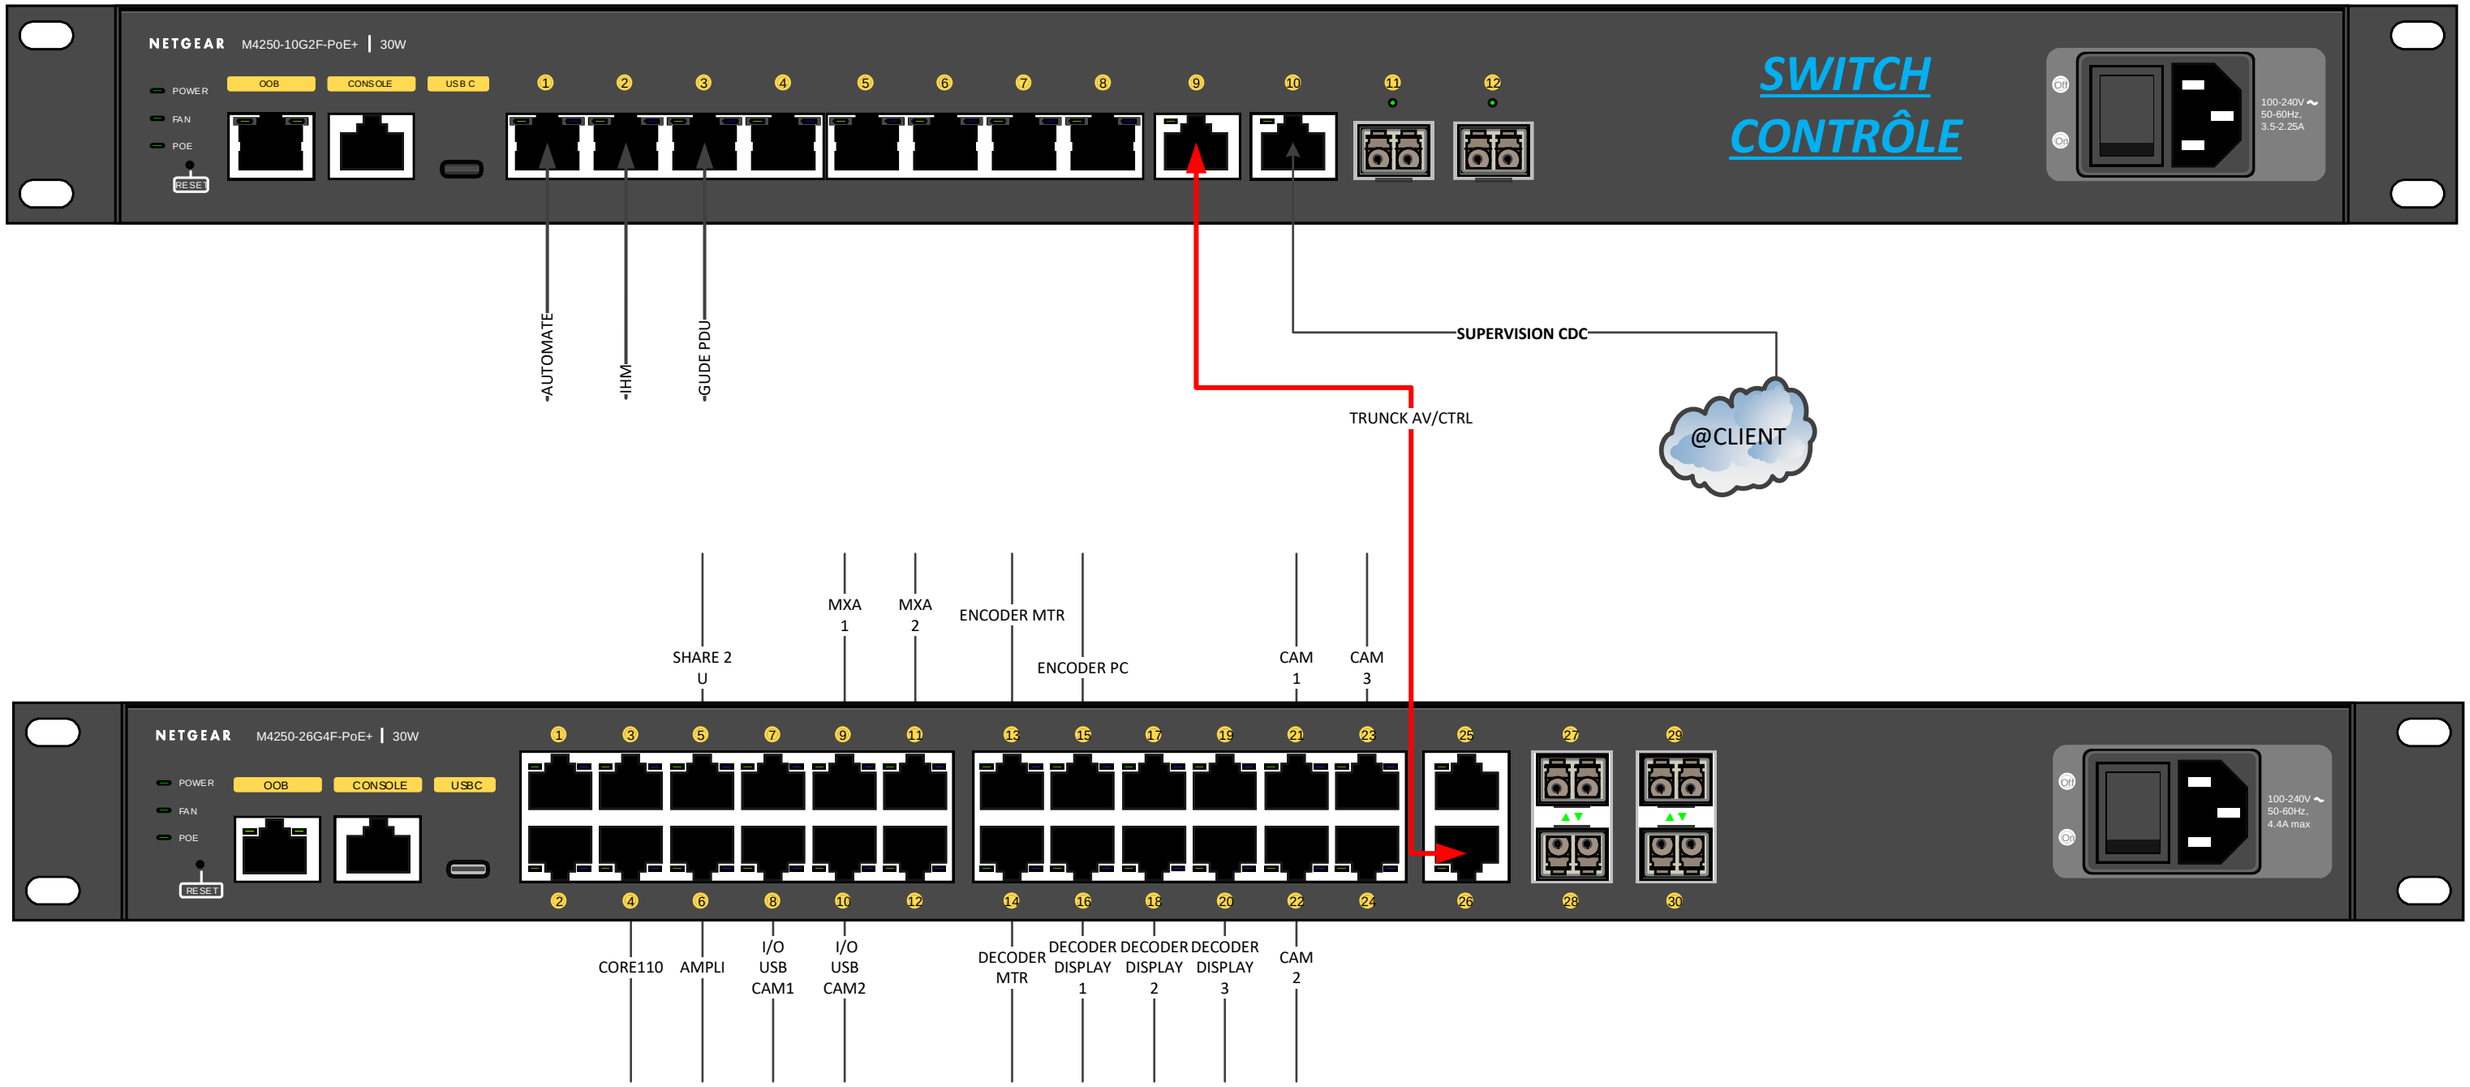

VIDEOSONIC
Image, Son & Technique
Za les portes de l'Oise
Batîment B2 – rue Henri
Becquerel
60230 CHAMBLY
Tel : 01 75 01 60 40
Fax : 01 75 01 60 41
t.fourmentraux@videosonic.fr

FOURMENTRAUX Thierry

16/05/2025

Caisse des dépôts et consignations

ANGERS CDC R+4 SALLE DE RÉUNION 40 PERSONNES

DIMENSION			RÉV
A3		SWITCH AV	1
ECHELLE 1:1			FEUILLE 3 / 5

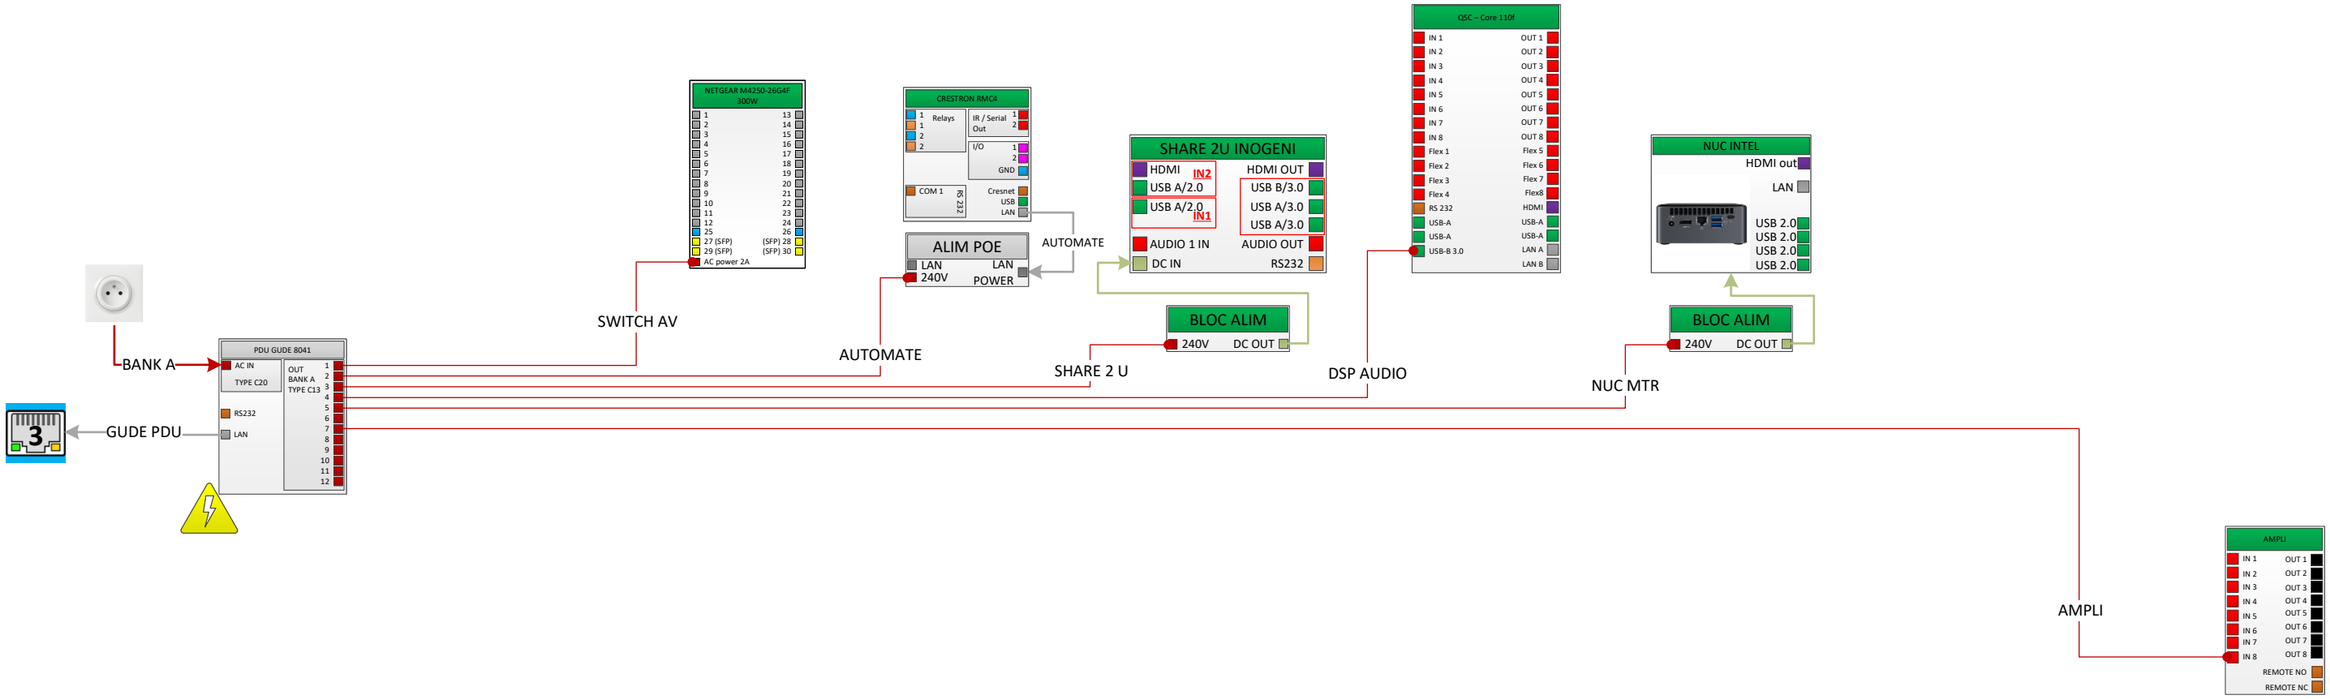

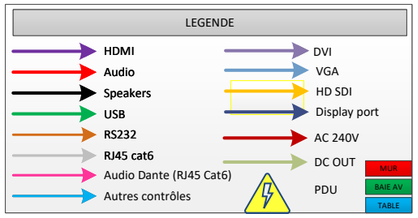

VIDEOSONIC
Image, Son & Technique
Za les portes de l'Oise
Batîment B2 – rue Henri Becquerel
60230 CHAMBLY
Tel : 01 75 01 60 40
Fax : 01 75 01 60 41
t.fourmentraux@videosonic.fr

Caisse des dépôts et consignations

ANGERS CDC R+4 SALLE DE RÉUNION 40 PERSONNES

FOURMENTRAUX Thierry	DIMENSION A3	PDU GUDE	RÉV 1
16/05/2025	ECHELLE 1:1		FEUILLE 4 / 5

BAIE AV 22U

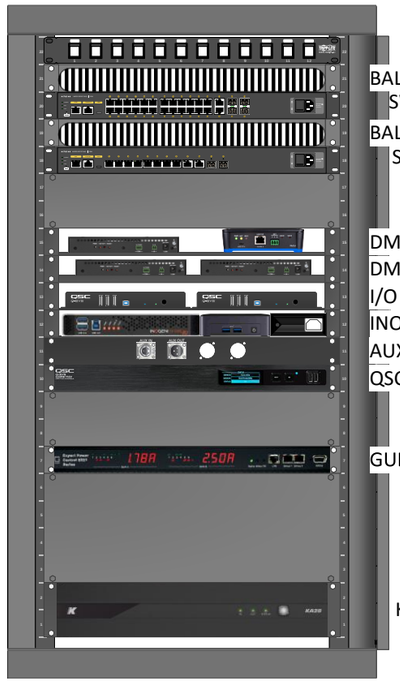

	PATCH RJ 45
1 U	BALAIS PASSE CABLE
	SWITCH AV M4250-26G4F-PoE+
1 U	BALAIS PASSE CABLE
	SWITCH CTRL M4250-10G2F-PoE+
2 U	
1 U	DM NVX ENCODER PC + AUTOMATE RMC4
1 U	DM NVX ENCODER MTR + DECODER MTR
1 U	I/O USB BRIDGE CAM 1 ET 2
1 U	INOGENIE SHARE2U + MTR + ALIM
1 U	AUXILIAIRE IN/OUT
1 U	QSC Q-SYS CORE 110F
2 U	
1 U	GUDE PDU 8041
4 U	
2 U	K ARRAY KA28

BAIE AV 22U

1 U	BANDEAU 9 PRISES

VIDEOSONIC
Image, Son & Technique

Za les portes de l'Oise
Batiment B2 – rue Henri Becquerel
60230 CHAMBLY

Tel : 01 75 01 60 40
Fax : 01 75 01 60 41
t.fourmentraux@videosonic.fr

FOURMENTRAUX Thierry

16/05/2025

Caisse des dépôts et consignations

ANGERS CDC R+4 SALLE DE RÉUNION 40 PERSONNES

DIMENSION			RÉV
A3		PLAN DE BAIE	1
ECHELLE 1:10		FEUILLE 5 / 5	