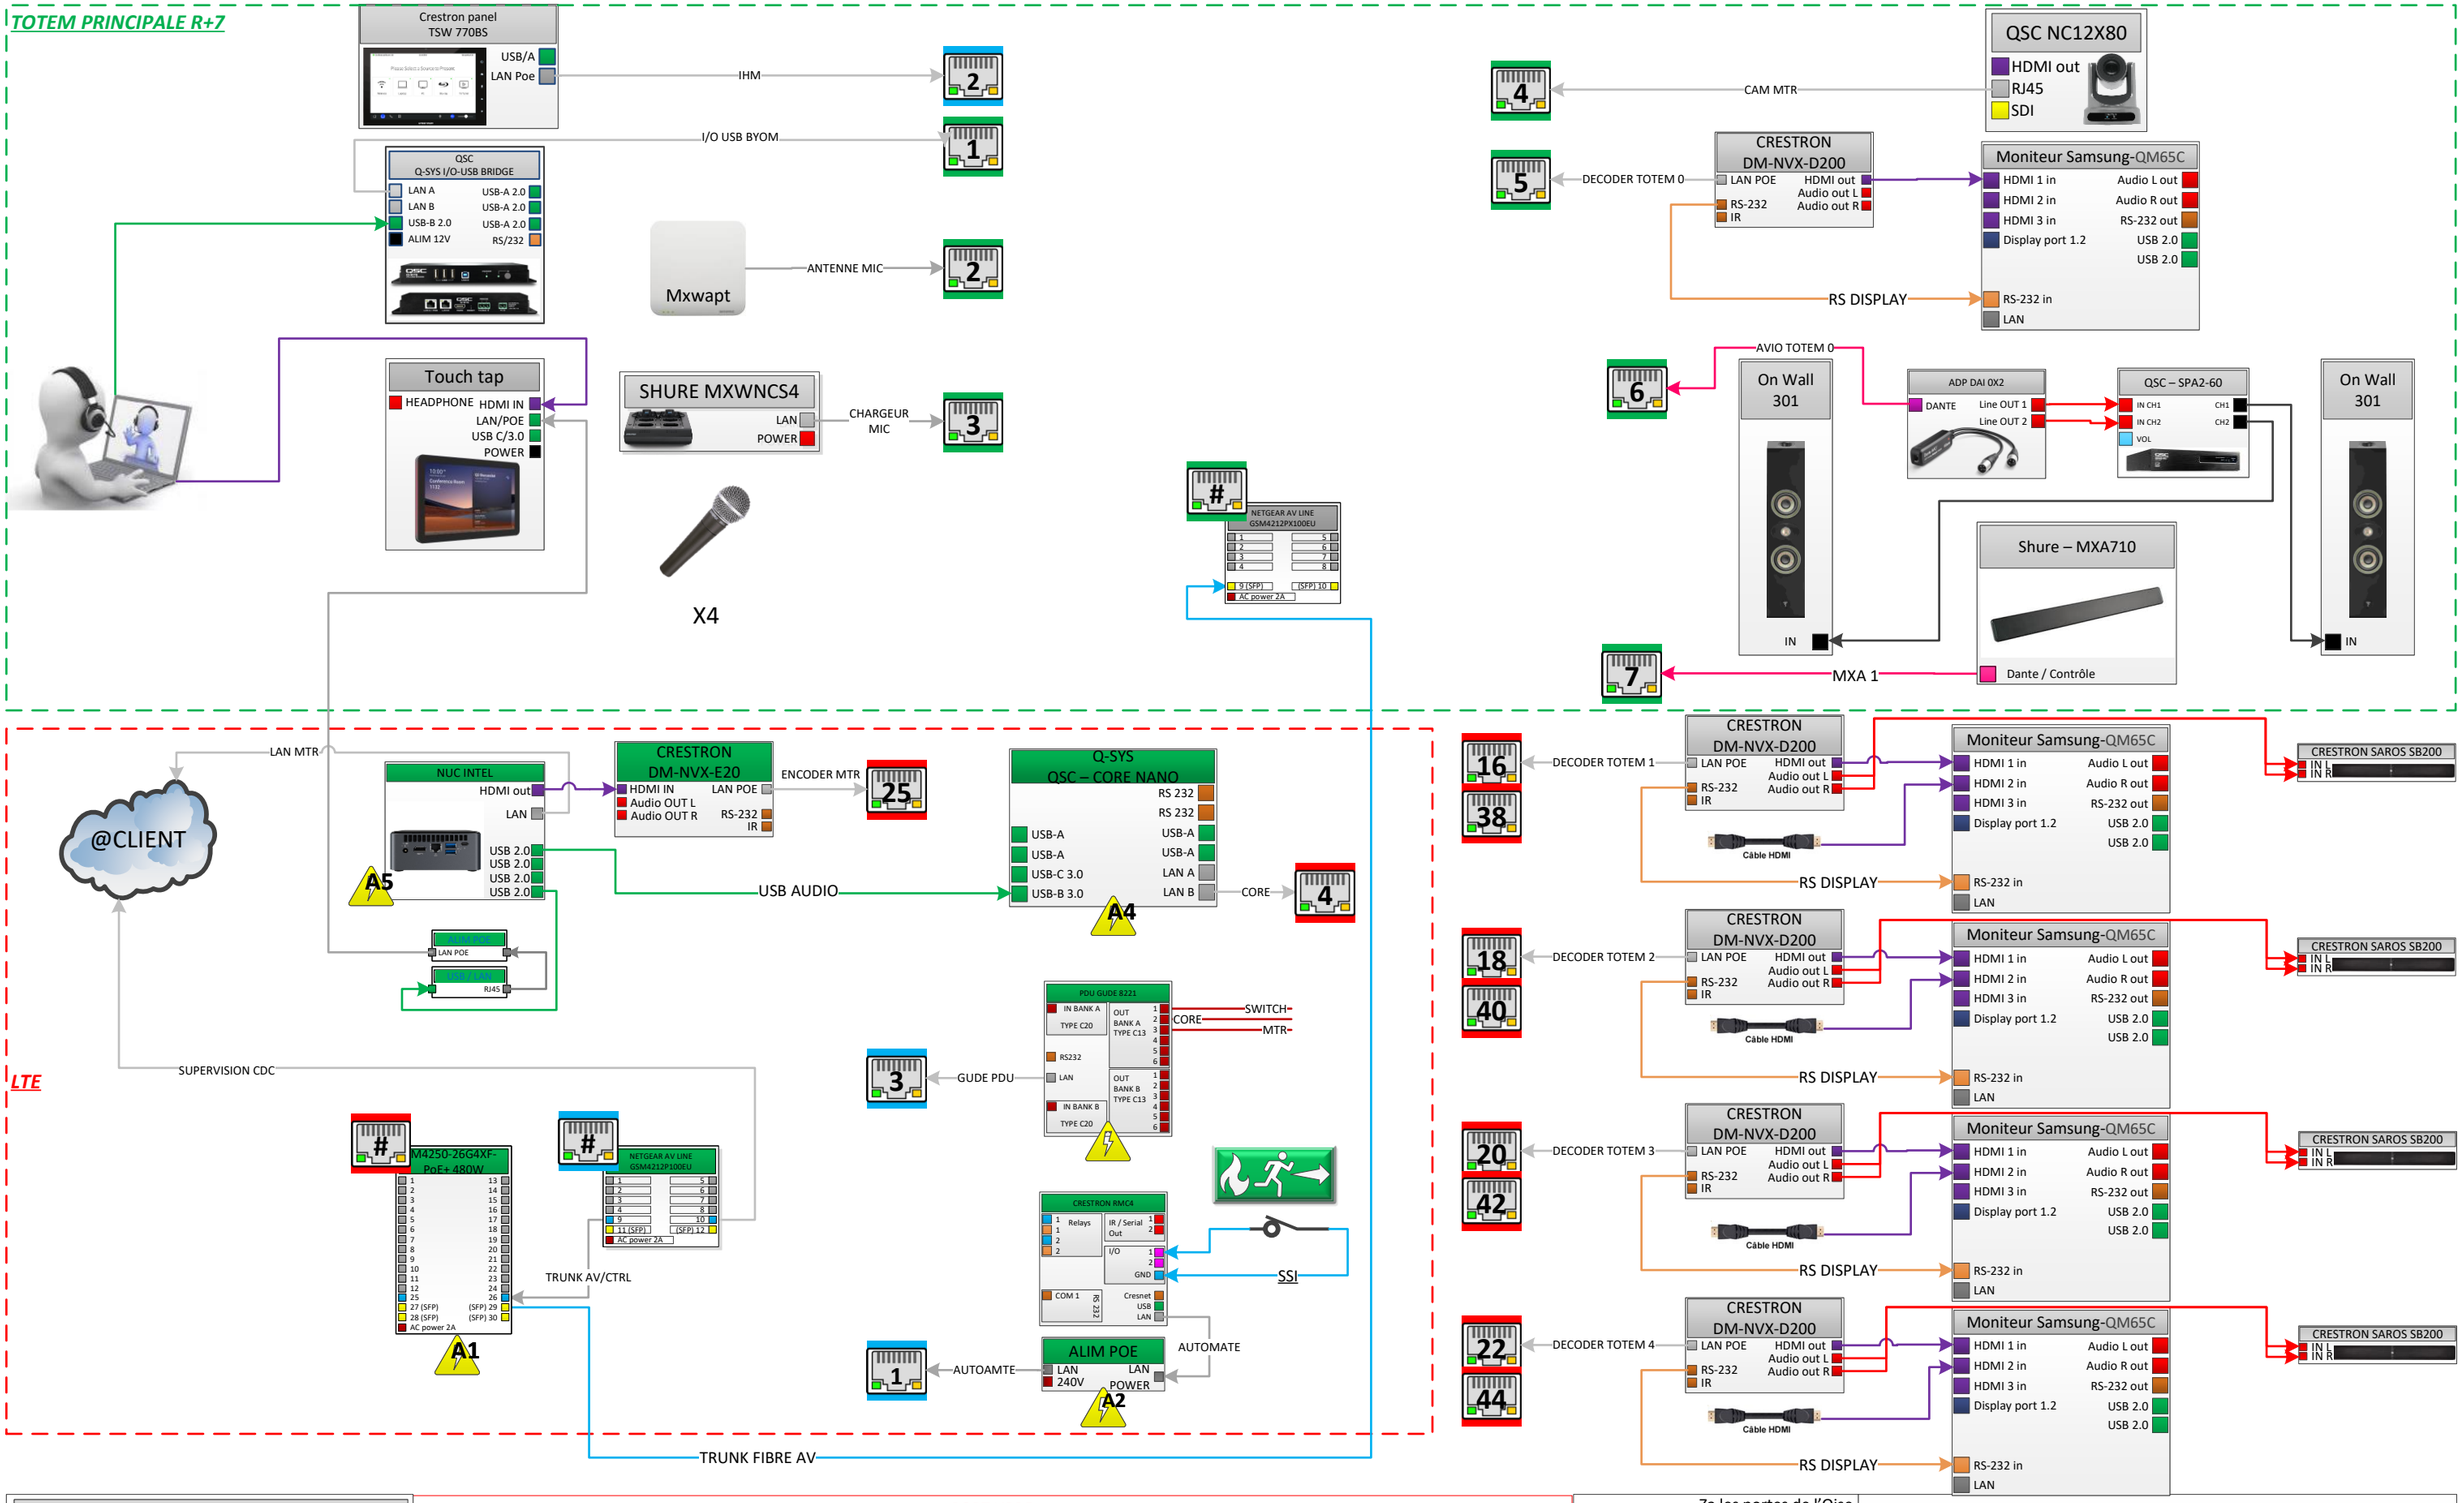

LEGENDE	
HDMI	DVI
Audio	VGA
Speakers	HD SDI
USB	Display port
RS232	AC 240V
RJ45 cat6	DC OUT
Audio Dante (RJ45 Cat6)	PDU
Autres contrôles	

MUR
BAIE AV
TABLE

PORT LIBRE

1 5 7 9 11 23 25
3 6 8 10 12 14 24
9
4 5 7
6 8

VIDEOSONIC
Image, Son & Technique
Za les portes de l'Oise
Batiment B2 – rue Henri Becquerel
60230 CHAMBLY
Tel : 01 75 01 60 40
Fax : 01 75 01 60 41
t.fourmentraux@videosonic.fr
FOURMENTRAUX Thierry

18/06/2025

Caisse des dépôts et consignations

ANGERS CDC R+7 ESPACE CRÉATIVITÉ

DIMENSION

SYNOPTIQUE AVC

RÉV 1

ECHELLE 1:1

FEUILLE 1 / 5

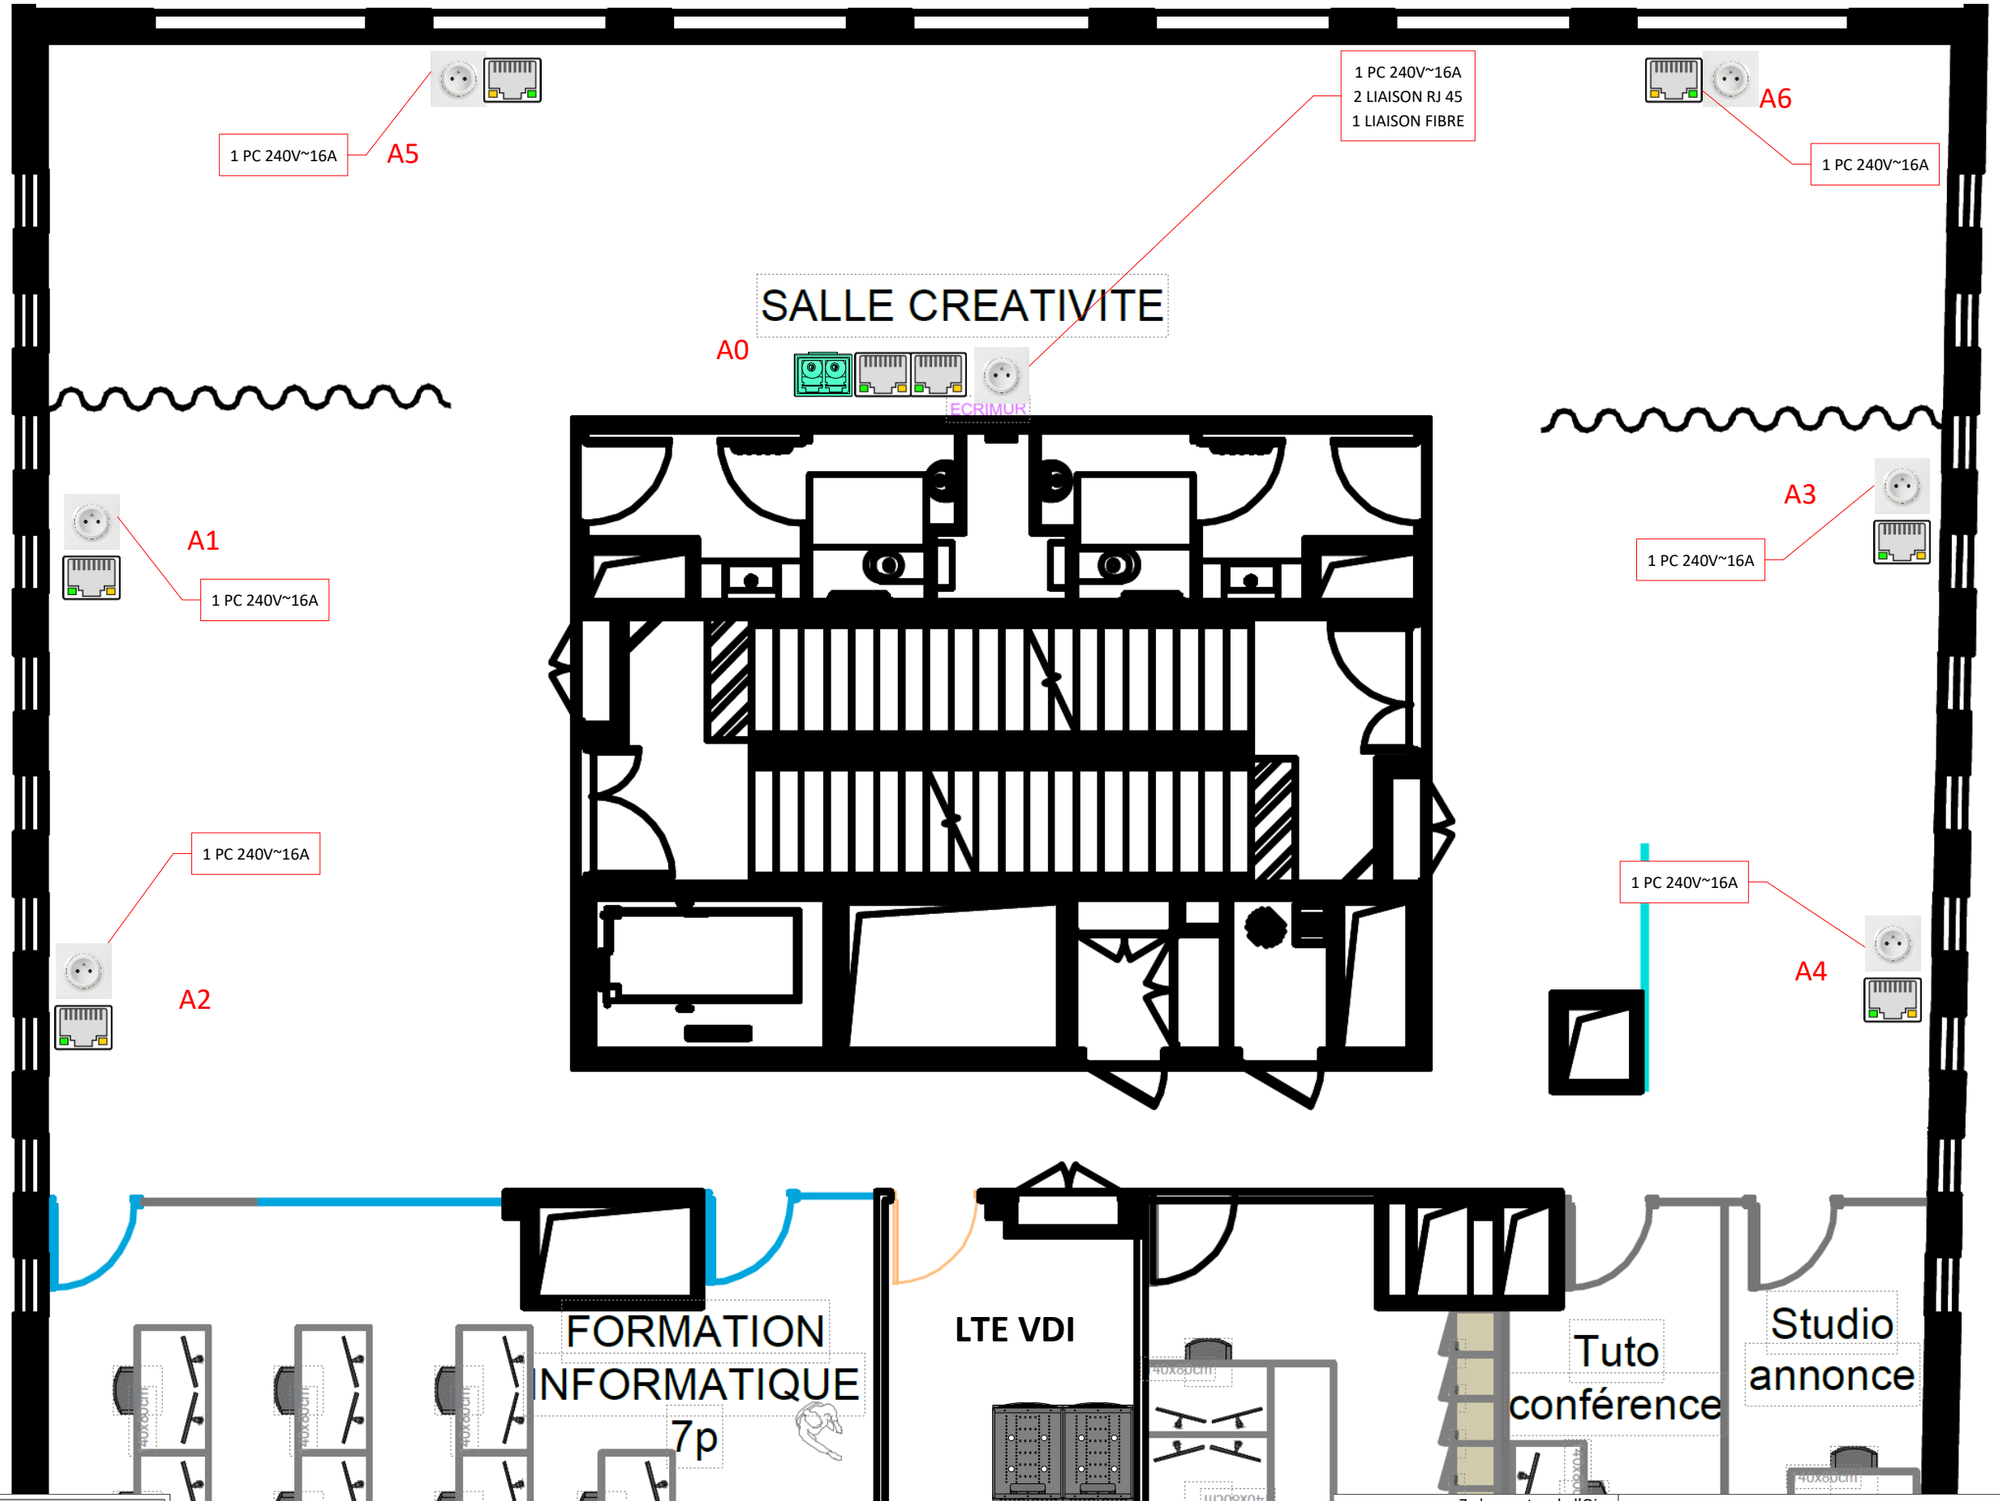

LEGENDE	
HDMI	DVI
Audio	VGA
Speakers	HD SDI
USB	Display port
RS232	AC 240V
RJ45 cat6	DC OUT
Audio Dante (RJ45 Cat6)	PDU
Autres contrôles	

MUR
BAIE AV
TABLE

VIDEOSONIC
Image, Son & Technique
Za les portes de l'Oise
Batîment B2 – rue Henri Becquerel
60230 CHAMBLY
Tel : 01 75 01 60 40
Fax : 01 75 01 60 41
t.fourmentraux@videosonic.fr
FOURMENTRAUX Thierry

18/06/2025

Caisse des dépôts et consignations

ANGERS CDC R+7 ESPACE CRÉATIVITÉ

DIMENSION		PLAN	RÉV
			1
ECHELLE	1:66,6667	FEUILLE	2 / 5

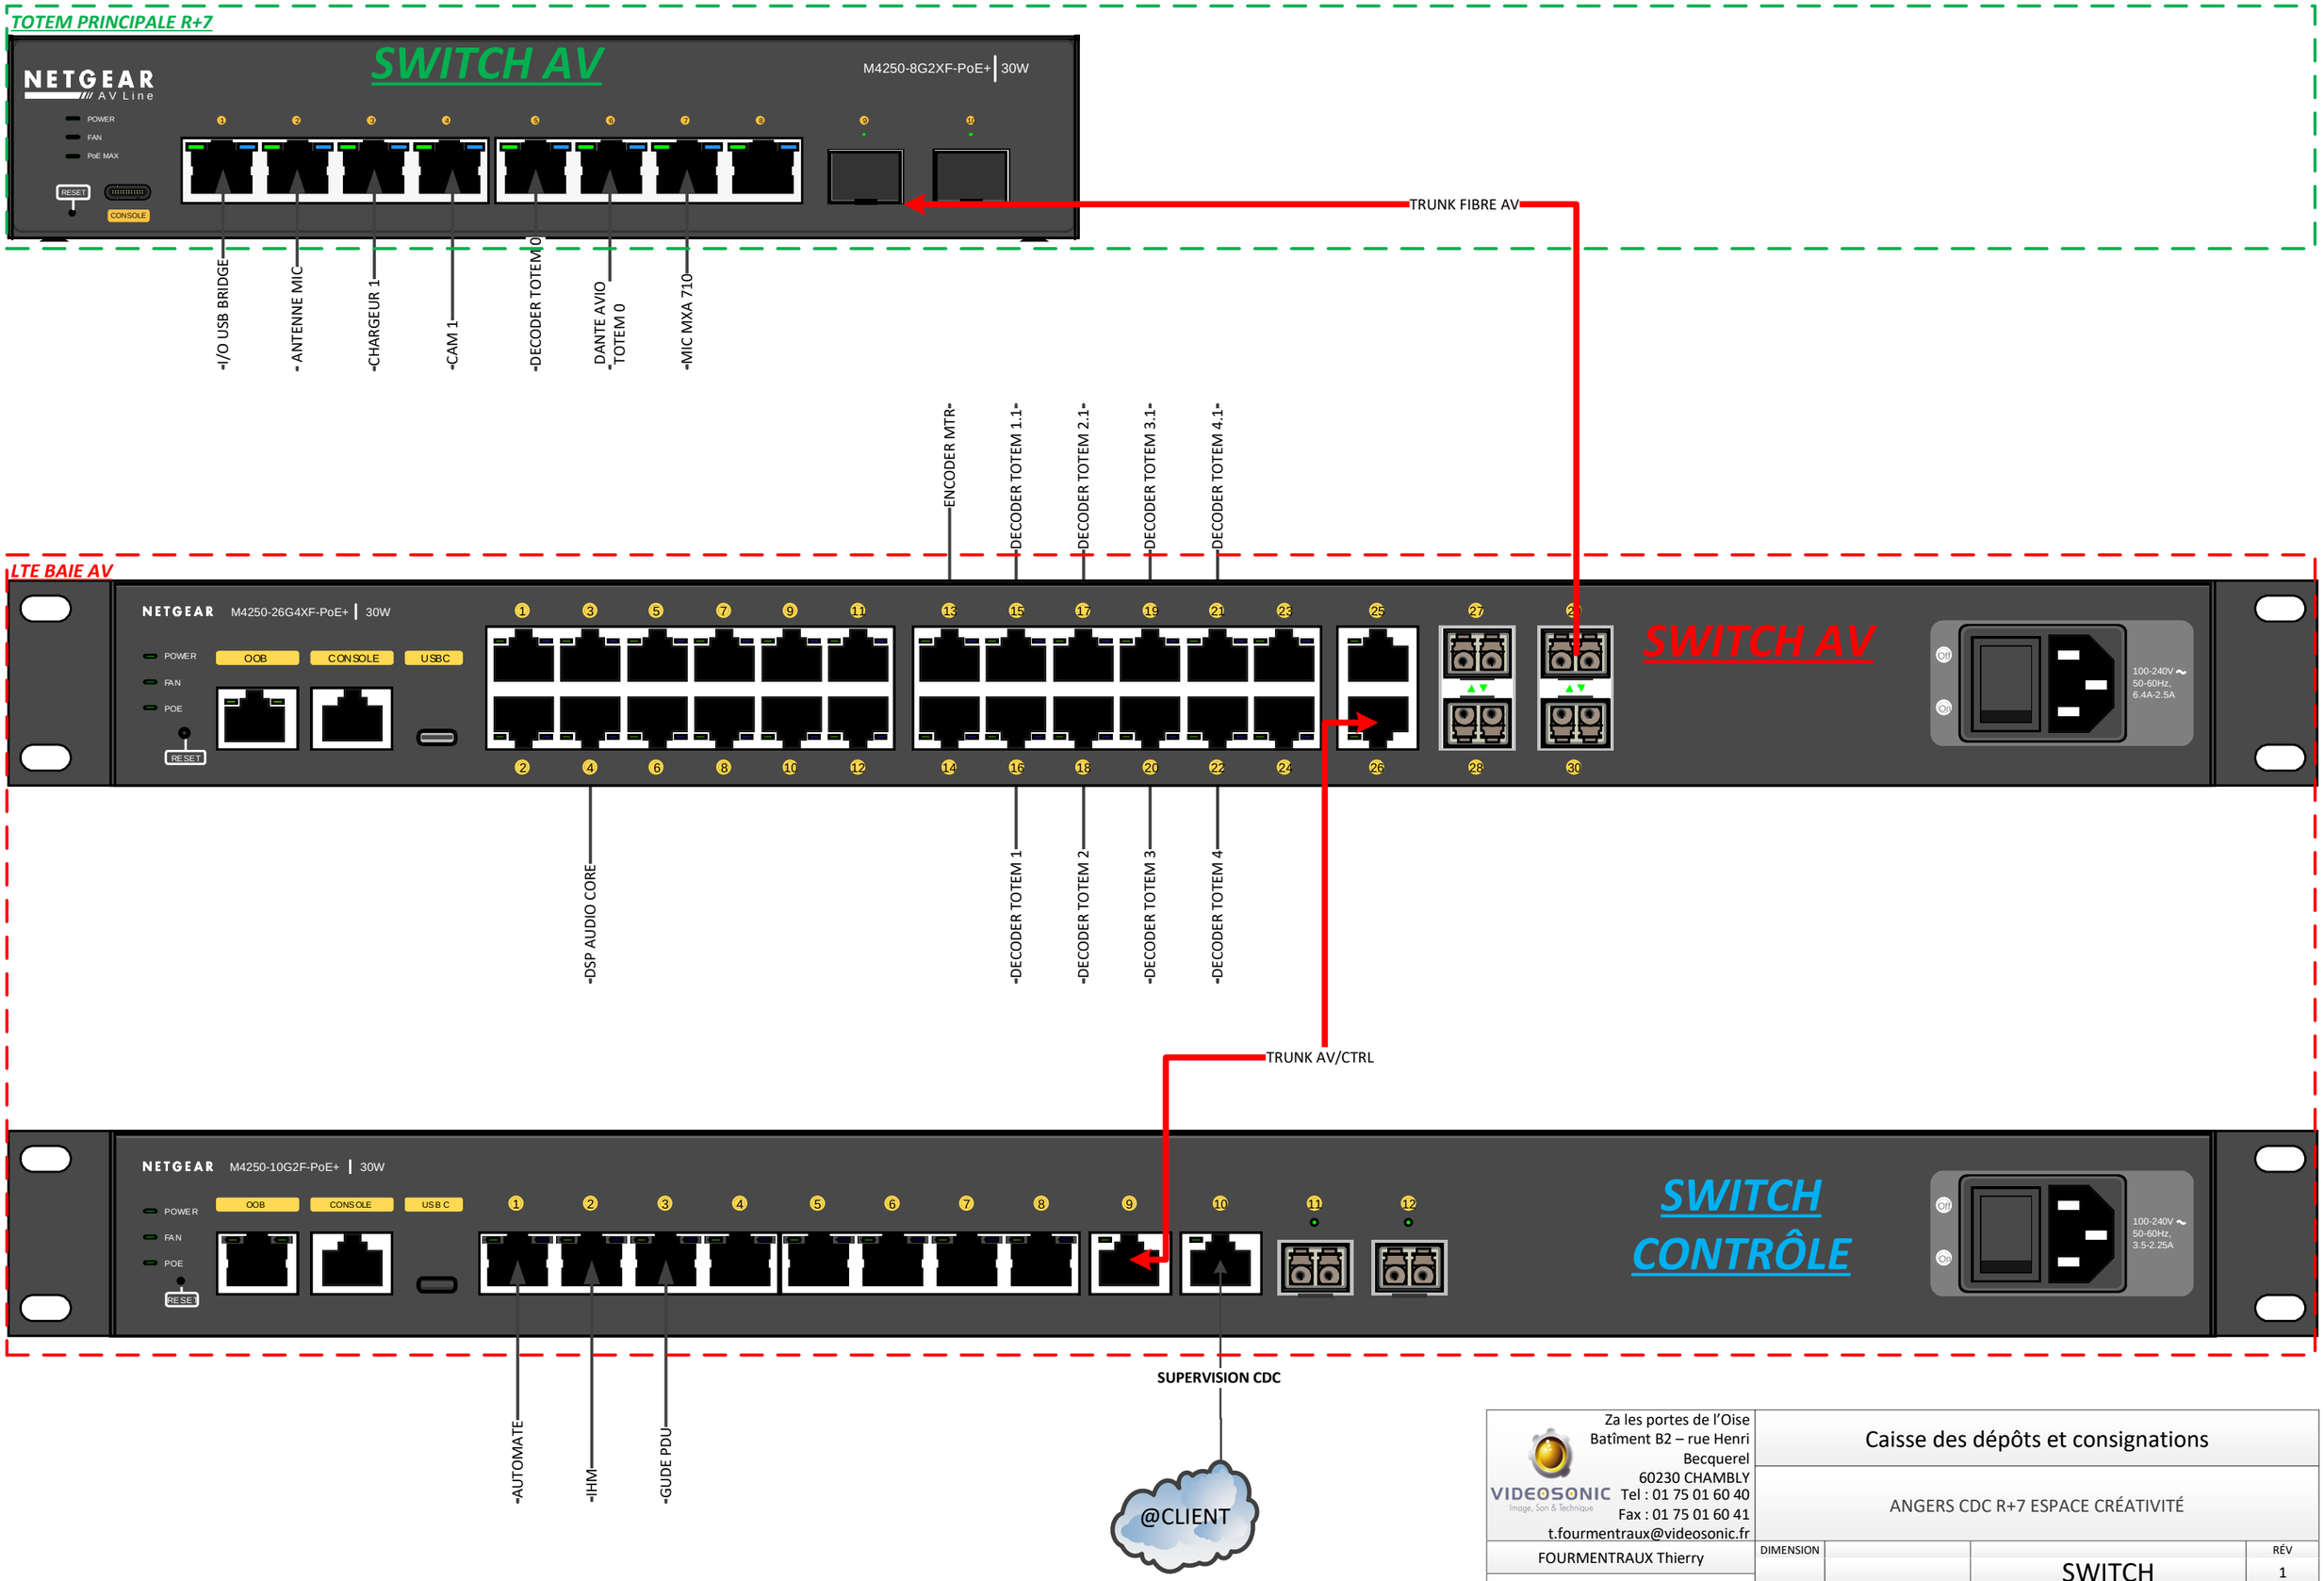

VIDEOSONIC Image, Son & Technique Za les portes de l'Oise Batîment B2 – rue Henri Becquerel 60230 CHAMBLY Tel : 01 75 01 60 40 Fax : 01 75 01 60 41 t.fourmentraux@videosonic.fr	Caisse des dépôts et consignations		
	ANGERS CDC R+7 ESPACE CRÉATIVITÉ		
FOURMENTRAUX Thierry	DIMENSION	SWITCH	RÉV 1
18/06/2025	ECHELLE 1:1		FEUILLE 3 / 5

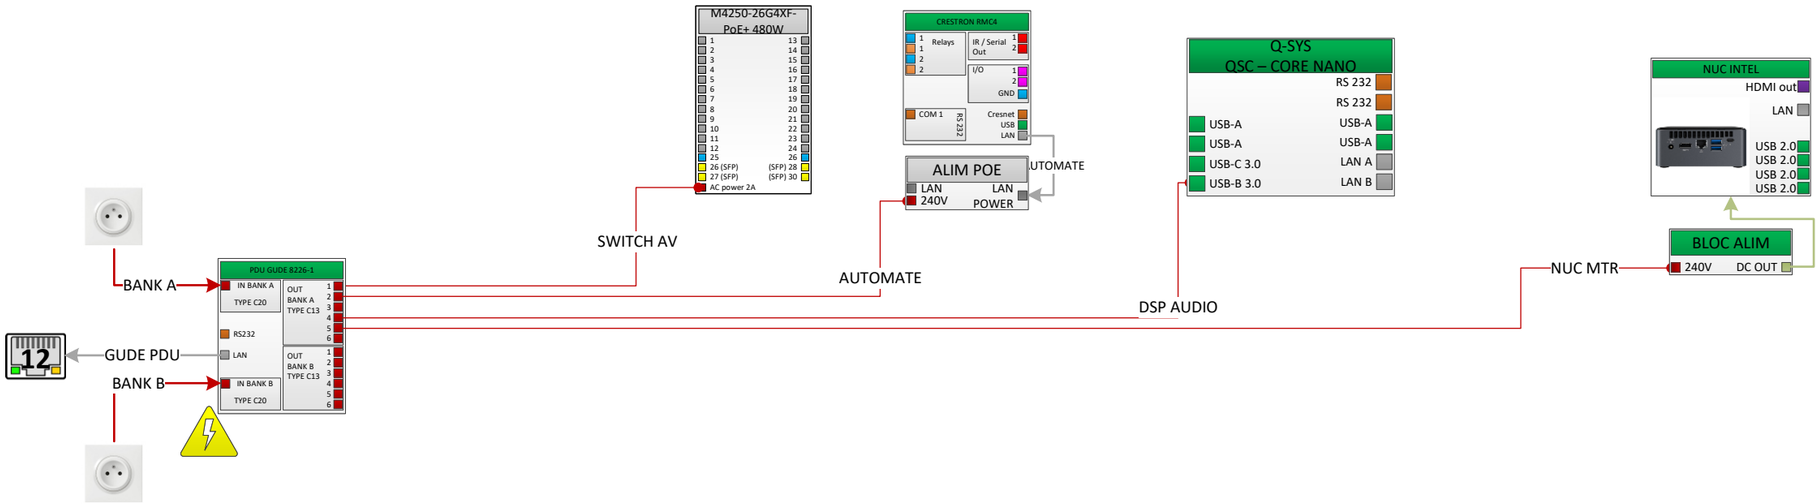

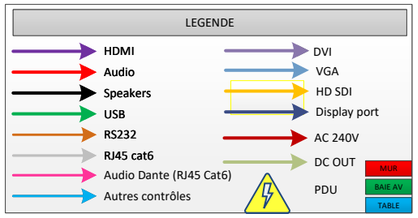

VIDEOSONIC
Image, Son & Technique
Za les portes de l'Oise
Batîment B2 – rue Henri Becquerel
60230 CHAMBLY
Tel : 01 75 01 60 40
Fax : 01 75 01 60 41
t.fourmentraux@videosonic.fr

FOURMENTRAUX Thierry

18/06/2025

Caisse des dépôts et consignations

ANGERS CDC R+7 ESPACE CRÉATIVITÉ

DIMENSION		SYNOPTIQUE PDU	RÉV
			1
ECHELLE 1:1		FEUILLE 4 / 5	

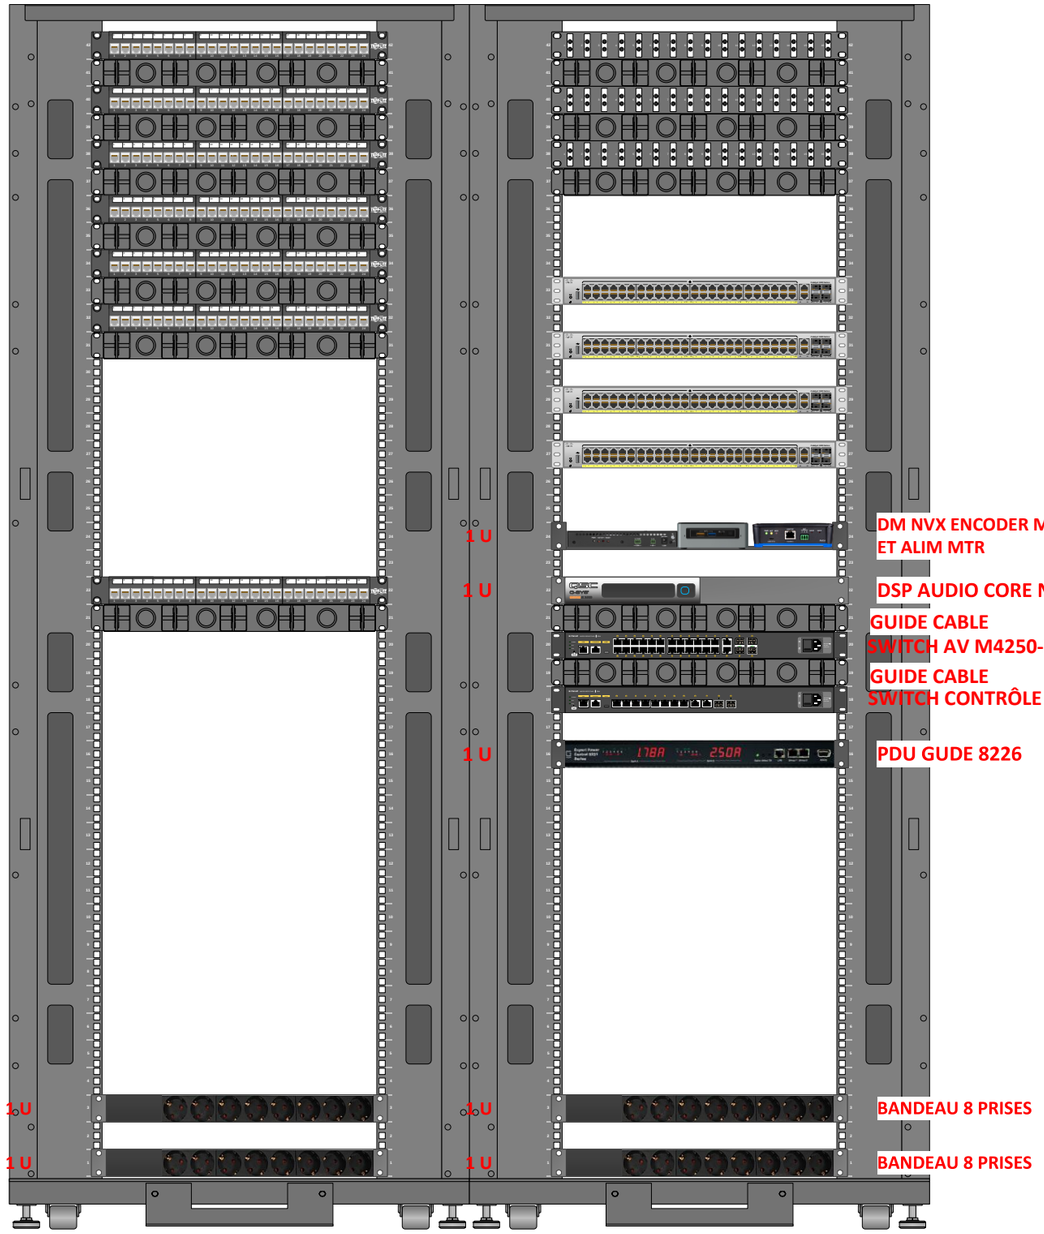

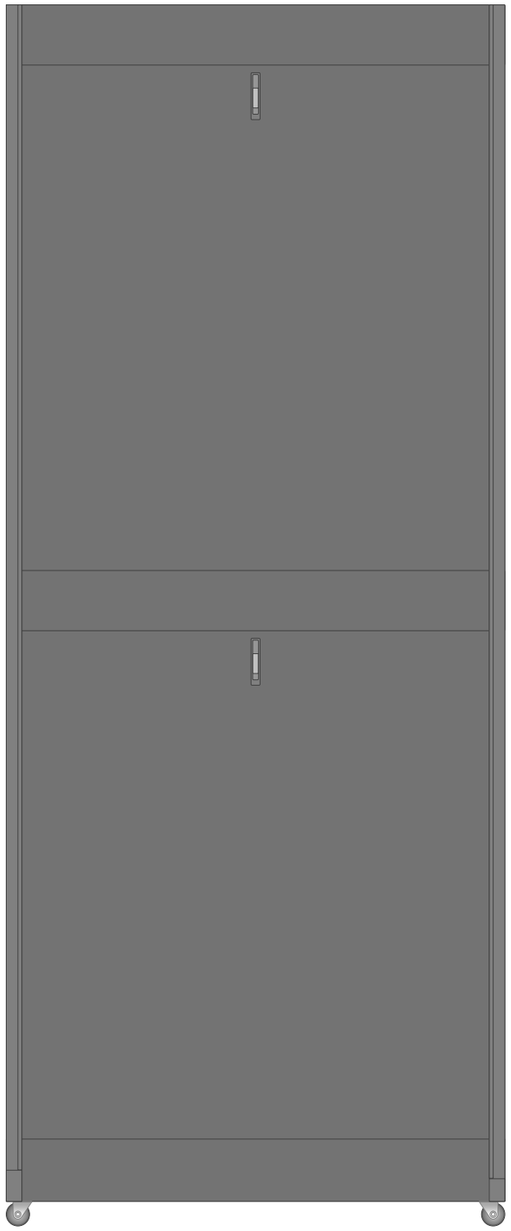

VIDEOSONIC
Image, Son & Technique
Za les portes de l'Oise
Batîment B2 – rue Henri Becquerel
60230 CHAMBLY
Tel : 01 75 01 60 40
Fax : 01 75 01 60 41
t.fourmentraux@videosonic.fr
FOURMENTRAUX Thierry

18/06/2025

Caisse des dépôts et consignations

ANGERS CDC R+7 ESPACE CRÉATIVITÉ

DIMENSION			RÉV
A3		PLAN DE BAIE	1
ECHELLE 1:10		FEUILLE 5 / 5	