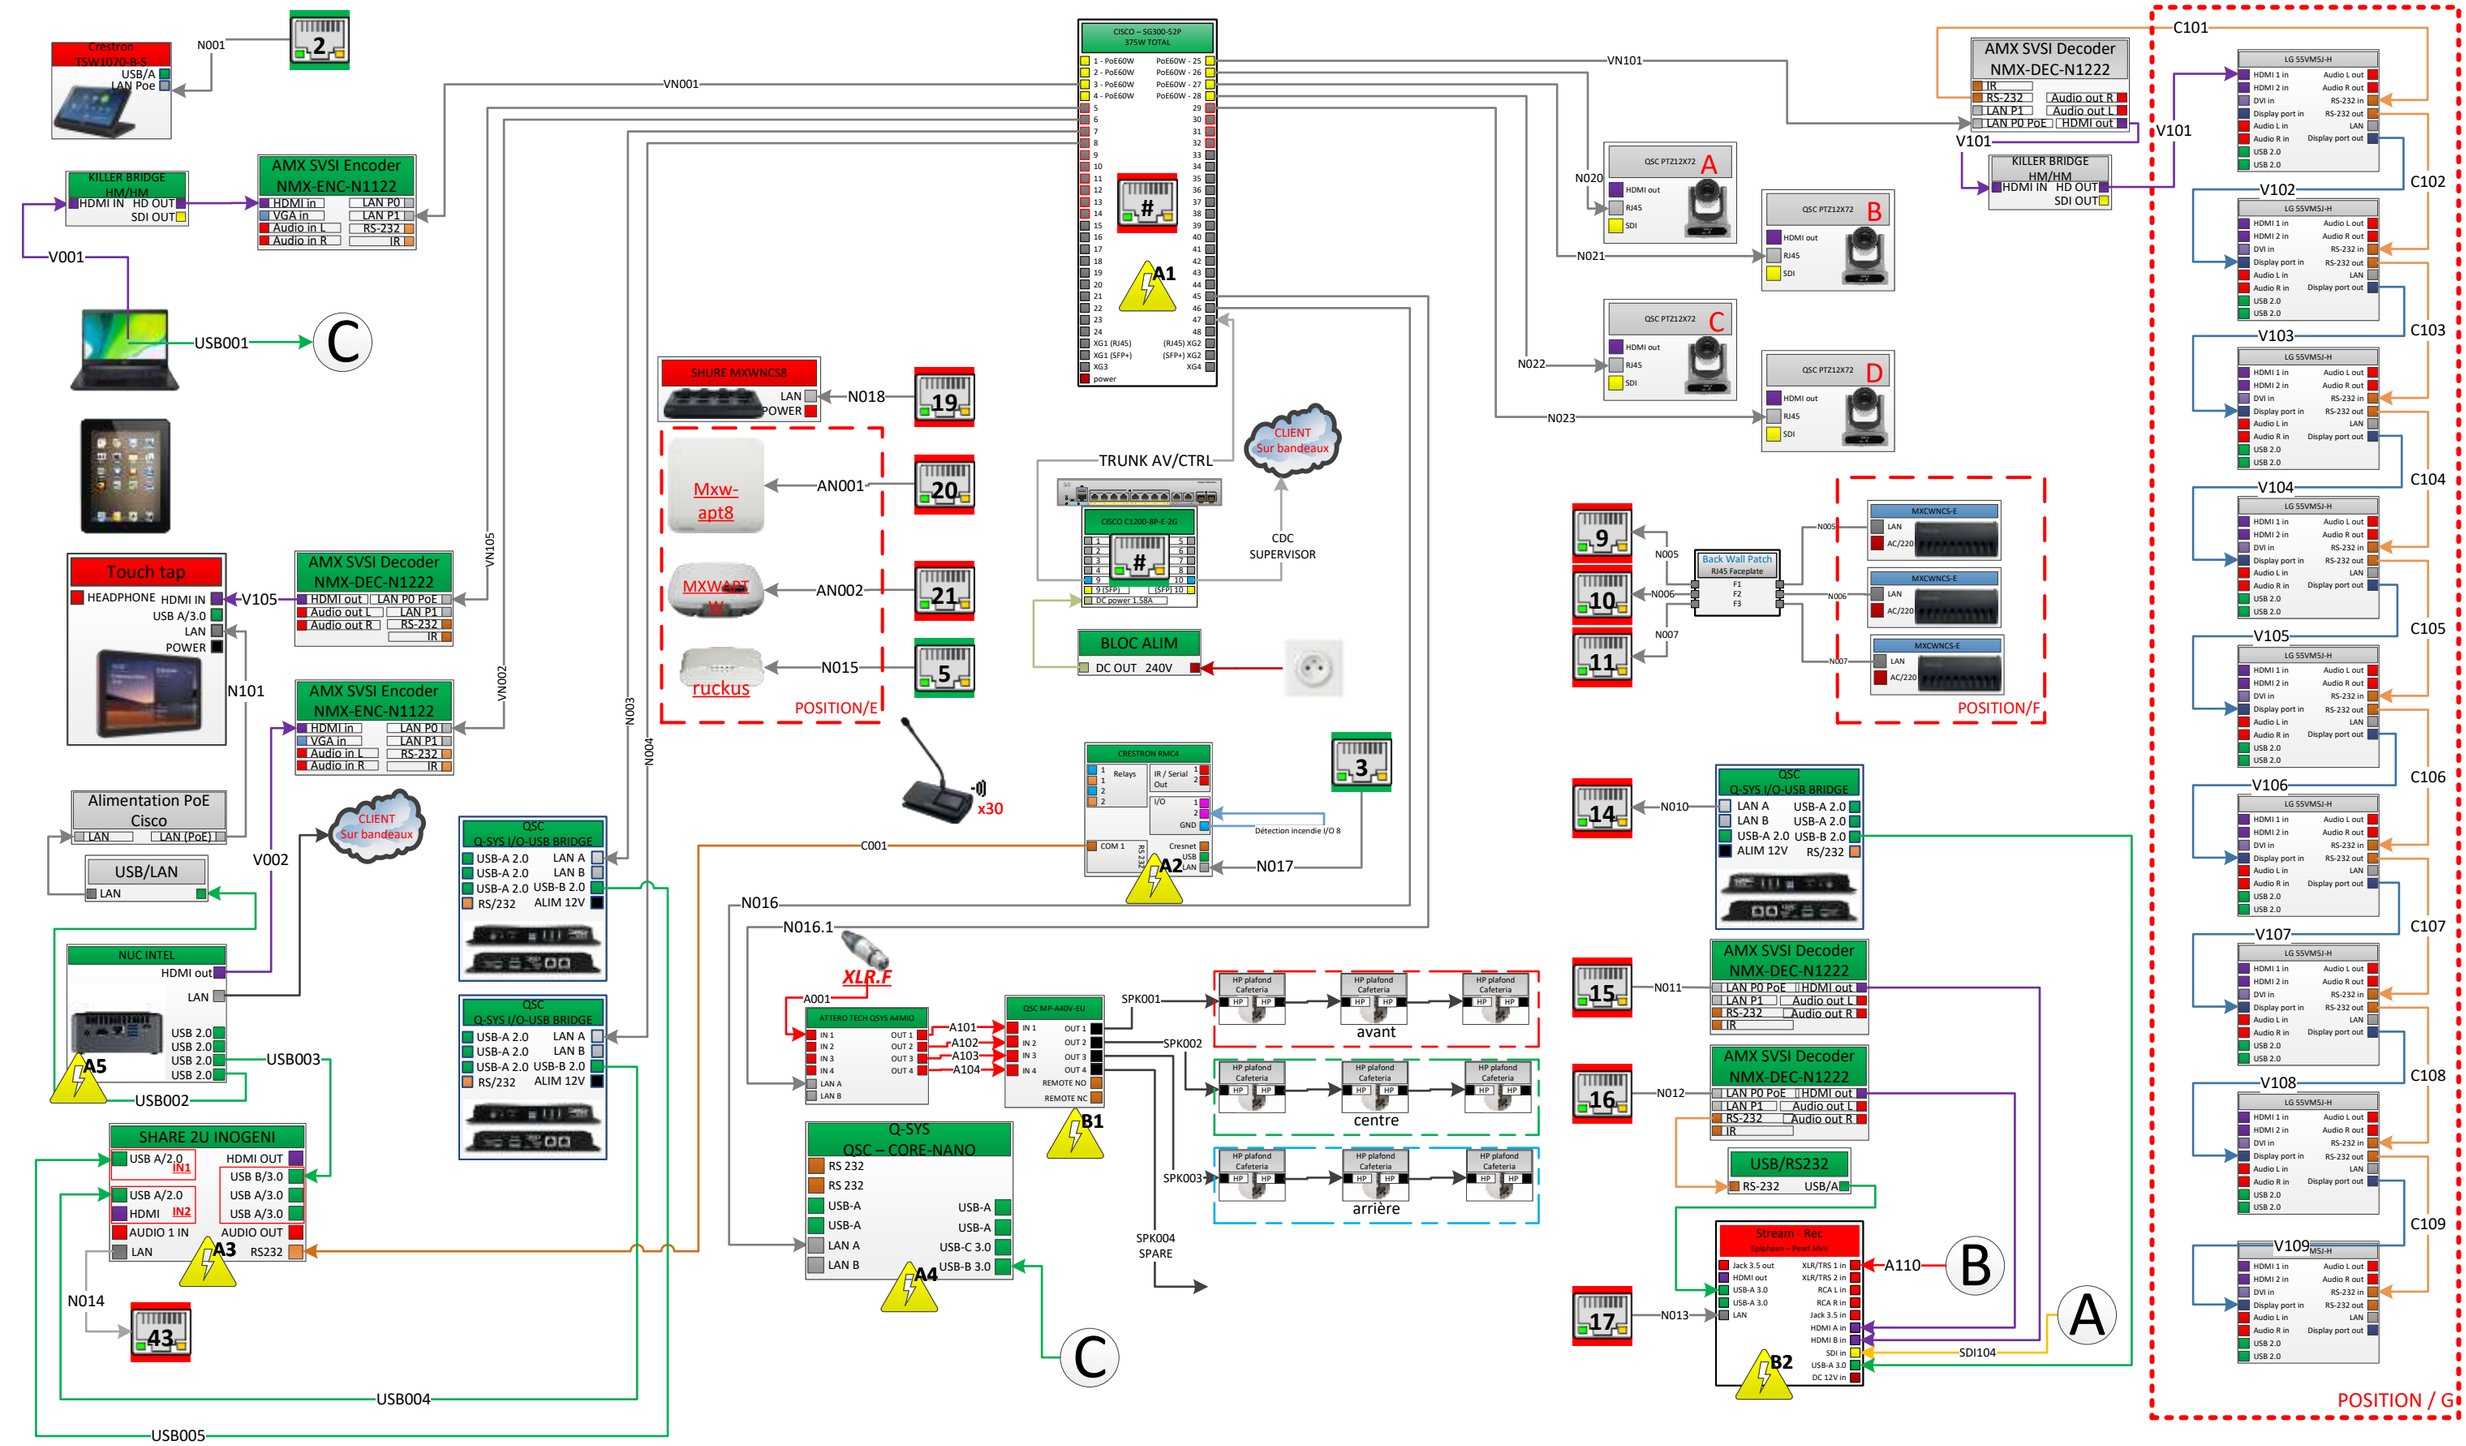

VIDEOSONIC
image, Son & Technique

Za les portes de l'Oise
Batîment B2 – rue Henri Becquerel
60230 CHAMBLY
Tel : 01 75 01 60 40
Fax : 01 75 01 60 41
t.fourmentraux@videosonic.fr

Fourmentraux Thierry

30/01/2025

Caisse des dépôts et consignation Austerlitz

Salle Annie Kovacs

DIMENSION		synoptique générale	RÉV
ECHELLE	1:1	FEUILLE	1 / 4

21 U

SOCAMOUNT

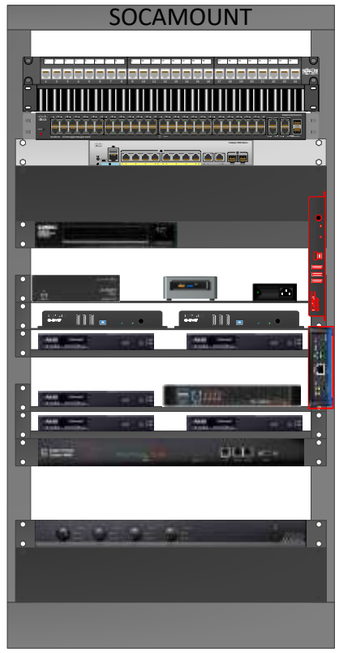

1 U	BALAIS PASSE CABLE SWITCH AV SWITCH CONTRÔLE
2 U	
1 U	DSP AUDIO CORE NANO
1 U	AXOM 4MIO + PC MTR + ALIM
1 U	QSC I/O BRIDGE USB INOGENI CAM 1 +2
1 U	SVSI DECODER STREAM 1 + 2
1 U	SVSI DECODER MTR TAP + SHARE 2U
1 U	SVSI ENCODER PC + ENCODER MTR
1 U	PDU GUDE 8226
1 U	AMPLIAUDAC EPA 254
2 U	

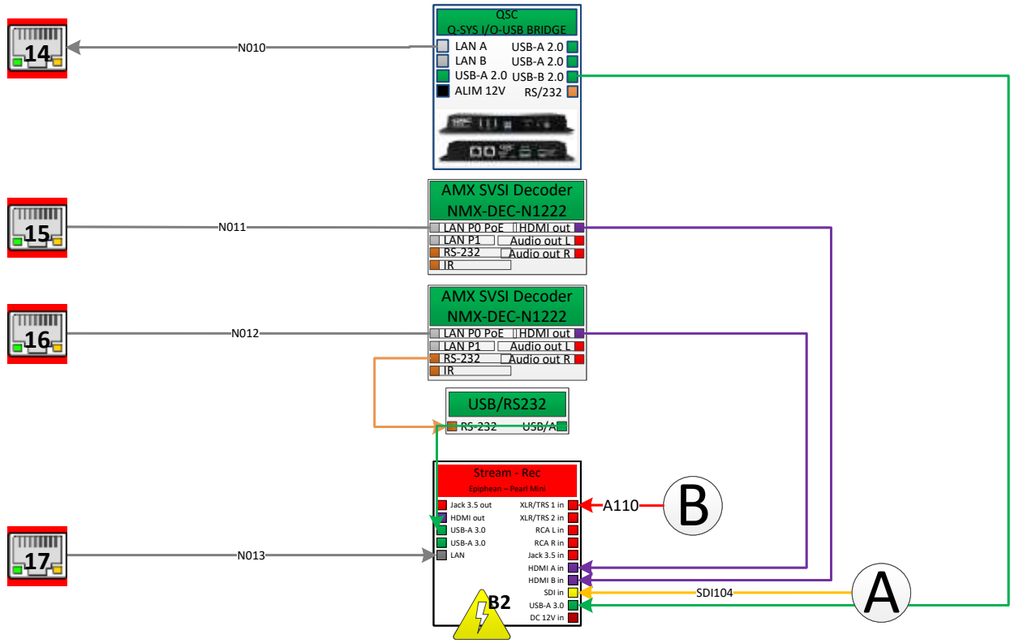

LEGENDE

- HDMI
- Audio
- Speakers
- USB
- RS232
- RJ45 cat6
- Audio Dante (RJ45 Cat6)
- Autres contrôles
- ALIMENTATION 240V~
- VGA
- DVI
- HD SDI
- Display port

BAIE

RÉGIE CDC

ÉTAGÈRE BAIE

VIDEOSONIC
Image, Son & Technique

Za les portes de l'Oise
Batîment B2 – rue Henri Becquerel
60230 CHAMBLY

Tel : 01 75 01 60 40
Fax : 01 75 01 60 41
t.fourmentraux@videosonic.fr

Fourmentraux Thierry

30/01/2025

Caisse des dépôts et consignation
Austerlitz

Salle Annie Kovacs

DIMENSION			RÉV
		LOCAL REGIE BAIE	1
ECHELLE	1:10	FEUILLE	2 / 4

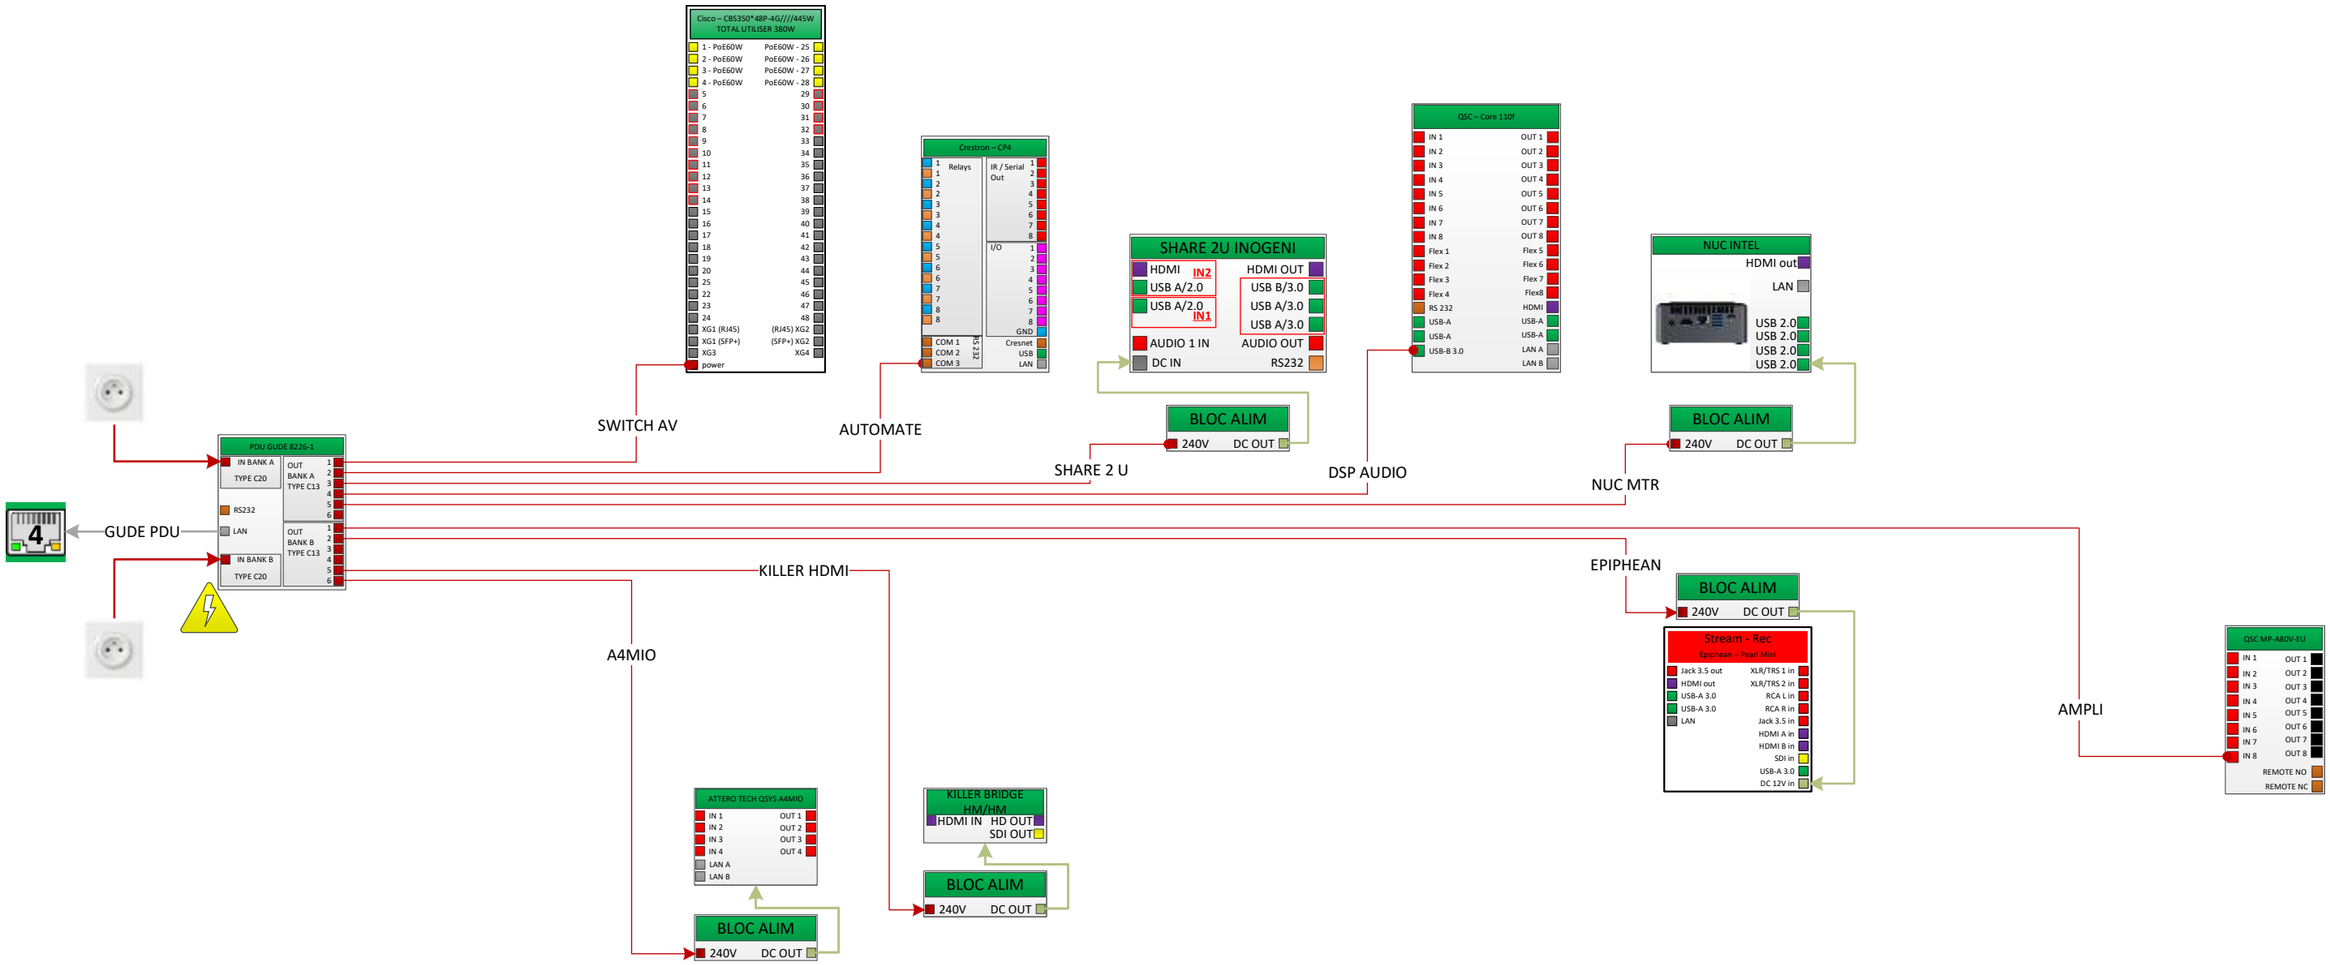

LEGENDE

- HDMI
- Audio
- Speakers
- USB
- RS232
- RJ45 cat6
- Audio Dante (RJ45 Cat6)
- Autres contrôles
- ALIMENTATION 240V~
- VGA
- DVI
- HD SDI
- Display port

BAIE
RÉGIE CDC
ÉTAGÈRE BAIE

VIDEOSONIC
Image, Son & Technique

Za les portes de l'Oise
Batîment B2 – rue Henri Becquerel
60230 CHAMBLY
Tel : 01 75 01 60 40
Fax : 01 75 01 60 41
t.fourmentraux@videosonic.fr

Fourmentraux Thierry

30/01/2025

Caisse des dépôts et consignation
Austerlitz

Salle Annie Kovacs

DIMENSION			RÉV
		PDU GUDE	1
ECHELLE 1:1			FEUILLE 3 / 4

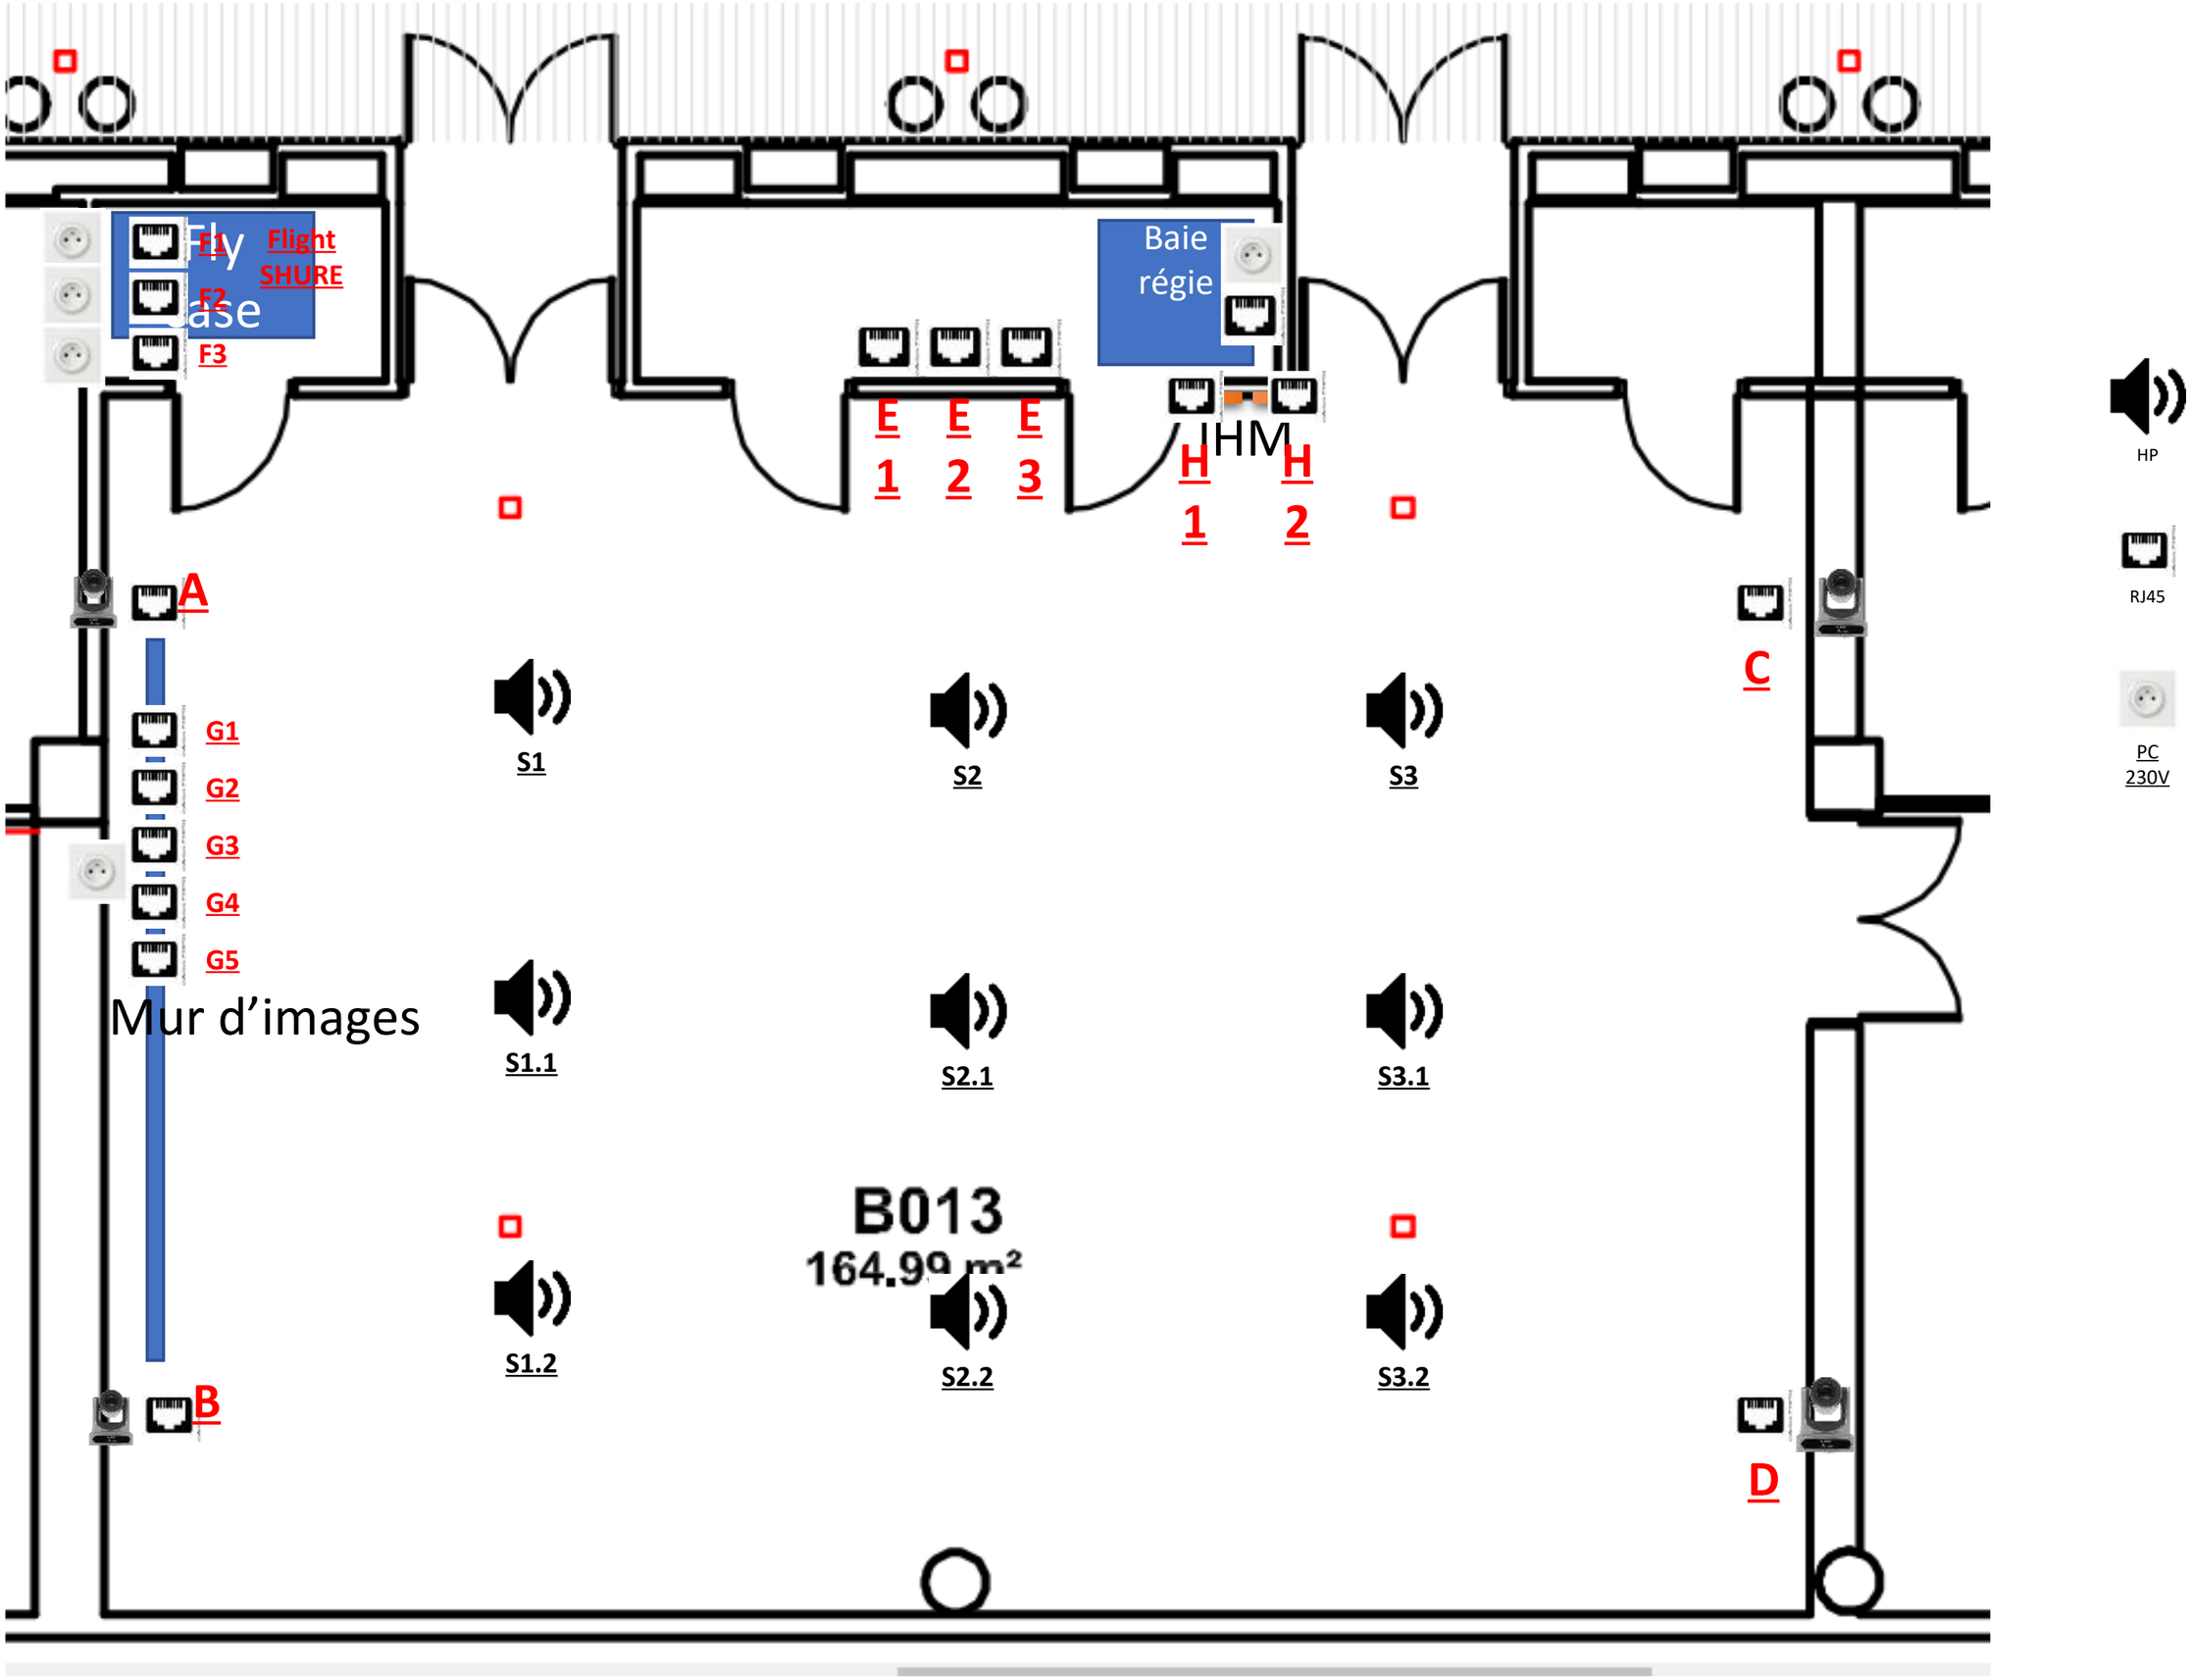
Fly Case
F1
F2
F3
Flight SHURE
Baie régie
E 1
E 2
E 3
JHM
H 1
H 2
HP
RJ45
PC 230V
A
B
C
D
G1
G2
G3
G4
G5
Mur d'images
S1
S2
S3
S1.1
S2.1
S3.1
S1.2
S2.2
S3.2
B013
164.99 m²