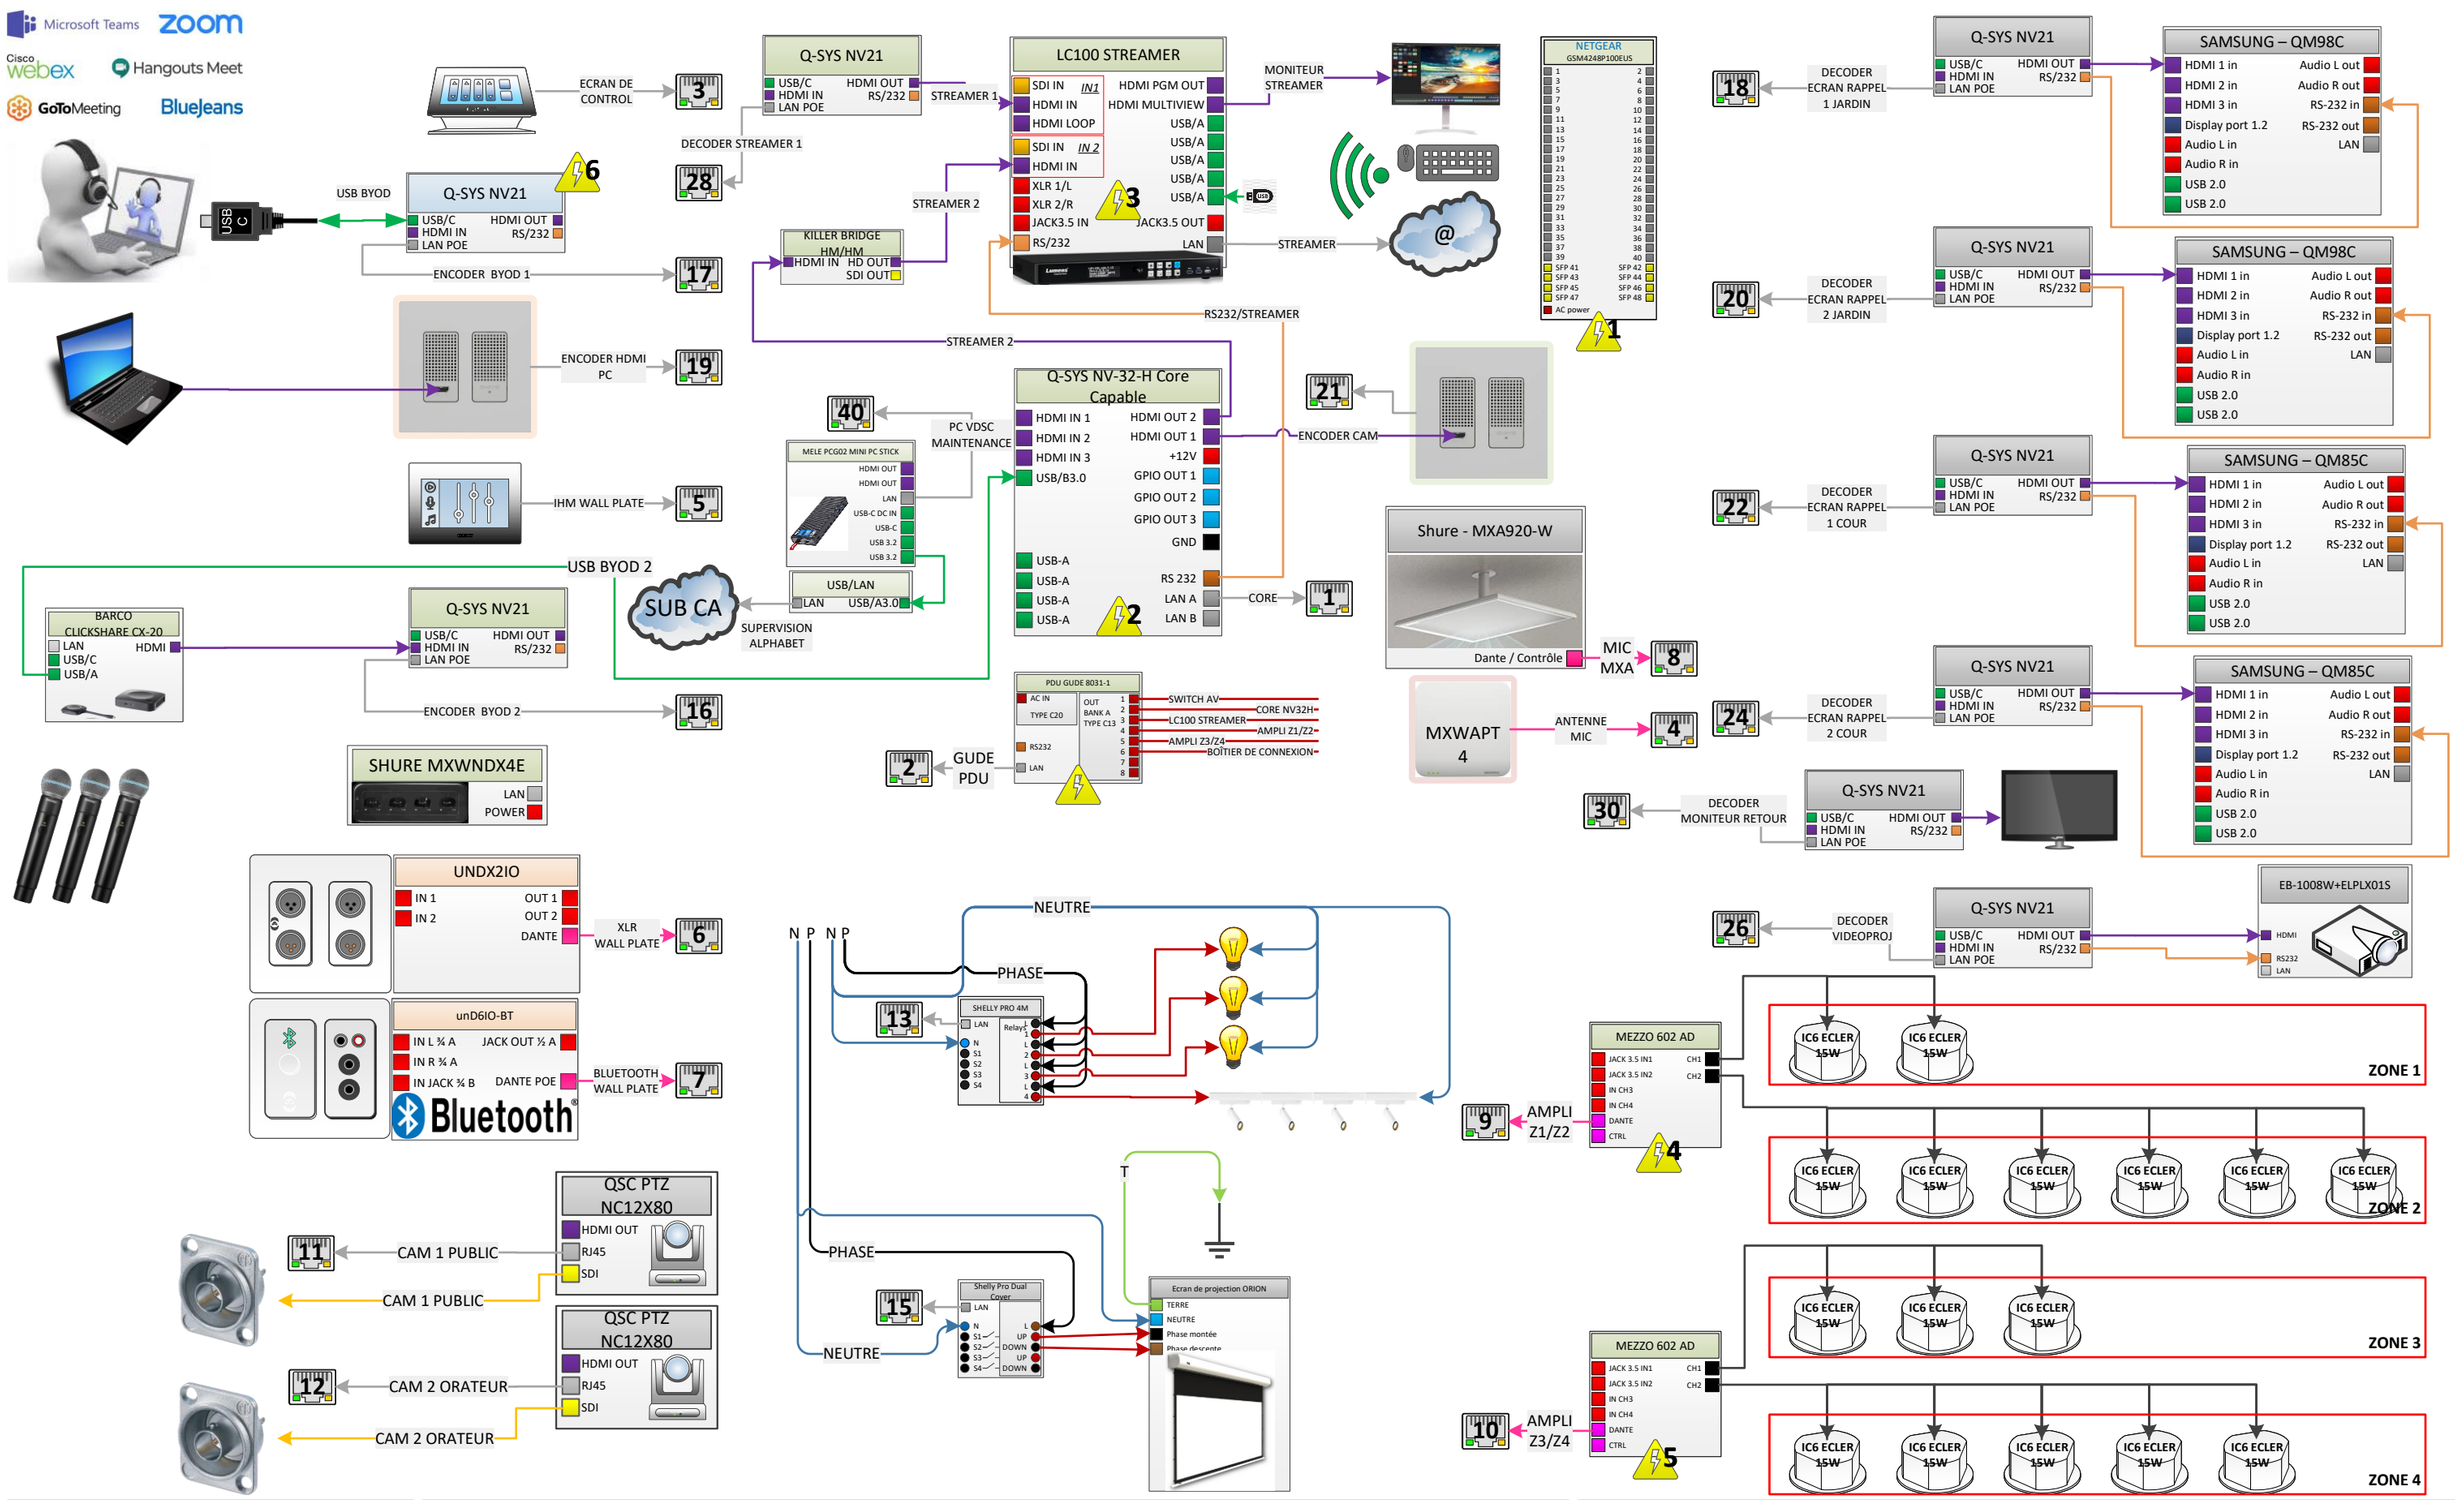

VIDEOSONIC
Image, Son & Technique
Za les portes de l'Oise
Batîment B2 – rue Henri Becquerel
60230 CHAMBLY
Tel : 01 75 01 60 40
Fax : 01 75 01 60 41
t.fourmentraux@videosonic.fr
FOURMENTRAUX Thierry

22/09/2025

Alphabet – Salle de Conference

2 allée des messageries, Bois-Colombes

DIMENSION			RÉV
A3		SYNOPTIQUE AVC	1
ECHELLE 1:1		FEUILLE	1 / 3

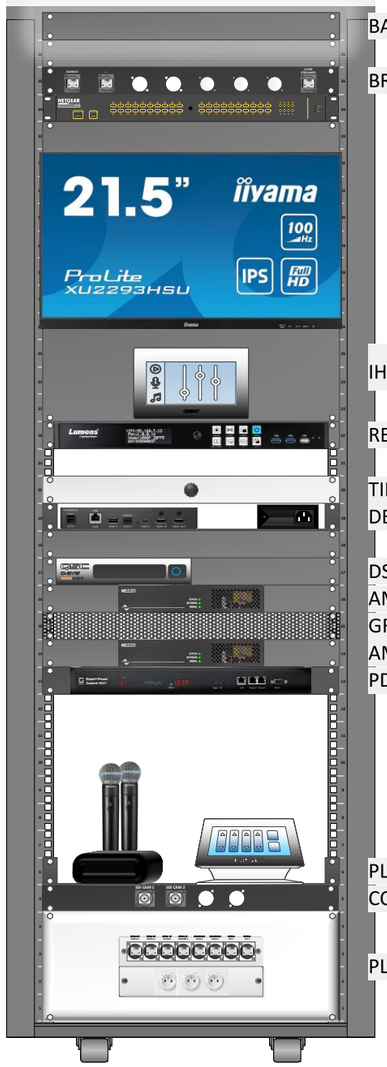

1 U	BANDEAUX D'ÉCLAIRAGE BAIE
1 U	
1 U	BRASSAGE SUB CA POUR STREAMER GSM4248P100EUS
2 U	
4 U	
4 U	IHM WALL PLATE
1 U	REC STREAMER
1 U	TIROIR CLAVIER/SOURIS
1 U	DECODER STREAMER 2 + ALIM
1 U	
1 U	DSP AUDIO CORE
1 U	AMPLIFICATEUR Z1/Z2
1 U	GRILLE 2U
1 U	AMPLIFICATEUR Z3/Z4
1 U	PDU GUDE 8031-1
1 U	PLATEAU POUR CHARGEUR MIC + ECRAN DE CONTROL
1 U	CONNEXION SDI CAM DIRECT
4 U	PLATINE DE CONNEXION

BAIE36EQU

Za les portes de l'Oise
Batîment B2 – rue Henri Becquerel
60230 CHAMBLY
Tel : 01 75 01 60 40
Fax : 01 75 01 60 41
t.fourmentraux@videosonic.fr
VIDEOSONIC Image, Son & Technique
FOURMENTRAUX Thierry

22/09/2025

Alphabet – Salle de Conference

2 allée des messageries, Bois-Colombes

DIMENSION	RÉV
A3	1

PLAN DE BAIE

ECHELLE 1:10 — FEUILLE 2 / 3

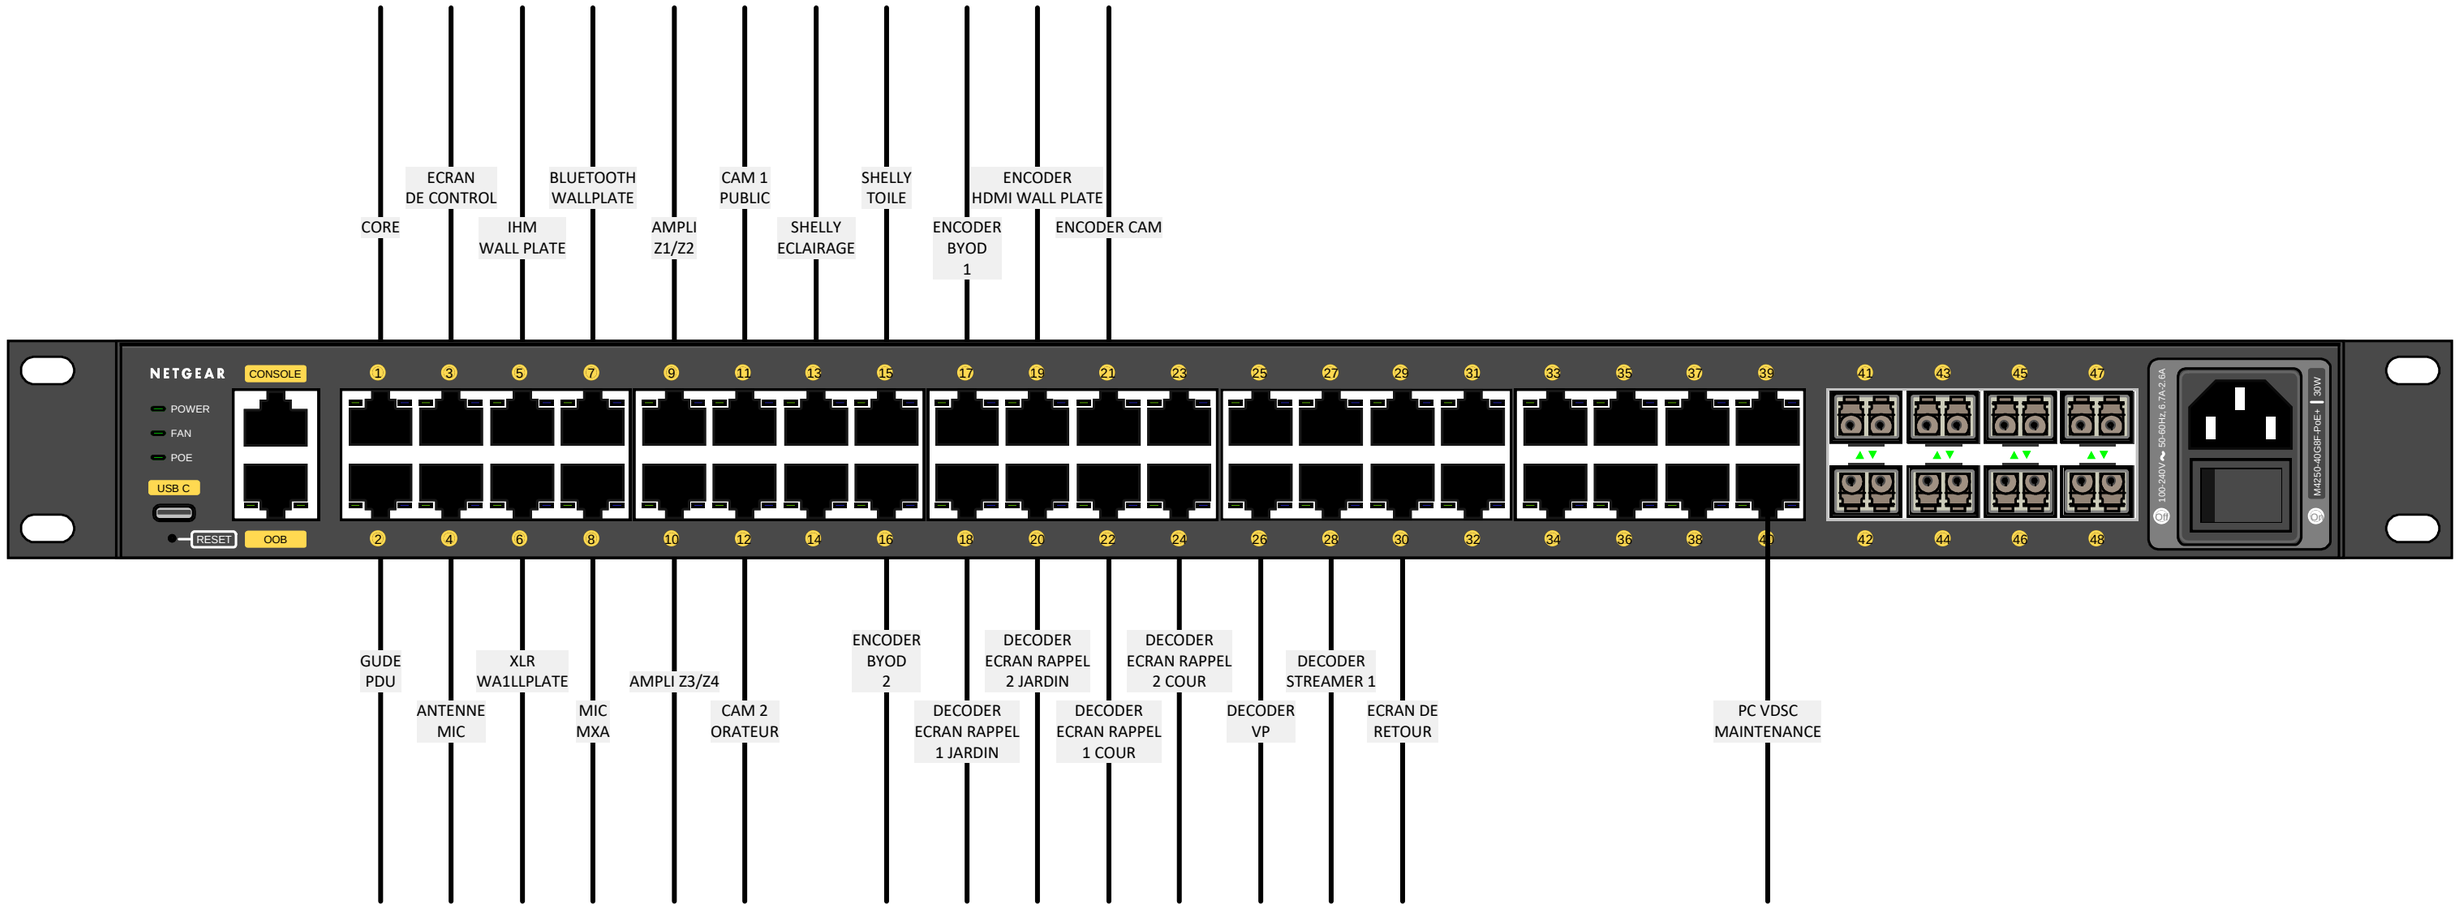

PORT LIBRE

VIDEOSONIC
Image, Son & Technique
Za les portes de l'Oise
Batîment B2 – rue Henri Becquerel
60230 CHAMBLY
Tel : 01 75 01 60 40
Fax : 01 75 01 60 41
t.fourmentraux@videosonic.fr

FOURMENTRAUX Thierry

22/09/2025

Alphabet – Salle de Conference

2 allée des messageries, Bois-Colombes

DIMENSION			RÉV
A3		SWITCH AV	1
ECHELLE 1:1			FEUILLE 3 / 3