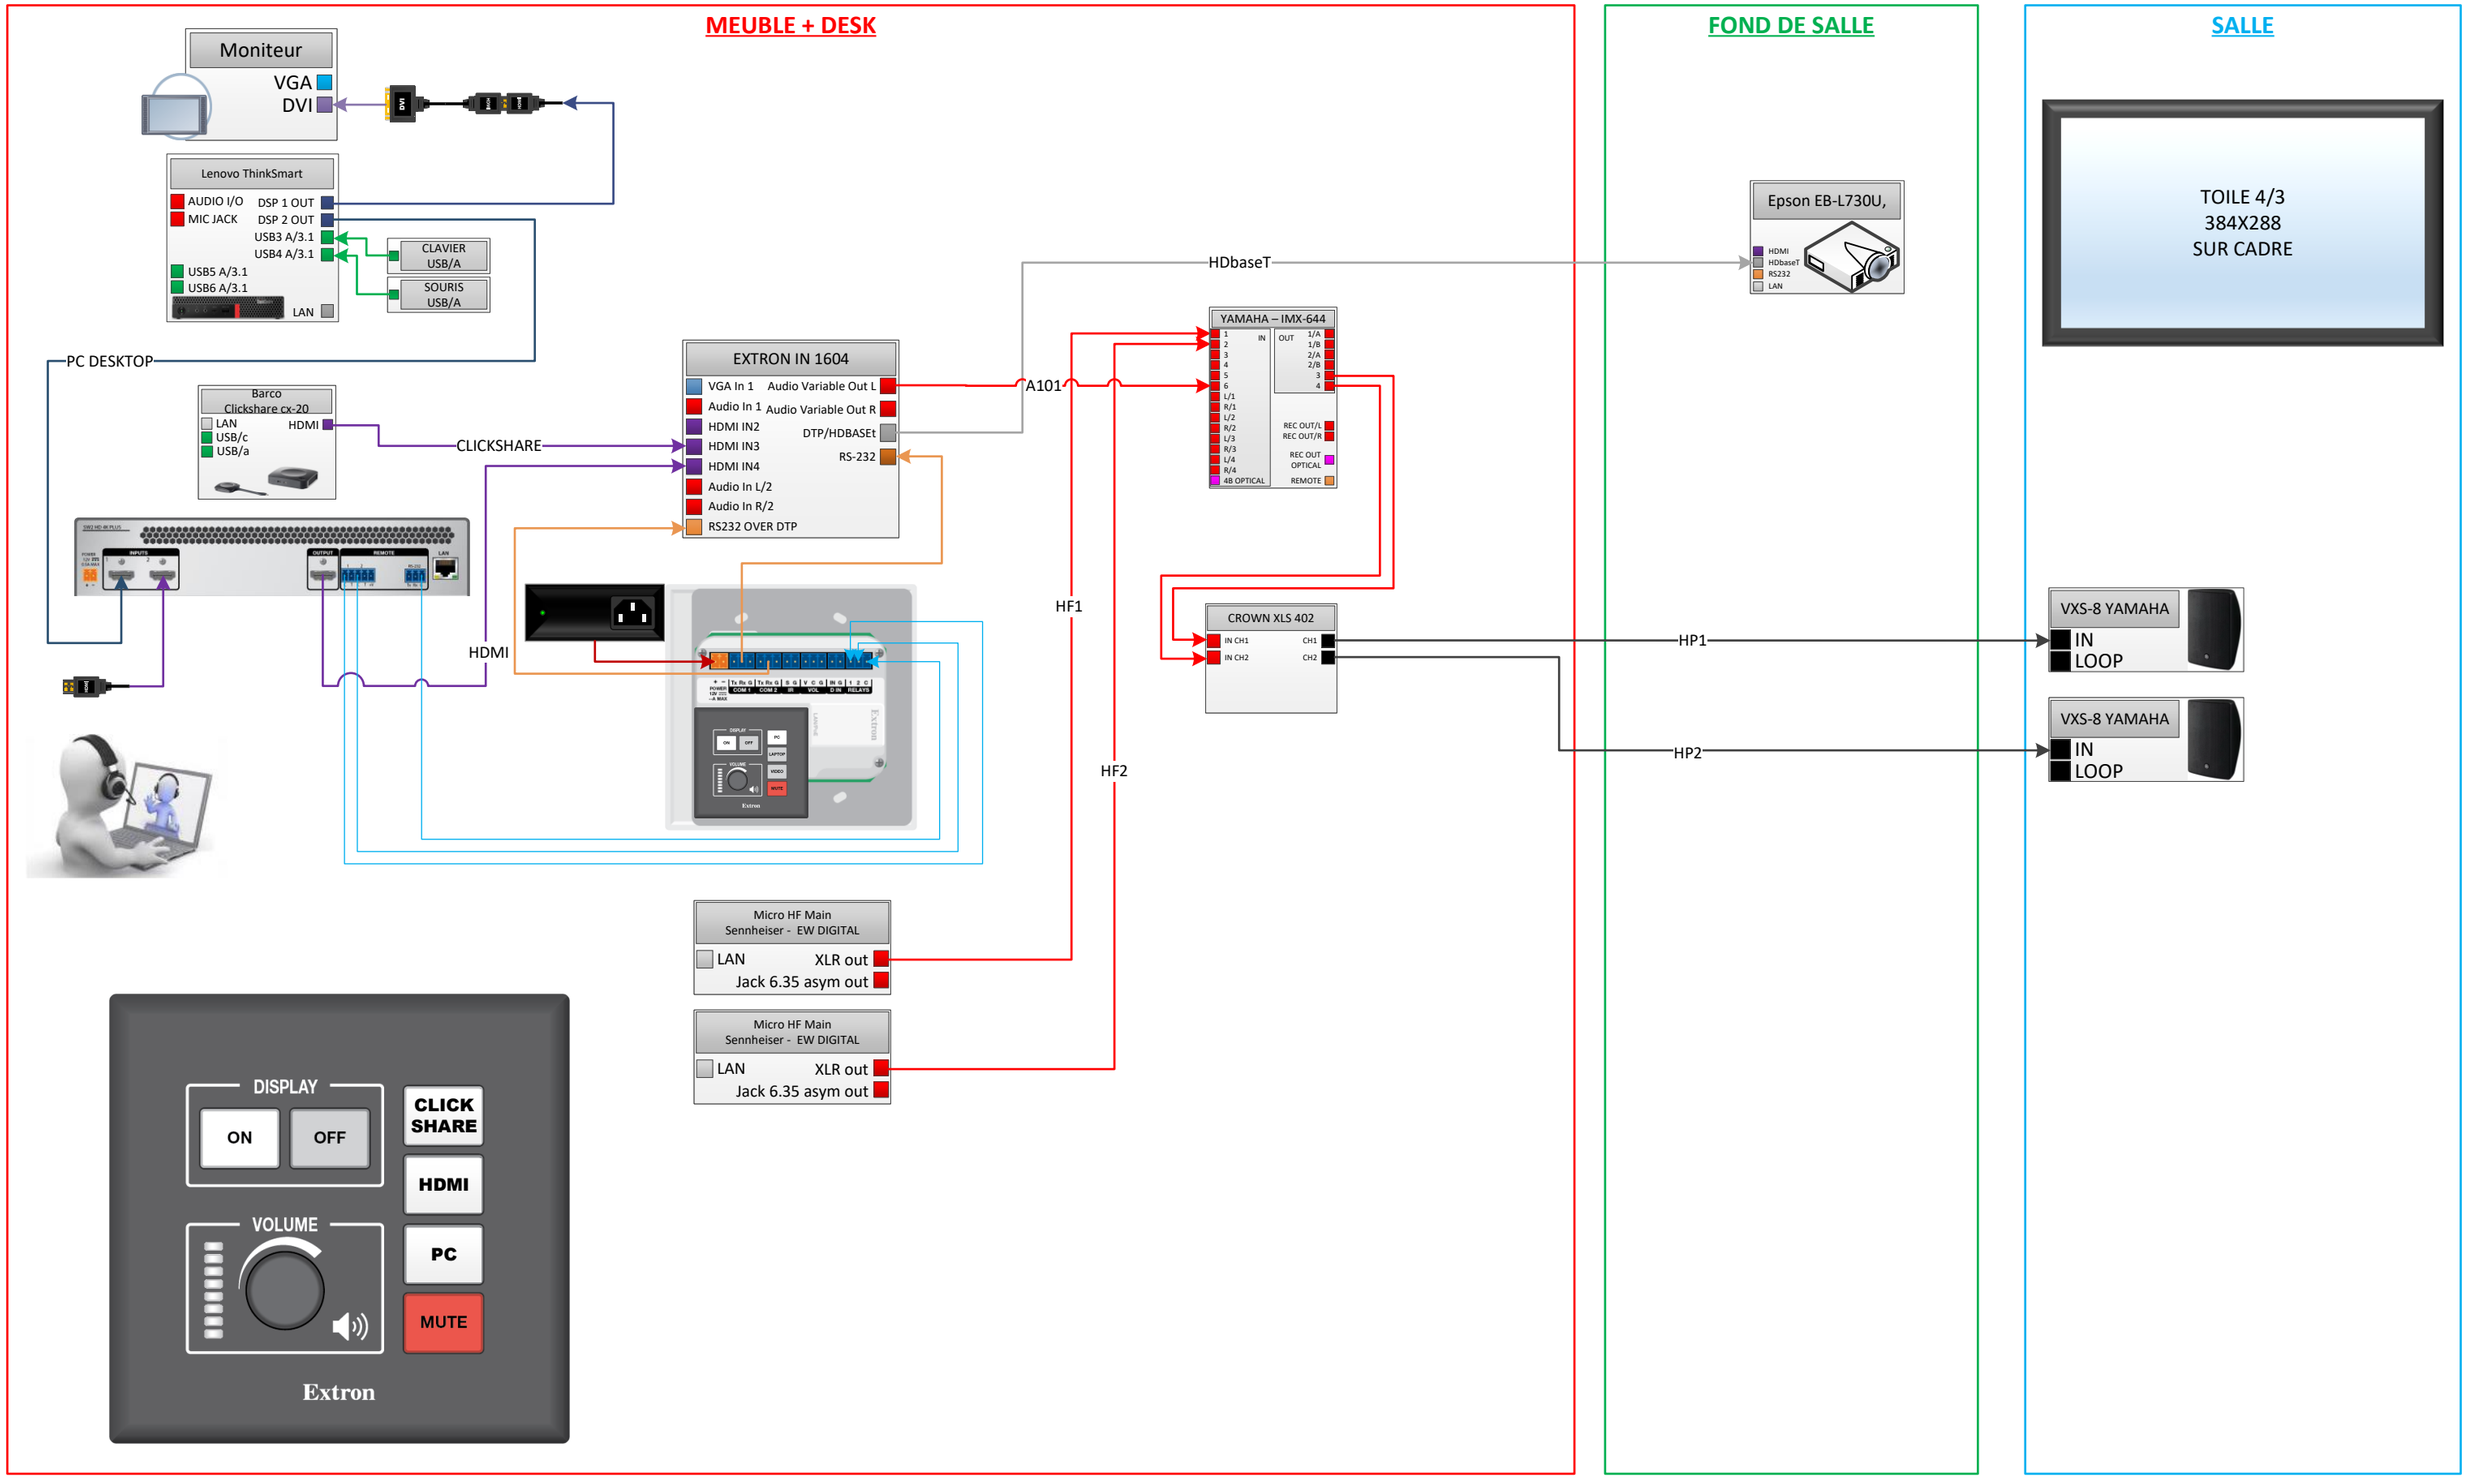

LEGENDE

- HDMI
- Audio
- Speakers
- USB
- RS232
- RJ45 cat6
- Audio Dante (RJ45 Cat6)
- Autres contrôles
- DVI
- VGA
- HD SDI
- Display port
- AC 240V
- DC OUT
- PDU

MUR
BAIE AV
TABLE

VIDEOSONIC
Image, Son & Technique
Za les portes de l'Oise
Batîment B2 – rue Henri Becquerel
60230 CHAMBLY
Tel : 01 75 01 60 40
Fax : 01 75 01 60 41
t.fourmentraux@videosonic.fr
FOURMENTRAUX Thierry

11/02/2025

CHÂTEAUFORM GRAND MELLO

SALLE LOUVOIS

SYNOPTIQUE AVC

DIMENSION	RÉV
A3	1
ECHELLE 1:1	FEUILLE 1 / 2

BAIE 12U DANS MEUBLE

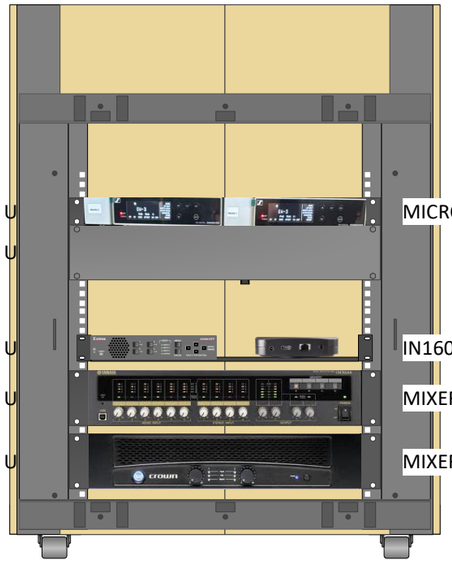

1 U MICRO HF SENNHEISER

2 U

1 U IN1604 DTP+ CX20

2 U MIXER YAMAHA IMX644

2 U MIXER YAMAHA IMX644

VIDEOSONIC
Image, Son & Technique

Za les portes de l'Oise
Batîment B2 – rue Henri Becquerel
60230 CHAMBLY
Tel : 01 75 01 60 40
Fax : 01 75 01 60 41
t.fourmentraux@videosonic.fr

FOURMENTRAUX Thierry

11/02/2025

CHÂTEAUFORM GRAND MELLO

SALLE LOUVOIS

DIMENSION			RÉV
A3		PLAN DE BAIE	1
ECHELLE 1:10		FEUILLE 2 / 2	