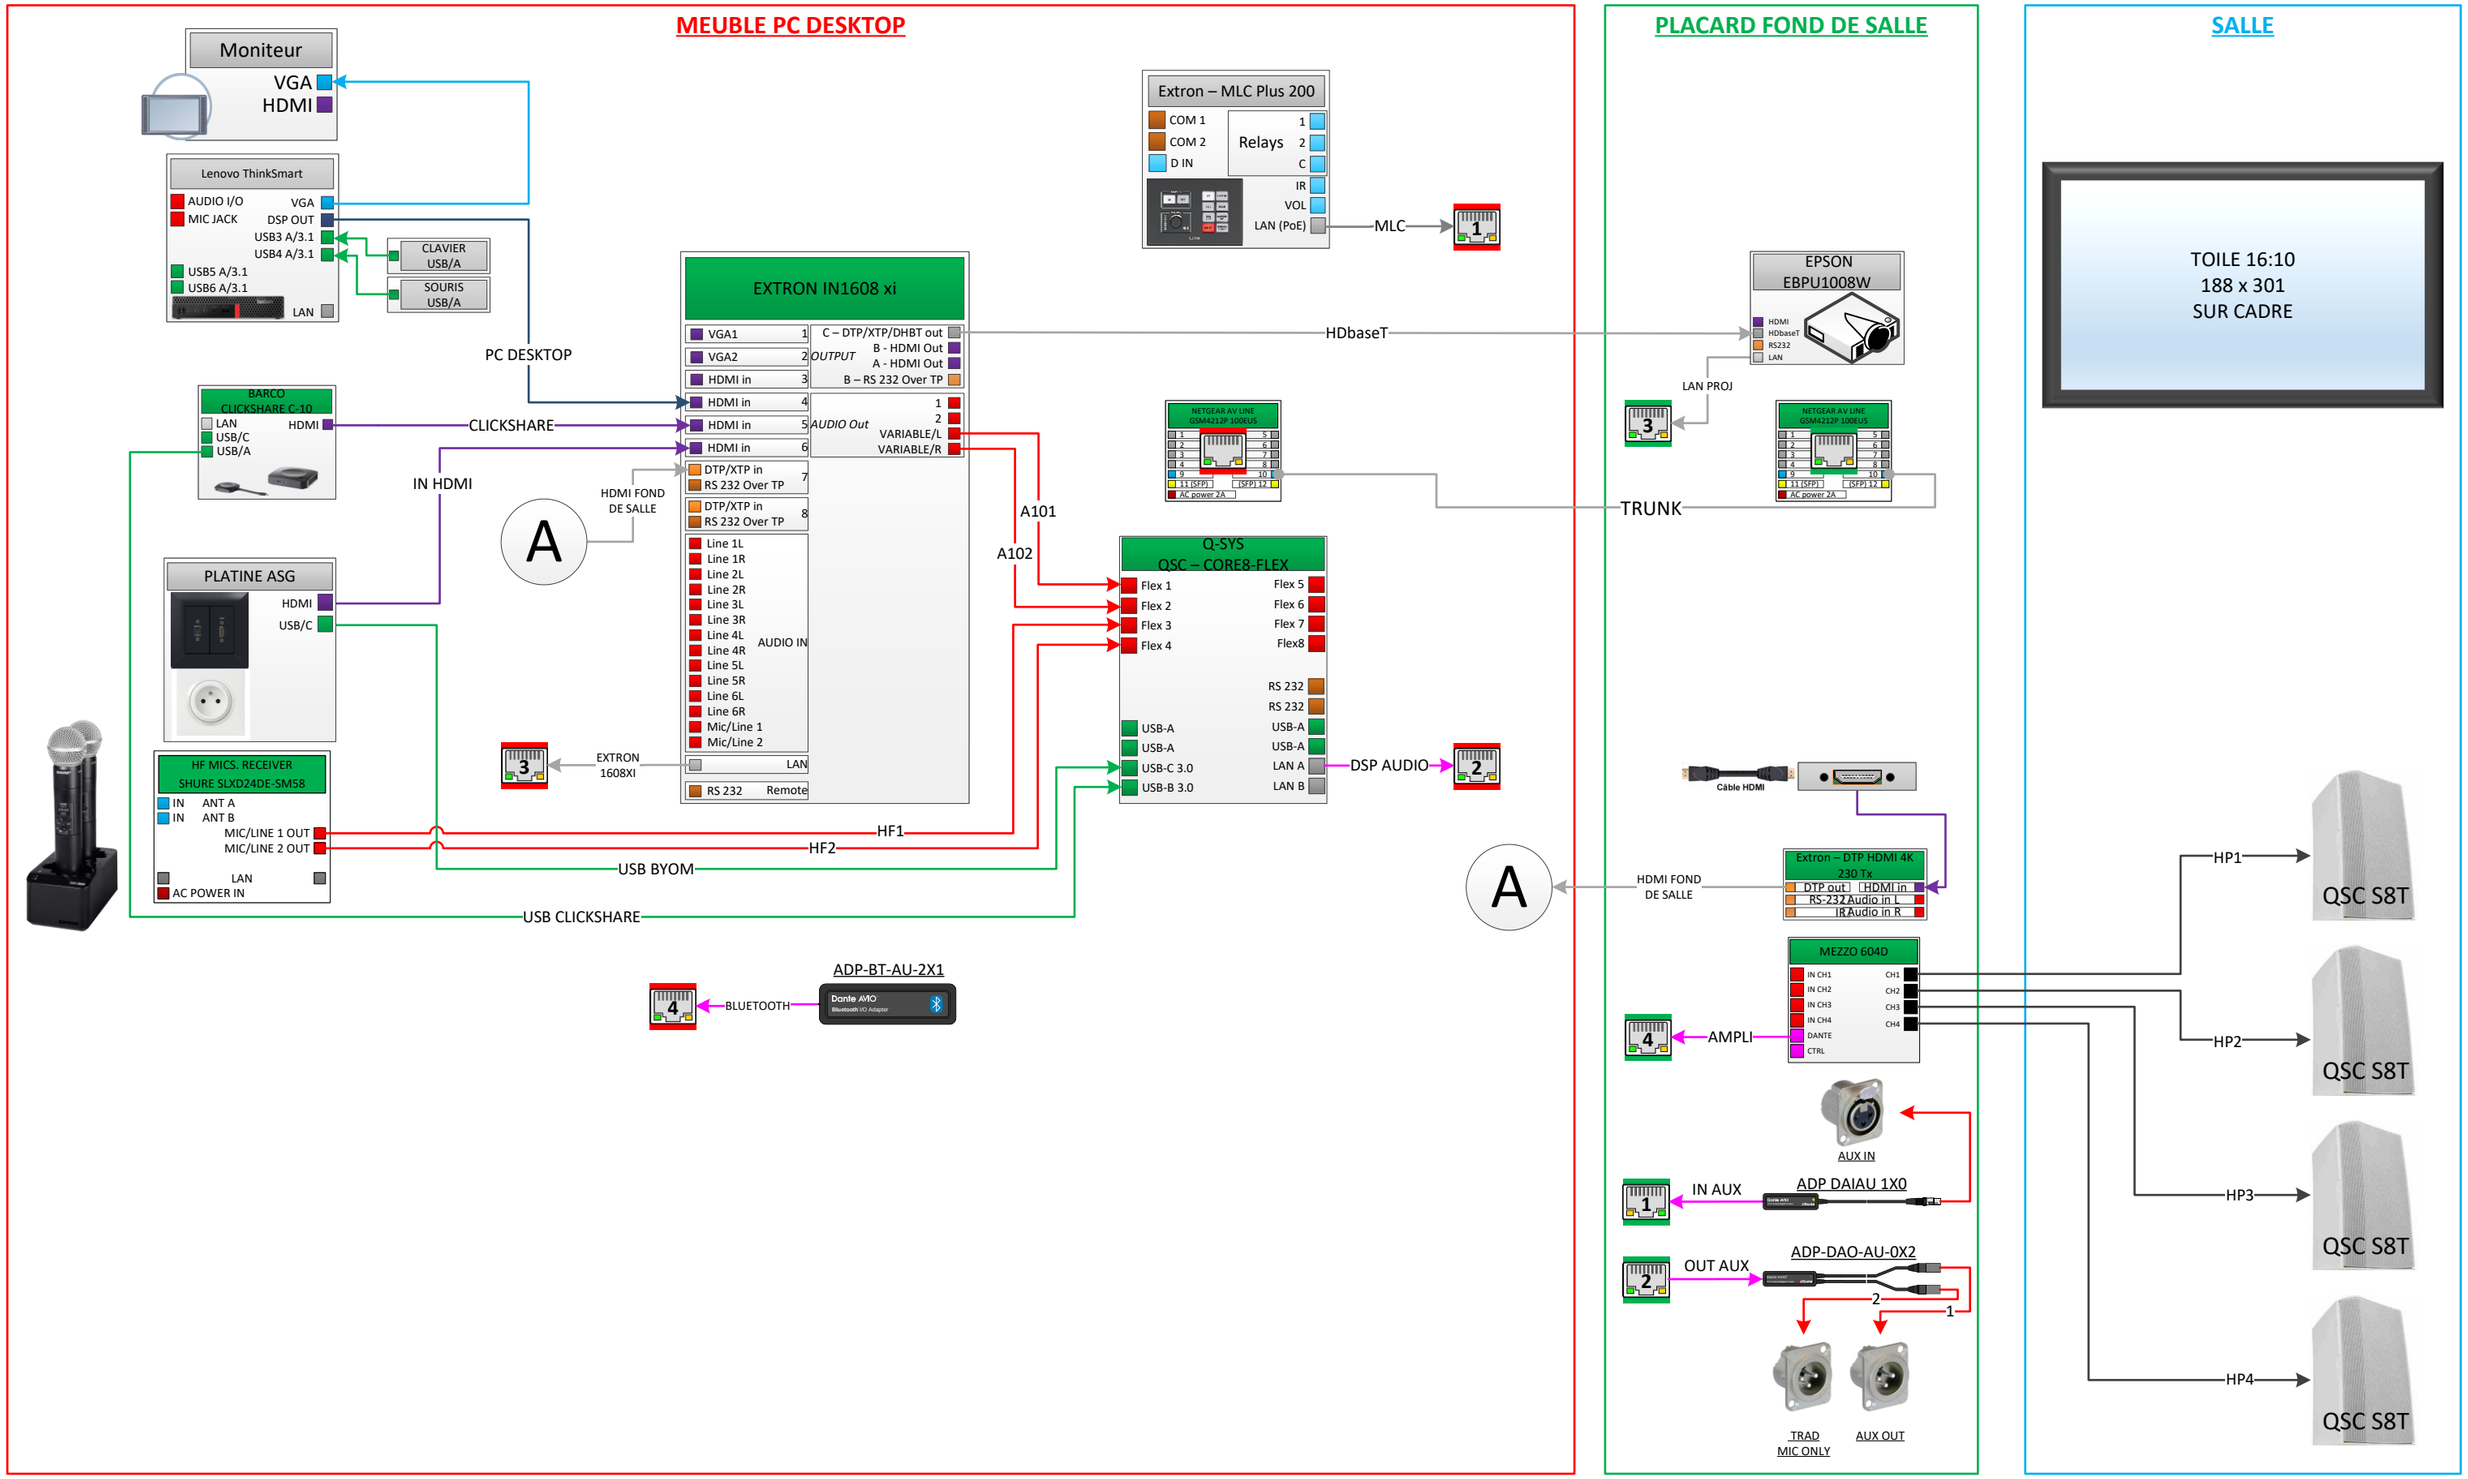

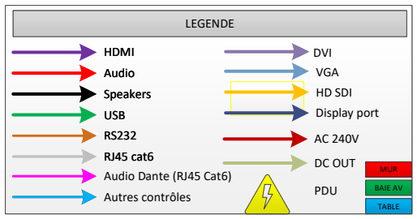

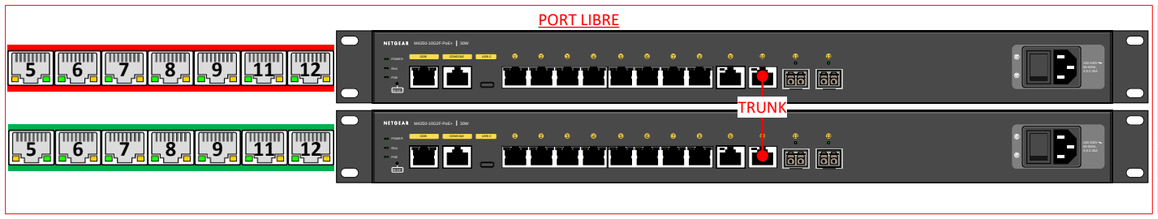

VIDEOSONIC
Image, Son & Technique
Za les portes de l'Oise
Batîment B2 – rue Henri Becquerel
60230 CHAMBLY
Tel : 01 75 01 60 40
Fax : 01 75 01 60 41
t.fourmentraux@videosonic.fr
FOURMENTRAUX Thierry

19/12/2024

CHÂTEAUFORM Méry-sur-Oise

SALLE RENOIR

SYNOPTIQUE AVC

DIMENSION	ECHELLE	FEUILLE	RÉV
A3	1:1	1 / 3	1

UTR104 EXTRON

4 U

2 U

RACK PLACARD

4 U

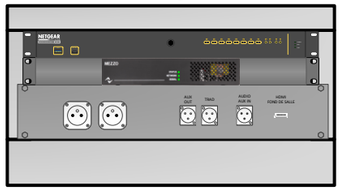

UTR104 EXTRON

4 U

1 U

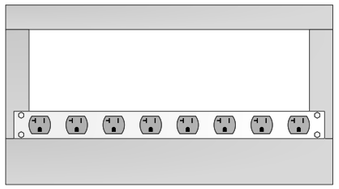

RACK PLACARD

4 U

1 U

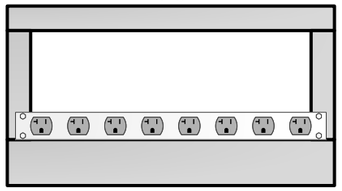

VIDEOSONIC
Image, Son & Technique

Za les portes de l'Oise
Batîment B2 – rue Henri Becquerel
60230 CHAMBLY
Tel : 01 75 01 60 40
Fax : 01 75 01 60 41
t.fourmentraux@videosonic.fr

FOURMENTRAUX Thierry

19/12/2024

CHÂTEAUFORM Méry-sur-Oise

SALLE RENOIR

DIMENSION			RÉV
A3		Plan de baie	1
ECHELLE 1:10		FEUILLE 2 / 3	

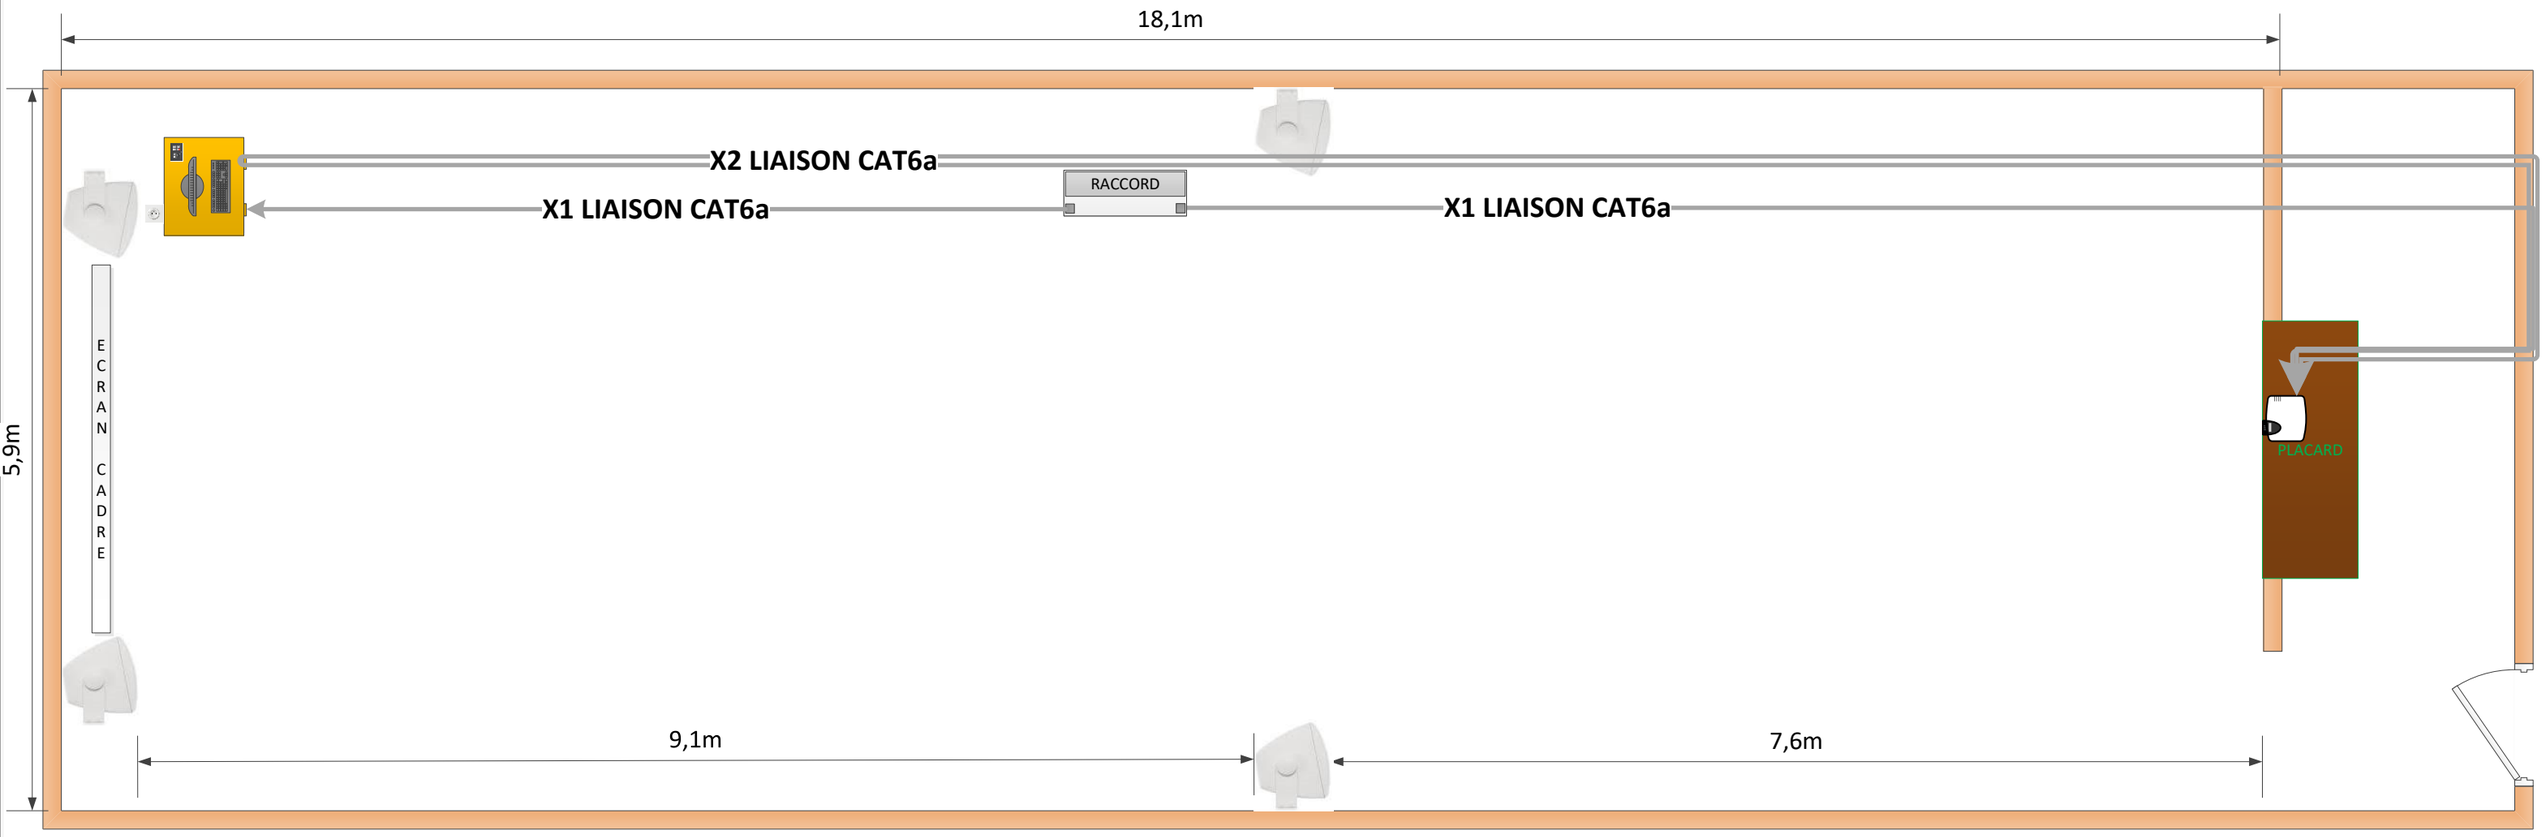

VIDEOSONIC
Image, Son & Technique
Za les portes de l'Oise
Batîment B2 – rue Henri Becquerel
60230 CHAMBLY
Tel : 01 75 01 60 40
Fax : 01 75 01 60 41
t.fourmentraux@videosonic.fr
FOURMENTRAUX Thierry

19/12/2024

CHÂTEAUFORM Méry-sur-Oise

SALLE RENOIR

DIMENSION			RÉV
A3		PLAN	1
ECHELLE 1:50		FEUILLE 3 / 3	