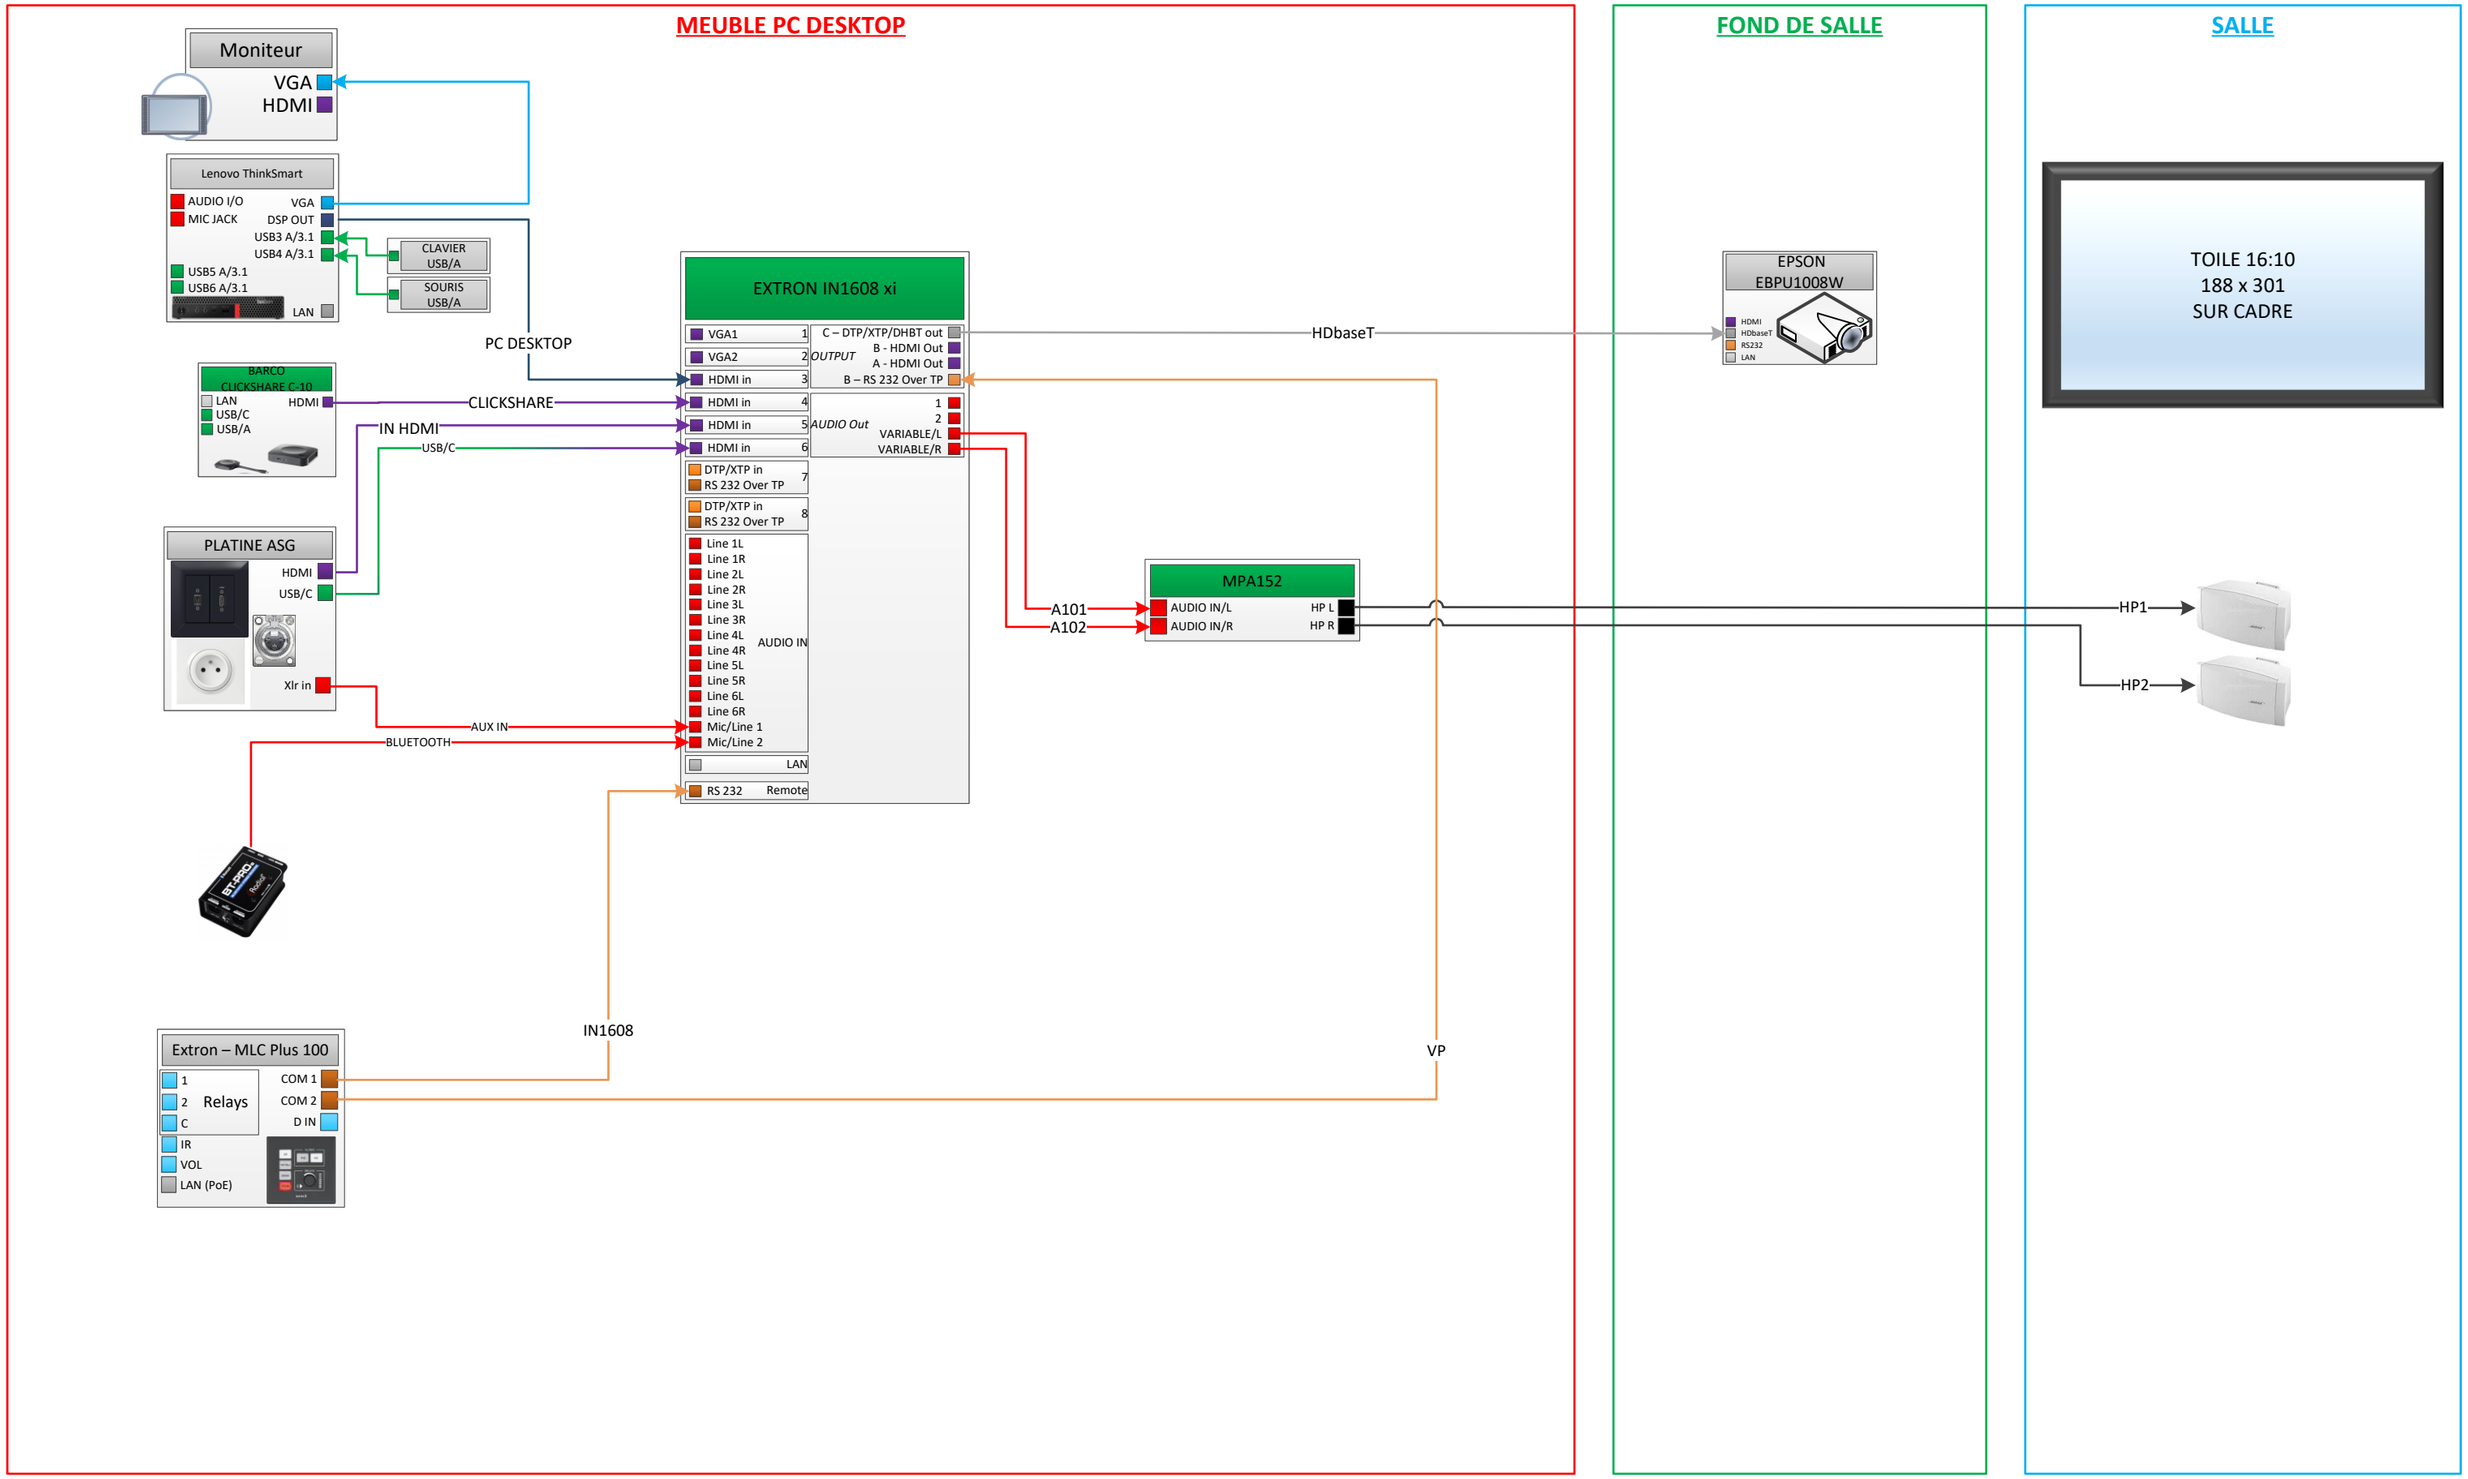

LEGENDE

- HDMI
- Audio
- Speakers
- USB
- RS232
- RJ45 cat6
- Audio Dante (RJ45 Cat6)
- Autres contrôles
- DVI
- FIBRE
- HD SDI
- Display port
- AC 240V
- DC OUT
- PDU

MUR
BAIE AV
TABLE

VIDEOSONIC
Image, Son & Technique
Za les portes de l'Oise
Batîment B2
rue Henri Becquerel
60230 CHAMBLY
Tel : 01 75 01 60 40
Fax : 01 75 01 60 41
t.fourmentraux@videosonic.fr

salle Degas.vsdm

Chteauform mery sur oise

Thierry FOURMENTRAUX	DIMENSION A3	N° CODE	PAGE synoptique acv	RÉV 16/01/2026
vendredi 16 janvier 2026	ECHELLE 1:1		FEUILLE 1 / 2	

UTR104 EXTRON

4 U

1 U MPA122+BLUETOOTH+CLICKSHARE

1 U IN 1608XI

2 U TIROIR

UTR104 EXTRON

4 U

1 U BANDEAU 9 PRISES

VIDEOSONIC
Image, Son & Technique

Za les portes de l'Oise
Batîment B2
rue Henri Becquerel
60230 CHAMBLY
Tel : 01 75 01 60 40
Fax : 01 75 01 60 41
t.fourmentraux@videosonic.fr

Thierry FOURMENTRAUX

16/01/2026

salle Degas.vsdm

DIMENSION	N° CODE	PAGE	RÉV
A3		plan de baie	16/01/2026
ECHELLE 1:10		FEUILLE 2 / 2	