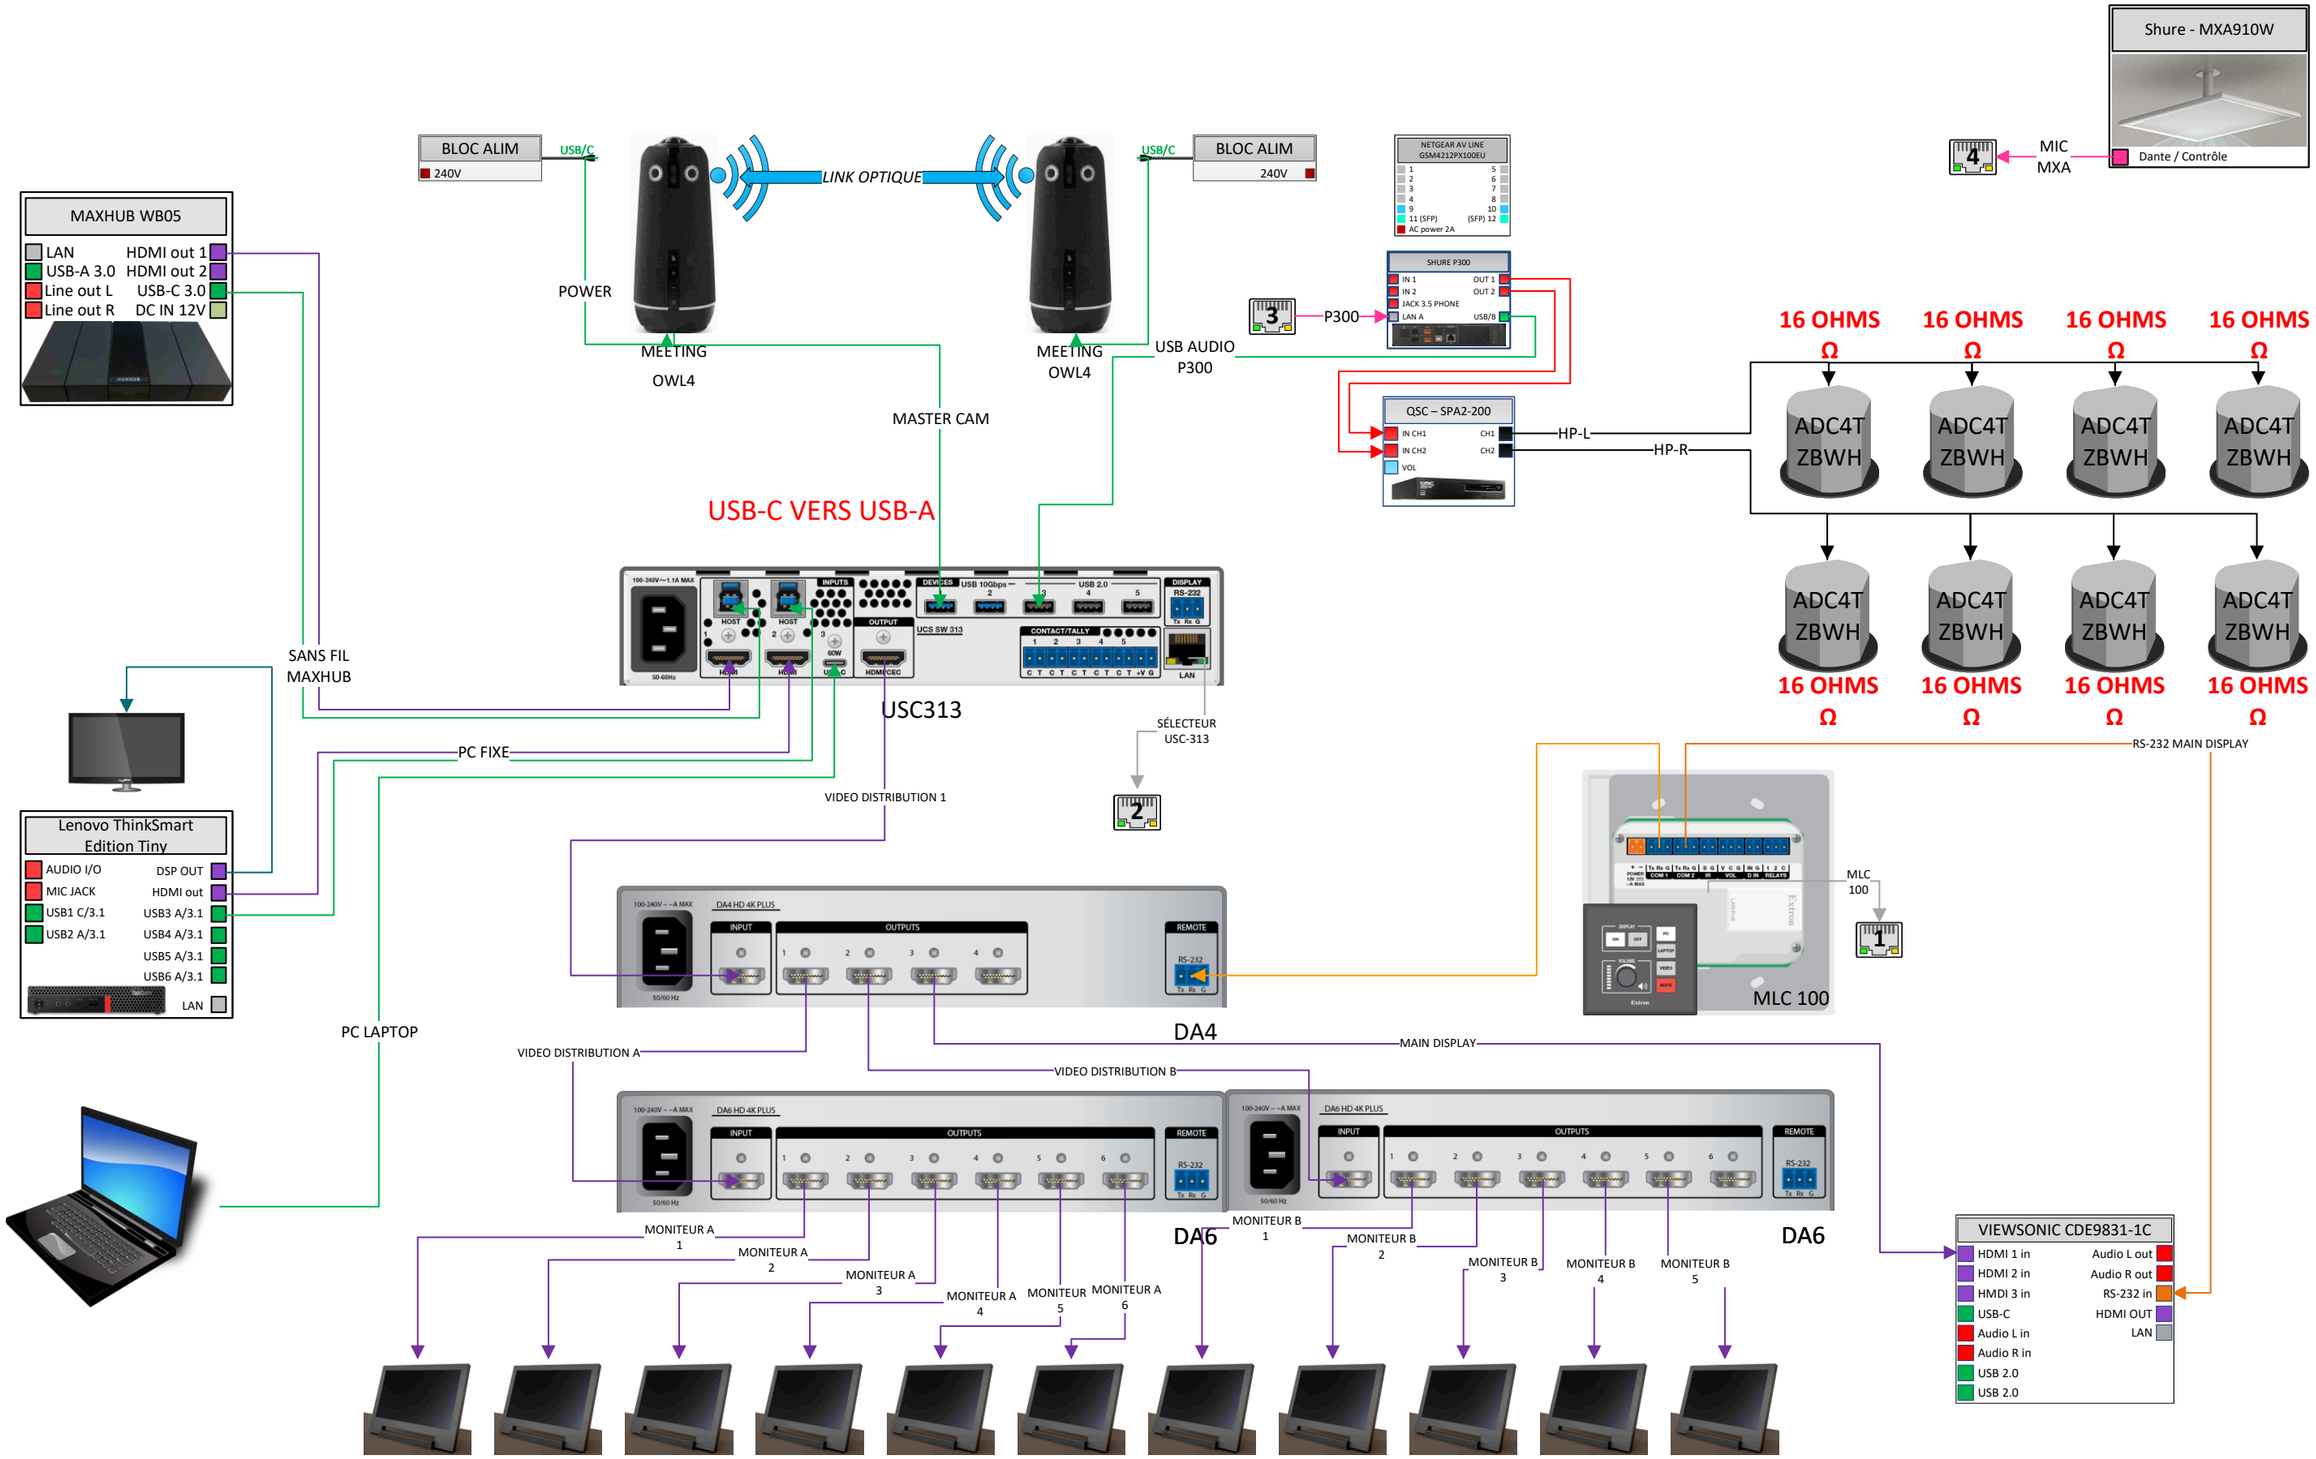

LEGENDE

- HDMI
- Audio
- Speakers
- USB
- RS232
- RJ45 cat6
- Audio Dante (RJ45 Cat6)
- Autres contrôles
- DVI
- FIBRE
- HD SDI
- Display port
- AC 240V
- DC OUT
- PDU

MDR / BAIE AV / TABLE

PORT LIBRE

VIDEOSONIC Image, Son & Technique
Za les portes de l'Oise
Batiment B2
rue Henri Becquerel
60230 CHAMBLY
Tel : 01 75 01 60 40
Fax : 01 75 01 60 41
t.fourmentraux@videosonic.fr

RENOVATION DE LA SALLE BONCOURT

Polytechnique
Route de Saclay
91120 PALAISEAU

Thierry FOURMENTRAUX	DIMENSION A3	N° CODE	PAGE synoptique acv	RÉV 05/03/2026
MARDI 27 JANVIER 2026	ECHELLE 1:1		FEUILLE 1 / 2	

BERCEAU SOUS TABLE
LOGILINK
4 U

1 U	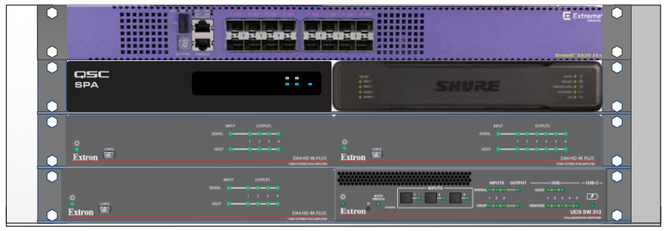	SWITCH AV EXTREM
1 U		QSC SPA2-200 + SHURE P300
1 U		HDMI DA 6 + DA 6
1 U		HDMI DA 4 + USC313 SELECTEUR

VIDEOSONIC
Image, Son & Technique
Za les portes de l'Oise
Batîment B2
rue Henri Becquerel
60230 CHAMBLY
Tel : 01 75 01 60 40
Fax : 01 75 01 60 41
t.fourmentraux@videosonic.fr

RENOVATION DE LA SALLE BONCOURT

Polytechnique
Route de Saclay
91120 PALAISEAU

Thierry FOURMENTRAUX

MARDI 27 JANVIER 2026

DIMENSION	N° CODE	PAGE	RÉV
A3		plan de baie	05/03/2026
ECHELLE 1:5		FEUILLE 2 / 2	