Groupama – Olivet

Salle du Conseil

Synoptiques d’exécution & Plan de baie

VIDEOSONIC
Image, Son & Technique
Za les portes de l’Oise
Batiment B2 – rue Henri Becquerel
60230 CHAMBLY
Tel : 01 75 01 60 40
Fax : 01 75 01 60 41
T.fourmentraux@videosonic.fr
FOURMENTRAUX THIERRY

30/01/2026

Salle du conseil

Groupama
60 Boulevard Duhamel du Monceau, 45166 Olivet

DIMENSION			RÉV
		Page de Garde	1
ECHELLE	1:1	FEUILLE	1 / 6

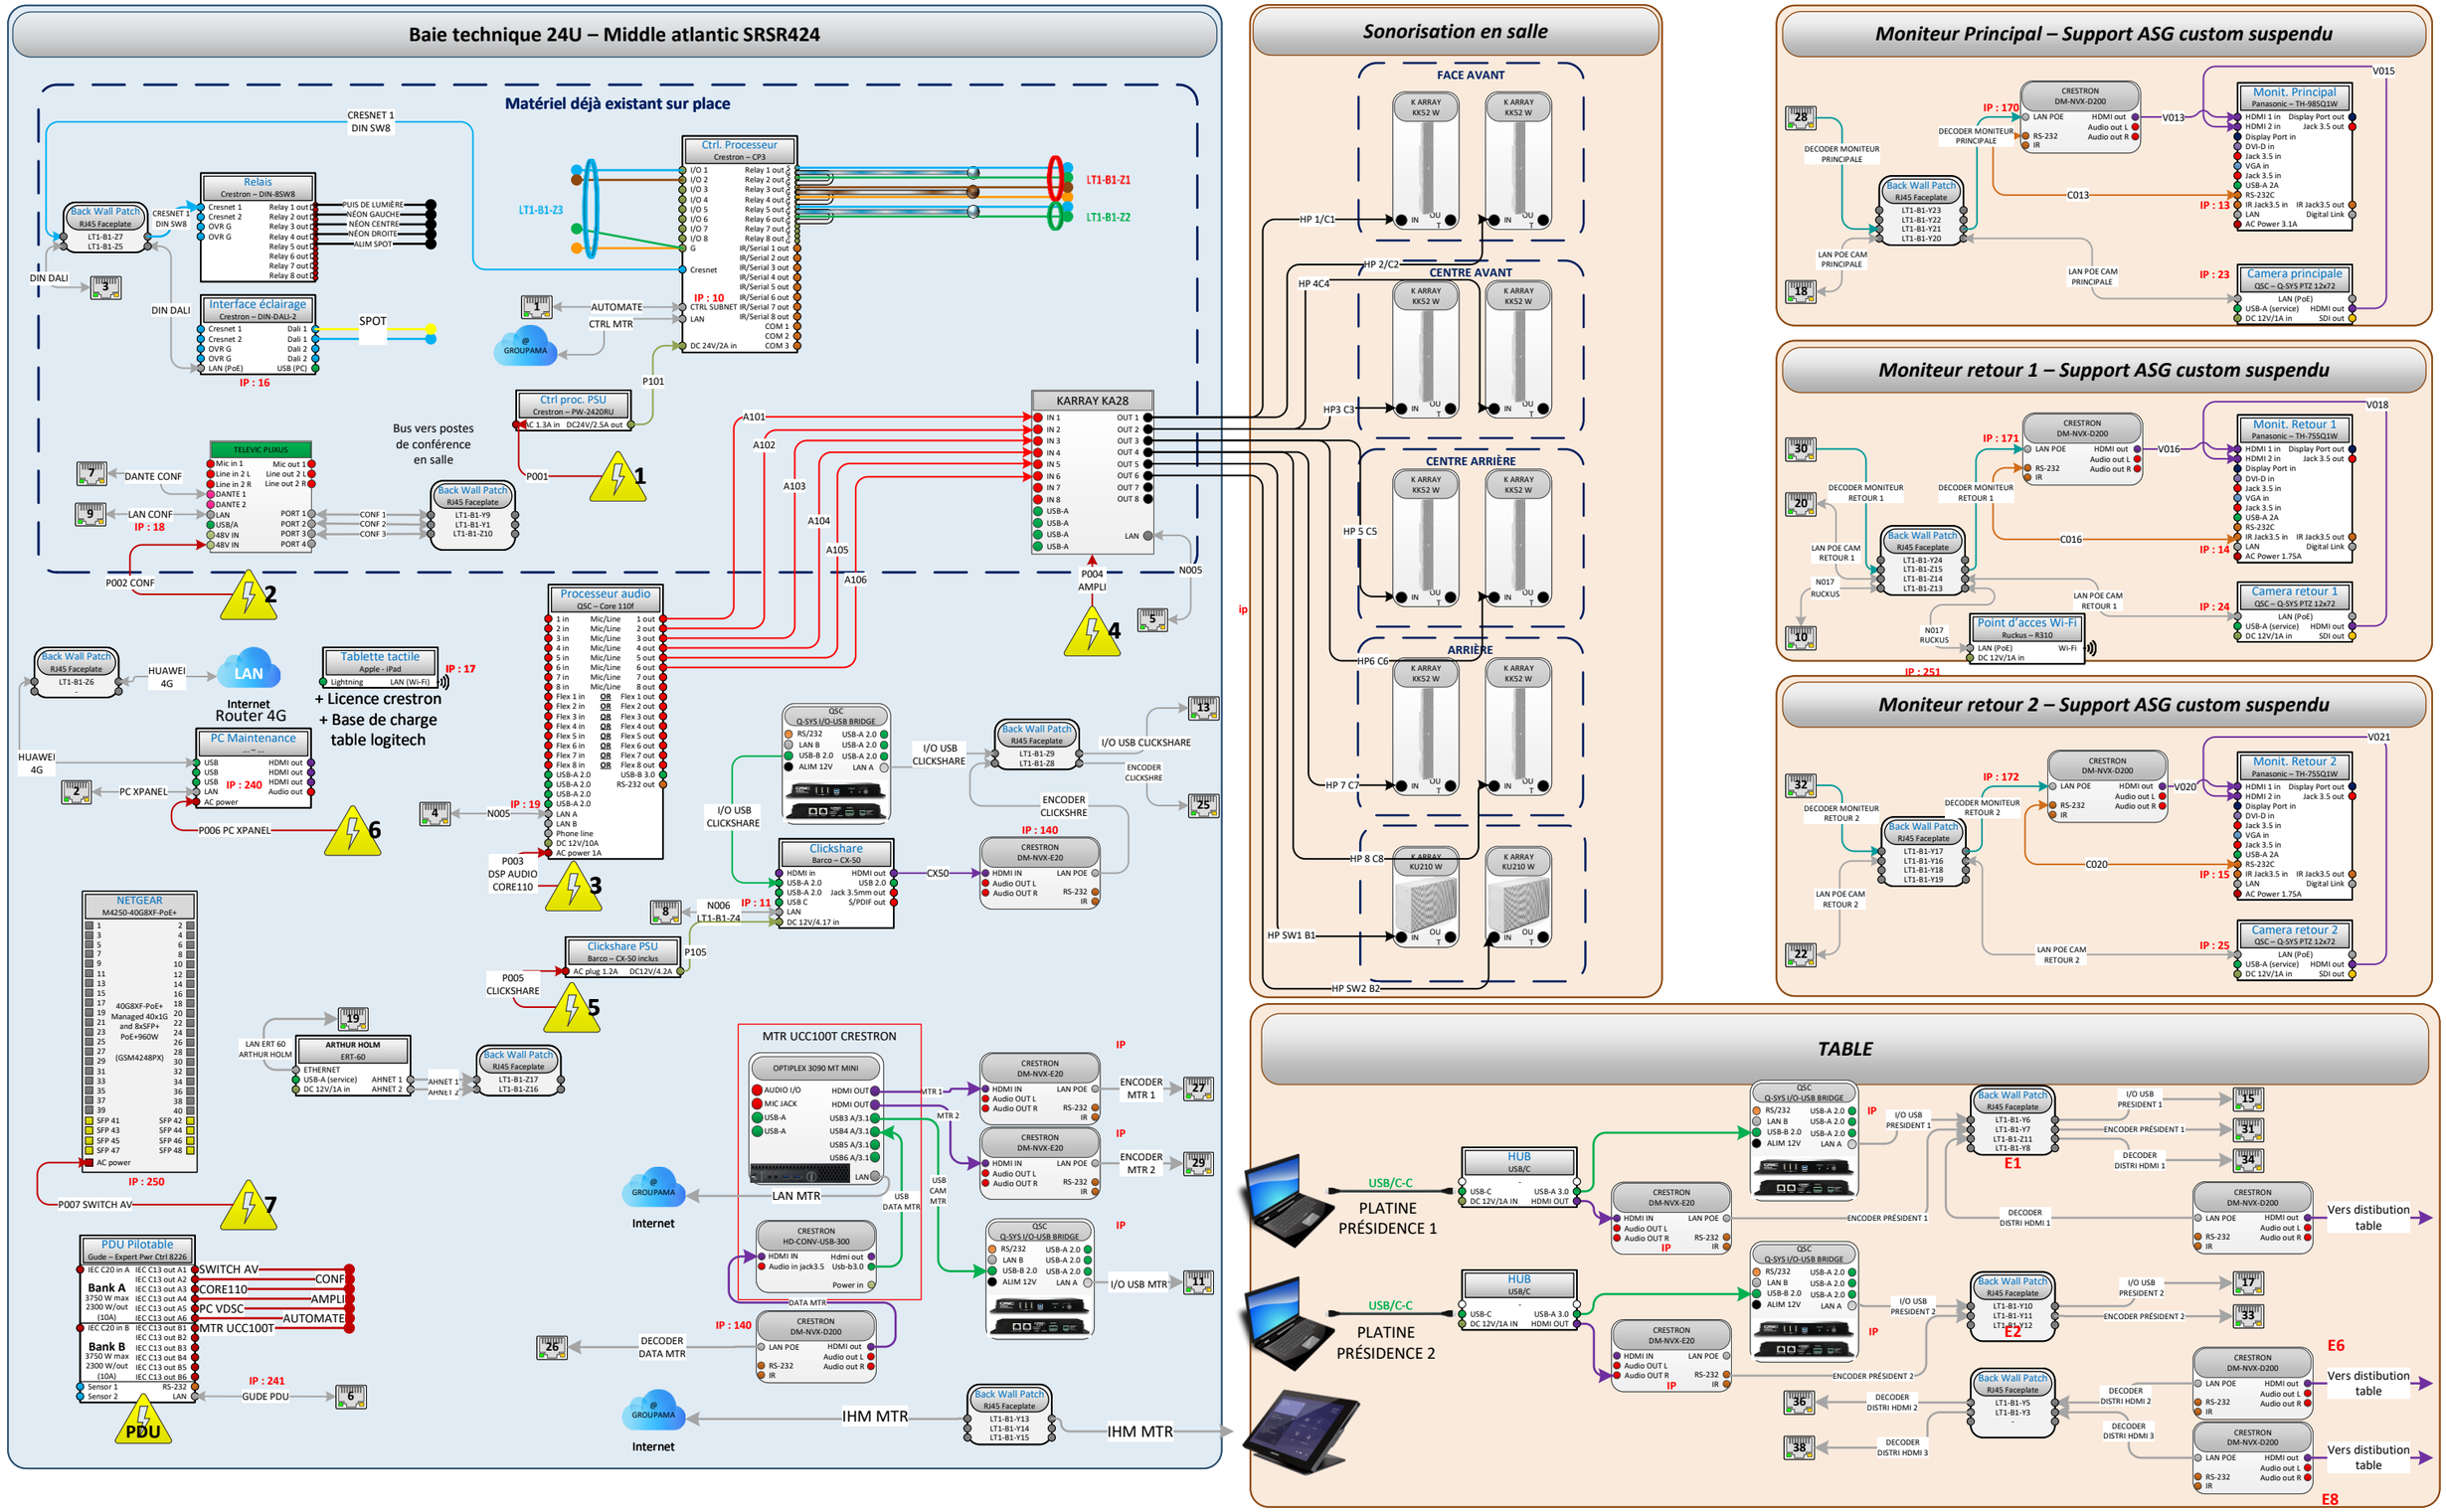

Légende

Code couleur du câblage

- HDMI
- Display Port
- (HD) SDI
- DVI
- VGA
- Vidéo autres
- Audio Analogique
- Audio Numérique
- Haut Parleur
- RJ45 Cat.6 Audio
- RJ45 Cat.6 Video
- RJ45 Cat.6 Réseau
- Fibre Optique
- USB
- RS-232
- Electricité C Fort
- Electricité C Faible
- Contrôle autres

Adressage IP

Base des adresses IP : 192.168.0.xxx

IP : xxx :
Dernier nombre IPv4 de la machine

Etiquettes d'envoi du câblage

NOM DE PAGE
Nom de la machine – Nom du port

Nom de la machine – Nom du port

Numérotation de câblage

A	Audio	N	Réseau (Network)
AN	Réseau audio (Audio Network)	P	Puissance
C	Contrôle	S	Haut-Parleurs (Speakers)
D	Divers	V	Video
U	USB	VN	Réseau Vidéo (Video Network)

VIDEOSONIC
Image, Son & Technique
Za les portes de l'Oise
Batiment B2 – rue Henri Becquerel
60230 CHAMBLY
Tel : 01 75 01 60 40
Fax : 01 75 01 60 41
T.fourmentraux@videosonic.fr
FOURMENTRAUX THIERRY

30/01/2026

Salle du conseil

Groupama
60 Boulevard Duhamel du Monceau, 45166 Olivet

DIMENSION		Synoptique	RÉV
			1
ECHELLE	1:1	FEUILLE	2 / 7

BAIE IT 42U

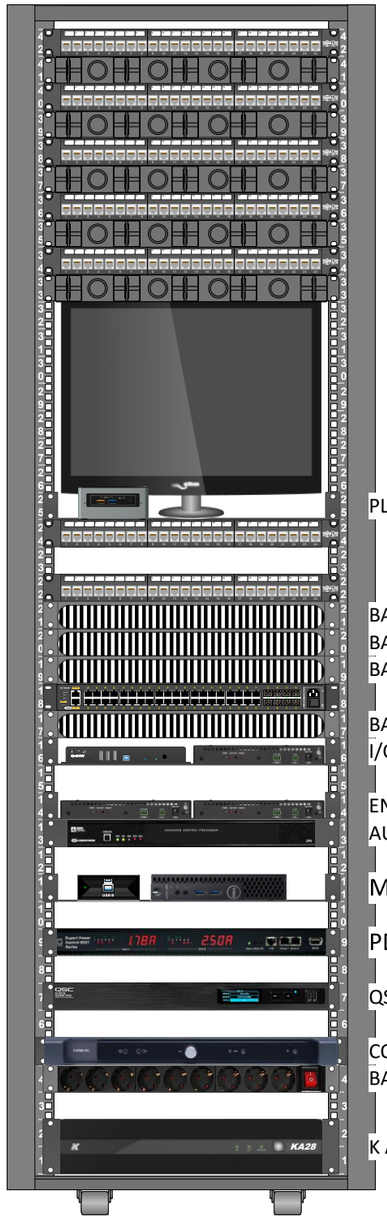

	PATCH RJ45
	PATCH RJ45
	PATCH RJ45
	PATCH RJ45
	PATCH RJ45
1 U	PLATEAU PC CRESTRON XPANEL
	PATCH Y RJ45
	PATCH Z RJ45
1 U	BALAIS PASSE CABLE
1 U	BALAIS PASSE CABLE
1 U	BALAIS PASSE CABLE
1 U	BALAIS PASSE CABLE
1 U	I/O USB MTR + DECODER DATA MTR
1 U	ENCODER MTR 1+ MTR 2
1 U	AUTOMATE CRESTRON CP4
1 U	MTR CRESTRON KIT UCC100T
1 U	PDU GUDE
1 U	QSC Q-SYS CORE 110F
1 U	CONF TELEVIC PLIXUS AE-R
1 U	BANDEAU 9 PRISES
2 U	K ARRAY KA28

VIDEOSONIC
Image, Son & Technique
Za les portes de l'Oise
Batiment B2 – rue Henri Becquerel
60230 CHAMBLY
Tel : 01 75 01 60 40
Fax : 01 75 01 60 41
@ : contact@videosonic.fr

Salle du conseil

Groupama
60 Boulevard Duhamel du Monceau, 45166 Olivet

FOURMENTRAUX THIERRY

30/01/2026

DIMENSION			RÉV
		Plan d e baie	1
ECHELLE	1:10	FEUILLE	3 / 6

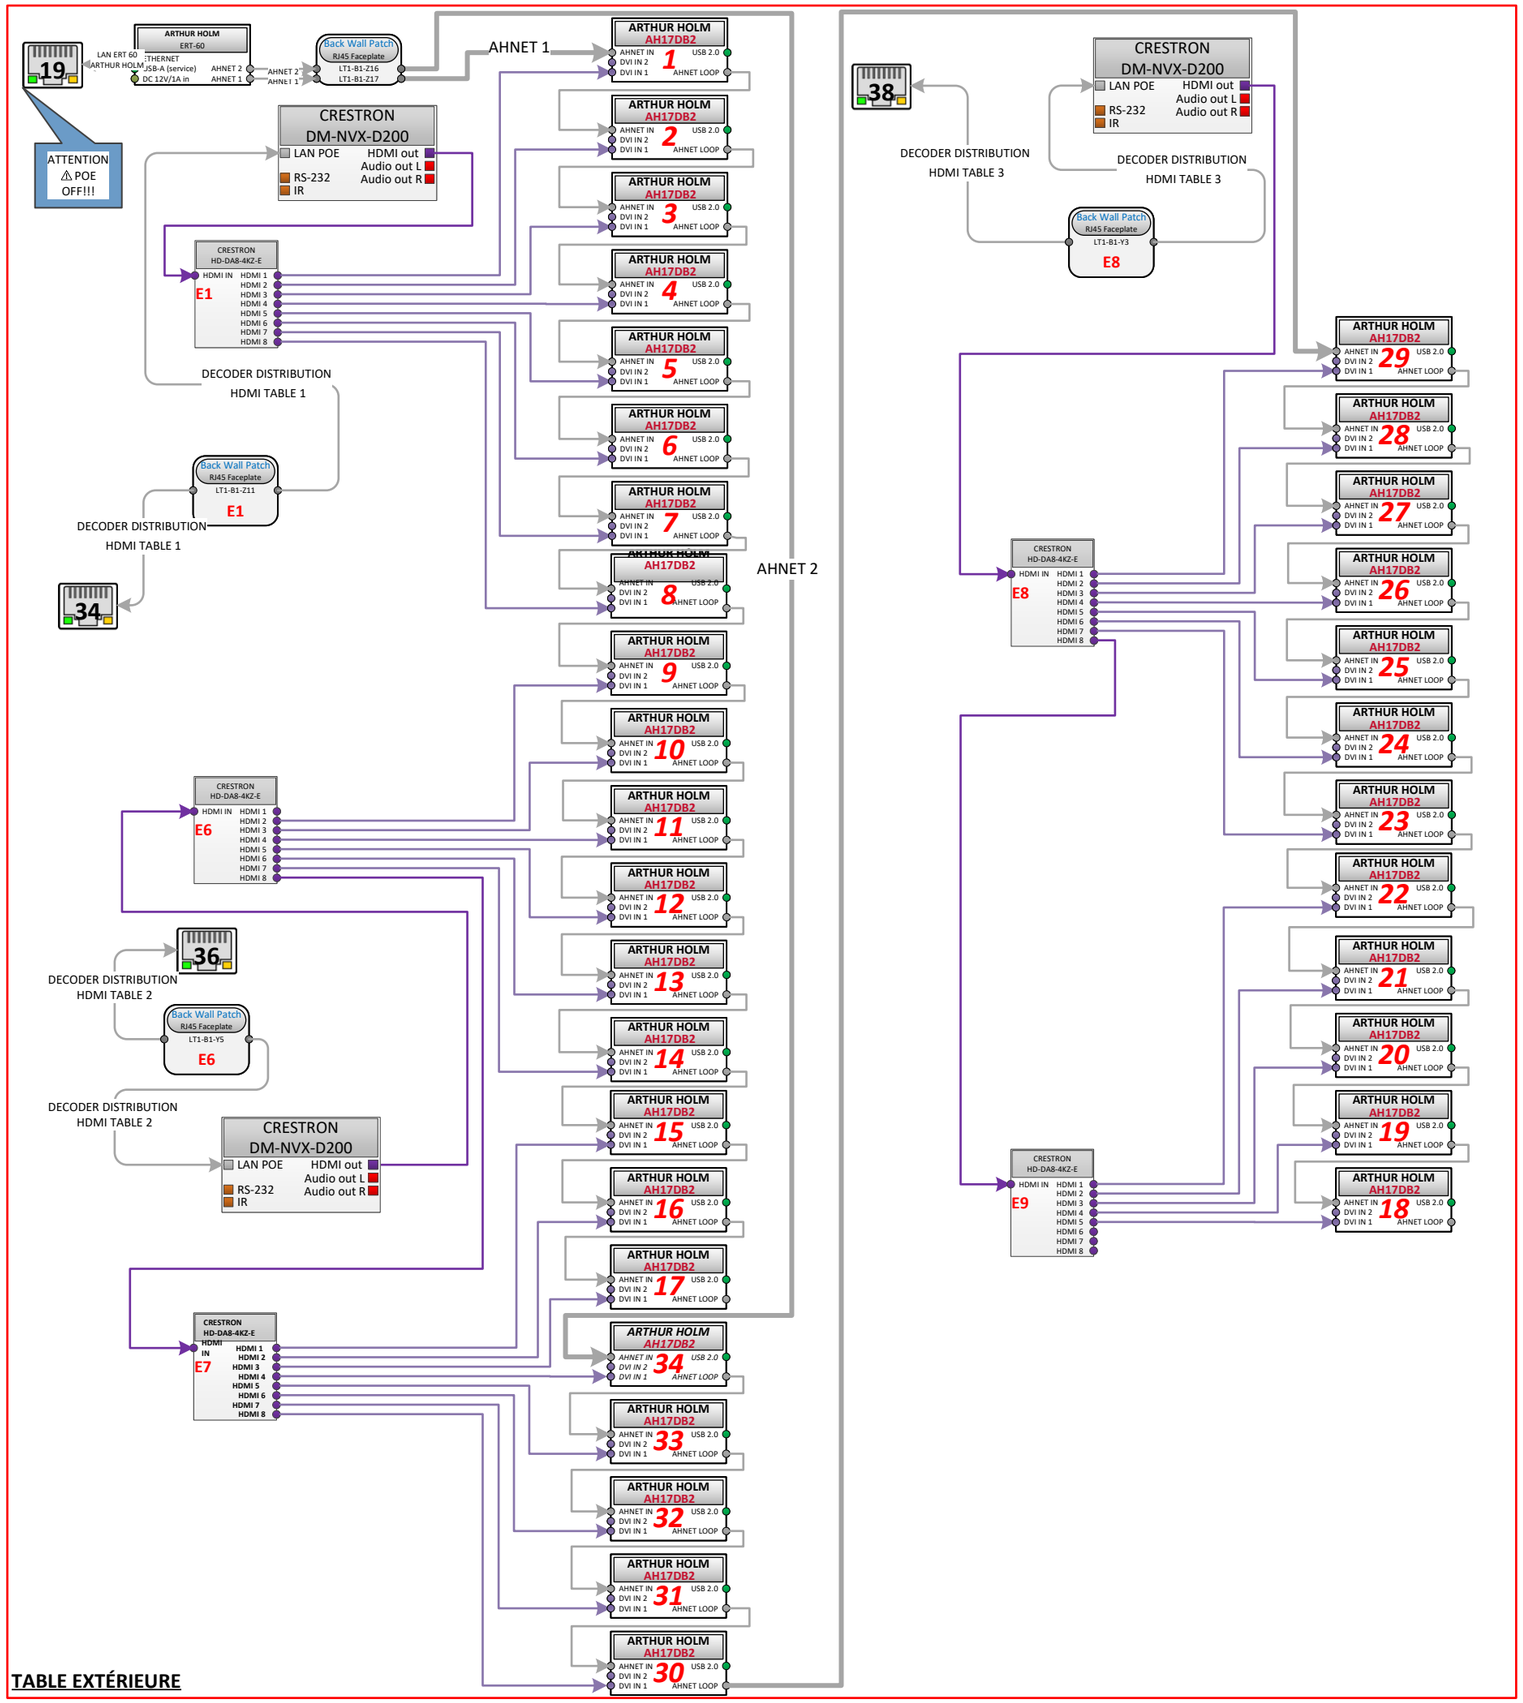

TABLE EXTÉRIEURE

TABLE INTÉRIEURE

VIDEOSONIC
Image, Son & Technique
Za les portes de l'Oise
Batiment B2 – rue Henri Becquerel
60230 CHAMBLY
Tel : 01 75 01 60 40
Fax : 01 75 01 60 41
T.fourmentraux@videosonic.fr

FOURMENTRAUX THIERRY

30/01/2026

Salle du conseil

Groupama
60 Boulevard Duhamel du Monceau, 45166 Olivet

DIMENSION			RÉV
		DISTRIBUTION VIDÉO TABLE	1
ECHELLE	1:1	FEUILLE	4 / 7

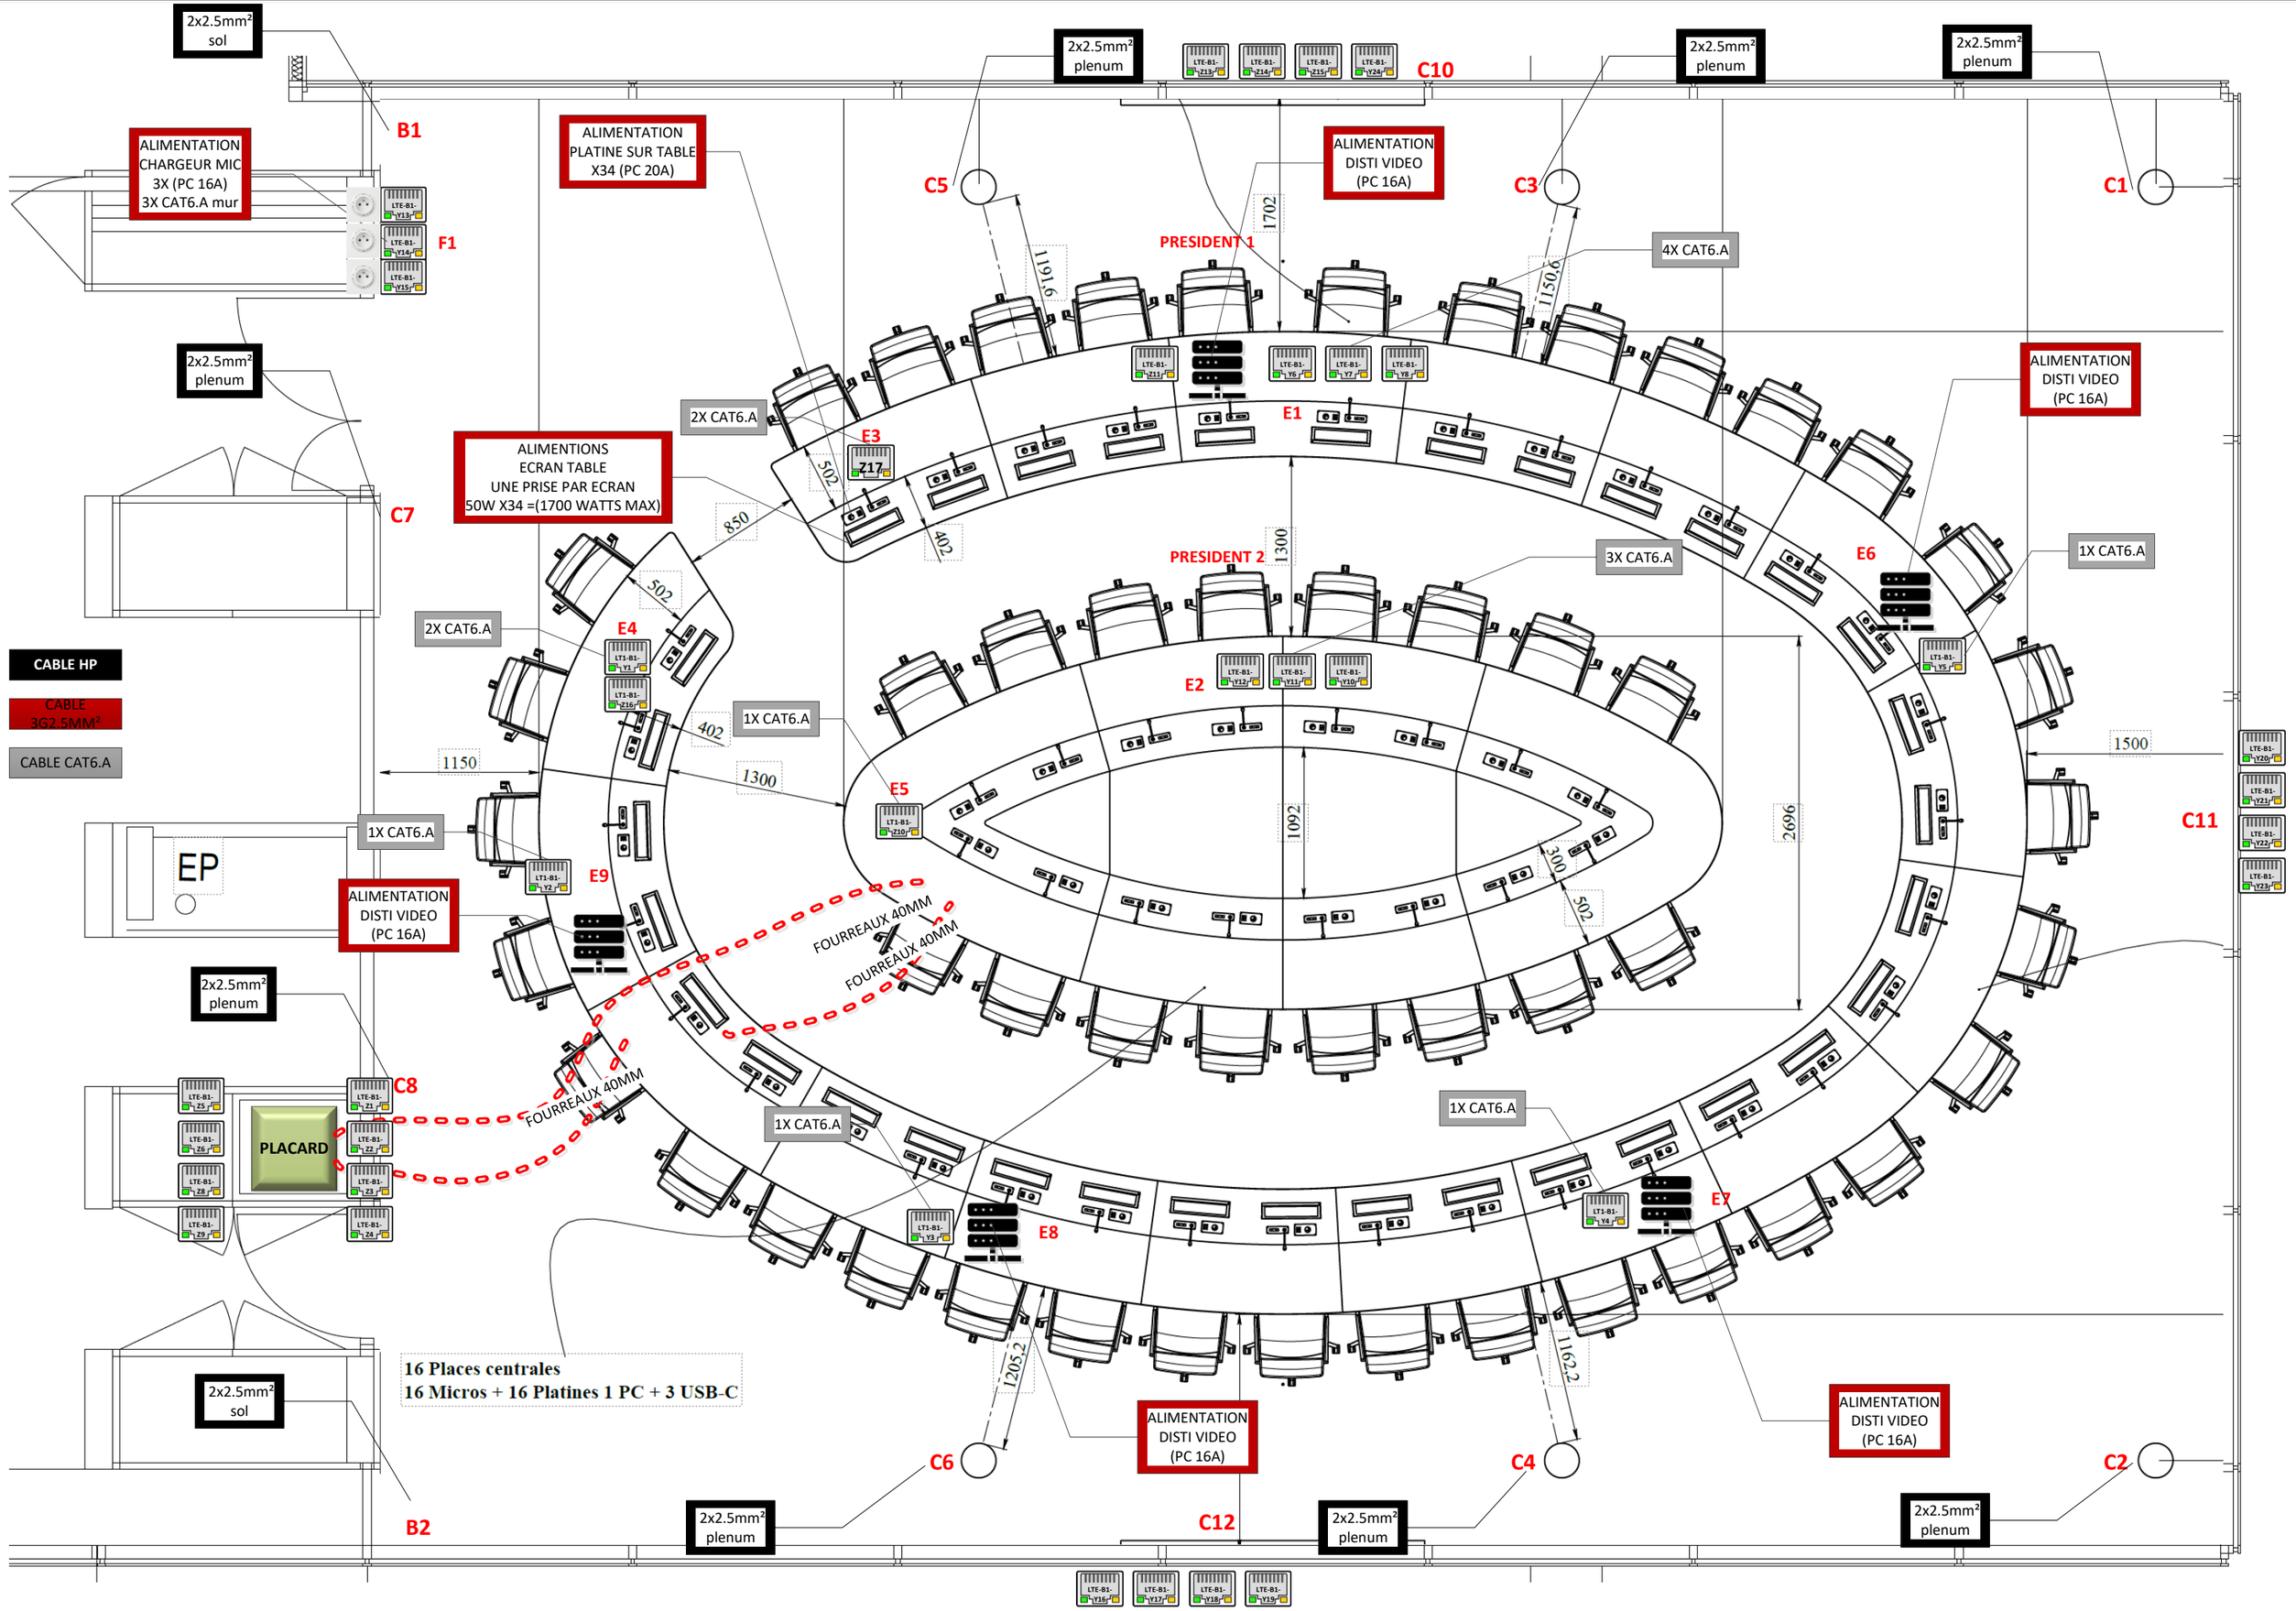
2x2.5mm² sol
B1
ALIMENTATION CHARGEUR MIC 3X (PC 16A) 3X CAT6.A mur
F1
2x2.5mm² plenum
C7
CABLE HP
CABLE 3G2.5MM²
CABLE CAT6.A
EP
ALIMENTATION PLATINE SUR TABLE X34 (PC 20A)
ALIMENTIONS ECRAN TABLE UNE PRISE PAR ECRAN 50W X34 =(1700 WATTS MAX)
2X CAT6.A
1X CAT6.A
ALIMENTATION DISTI VIDEO (PC 16A)
2x2.5mm² plenum
C8
PLACARD
FOURREAUX 40MM
2x2.5mm² sol
B2
16 Places centrales
16 Micros + 16 Platines 1 PC + 3 USB-C
C5
C3
C1
C10
C11
C12
C6
C4
C2
PRESIDENT 1
PRESIDENT 2
4X CAT6.A
3X CAT6.A
E1
E2
E3
E4
E5
E6
E7
E8
E9
Z17
1702
1191,6
1150,6
850
502
402
1300
1150
1092
2696
1500
300
1205,2
1162,2

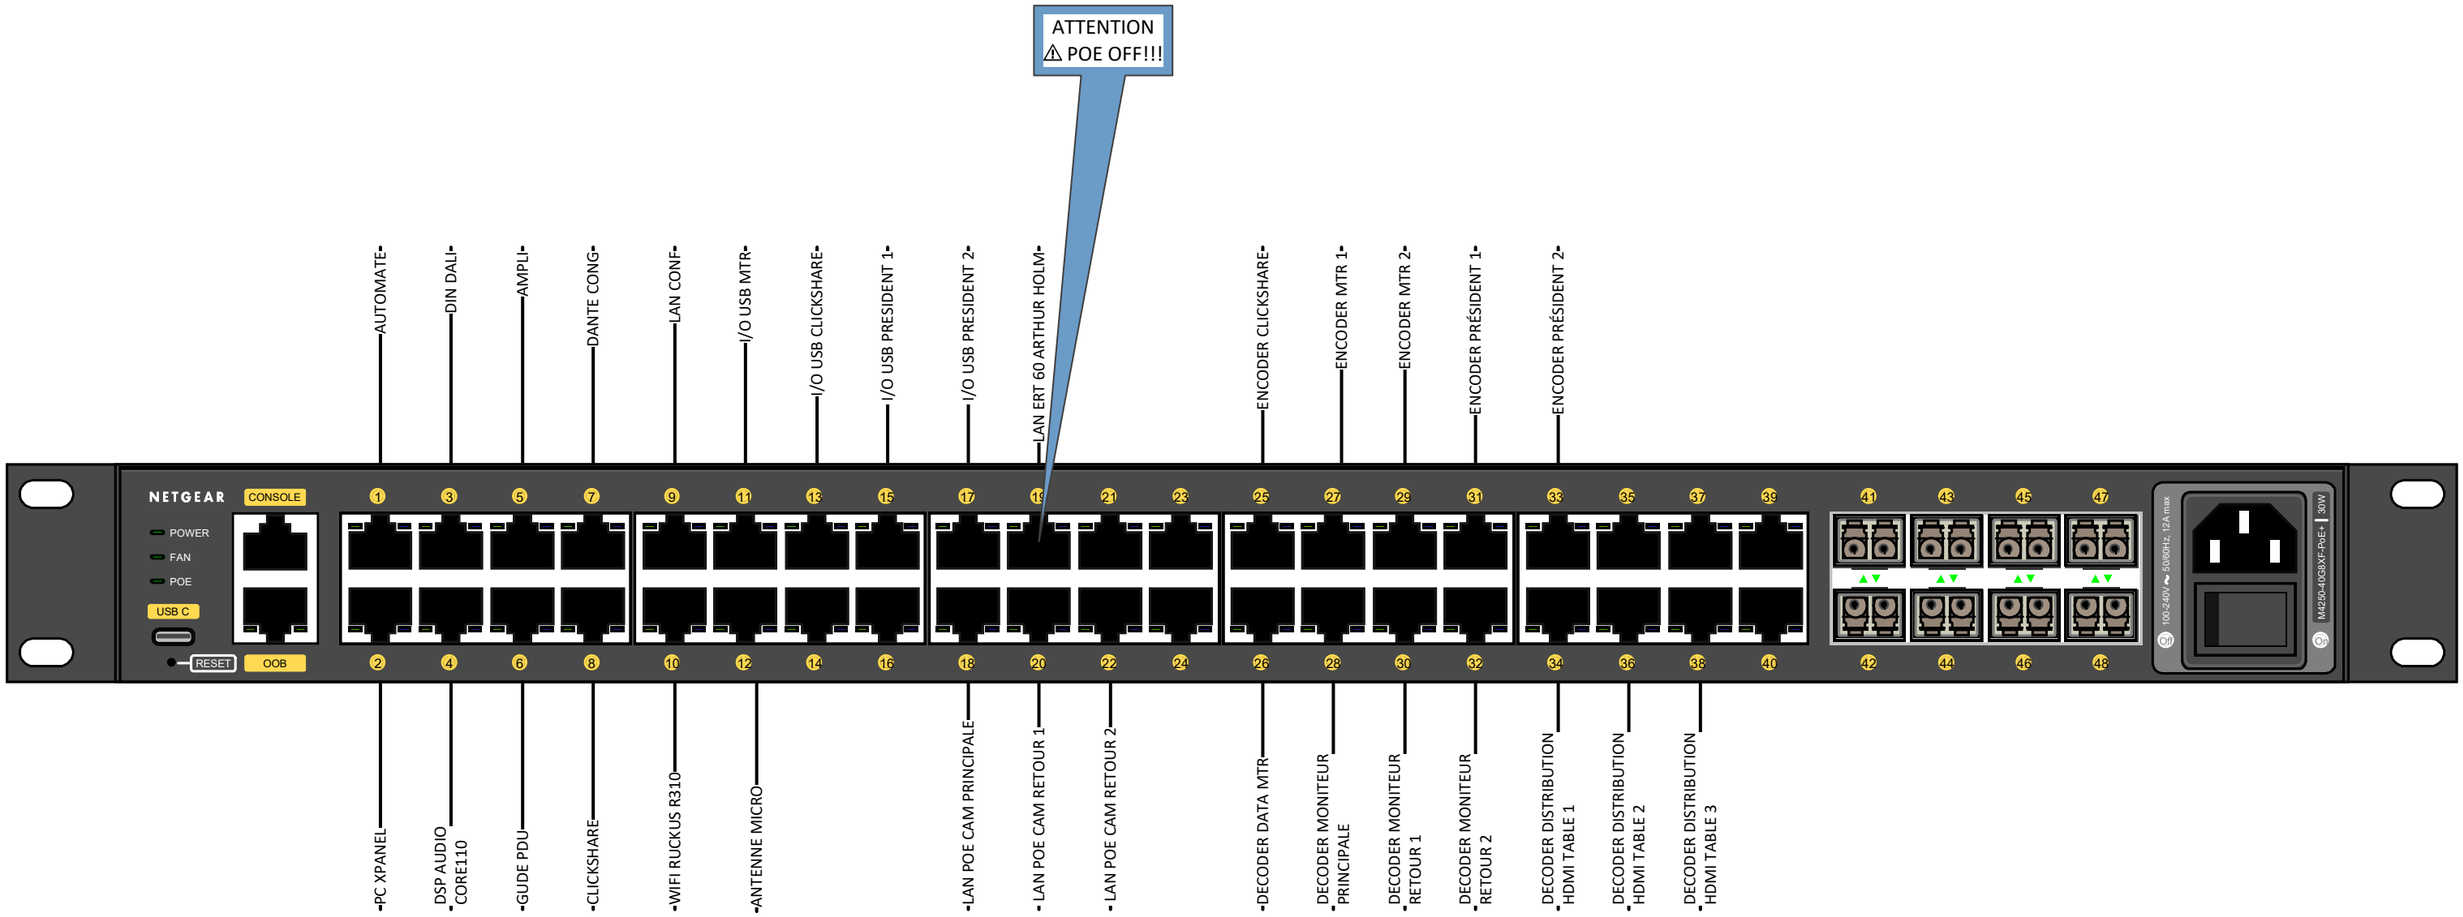

VIDEOSONIC
Image, Son & Technique
Za les portes de l'Oise
Batiment B2 – rue Henri Becquerel
60230 CHAMBLY
Tel : 01 75 01 60 40
Fax : 01 75 01 60 41
T.fourmentraux@videosonic.fr

FOURMENTRAUX THIERRY

30/01/2026

Salle du conseil

Groupama
60 Boulevard Duhamel du Monceau, 45166 Olivet

DIMENSION		SWITCH AV	RÉV 1
ECHELLE 1:1		FEUILLE 6 / 7	

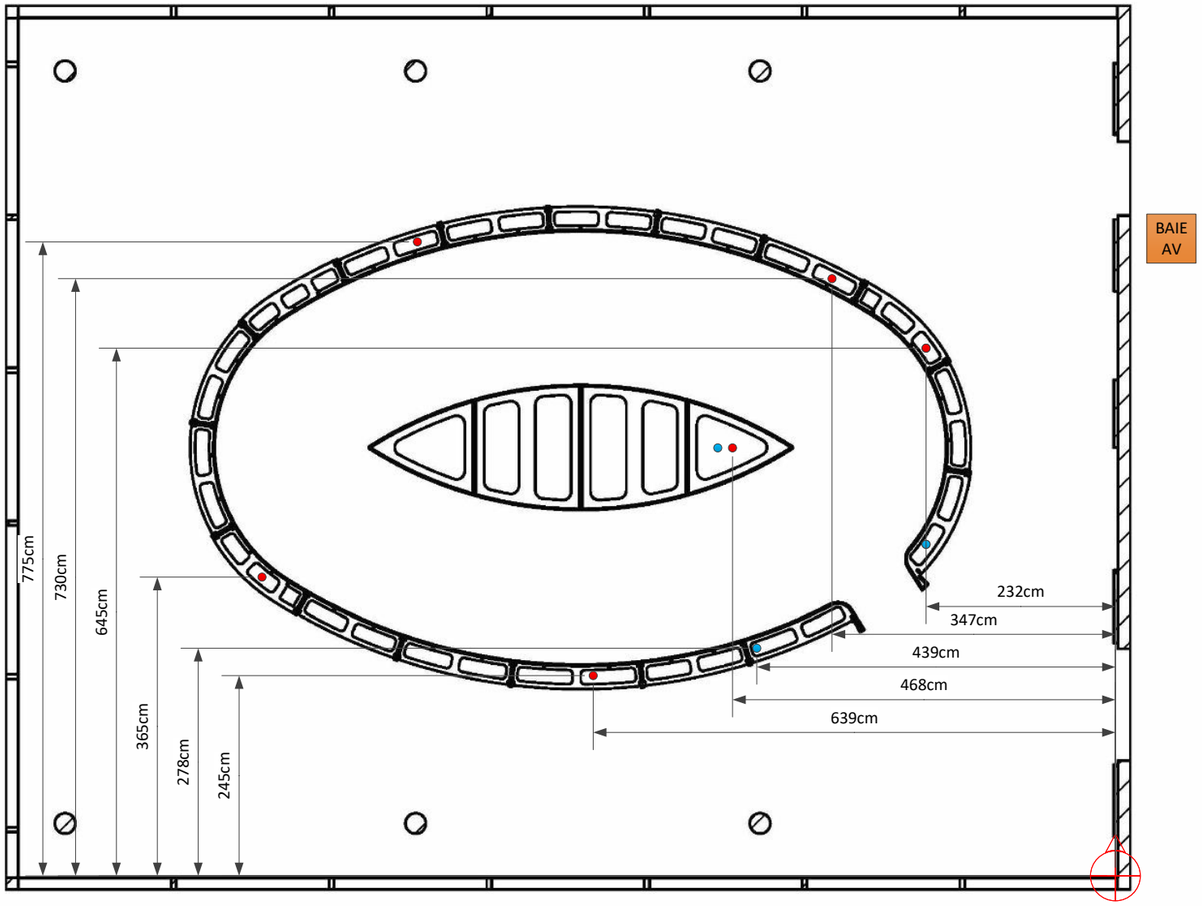

PERCEMENT POUR ALIMENTATION

PERCEMENT POUR RJ 45

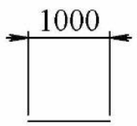

Indice	Date	Modifications	Visa

Tolérance générale Tolerie : NF-E 02-352 (n)	Tol. géné. menuiserie : +/- 1mm	Tol. géné. plasturgie : +/- 0.2mm hors épaisseurs
Echelle: 1:75 Format: A3	Matière: Voir nomenclature	Masse (g): 100831799.1 Date:

VIDEOSONIC Image, Son & Technique
Za les portes de l'Oise
Batîment B2
rue Henri Becquerel
60230 CHAMBLY
Tel : 01 75 01 60 40
Fax : 01 75 01 60 41
t.fourmentraux@videosonic.fr

Groupama Olivet - Salle du conseil - Synoptique d'execution v2.vsdx

Thierry FOURMENTRAUX	DIMENSION A3	N° CODE	PAGE tracé de sol	RÉV 30/01/2026
30/01/2026	ECHELLE 1:75		FEUILLE 7 / 7	