DESK

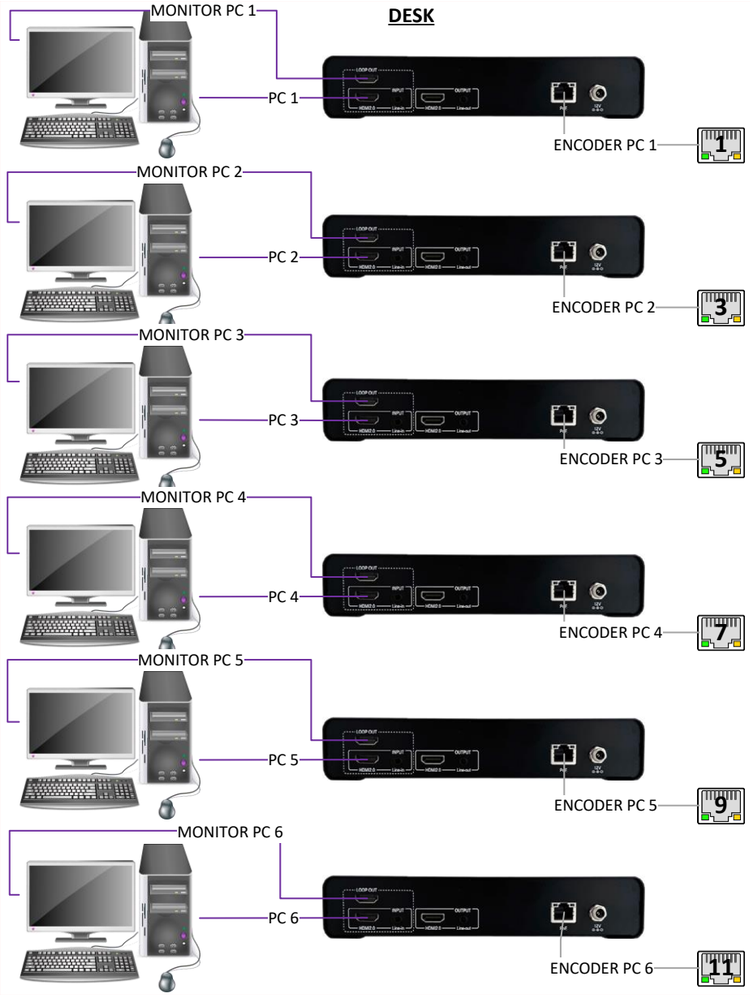

BAIE

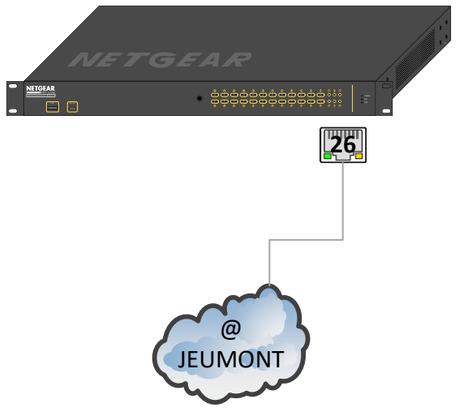

SUPPORT ECRAN

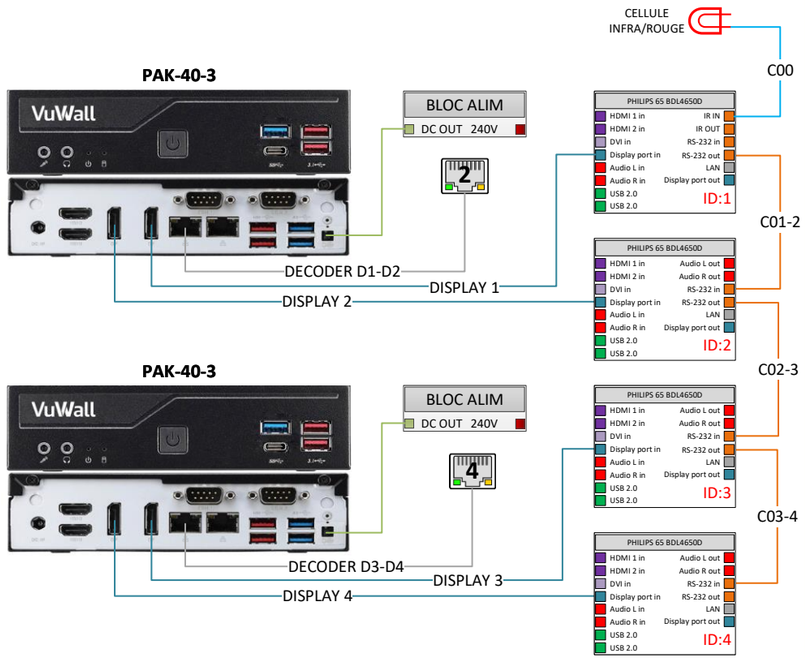

MFP62 BLUSTREAM SÉLECTEUR

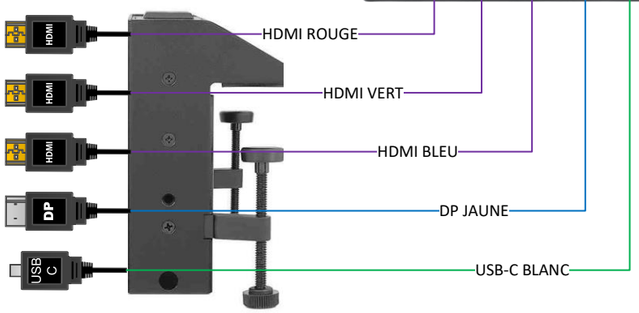

TABLE

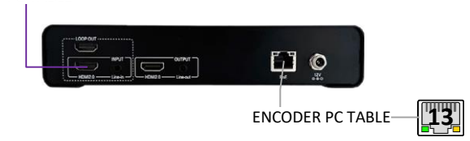

Bloc bureau3 x 2P+T - 1 USB Type-A/C - 1 RJ45 Cat.6 - HDMI - cordon 2m

Bloc bureau3 x 2P+T - 1 USB Type-A/C - 1 RJ45 Cat.6 - HDMI - cordon 2m

LEGENDE

- HDMI
- Audio
- Speakers
- USB
- RS232
- RJ45 cat6
- Audio Dante (RJ45 Cat6)
- Autres contrôles
- DVI
- FIBRE
- HD SDI
- Display port
- AC 240V
- DC OUT
- PDU

MUR
BAIE AV
TABLE

PORT LIBRE

VIDEOSONIC
Image, Son & Technique
Za les portes de l'Oise
Batîment B2
rue Henri Becquerel
60230 CHAMBLY
Tel : 01 75 01 60 40
Fax : 01 75 01 60 41
t.fourmentraux@videosonic.fr

synoptique control room.vsdm

JEUMONT ELECTRIC
367 rue de l'industrie
59572 JEUMONT

Thierry FOURMENTRAUX	DIMENSION A3	N° CODE	PAGE synoptique acv	RÉV 23/02/2026
lundi 23 février 2026	ECHELLE 1:1		FEUILLE 1 / 3	

1 U

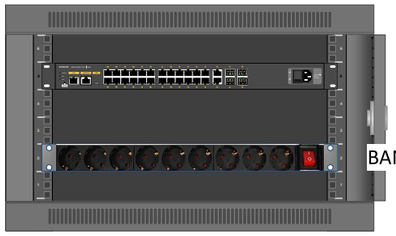

BANDEAU 9 PRISES

VIDEOSONIC
Image, Son & Technique
Za les portes de l'Oise
Batîment B2
rue Henri Becquerel
60230 CHAMBLY
Tel : 01 75 01 60 40
Fax : 01 75 01 60 41
t.fourmentraux@videosonic.fr

synoptique control room.vsdm

JEUMONT ELECTRIC
367 rue de l'industrie
59572 JEUMONT

Thierry FOURMENTRAUX

lundi 23 février 2026

DIMENSION	N° CODE	PAGE	RÉV
A3		plan de baie	23/02/2026
ECHELLE 1:10		FEUILLE 2 / 3	

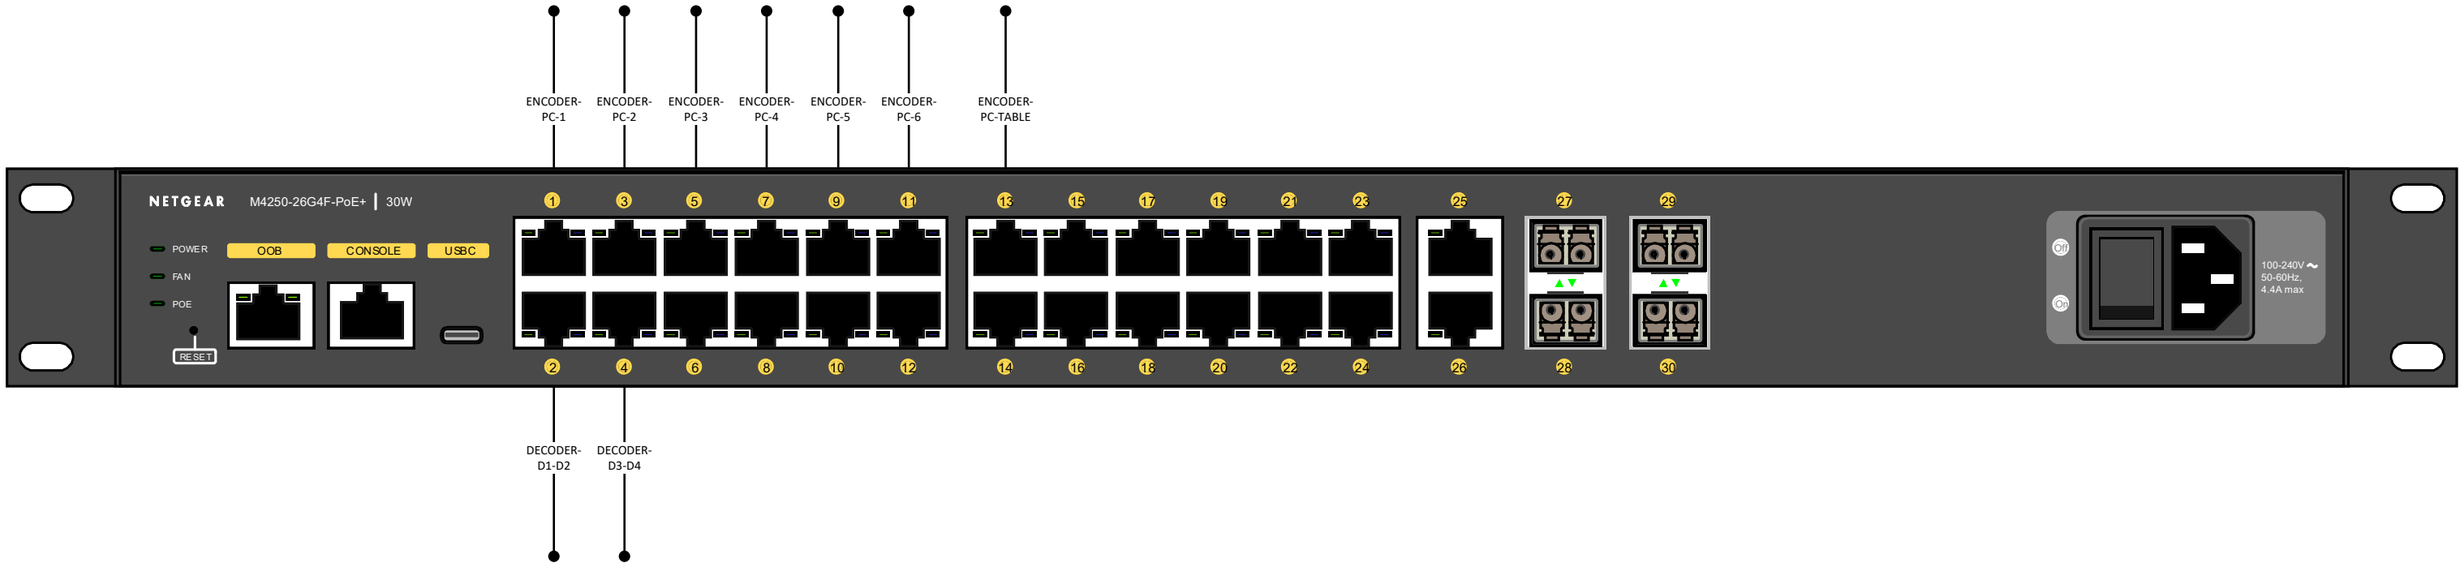

Équipement	Quanti	Norme PoE	Puissance unitaire (W	Puissance totale (W)
ENCODER VuStream 150	7	IEEE 802.3at Type 2	30	210
DECODER PAK 40	2		0	0
				0
				0
				0
				0
				0
				0
				0
				0
total port switch/amphi	9			
Budget PoE brut (W)	210			
Budget PoE recommandé (+30%) (W)	273			

VIDEOSONIC
Image, Son & Technique
Za les portes de l'Oise
Batîment B2
rue Henri Becquerel
60230 CHAMBLY
Tel : 01 75 01 60 40
Fax : 01 75 01 60 41
t.fourmentraux@videosonic.fr

synoptique control room.vsdm

JEUMONT ELECTRIC
367 rue de l'industrie
59572 JEUMONT

Thierry FOURMENTRAUX	DIMENSION A3	N° CODE	PAGE SWITCH AV	RÉV 23/02/2026
lundi 23 février 2026	ECHELLE 1:1		FEUILLE 3 / 3	