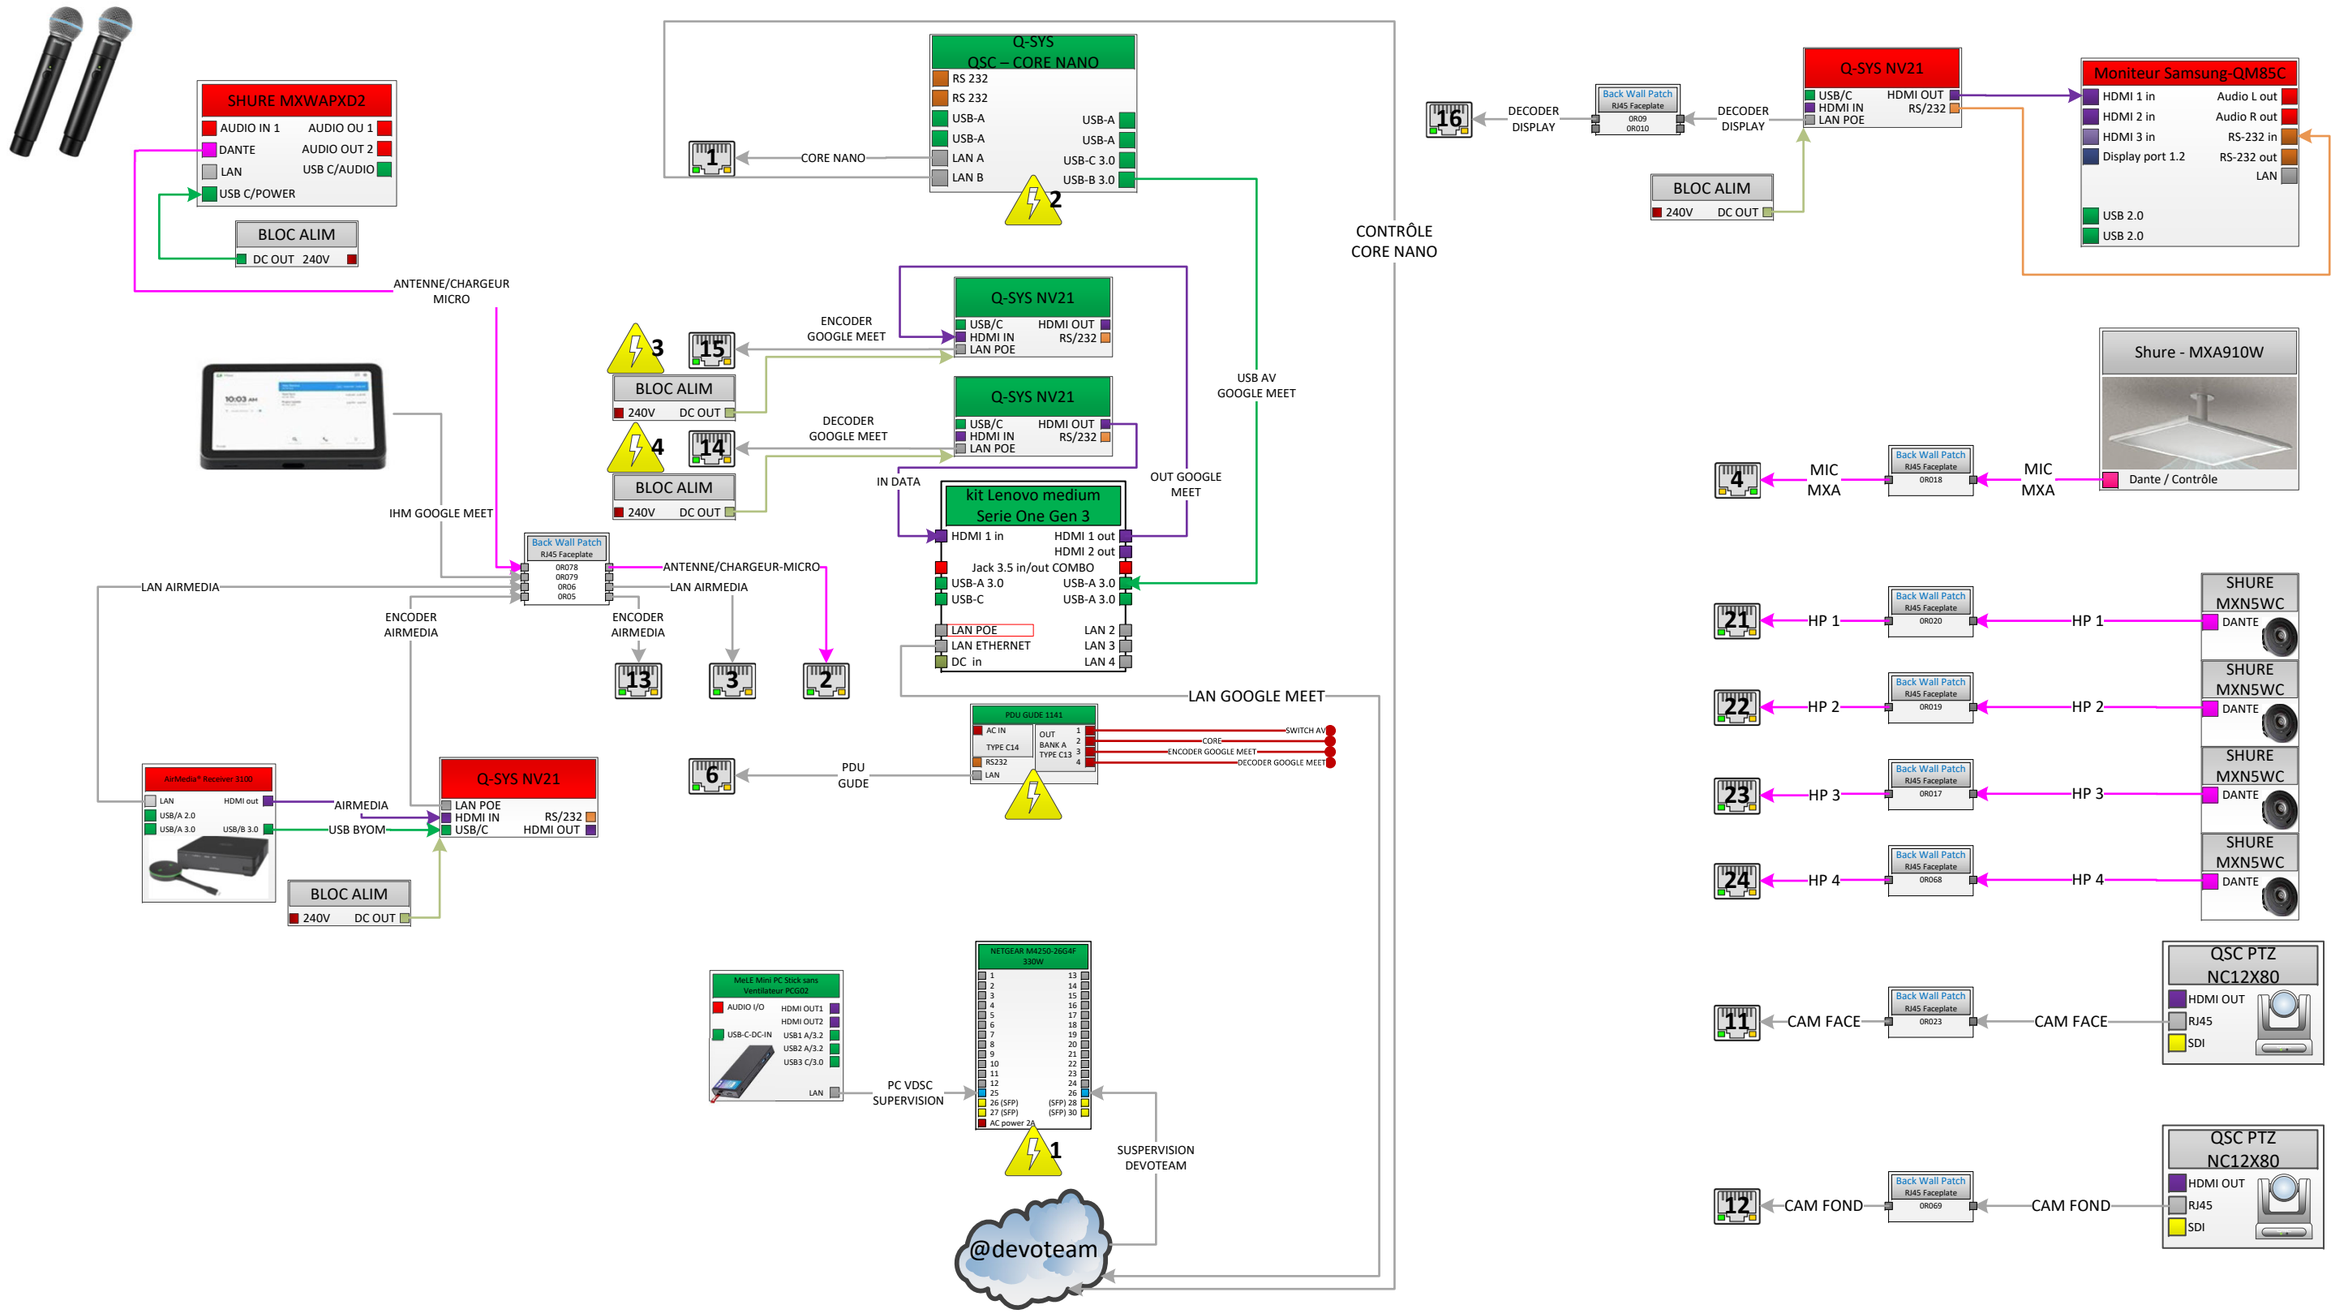

LEGENDE

- HDMI
- Audio
- Speakers
- USB
- RS232
- RJ45 cat6
- Audio Dante (RJ45 Cat6)
- Autres contrôles
- DVI
- FIBRE
- HD SDI
- Display port
- AC 240V
- DC OUT
- PDU

MUR
BAIE AV
TABLE

PORT LIBRE

3 5 9 19 27 29

8 10 18 20 28 30

VIDEOSONIC
Image, Son & Technique
Za les portes de l'Oise
Batîment B2
rue Henri Becquerel
60230 CHAMBLY
Tel : 01 75 01 60 40
Fax : 01 75 01 60 41
t.fourmentraux@videosonic.fr

synoptique atrium Toulouse.vsdm

8 RUE CLAUDE-MARIE PERROUD
TOULOUSE

Thierry FOURMENTRAUX	DIMENSION A3	N° CODE	PAGE synoptique acv	RÉV 19/02/2026
Mardi 6 janvier 2026	ECHELLE 1:1		FEUILLE 1 / 5	

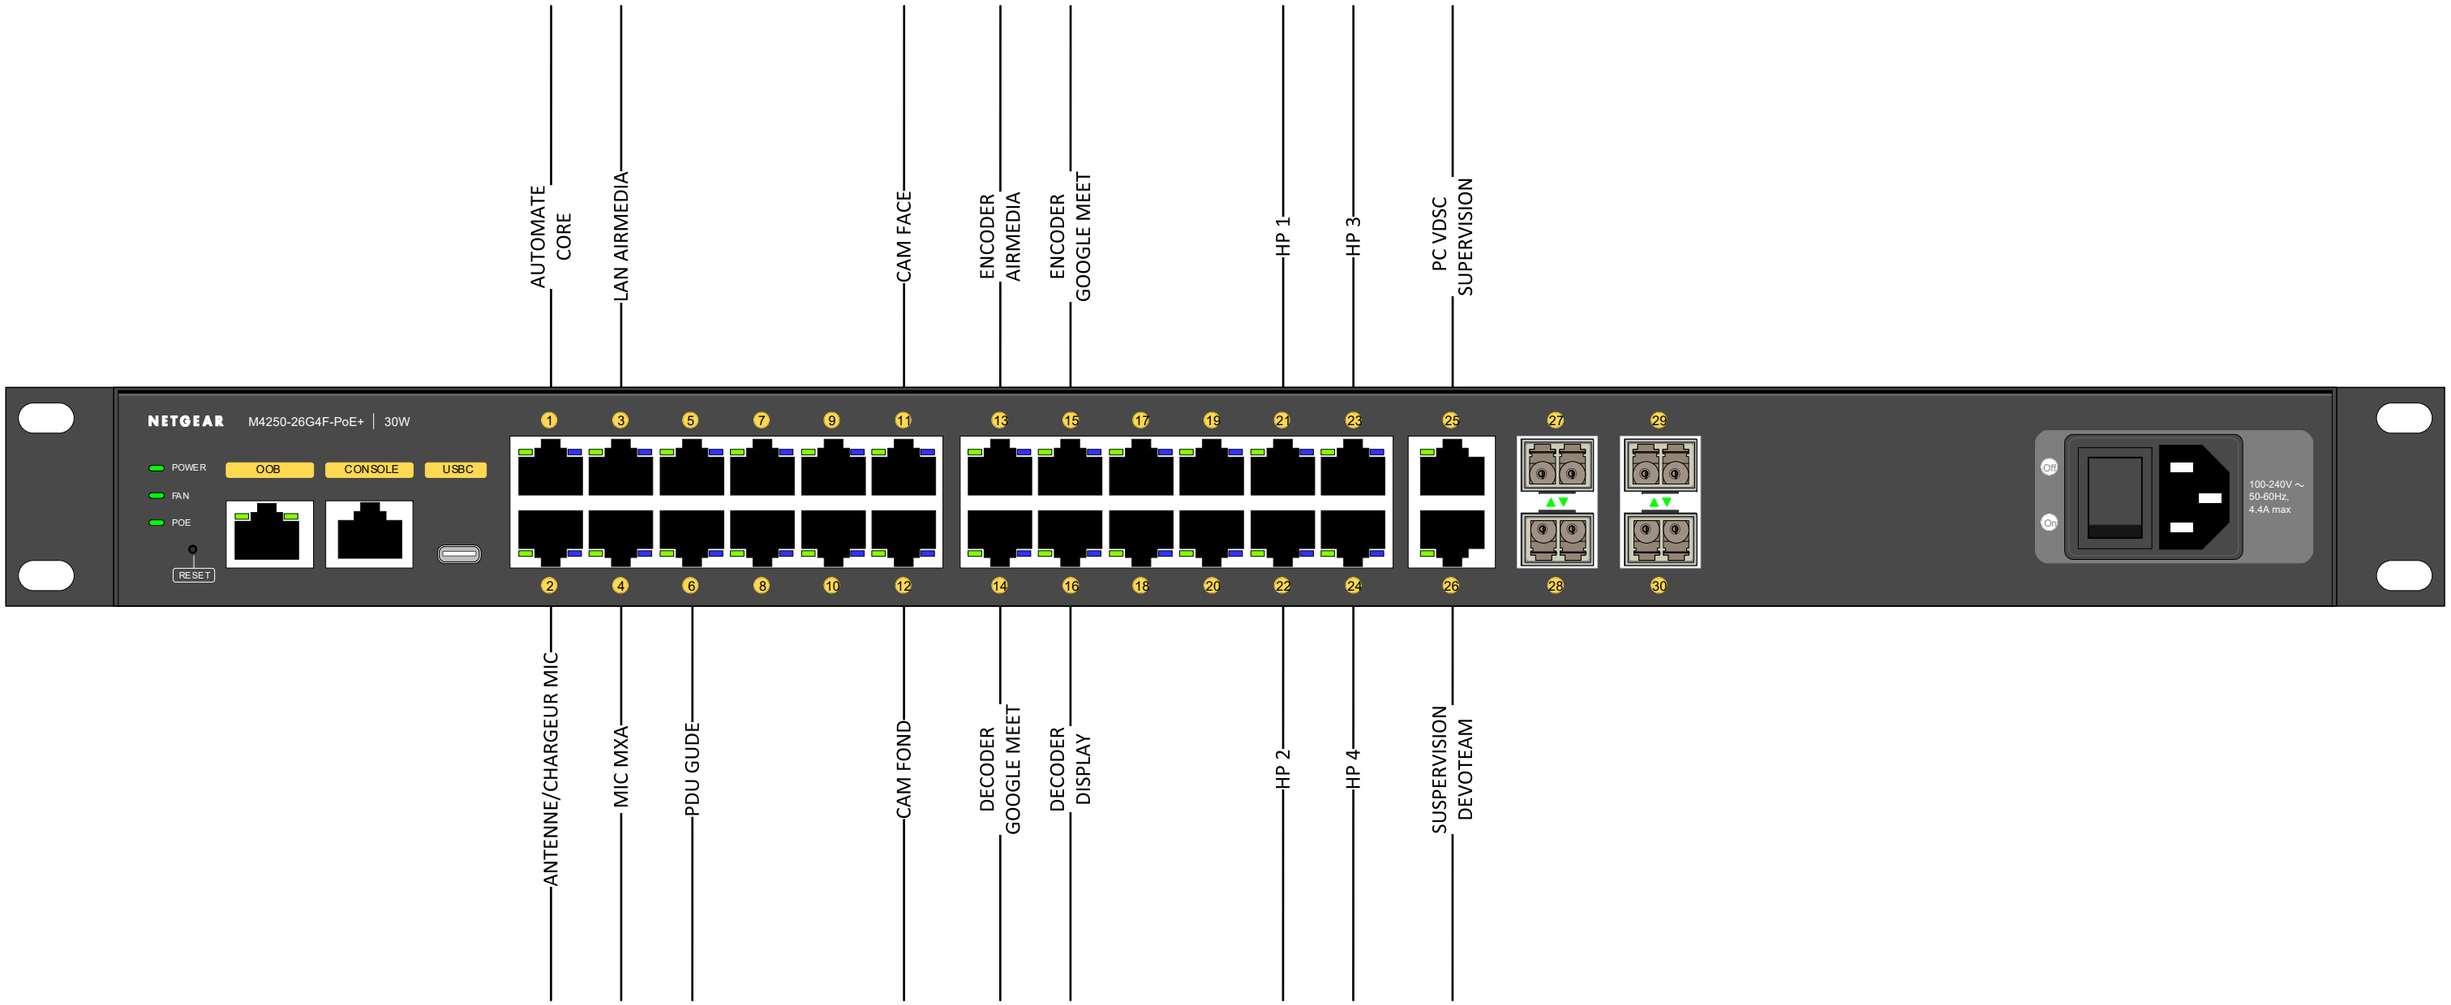

VIDEOSONIC Image, Son & Technique
Za les portes de l'Oise
Batîment B2
rue Henri Becquerel
60230 CHAMBLY
Tel : 01 75 01 60 40
Fax : 01 75 01 60 41
t.fourmentraux@videosonic.fr

synoptique atrium Toulouse.vsdm

8 RUE CLAUDE-MARIE PERROUD
TOULOUSE

Thierry FOURMENTRAUX	DIMENSION	N° CODE	PAGE	RÉV
	A3		SWITCH AV	19/02/2026
19/02/2026	ECHELLE 1:1		FEUILLE 2 / 5	

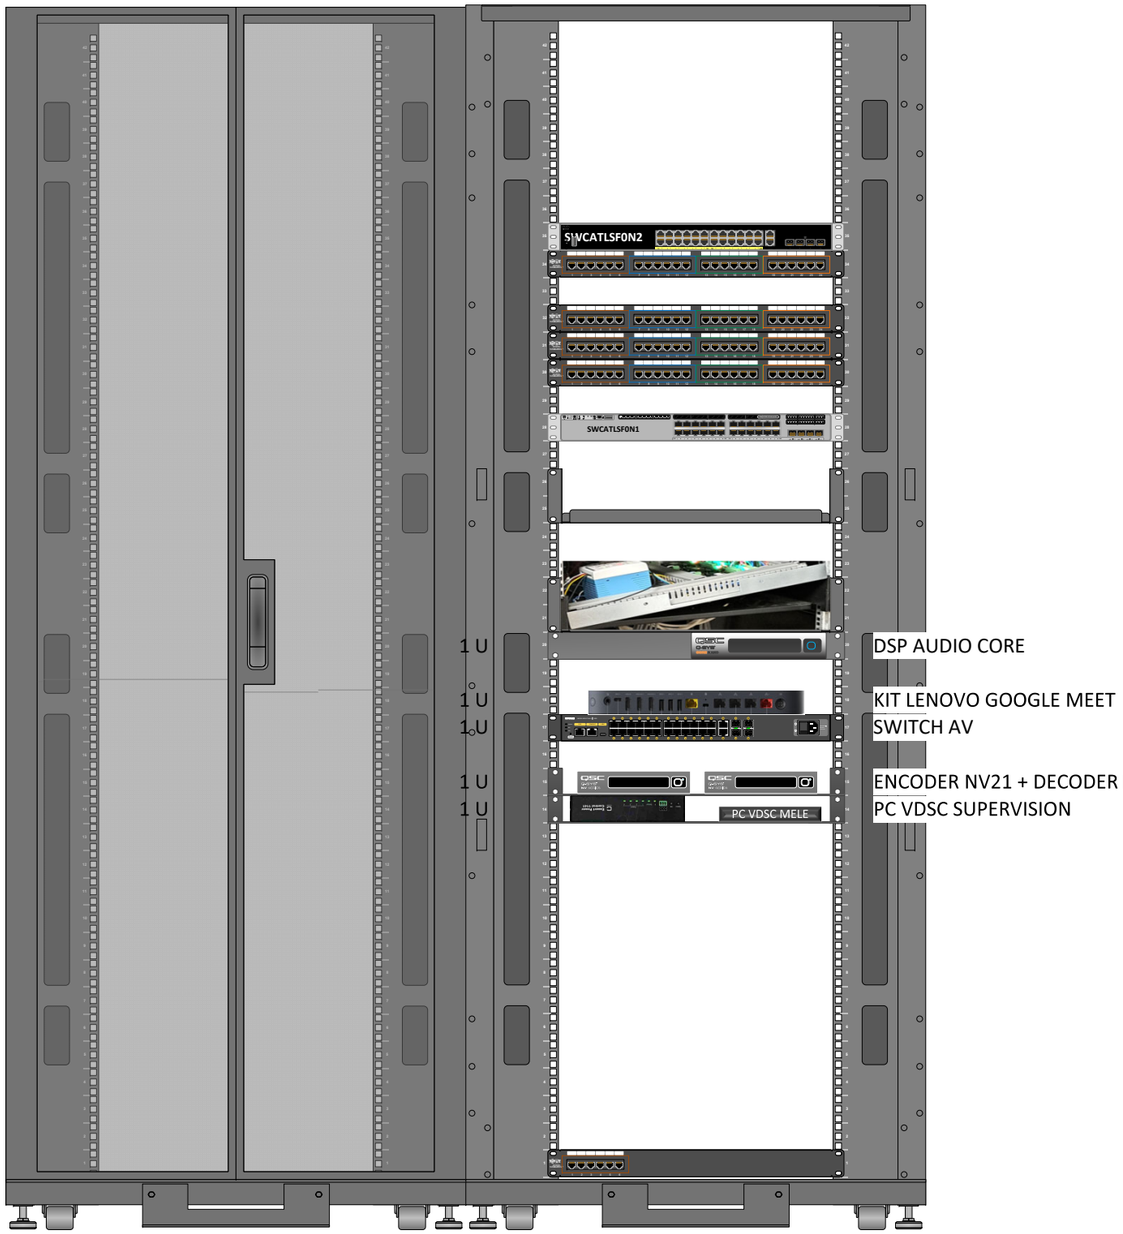

Za les portes de l'Oise
Batîment B2
rue Henri Becquerel
60230 CHAMBLY
Tel : 01 75 01 60 40
Fax : 01 75 01 60 41
t.fourmentraux@videosonic.fr

synoptique atrium Toulouse.vsdm

8 RUE CLAUDE-MARIE PERROUD
TOULOUSE

Thierry FOURMENTRAUX

Mardi 6 janvier 2026

DIMENSION	N° CODE	PAGE	RÉV
A3		plan de baie	19/02/2026
ECHELLE 1:10		FEUILLE 3 / 5	

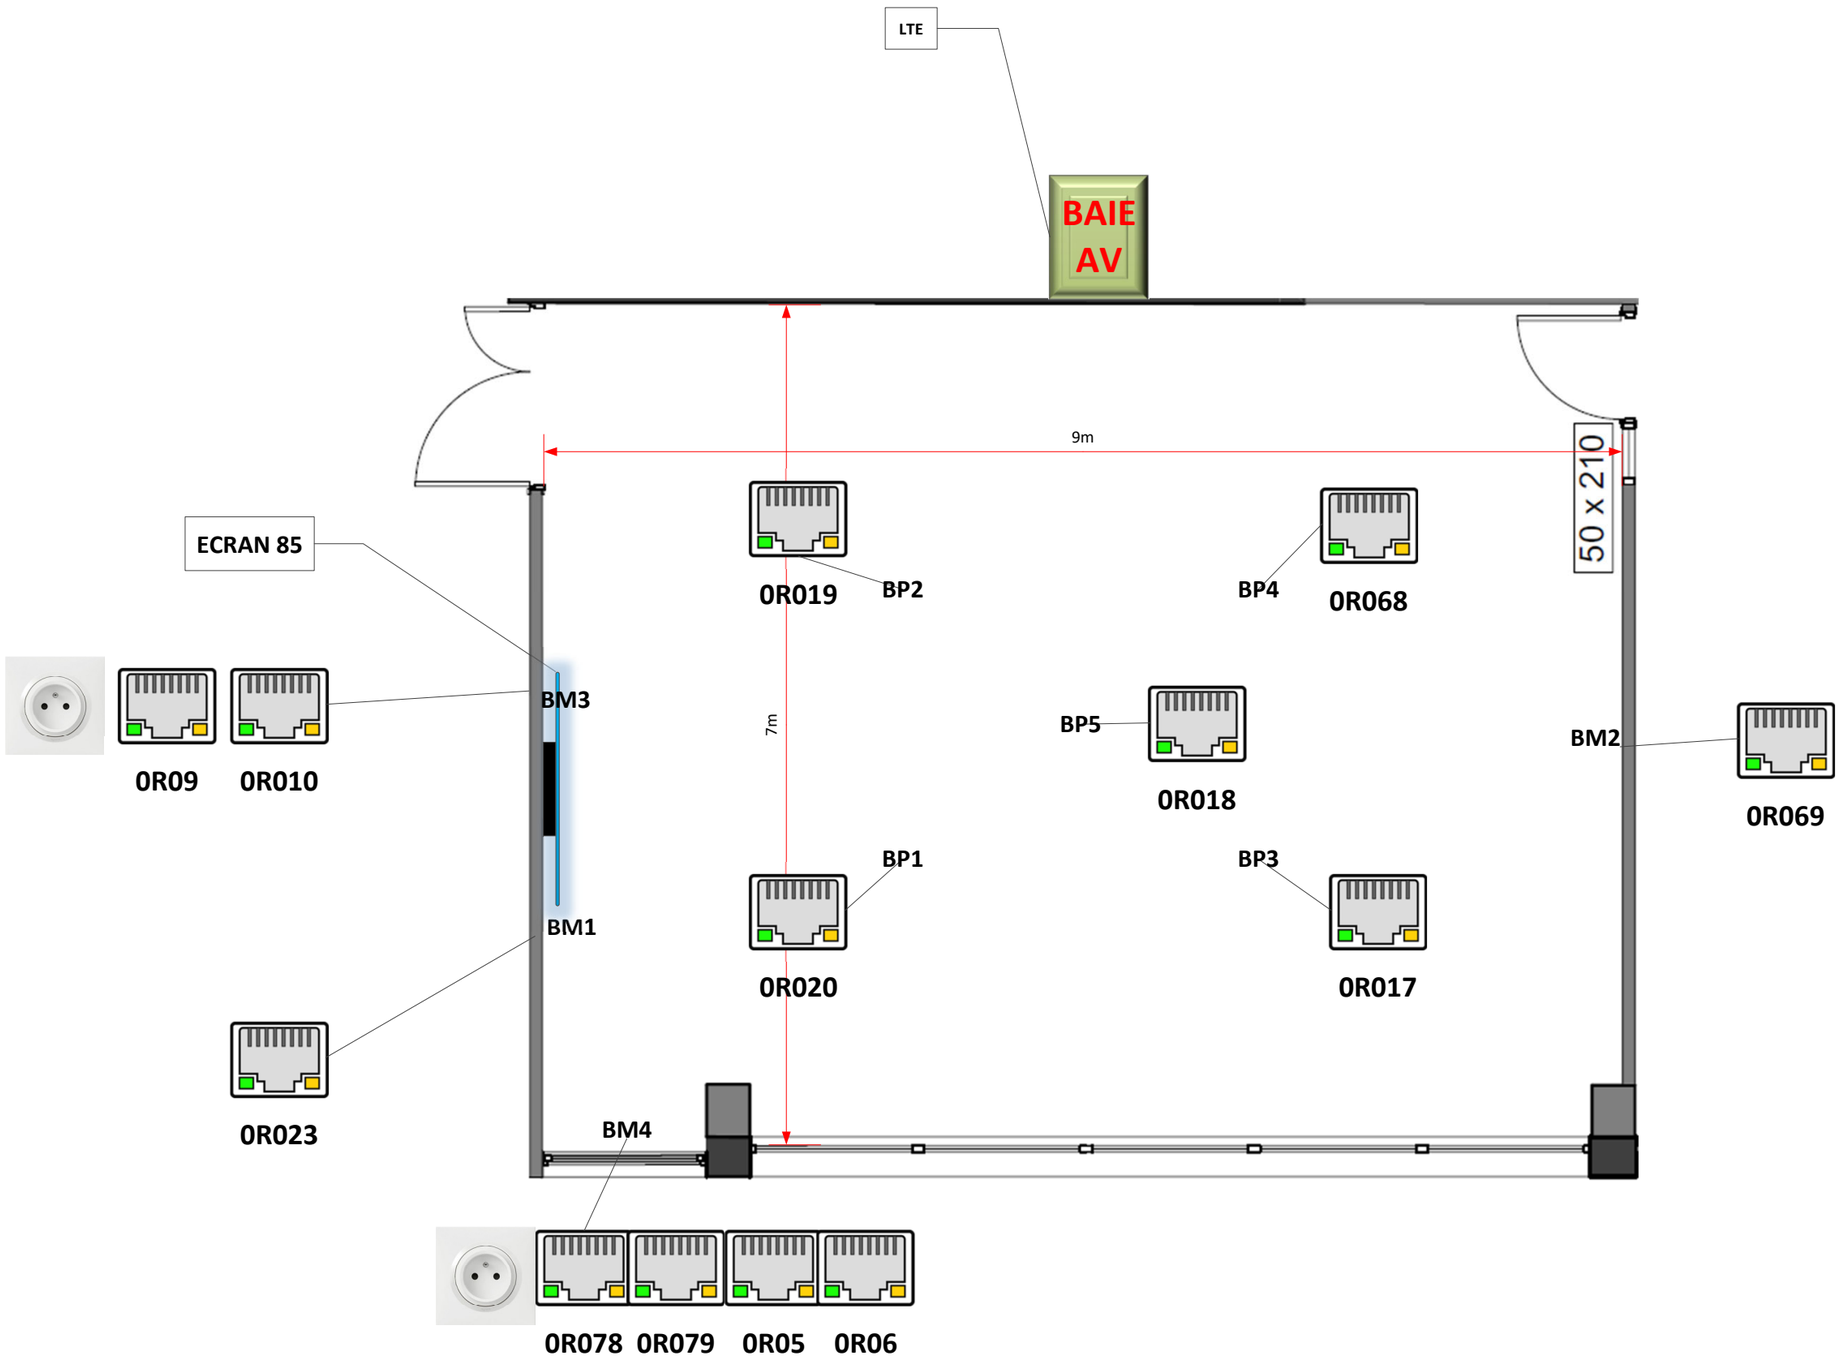

LEGENDE
BM = BOITIER MURALE
BP = BOITIER PLAFOND
BS = BOITIER DE SOL
BT = BOITIER TABLE
BAV = BAIE AUDIOVISUEL

MUR
BAIE AV
TABLE

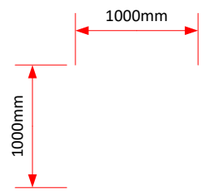

VIDEOSONIC
Image, Son & Technique
Za les portes de l'Oise
Batîment B2
rue Henri Becquerel
60230 CHAMBLY
Tel : 01 75 01 60 40
Fax : 01 75 01 60 41
t.fourmentraux@videosonic.fr

synoptique atrium Toulouse.vsdm

8 RUE CLAUDE-MARIE PERROUD
TOULOUSE

Thierry FOURMENTRAUX	DIMENSION A3	N° CODE	PAGE POSITIONNEMENT	RÉV 19/02/2026
Mardi 6 janvier 2026	ECHELLE 1:50		FEUILLE 4 / 5	

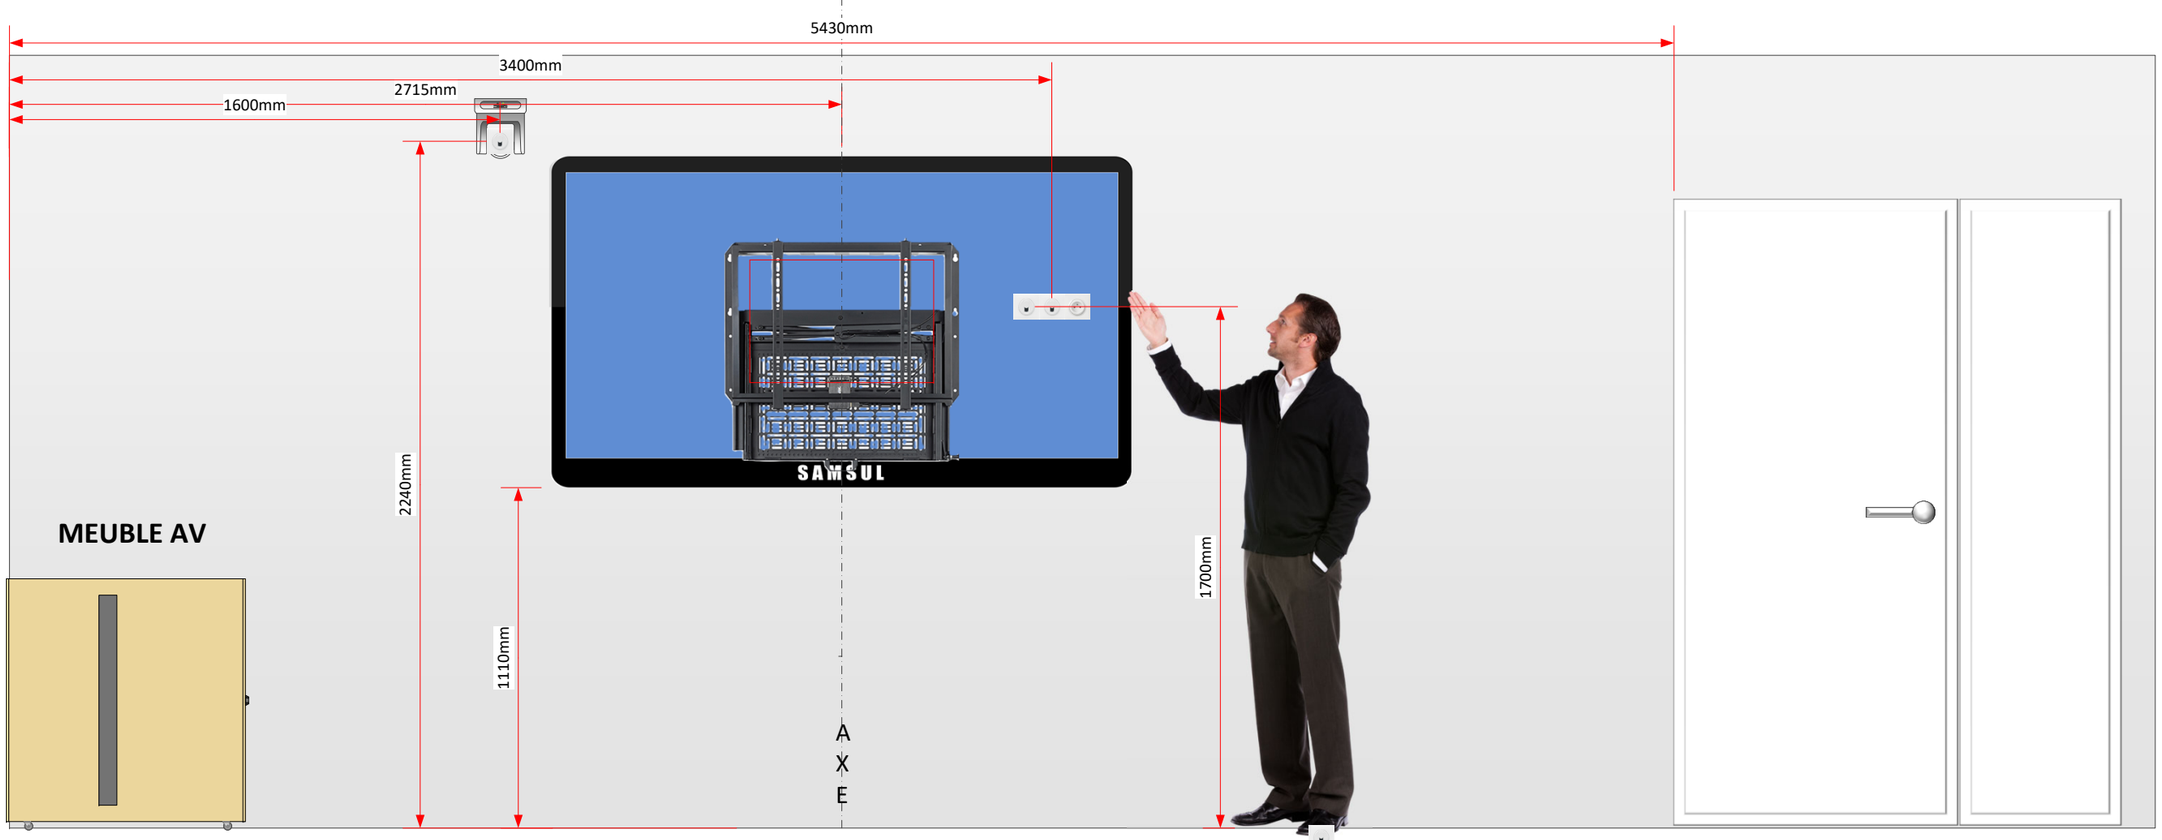

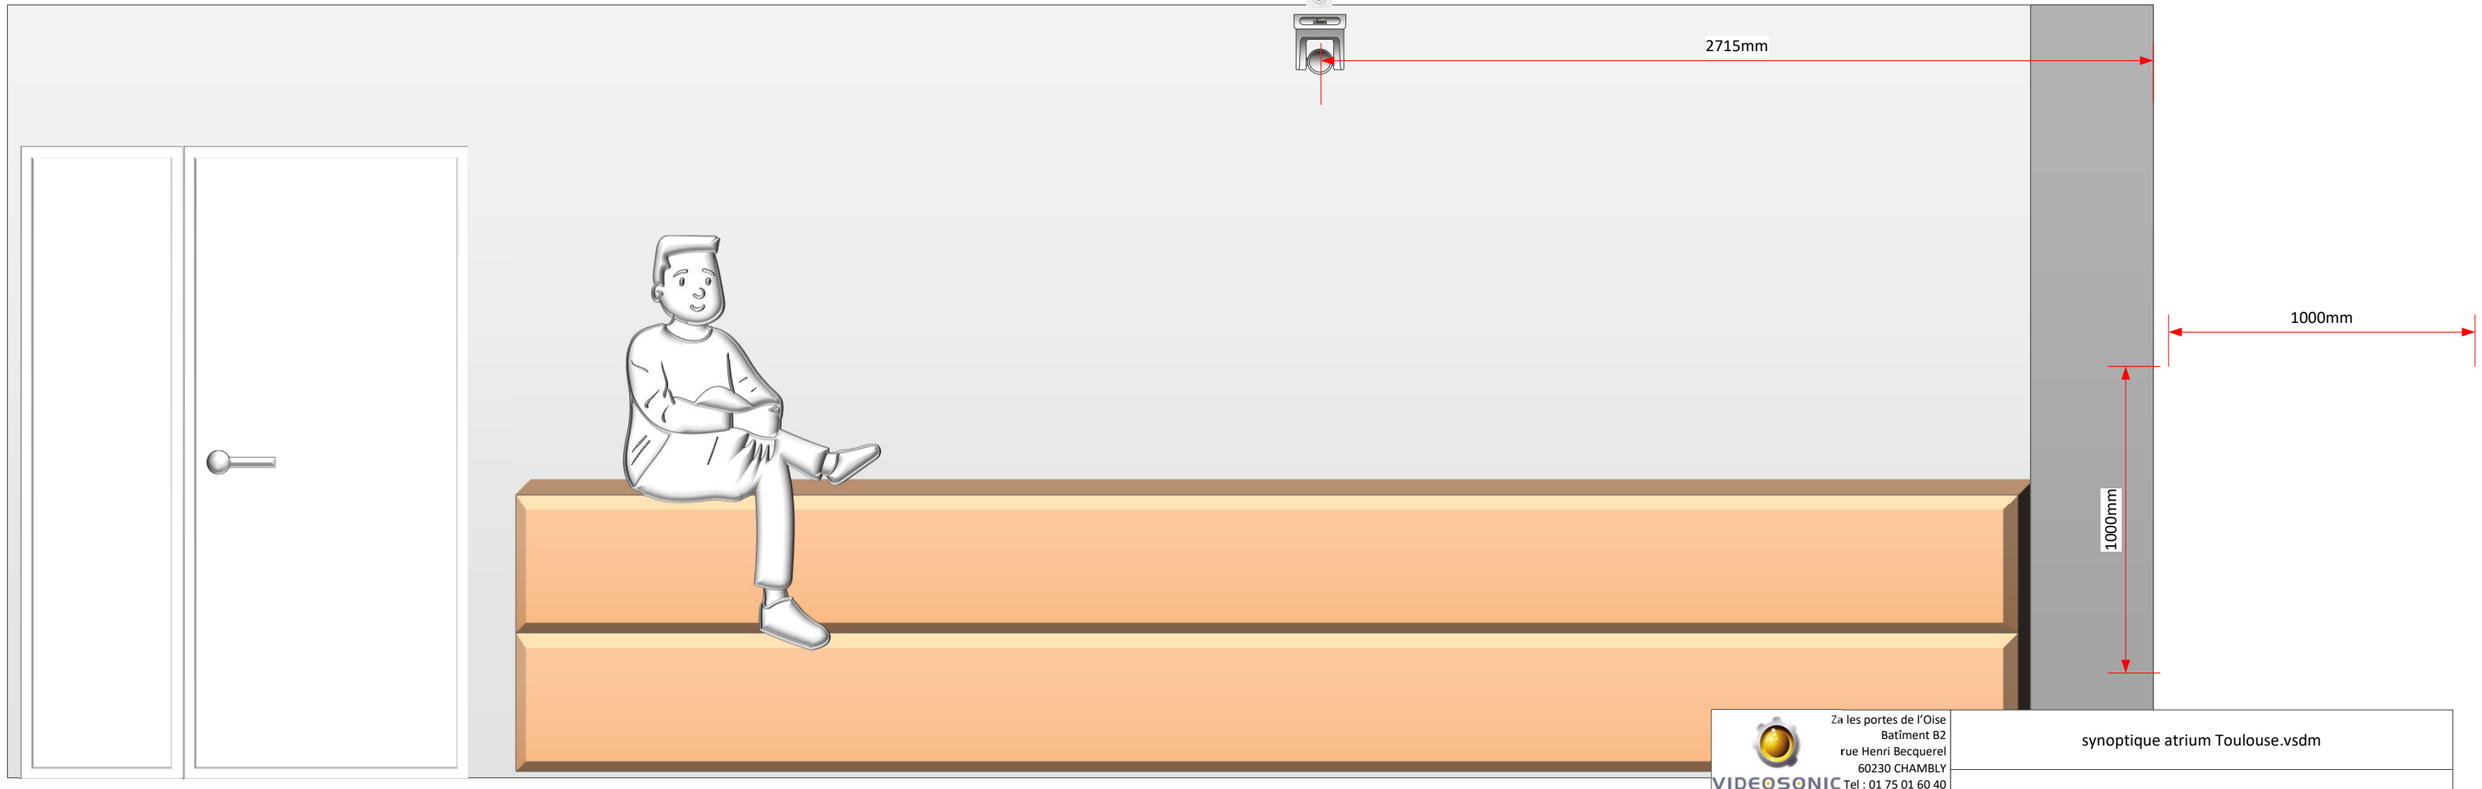

Za les portes de l'Oise
Batîment B2
rue Henri Becquerel
60230 CHAMBLY
VIDEOSONIC
Image, Son & Technique
Tel : 01 75 01 60 40
Fax : 01 75 01 60 41
t.fourmentraux@videosonic.fr

synoptique atrium Toulouse.vsdm

8 RUE CLAUDE-MARIE PERROUD
TOULOUSE

Thierry FOURMENTRAUX

Mardi 6 janvier 2026

DIMENSION	N° CODE	PAGE	RÉV
A3		mur	19/02/2026
ECHELLE 1:20		FEUILLE 5 / 5	